การประกอบเลขที่ ASSEMBLY NO. 5258

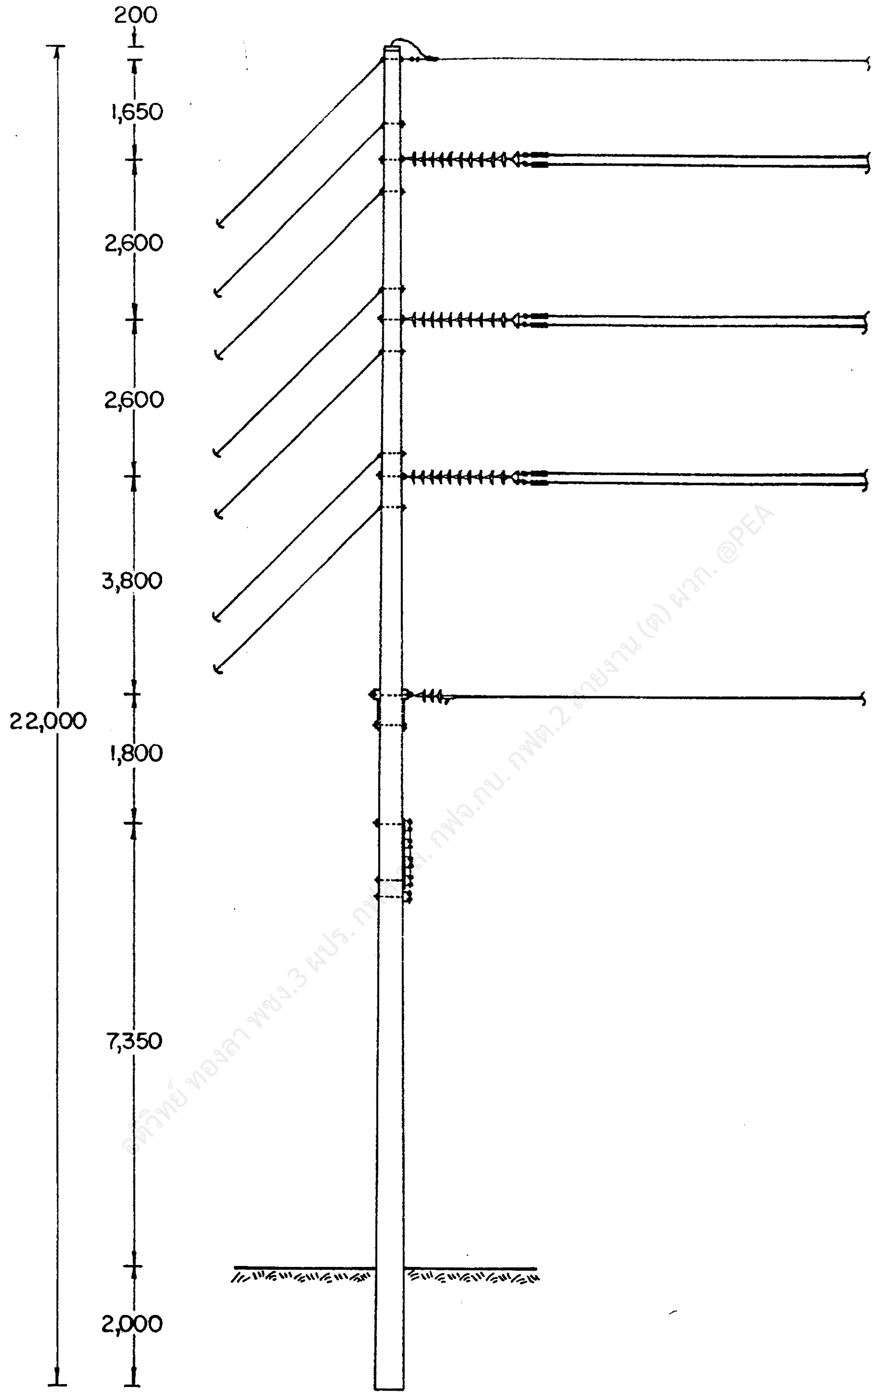

อติวิทย์ ทองลา พชง.3 ผปร. กฟ[illegible] กฟจ.กบ. กฟต.2 ฝ่ายงาน (ต) ผวก. @PEA

กองวิศวกรรมไฟฟ้าและเครื่องกล
ฝ่ายวิศวกรรม

ผู้เขียน
ผู้สำรวจ
วิศวกร
หัวหน้าแผนก
หัวหน้ากอง
ผู้อำนวยการฝ่าย
23
รองผู้ว่าการฝ่ายเทคนิค

การไฟฟ้าส่วนภูมิภาค

ผู้ว่าการ .... 24 มิ.ค.23

115 kV วงจรเดี่ยว สายไฟฟ้าคู่
เสาสำหรับเจ้าปลายสาย
แบบ SD-DE-1

115 kV SINGLE CIRCUIT DOUBLE CONDUCTOR
DEAD END STRUCTURE
TYPE SD-DE-1

ใช้แทนแบบ
ถูกแทนโดยแบบ
เขียนเสร็จวันที่ 2 มค.23
แก้แบบวันที่
มิติเป็น มม.
มาตราส่วน 1 : 125

แบบเลขที่ SAI-015/23012
แผ่นที่ 1 ของจำนวน 3 แผ่น

ศก 7573

การประกอบเลขที่ 5258
ASSEMBLY NO.

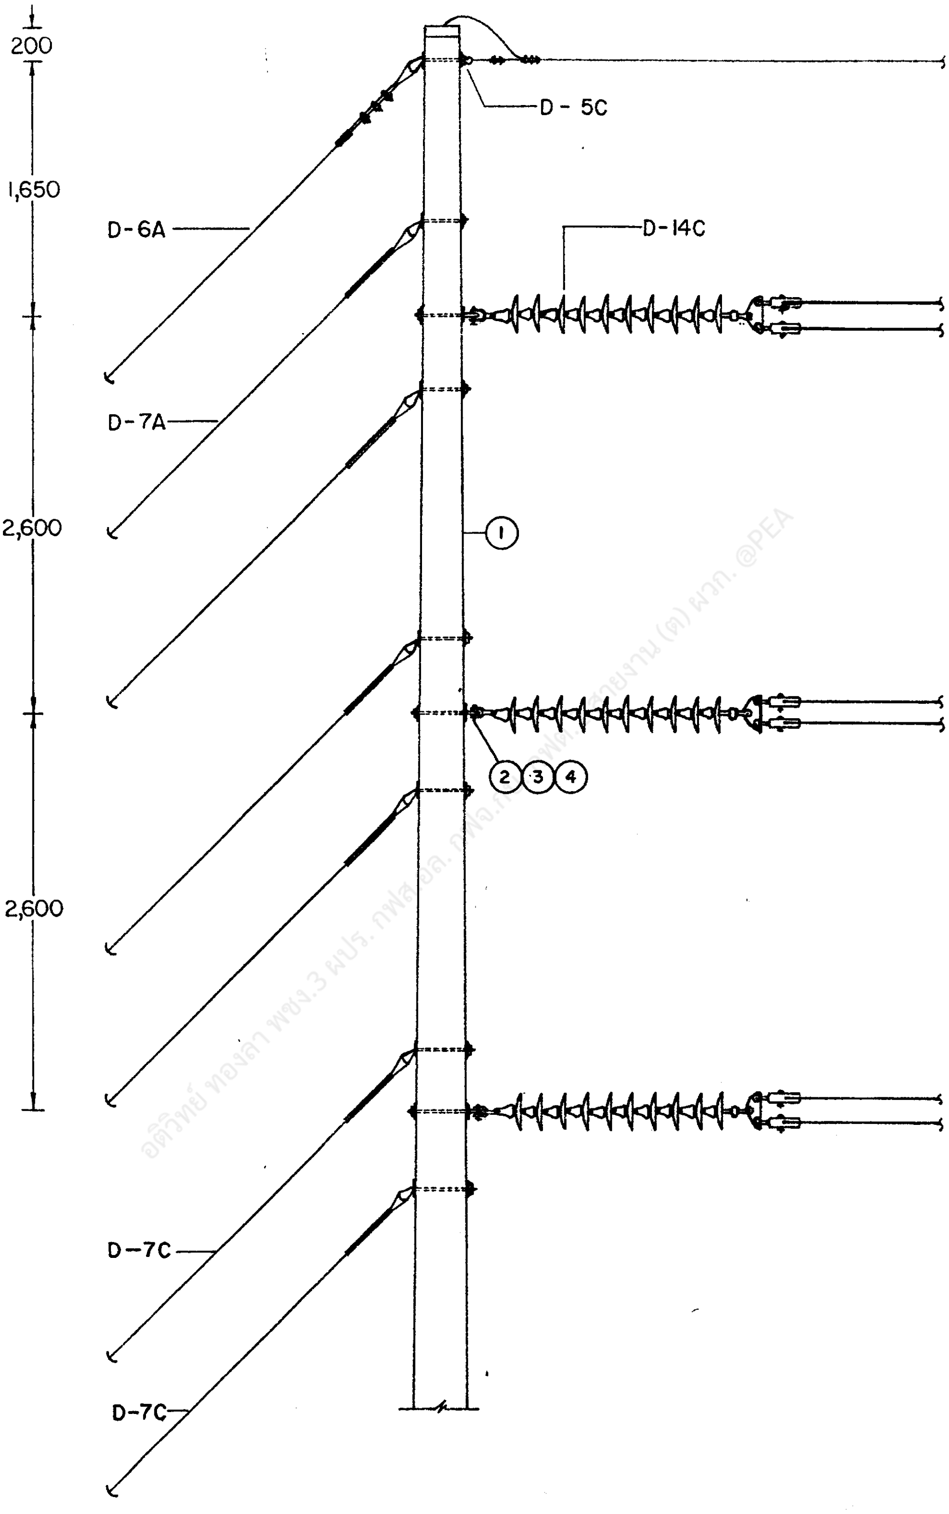

กองวิศวกรรมไฟฟ้าและเครื่องกล ฝ่ายวิศวกรรม	การไฟฟ้าส่วนภูมิภาค	ใช้แทนแบบ ถูกแทนโดยแบบ
ผู้เขียน ผู้สำรวจ วิศวกร หัวหน้าแผนก หัวหน้ากอง ผู้อำนวยการฝ่าย	ผู้ว่าการ 24 มี.ค. 23	เขียนเสร็จวันที่ 2 ม.ค.23 แก้แบบวันที่ 15 ก.ย.40
	115 kV วงจรเดี่ยว สายไฟฟ้าคู่ เสาสำหรับเข้าปลายสาย แบบ SD-DE-1	มิติเป็น มม. มาตราส่วน 1 : 50
28 มี.ค. 23 รองผู้ว่าการฝ่ายเทคนิค	115 kV SINGLE CIRCUIT DOUBLE CONDUCTOR DEAD END STRUCTURE TYPE SD-DE-1	แบบเลขที่ SAI-015/23012 แผ่นที่ 2 จากจำนวน 3 แผ่น

การประกอบเลขที่
ASSEMBLY NO: 5258

บัญชีวัสดุ
BILL OF MATERIAL

ลำดับที่ ITEM	รายละเอียด DESCRIPTION	จำนวน REQ'D	วัสดุเลขที่ MAT. NO.
1	เสาคอนกรีต 22 ม. POLE, CONCRETE 22 m LONG	1	00010011 (0041)
2	สลักห่วงโอแวล M 20X350 มม. BOLT, OVAL EYE M 20 X 350 mm	3	01150100 (0260)
3	แหวนสี่เหลี่ยมแบน 62X62X6 มม. รู Ø 22 มม. มอก. 258 WASHER, SQUARE, FLAT 62X62X6 mm HOLE Ø 22 mm TIS 258	6	01180101 (0356)
4	แหวนสปริง M 20 มอก. 259 WASHER, LOCK, M 20, TIS 259	3	01180302 (0366)

รายละเอียด
DETAIL

D-5C	การต่อสายล่อฟ้า OVERHEAD GROUND WIRE CONNECTION	1	
D-6A	การประกอบสายยึดโยงลวดเหล็กตีเกลียว 50 ต.มม. STEEL STRANDED WIRE 50 mm^2 GUY ASSEMBLY	1	
D-7A	การประกอบสายยึดโยงลวดเหล็กตีเกลียว 95 ต.มม. STEEL STRANDED WIRE 95 mm^2 GUY ASSEMBLY	4	
D-7C	การประกอบสายยึดโยงลวดเหล็กตีเกลียว 95 ต.มม. STEEL STRANDED WIRE 95 mm^2 GUY ASSEMBLY	2	
D-9A	สมอบกคอนกรีต CONCRETE ANCHOR	1	
D-10A	ฐานรากเสา POLE FOUNDATION	1	
D-14C	การประกอบลูกถ้วยแขวน SUSPENSION INSULATOR ASSEMBLY	3	

อติวิทย์ ทองลา พชง.3 [illegible] กฟฉ.อล. กฟจ.กบ. [illegible] 2 สายงาน (ค) ผวก. @PEA

กองวิศวกรรมไฟฟ้าและเครื่องกล
ฝ่ายวิศวกรรม
ผู้เขียน
ผู้สำรวจ
วิศวกร
หัวหน้าแผนก
หัวหน้ากอง
ผู้อำนวยการฝ่าย
รองผู้ว่าการฝ่ายเทคนิค

การไฟฟ้าส่วนภูมิภาค
ผู้ว่าการ 24 มี.ค.23

115 kV วงจรเดี่ยว สายไฟฟ้าคู่
เสาสำหรับเข้าปลายสาย
แบบ SD-DE-1

3 115 kV SINGLE CIRCUIT DOUBLE CONDUCTOR
DEAD END STRUCTURE
TYPE SD-DE-1

ใช้แทนแบบ
ถูกแทนโดยแบบ
เขียนเสร็จวันที่ 2 ม.ค.23
แก้แบบวันที่ 15 กย.40
ผลิตเป็น
มาตราส่วน

แบบเลขที่ SAI-015/23012
แผ่นที่ 3 ของจำนวน 3 แผ่น

10 พ.ค. 2523