

การประกอบเลขที่ 3803
ASSEMBLY NO.

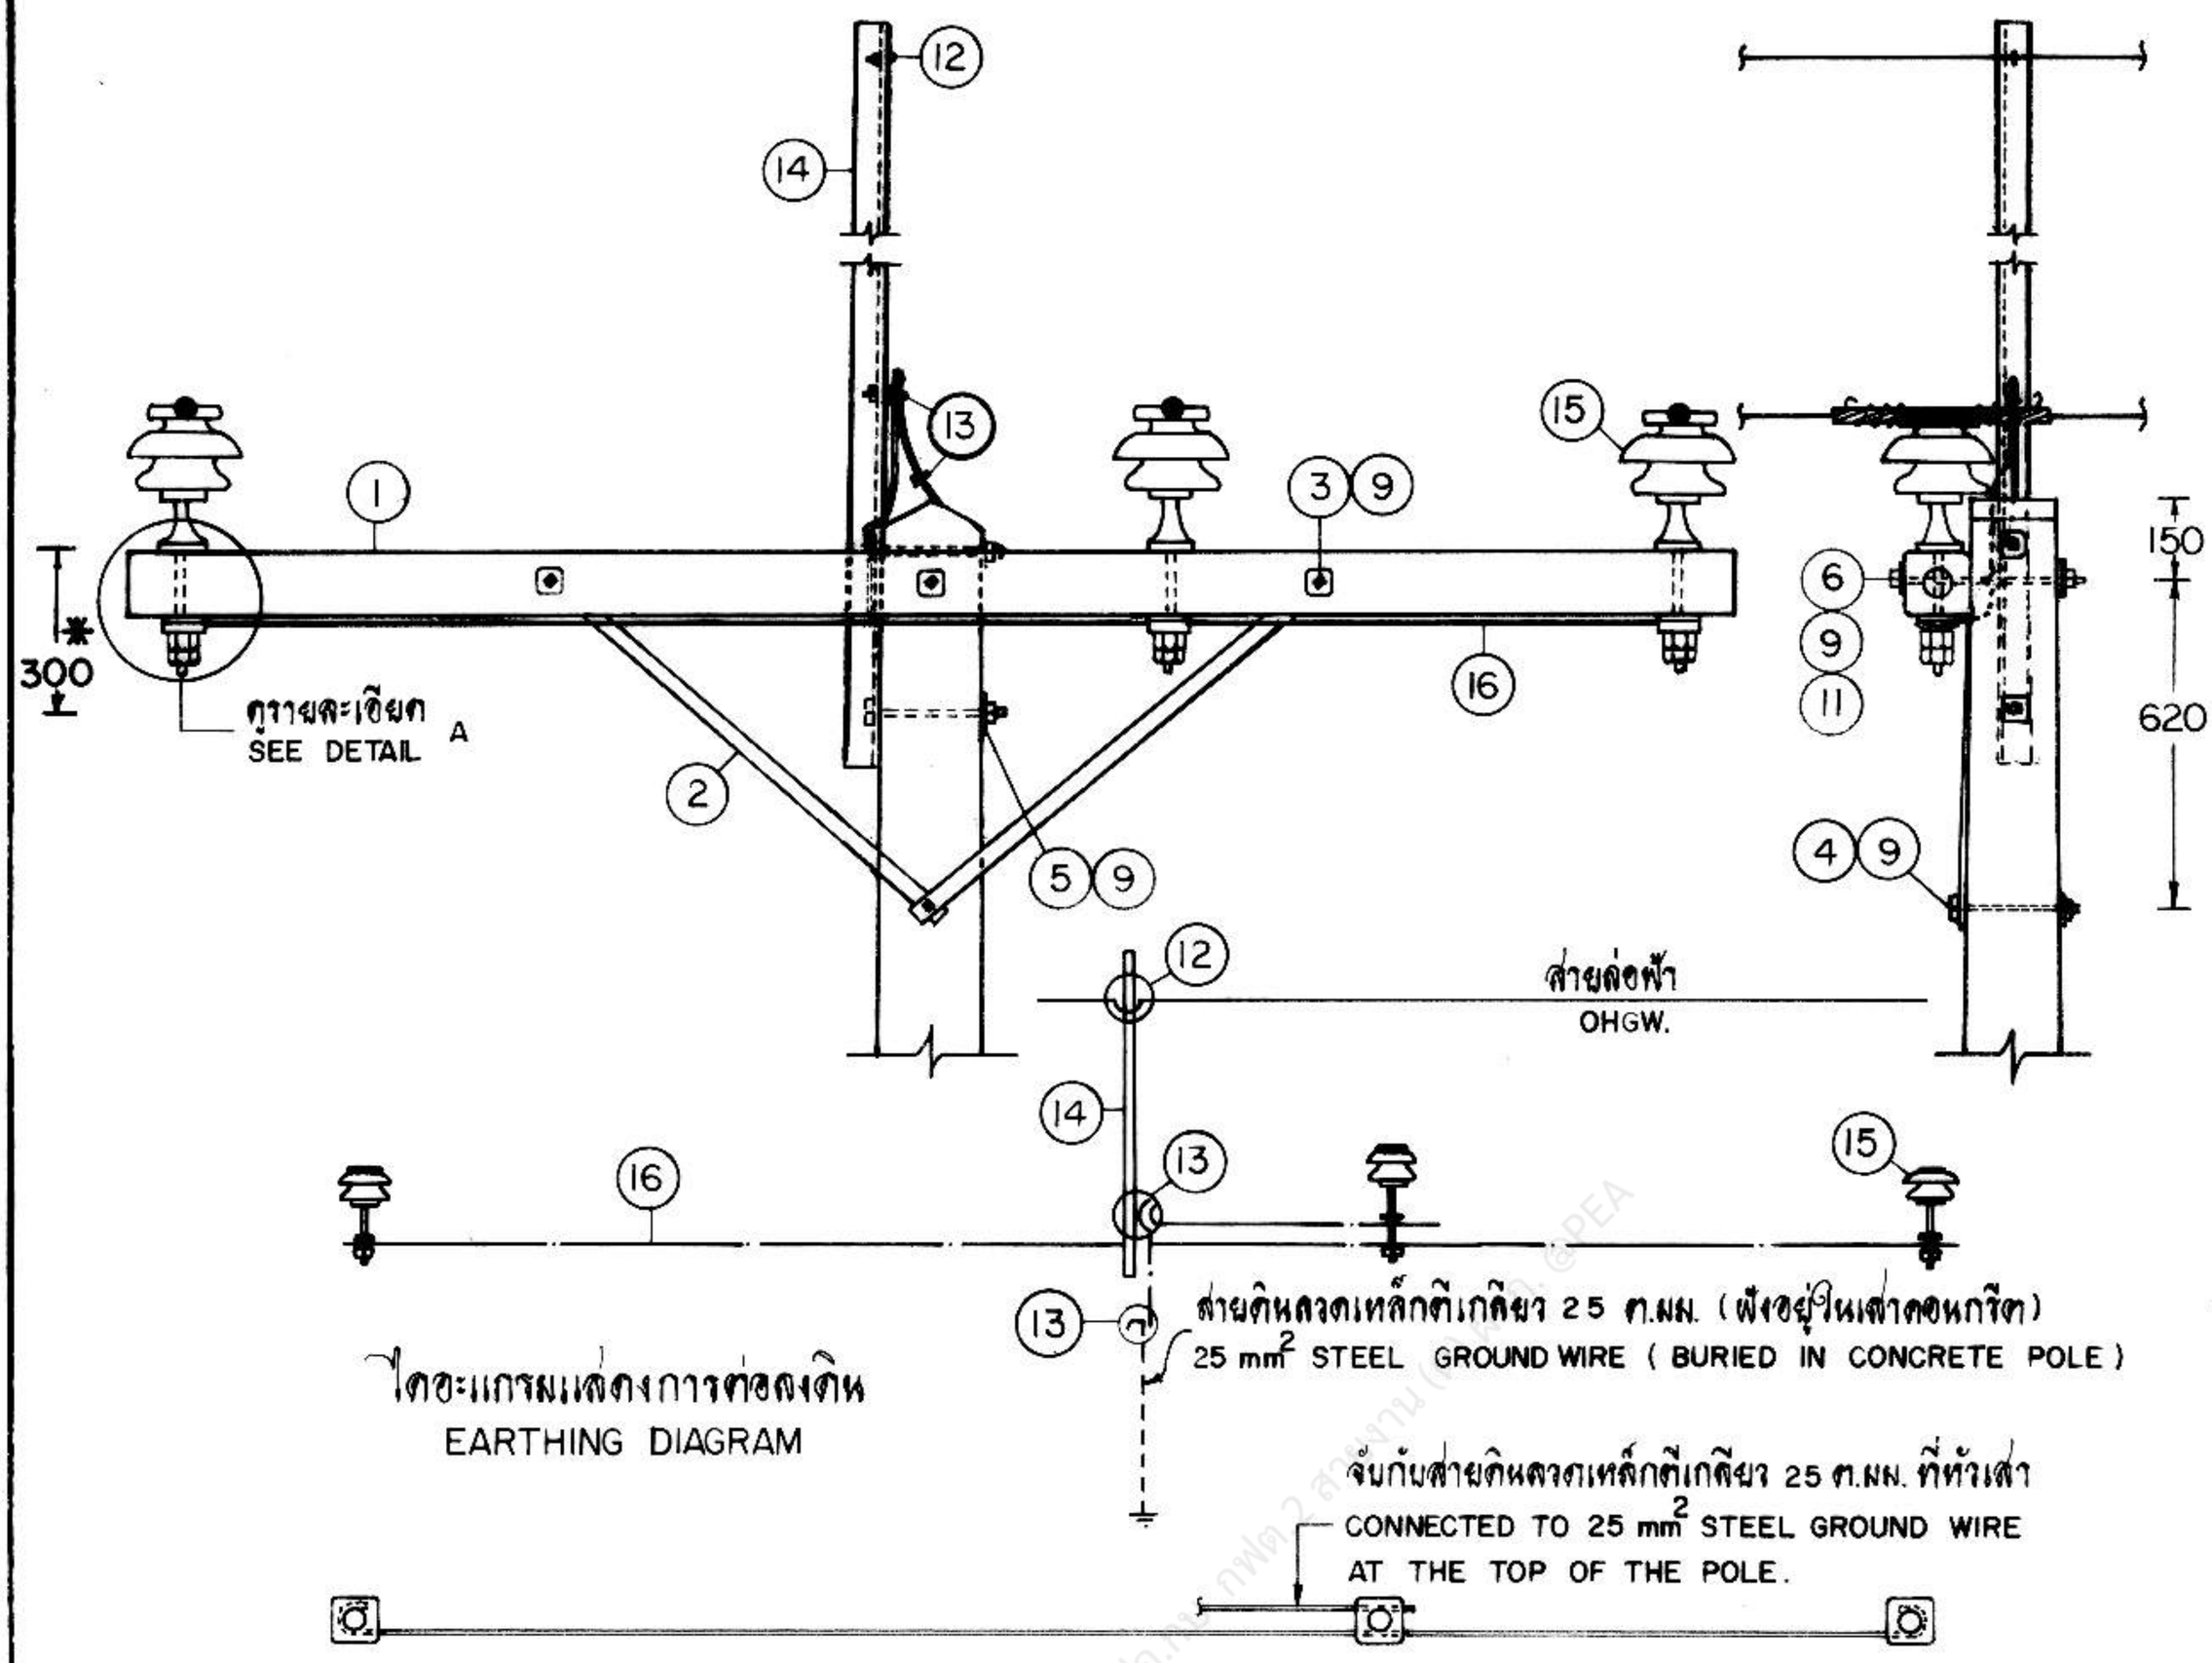

ไดอะแกรมแสดงการต่อลงดิน
EARTHING DIAGRAM

การโค้งดัดสายดินลวดเหล็กเส้นเดียว Ø 4 มม. ต่อระหว่างก้านลูกถ้วย ประกอบที่คอน คอร. สปัน
THE ARRANGEMENT OF Ø 4 mm GALVANIZED STEEL WIRE BOND BETWEEN INSULATOR PINS

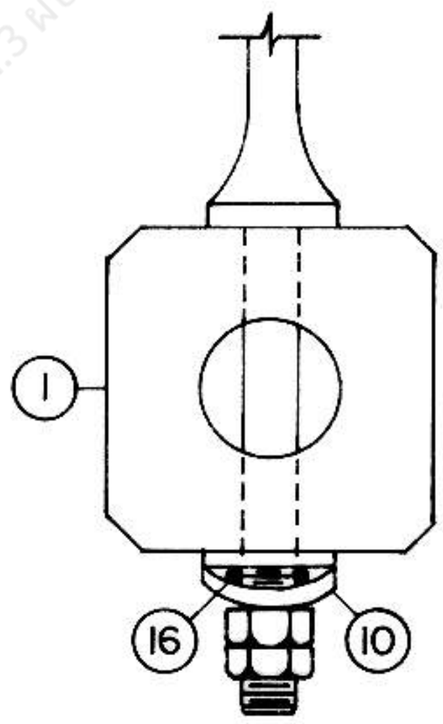


รายละเอียด A
DETAIL A

* กรณีที่ใช้เหล็กรัยสายล่อฟ้า วัสดุเลขที่ 01010006 ให้ใช้ระยะการยึดกับเสาเป็นระยะ 500 มม.
IN CASE OF USE OVERHEAD GROUND WIRE BAYONET MAT. NO. 01010006, THE DISTANCE FOR FITTING ON POLE SHALL BE 500 mm .


กองวิศวกรรมไฟฟ้าและเครื่องกล ฝ่ายวิศวกรรม	การไฟฟ้าส่วนภูมิภาค	ใช้แทนแบบ ถูกแทนโดยแบบ เขียนเสร็จวันที่ 22 มี.ค. 21 แก้แบบวันที่ 1 มิ.ย. 21 มิติเป็น มม. 2 ส.ค. 39 มาตราส่วน 1 : 25
ผู้เขียน ผู้สำรวจ วิศวกร หัวหน้าแผนก หัวหน้ากอง ผู้อำนวยการฝ่าย รองผู้ว่าการฝ่ายเทคนิค	ผู้ว่าการ การประกอบคอน คอร. สปัน กันเสาคอนกรีต ระยะ 33 kV ก สำหรับทางตรง 0°-5° SPUN PRESTRESSED CONCRETE CROSSARM ASSEMBLY 33 kV SYSTEM A TANGENT STRUCTURE 0°-5°	แบบเลขที่ SAI-015/21021 แผ่นที่ 1 ของจำนวน 3 แผ่น

การประกอบเลขที่ ASSEMBLY NO. 3803

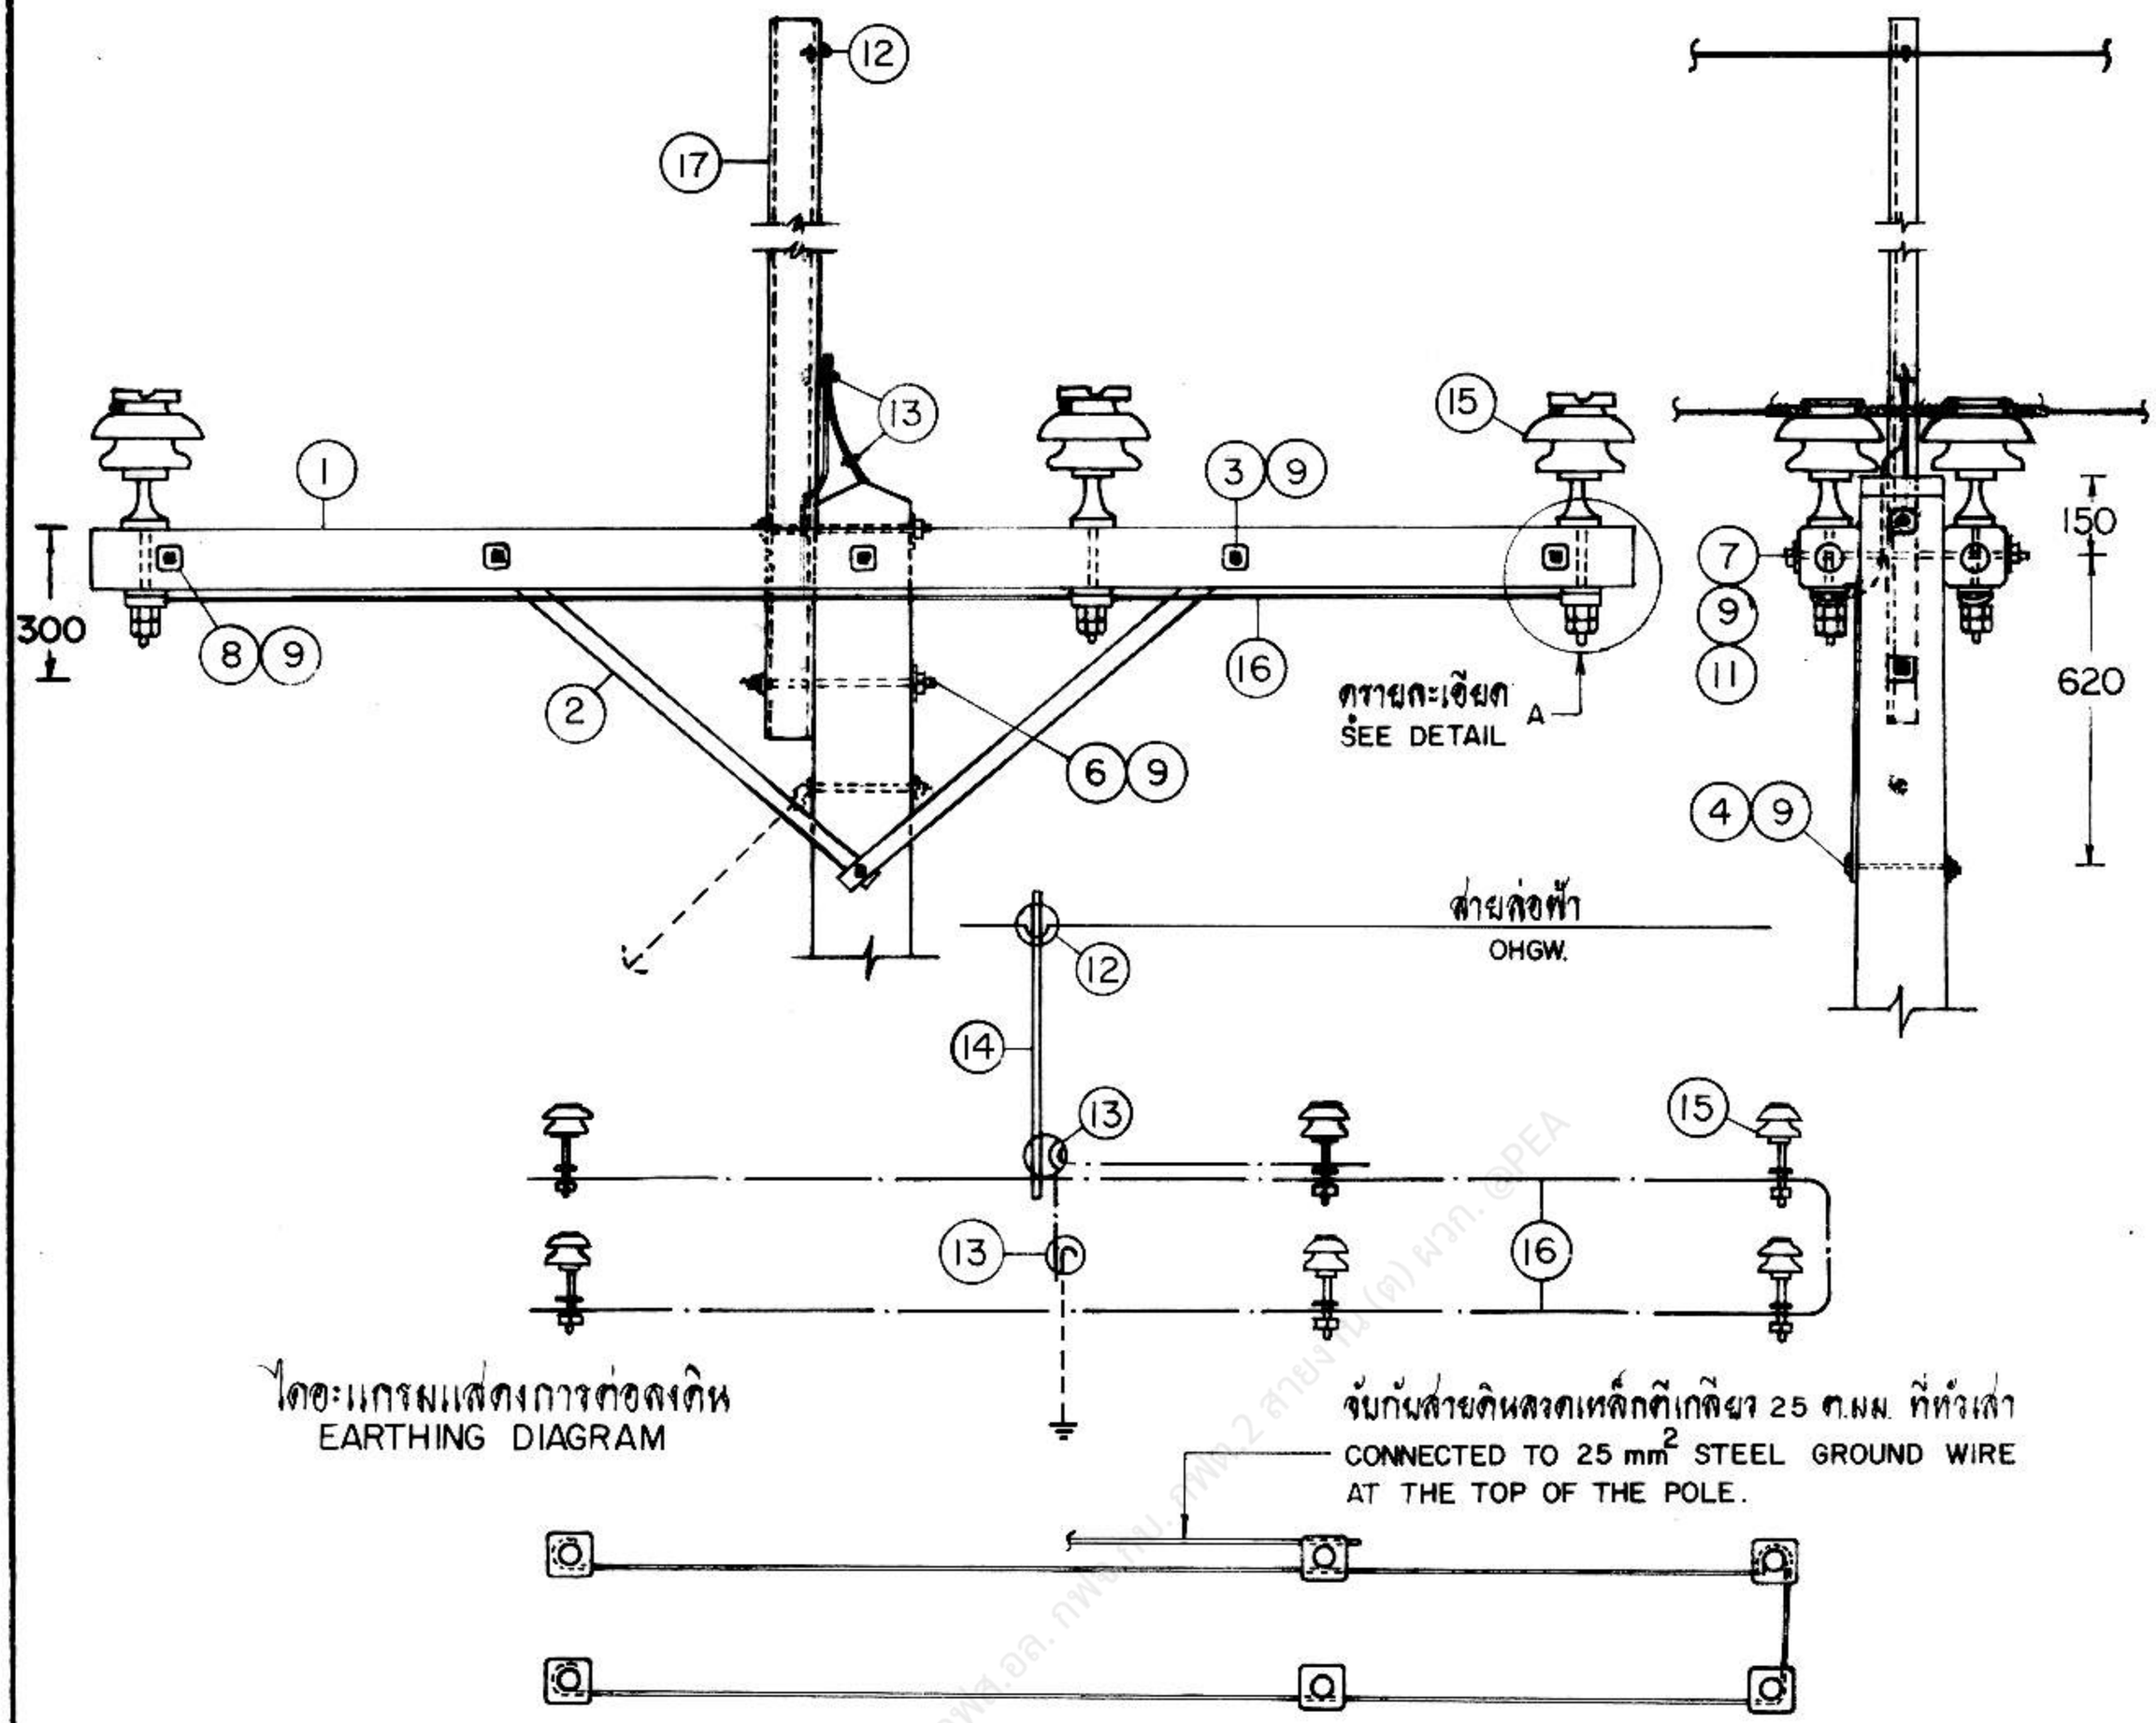

ไดอะแกรมแสดงการต่อลงดิน
EARTHING DIAGRAM

การโค้งดัดสายดินลวดเหล็กเส้นเดี่ยว Ø 4 มม. ต่อระหว่างก้านลูกถ้วย ประกอบที่คอน คอร. สปัน
THE ARRANGEMENT OF Ø 4 mm GALVANIZED STEEL WIRE BOND BETWEEN INSULATOR PINS

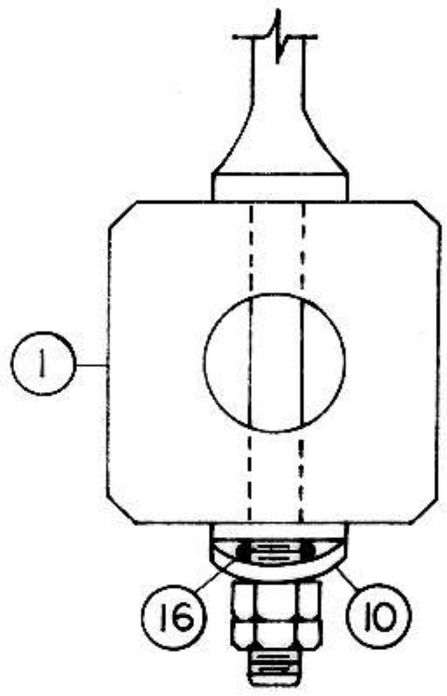

รายละเอียด A
DETAIL

กองวิศวกรรมไฟฟ้าและเครื่องกล ฝ่ายวิศวกรรม	การไฟฟ้าส่วนภูมิภาค	ใช้แทนแบบ ถูกแทนโดยแบบ เขียนเสร็จวันที่ 22 มิ.ค. 21 แก้แบบวันที่ 1 มิ.ย. 21 2 ส.ค. 39 มิติเป็น มม. มาตราส่วน 1:25
ผู้เขียน ผู้สำรวจ วิศวกร หัวหน้าแผนก หัวหน้ากอง ผู้อำนวยการฝ่าย รองผู้ว่าการฝ่ายเทคนิค	ผู้ว่าการ การประกอบคอน คอร. สปัน กันเสาคอนกรีต ระบบ 33 kV ฯ สำหรับทางโค้ง 5°-30° SPUN PRESTRESSED CONCRETE CROSSARM ASSEMBLY 33 kV SYSTEM B SMALL ANGLE STRUCTURE 5°-30°	แบบเลขที่ SA1-015/21021 แผ่นที่ 2 ของจำนวน 3 แผ่น

การประกอบเลขที่ ASSEMBLY NO. 3803

บัญชีวัสดุ
BILL OF MATERIAL

ลำดับที่ ITEM	รายละเอียด DESCRIPTION	จำนวน REQ'D ก/A	จำนวน REQ'D ข/B	วัสดุเลขที่ MAT. NO.
1	คอน คอร. สปัน ขนาด 120 X 120 X 3,000 มม. CROSSARM, SPUN, PRESTRESSED CONCRETE 120 X 120 X 3,000 mm	1	2	00110002
2	เหล็กประกับไม้คอน ขนาด 40 X 6 X 1,000 มม. BRACE, FLAT, FOR CROSSARM 40 X 6 X 1,000 mm	2	2	01200002
3	สลักเกลียว M 16 X 170 มม. BOLT, MACHINE, M 16 X 170 mm	2	2	01110201
4	สลักเกลียว M 16 X 200 มม. BOLT, MACHINE, M 16 X 200 mm	1	1	01110202
5	สลักเกลียว M 16 X 250 มม. BOLT, MACHINE, M 16 X 250 mm	2	-	01110203
6	สลักเกลียว M 16 X 350 มม. BOLT, MACHINE, M 16 X 350 mm	1	2	01110205
7	สลักเกลียว M 16 X 450 มม. BOLT, MACHINE, M 16 X 450 mm	-	1	01110207
8	สลักเกลียวตลอด M 16 X 450 มม. BOLT, DOUBLE ARMING M 16 X 450 mm	-	2	01120001
9	แหวนสี่เหลี่ยมแบน ขนาด 52X52X4.5 มม. รู Ø 18 มม. มอก. 258 WASHER, SQUARE, FLAT 52X52X4.5 mm HOLE Ø 18 mm TIS 258	7	15	01180100
10	แหวนสี่เหลี่ยมโค้ง ขนาด 60 X 60 X 5 มม. รู Ø 22 มม. WASHER, SQUARE, CURVED 60 X 60 X 5 mm HOLE Ø 22 mm	3	6	01180201
11	แหวนสปริง M 16 มอก.259 WASHER, LOCK M 16 TIS 258	1	1	01180301
12	กราวด์วายรัดสลัมป์ แบบ J 1152 GROUND WIRE CLAMP J 1152	1	1	01230205
13	ยูแคล้มป์ สลัก 1 ตัว M 8 (ไวร์ โร้ป คลิ้พ) CLAMP, SINGLE U-BOLT M 8 (WIRE ROPE CLIP)	2	2	01230000
14	เหล็กฉากรับสายล่อฟ้า 65 X 65 X 6 มม. ยาว 2,250 มม. OVERHEAD GROUND WIRE BAYONET 65 X 65 X 6 mm 2,250 mm LONG	1		01010003
15	ลูกถ้วยก้านตรง 33 kV แบบ ค (แบบ 56-3) มอก. 279 พร้อมก้าน INSULATOR, PIN TYPE, 33 kV, TYPE C (CLASS 56-3) TIS 279 COMP. WITH PIN	3	6	03000002 03100001
16	ลวดเหล็กกลม เส้นผ่าศูนย์กลาง 4 มม. เส้นเดียว (มอก. 71) น้ำหนักประมาณ 0.1 กก./ม. WIRE, STEEL, SOLID, DIAMETER 4 mm (TIS 71) WEIGHT 0.1 kg/m	4 ม. m	7 ม. m	01100000
17	เหล็กรูปรางน้ำ ขนาด 100 X 50 X 5 มม. ยาว 2,250 มม. STEEL, SHANNEL, 100 X 50 X 5 mm, 2,250 mm LONG	-	1	01000100

กองวิศวกรรมไฟฟ้าและเครื่องกล ฝ่ายวิศวกรรม	การไฟฟ้าส่วนภูมิภาค	ใช้แทนแบบ ถูกแทนโดยแบบ เขียนเสร็จวันที่ 22 มี.ค. 21 แก้แบบวันที่ 1 มิ.ย. 21 มิติเป็น 2 ส.ค. 39 มาตราส่วน
ผู้เขียน ผู้สำรวจ วิศวกร หัวหน้าแผนก หัวหน้ากอง ผู้อำนวยการฝ่าย	ผู้ว่าการ 24 มิ.ย. 21	
รองผู้ว่าการฝ่ายเทคนิค	การประกอบคอน คอร. สปัน กับเสาคอนกรีต ระบบ 33 kV SPUN PRESTRESSED CONCRETE CROSSARM ASSEMBLY 33 kV SYSTEM	แบบเลขที่ SAI-015/21021 แผ่นที่ 3 ของจำนวน 3 แผ่น