กิโลวัตต์-ชั่วโมงมิเตอร์ แผนวัดค่า 2 อัตรา

TWO-RATE TARIFF kWh-METER


FL 240 xdm 11.1 ybm 11.1 ybf6—1.5/6

การประกอบเลขที่ ASSEMBLY NO. 0533

สวิตช์เวลา

TIME SWITCH

KZB 1 ud

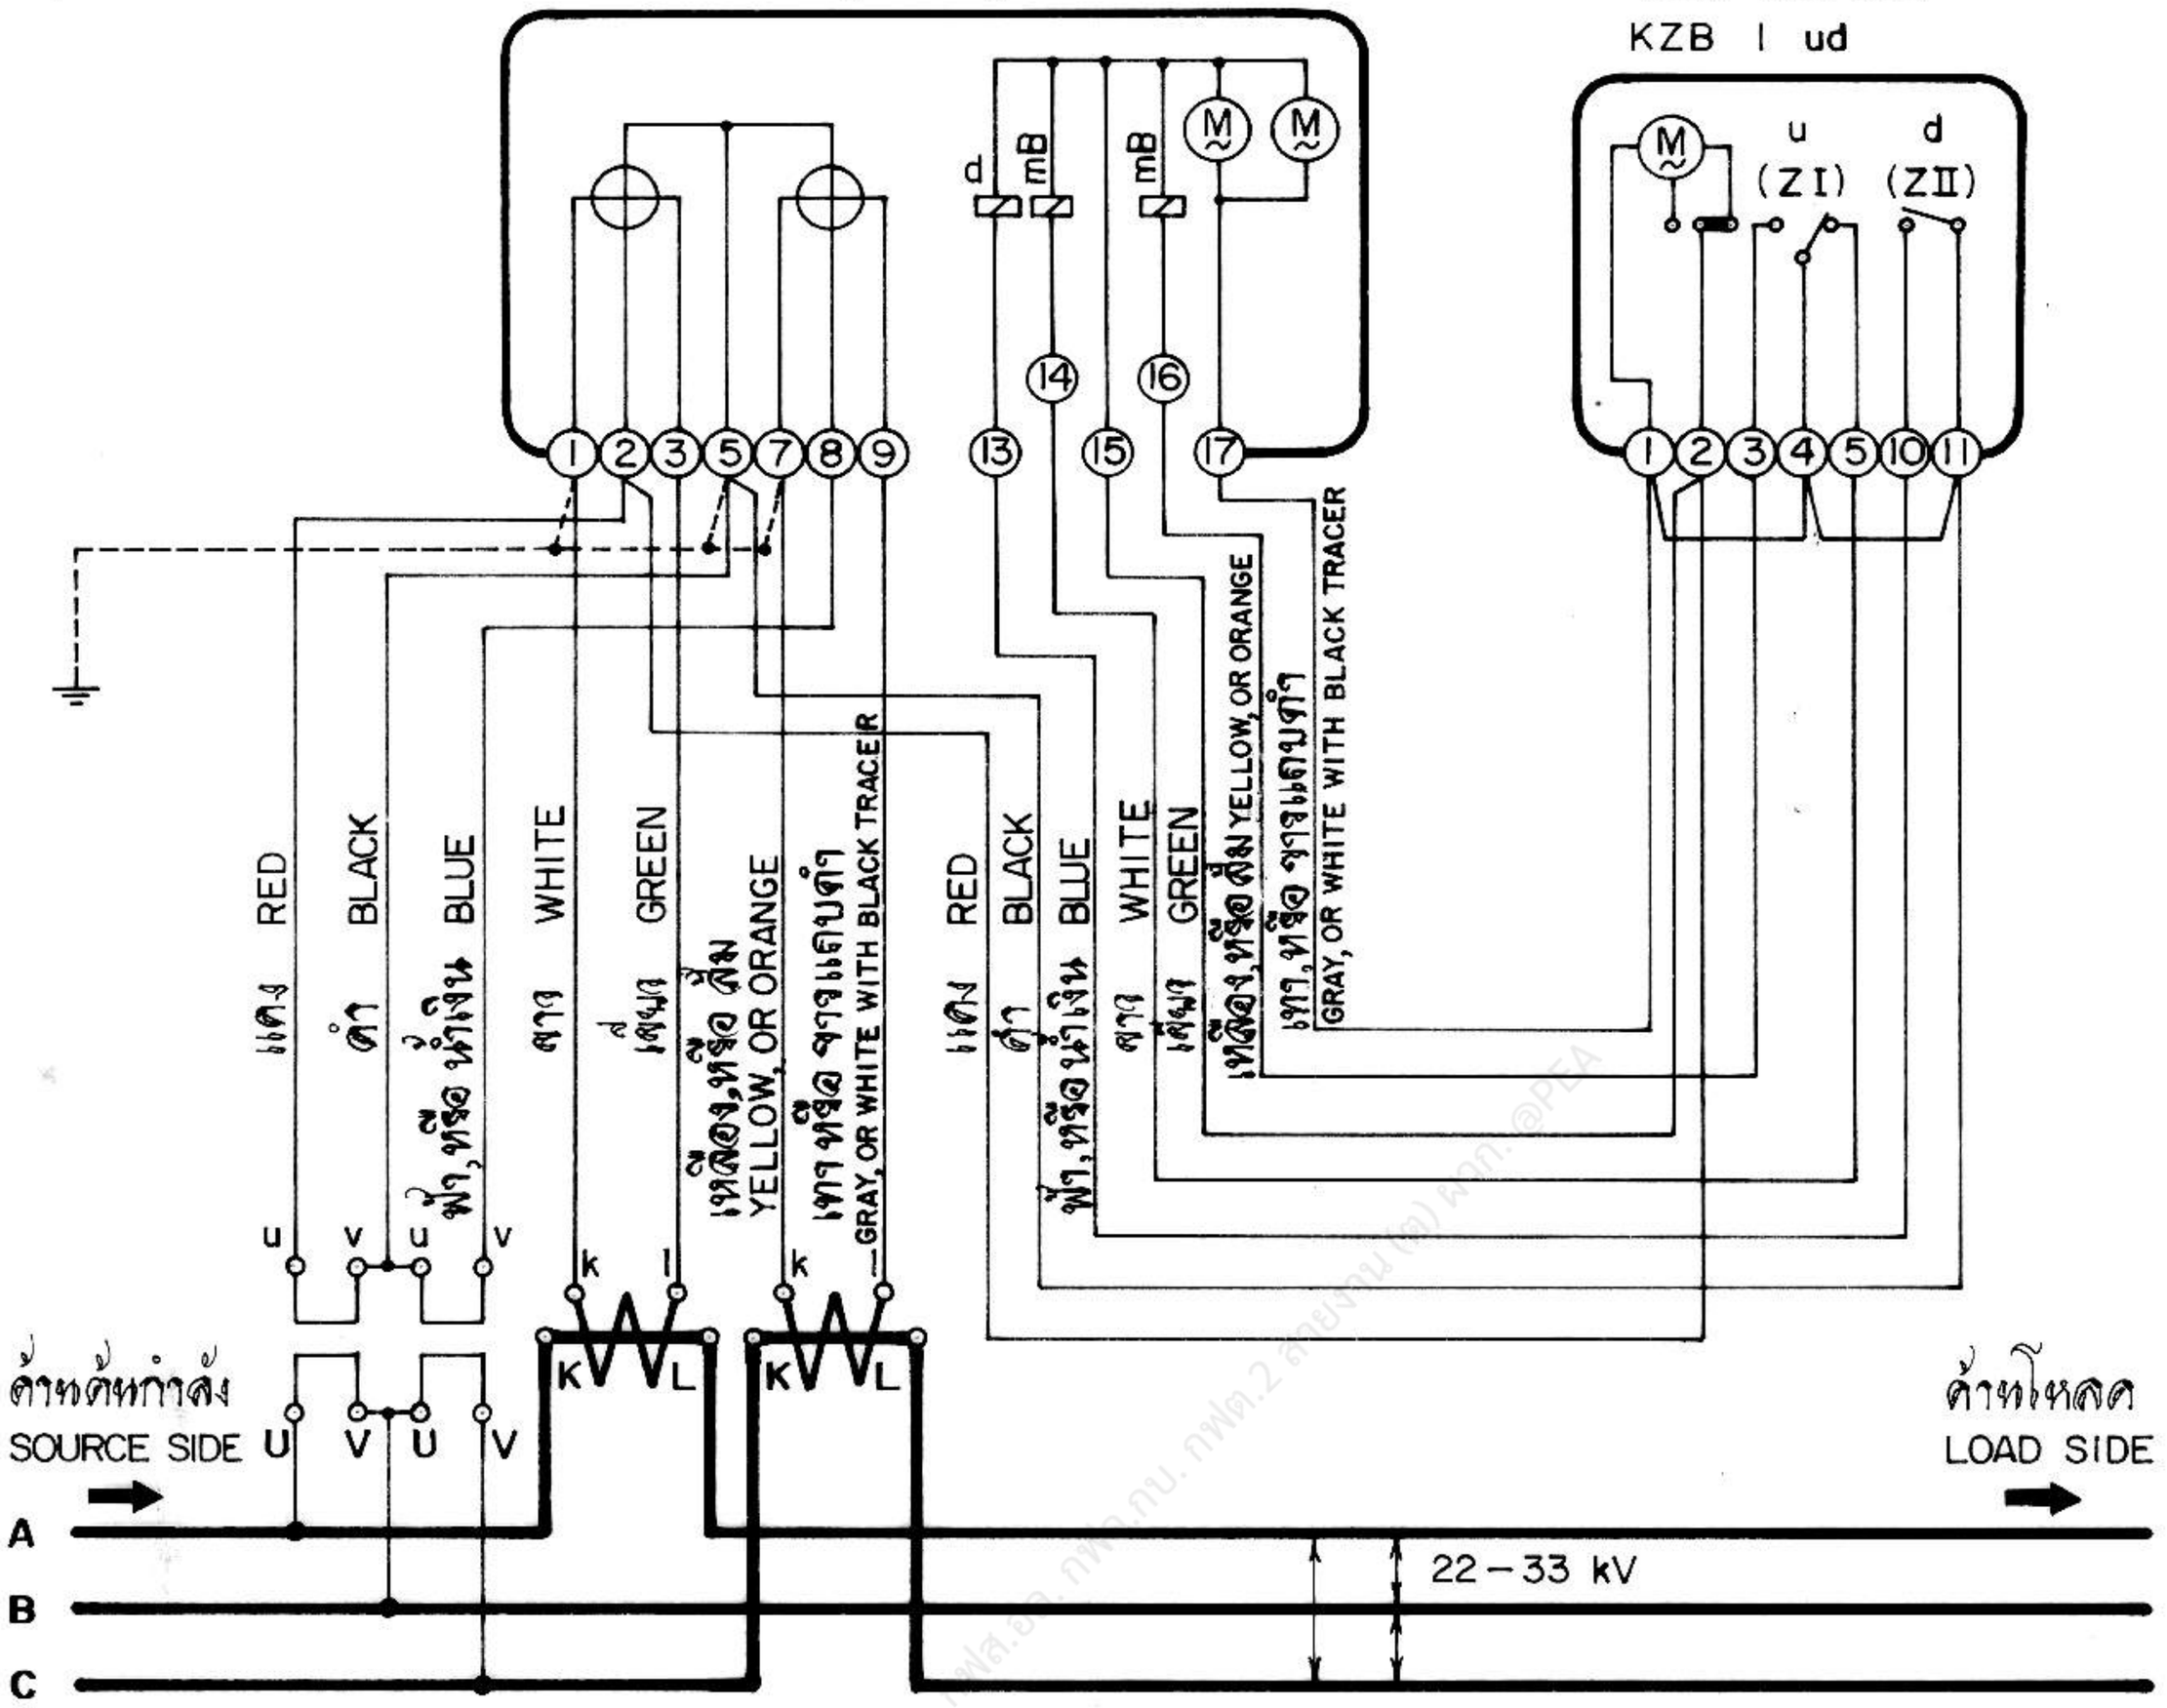

หมายเหตุ 1. การต่อสายตามแผนผังนี้ใช้สำหรับมิเตอร์ผลิตภัณฑ์ของ LANDIS & GYR LTD. เท่านั้น

2. ใช้สายคอนโทรลเคเบิล 7X2.5 ต.มม. (รัศดุเลขที่ 4275) เป็นสายต่อเข้ามิเตอร์ และ สวิตช์เวลา

NOTES 1. THIS CONNECTION DIAGRAM ARE ONLY FOR METER MANUFACTURED BY LANDIS & GYR LTD..

2. USE 7X2.5 mm^2. CONTROL CABLE FOR METER AND TIME SWITCH CONNECTION.

แผนอ้างอิง REFERENCE DRAWING		แผนเลขที่ DWG. NO.	การประกอบเลขที่ ASSEMBLY NO.
1.	การต่อลงดิน ระบบแรงสูง และ แรงต่ำ แผ่นที่ 15 และ 17 H.T. AND L.T. EARTHING SYSTEM, SHEET NO. 15 AND 17	S02-015/23039	9701
2.	วิธีการอ่าน และหาค่ากิโลวัตต์-ชั่วโมง และดีมานด์สูงสุด METHOD OF KILOWATT-HOUR AND MAXIMUM DEMAND READING	SAI-015/25001	0529

กองวิศวกรรมไฟฟ้าและเครื่องกล ฝ่ายวิศวกรรม	การไฟฟ้าส่วนภูมิภาค	ใช้แทนแผน ถูกแทนโดยแผน เขียนแบบเสร็จวันที่ 15 ก.พ. 28 แก้แผนวันที่ 5 ก.ย. 34
ผู้เขียน ผู้สังเกตรอย วิศวกร หัวหน้าแผนก ผู้อำนวยการกอง ผู้อำนวยการฝ่าย	ผู้จ่าการ 8 ส.ค. 28	มิติเป็น มาตราส่วน
ของผู้จ่าการฝ่ายเทคนิค	แผนผังการต่อมิเตอร์แรงสูง 3 เฟส 3 สาย แผนวัดค่า 2 อัตรา ระบบ 22 — 33 kV CONNECTION DIAGRAM OF 3-PHASE, 3-WIRES, H.T. METER TWO-RATE TARIFF, 22—33 kV SYSTEM	แผนเลขที่ SAI-015/28005 แผ่นที่ 1 ของจำนวน 1 แผ่น