การประกอบเลขที่
ASSEMBLY NO. 5255A

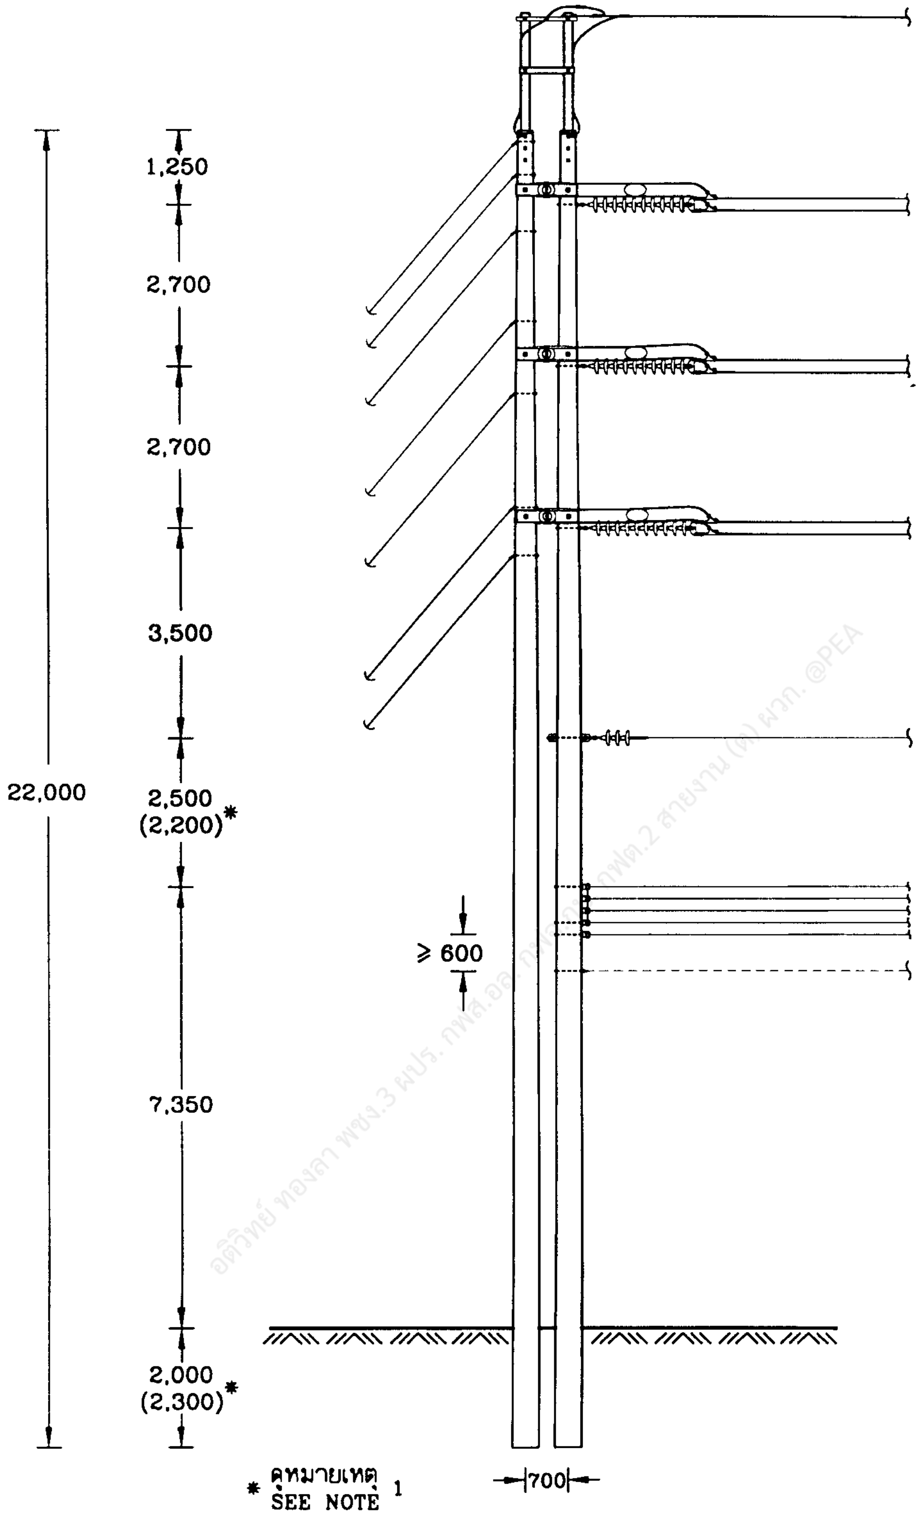

* ดูหมายเหตุ
SEE NOTE 1

อติวิทย์ ทองลา พชง.3 ผปร. กฟส.อล กฟต.2 สายงาน (ต) ผวก. @PEA

กองมาตรฐานระบบไฟฟ้า
ฝ่ายมาตรฐานและความปลอดภัย

การไฟฟ้าส่วนภูมิภาค

ผู้เขียน ...สมชาย...........
ผู้สำรวจ ....
วิศวกร ....
หัวหน้าแผนก ....
ผู้อำนวยการกอง ....
ผู้อำนวยการฝ่าย ....

รองผู้ว่าการฝ่ายวางแผนและพัฒนาระบบไฟฟ้า
....

ผู้ว่าการ ....

115 kV วงจรเดี่ยว สายไฟคู่
เสาคู่ (ชนิดมีกราวด์เพลทในเสา) สำหรับทางโค้ง 90
แบบ SD-LA-2

27 ส.ค. 2547

115 kV SINGLE CIRCUIT DOUBLE CONDUCTOR
DOUBLE POLE (WITH GROUND PLATE IN POLE), 90° ANGLE STRUCTURE
TYPE SD-LA-2

ใช้แทนแบบ ....
ถูกแทนโดยแบบ ....
เขียนเสร็จวันที่ 2 มิ.ย. 2547
แก้แบบวันที่ ....
มิติเป็น ..มิลลิเมตร........
มาตราส่วน ..1:125........
แบบเลขที่ SA1-015/47012
แผ่นที่ 1 ของจำนวน 4 แผ่น

27 ส.ค. 2547

การประกอบเลขที่ 5 2 5 5 A
ASSEMBLY NO.

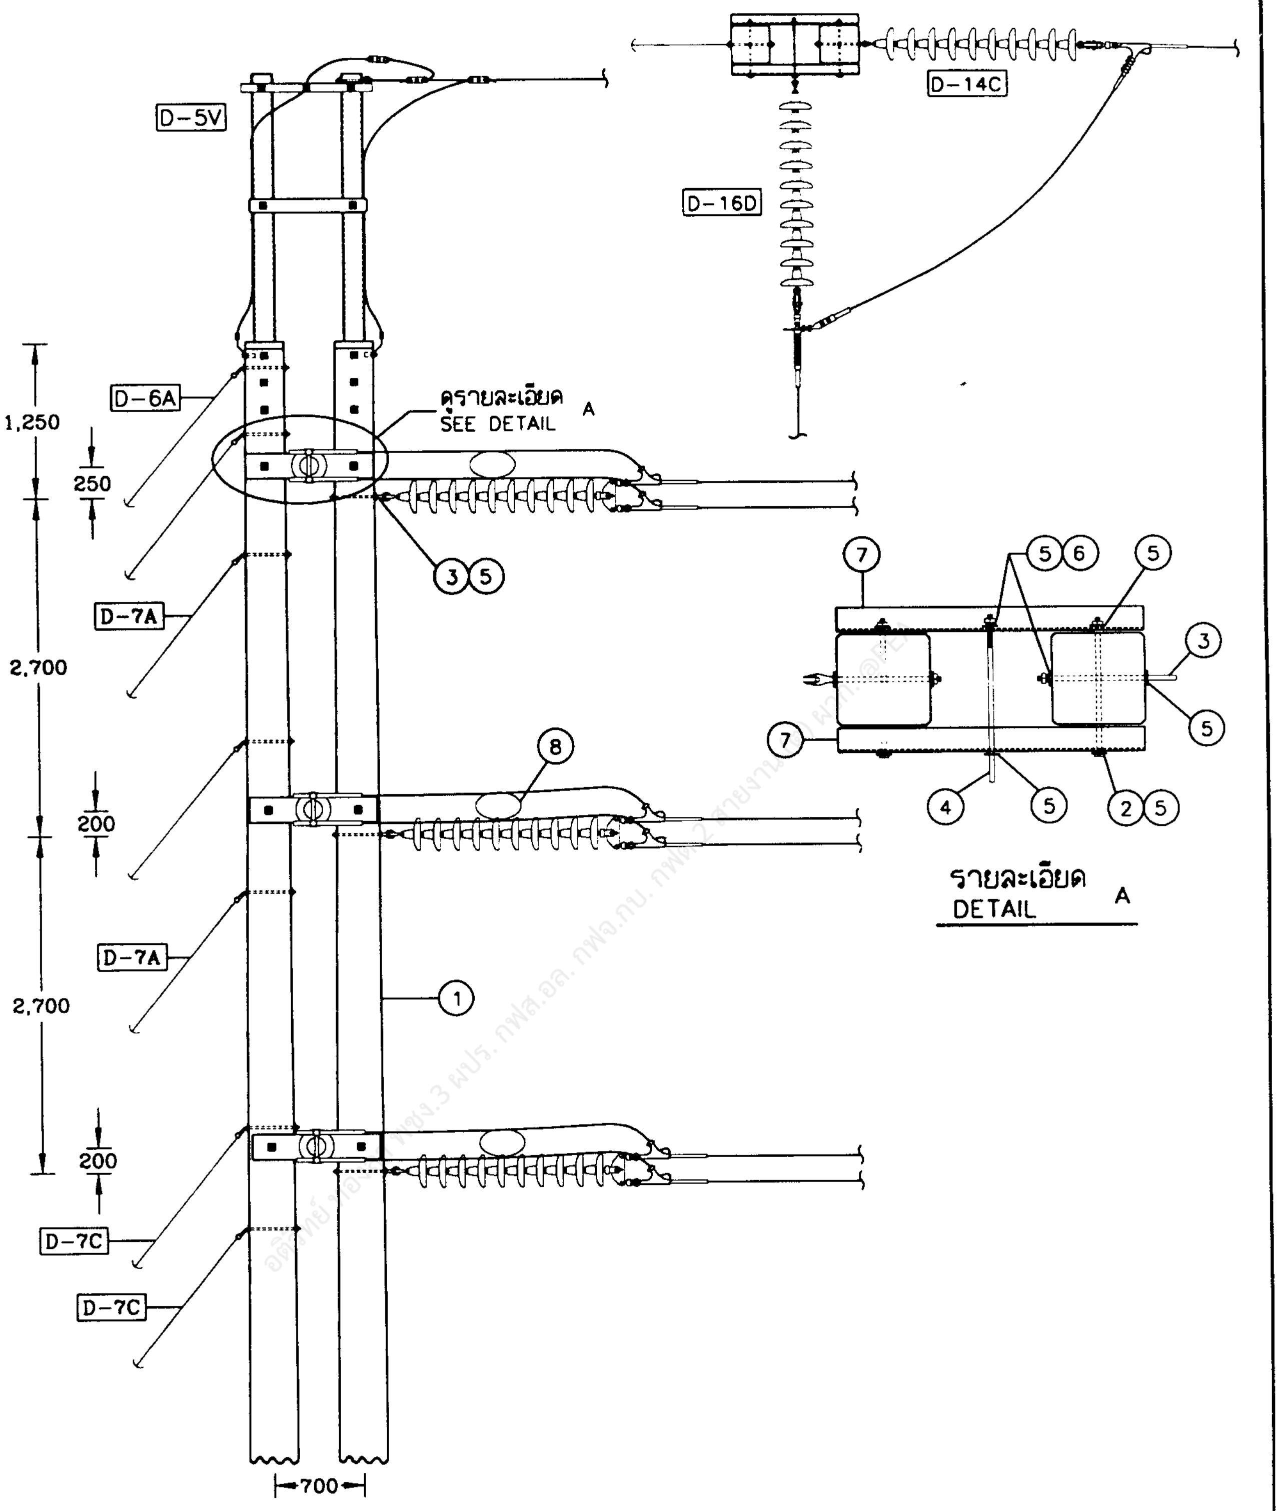

กองมาตรฐานระบบไฟฟ้า
ฝ่ายมาตรฐานและความปลอดภัย

การไฟฟ้าส่วนภูมิภาค

ผู้เขียน สมชาย
ผู้สำรวจ
วิศวกร
หัวหน้าแผนก
ผู้อำนวยการกอง
ผู้อำนวยการฝ่าย

ผู้ว่าการ

รองผู้ว่าการฝ่ายวางแผนและพัฒนาระบบไฟฟ้า

115 kV วงจรเดี่ยว สายไฟฟ้า 27 ส.ค. 2547
เสาคู่ (ชนิดมีกราวด์เพลทในเสา) สำหรับทางโค้ง 90°
แบบ SD-LA-2

115 kV SINGLE CIRCUIT DOUBLE CONDUCTOR
DOUBLE POLE (WITH GROUND PLATE IN POLE), 90° ANGLE STRUCTURE
TYPE SD-LA-2

ใช้แทนแบบ
ถูกแทนโดยแบบ
เขียนเสร็จวันที่ 2 มิ.ย. 2547
แก้แบบวันที่
มิติเป็น มิลลิเมตร
มาตราส่วน 1:60

แบบเลขที่ SA1-015/47012
แผ่นที่ 2 ของจำนวน 4 แผ่น

2 [illegible] 2547

การประกอบเลขที่ 5256A
ASSEMBLY NO. 5256A

บัญชีวัสดุ
BILL OF MATERIAL

ลำดับที่ ITEM	รายละเอียด DESCRIPTION	จำนวน REQ.D	วัสดุเลขที่ MAT. NO.
1	เสา คอร. ยาว 22.00 ม. ชนิดมีกราวด์เพลทในเสา POLE, CONCRETE, 22.00 m LONG, WITH GROUND PLATE IN POLE	2	00010015
2	สลักเกลียว M 20x450 มม. BOLT, MACHINE, M 20x450 mm	6	01110302
3	สลักห่วงโอแวล M 20x350 มม. BOLT, OVAL EYE, M 20x350 mm	3	01150100
4	สลักห่วงโอแวล M 20x450 มม. BOLT, OVAL EYE, M 20x450 mm	3	01150101
5	แหวนสี่เหลี่ยมแบน 62x62x6 มม. รู⌀22 มม. มอก.258 WASHER, SQUARE, FLAT, 62x62x6 mm, HOLE ⌀22 mm, TIS 258	24	01180101
6	แหวนสปริง M 20 มอก. 259 WASHER, LOCK, M 20, TIS 259	6	01180302
7	เหล็กรูปรางน้ำ 200x80x7.5 มม. ยาว 1,000 มม. STEEL CHANNEL, 200x80x7.5 mm, 1,000 mm LONG	6	01000400
8	ปริฟอร์มแยกสาย SPACER, HELICAL ROD, PREFORMED	3	02240000
	รายละเอียด DETAIL		
D-14C	การประกอบลูกถ้วยแขวน SUSPENSION INSULATOR ASSEMBLY	3	
D-16D	การประกอบลูกถ้วยแขวน SUSPENSION INSULATOR ASSEMBLY	3	
** D-5V	การประกอบสายล่อฟ้า OVERHEAD GROUND WIRE ASSEMBLY	1	
D-6A	การประกอบสายยึดโยงลวดเหล็กตีเกลียว 50 ต.มม. STEEL STRANDED WIRE 50 mm^2 GUY ASSEMBLY	1	
D-7A	การประกอบสายยึดโยงลวดเหล็กตีเกลียว 95 ต.มม. STEEL STRANDED WIRE 95 mm^2 GUY ASSEMBLY	4	
D-7C	การประกอบสายยึดโยงลวดเหล็กตีเกลียว 95 ต.มม. STEEL STRANDED WIRE 95 mm^2 GUY ASSEMBLY	2	
D-9A	สมอบกคอนกรีต CONCRETE ANCHOR	1	
D-10B	ฐานรากเสา POLE FOUNDATION	1	
D-25	การต่อลงดิน GROUNDING	1	

กฟจ.กบ. กฟต.2 สายงาน (ก) ผวก. @PEA

กองมาตรฐานระบบไฟฟ้า
ฝ่ายมาตรฐานและความปลอดภัย

ผู้เขียน สมชาย
ผู้สำรวจ
วิศวกร
หัวหน้าแผนก
ผู้อำนวยการกอง
ผู้อำนวยการฝ่าย

รองผู้ว่าการฝ่ายวางแผนและพัฒนาระบบไฟฟ้า

การไฟฟ้าส่วนภูมิภาค

ผู้ว่าการ

27 ส.ค. 2547

115 kV วงจรเดี่ยว สายไฟฟ้าคู่
เสาคู่ (ชนิดมีกราวด์เพลทในเสา) สำหรับทางโค้ง 90°
แบบ SD-LA-2

115 kV SINGLE CIRCUIT DOUBLE CONDUCTOR
DOUBLE POLE (WITH GROUND PLATE IN POLE), 90° ANGLE STRUCTURE
TYPE SD-LA-2

ใช้แทนแบบ
ถูกแทนโดยแบบ
เขียนเสร็จวันที่ 2 มิ.ย. 2547
แก้แบบวันที่
มิติเป็น
มาตราส่วน

แบบเลขที่ SA1-015/47012
แผ่นที่ 3 ของจำนวน 4 แผ่น

27 ส.ค. 2547

การประกอบเลขที่ ASSEMBLY NO.	5255A

หมายเหตุ

1.* กรณีก่อสร้างในพื้นที่เขตทางหลวง ให้ใช้ค่าระยะห่างตามแนวดิ่งในวงเล็บ โดยดูรายละเอียดเพิ่มเติมในแบบเลขที่ SA1-015/43012 (การประกอบเลขที่ 5687)
2.** กรณีไม่มีสายยึดโยง ให้ใช้การประกอบสายล่อฟ้า แบบ D-5U แทน
3. ระยะห่างระหว่างช่วงเสาของโครงสร้างสายส่ง 115 kV โครงสร้างเสาสำหรับทางโค้ง 90° ให้ดูแบบเลขที่ SA1-015/47009 (การประกอบเลขที่ 5161)
4. กรณีมีการพาดสายต่อไป เป็นลักษณะโครงสร้างเสาสำหรับแยกสาย ให้ใช้ระยะห่างระหว่างช่วงเสาของโครงสร้างสายส่ง 115 kV โครงสร้างเสาสำหรับแยกสาย แบบเลขที่ SA1-015/47010 (การประกอบเลขที่ 5162)

NOTES

1.* IN CASE OF CONSTRUCTION IN HIGHWAY AREA, USE A VERTICAL CLEARANCE VALUE IN THE PARENTHESIS. FOR ADDITIONAL DETAIL, SEE DWG NO. SA1-015/43012 (ASSEMBLY NO. 5687) .
2.** IN CASE OF NO GUY, USE OVERHEAD GROUND WIRE ASSEMBLY TYPE D-5U .
3. SPAN LENGTHS FOR 115 kV CONSTRUCTION STRUCTURE, 90° ANGLE STRUCTURE, SEE DWG. NO. SA1-015/47009 (ASSEMBLY NO. 5161) .
4. IN CASE OF CONTINUATION STRINGING AS TAP LINE STRUCTURE, USE THE SPAN LENGTHS FOR 115 kV CONSTRUCTION STRUCTURE, TAP LINE STRUCTURE, DWG.NO. SA1-015/47010 (ASSEMBLY NO. 5162) .

อดิวิทย์ ทองลา พชง.3 ผปร. กฟส.อล. [illegible] กบ. กฟภ.2 สายงาน(ต) ผวก. @PEA

กองมาตรฐานระบบไฟฟ้า ฝ่ายมาตรฐานและความปลอดภัย	การไฟฟ้าส่วนภูมิภาค	ใช้แทนแบบ .... ถูกแทนโดยแบบ ....
ผู้เขียน ...สมชาย.......... ผู้สำรวจ.................. วิศวกร.................. หัวหน้าแผนก.............. ผู้อำนวยการกอง........... ผู้อำนวยการฝ่าย..........	ผู้ว่าการ................................	เขียนเสร็จวันที่ 2 มิ.ย. 2547 แก้แบบวันที่ ....
	115 kV วงจรเดี่ยว สายไฟฟ้าคู่ 27 ส.ค. 2547 เสาคู่ (ชนิดมีกราวด์เพลทในเสา) สำหรับทางโค้ง 90° แบบ SD-LA-2	มิติเป็น.................. มาตราส่วน..............
รองผู้ว่าการฝ่ายวางแผนและพัฒนาระบบไฟฟ้า	115 kV SINGLE CIRCUIT DOUBLE CONDUCTOR DOUBLE POLE (WITH GROUND PLATE IN POLE), 90° ANGLE STRUCTURE TYPE SD-LA-2	แบบเลขที่ SA1-015/47012 แผ่นที่ 4 ของจำนวน 4 แผ่น

27 ส.ค. 2547