


การประกอบเลขที่ 3214
ASSEMBLY NO.

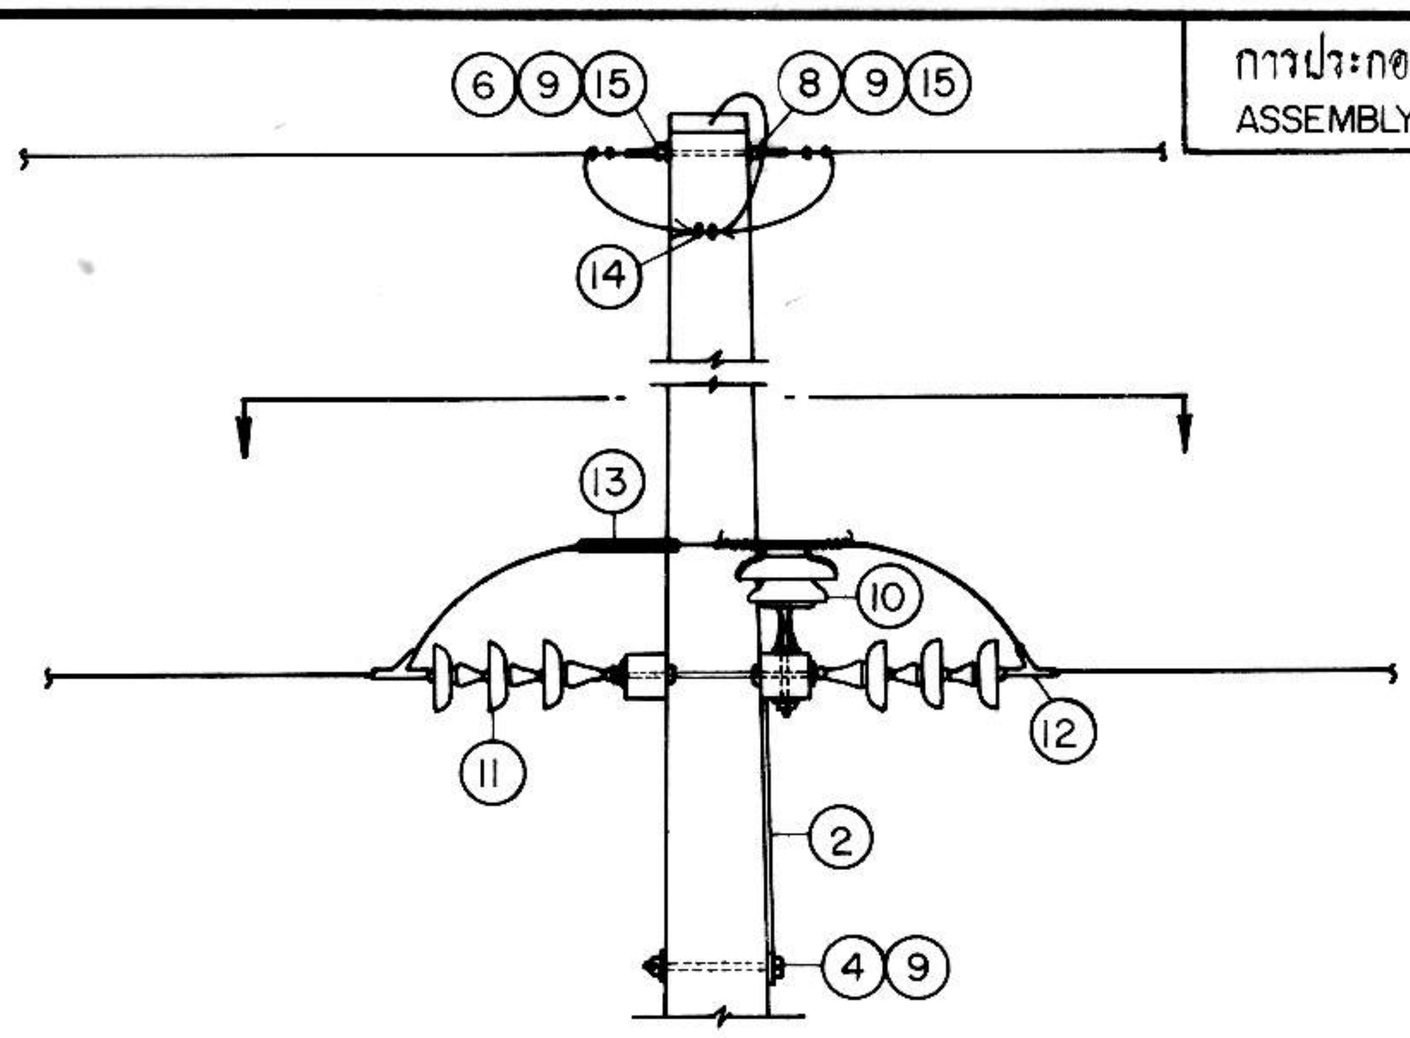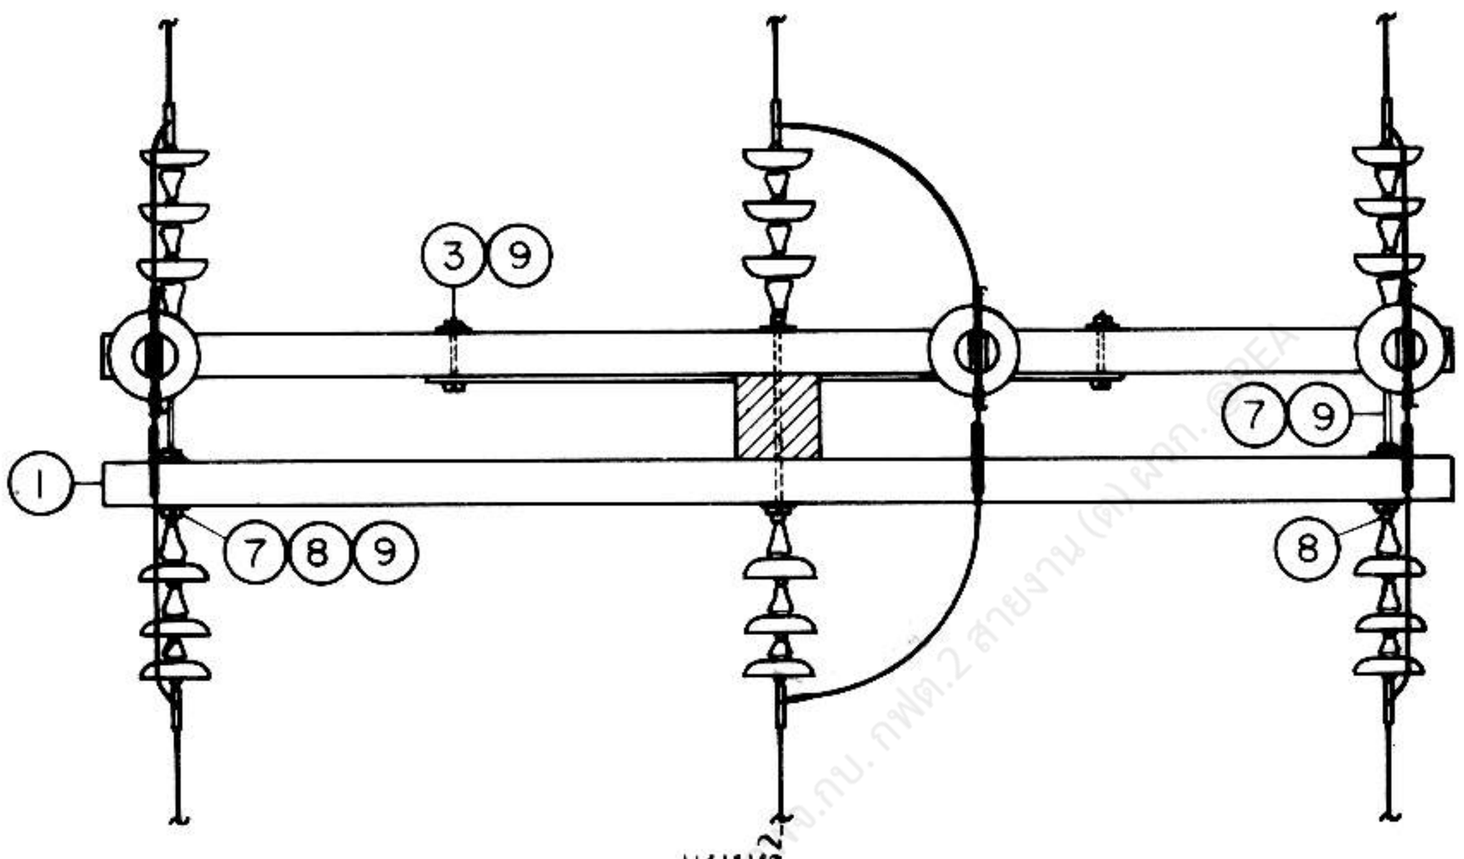


แบบที่ 1
TYPE

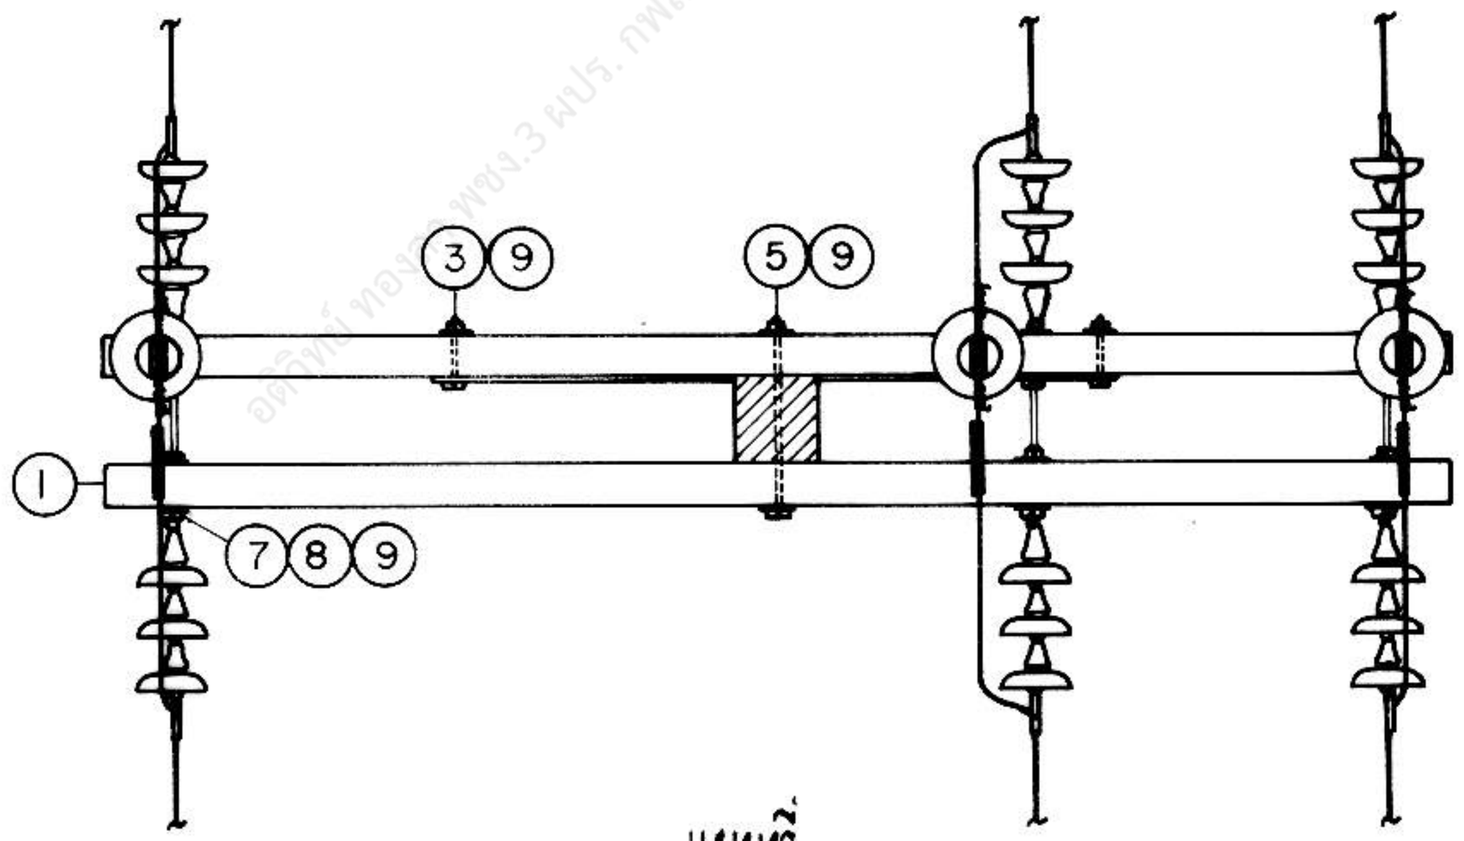


แบบที่ 2
TYPE

| | | |
|---|---|---|
| กองวิศวกรรมไฟฟ้าและเครื่องกล<br>ฝ่ายวิศวกรรม | การไฟฟ้าส่วนภูมิภาค | ใช้แทนแบบ<br>ถูกแทนโดยแบบ<br>เขียนเสร็จวันที่ 20 ก.พ. 21<br>แก้แบบวันที่ |
| ผู้เขียน<br>ผู้สำรวจ<br>วิศวกร<br>หัวหน้าแผนก<br>หัวหน้ากอง<br>ผู้อำนวยการฝ่าย | ผู้ว่าการ<br>27 ก.พ. 21 | มิติเป็น มม.<br>มาตราส่วน 1 : 30 |
| รองผู้ว่าการฝ่ายเทคนิค | การติดตั้งอุปกรณ์ที่เสา เข้าปลายสายต่องข้าง ระยะ 33 kV<br>( เสาคอนกรีต 14 ม. )<br>33 kV DOUBLE DEADEND INSTALLATION<br>( 14 m CONCRETE POLE ) | แบบเลขที่ SAI-015/21012<br>แผ่นที่ 1 ของจำนวน 2 แผ่น |

การประกอบเลขที่ ASSEMBLY NO. 3214

## บัญชีวัสดุ
## BILL OF MATERIAL

| ลำดับที่ ITEM | รายละเอียด DESCRIPTION | จำนวน REQ'D 1 | จำนวน REQ'D 2 | วัสดุเลขที่ MAT. NO. |
|---|---|---|---|---|
| 1 | ไม้คอนสายแรงสูง 100 X 120 X 3,000 มม.<br>CROSSARM, WOOD, H.T. 100 X 120 X 3,000 mm | 2 | 2 | 00100003<br>(0101) |
| 2 | เหล็กประกับไม้คอน 40 X 6 X 1,000 มม.<br>BRACE, FLAT, FOR CROSSARM 40 X 6 X 1,000 mm | 2 | 2 | 01200002<br>(0121) |
| 3 | สลักเกลียว M 16 X 130 มม.<br>BOLT, MACHINE, M 16 X 130 mm | 2 | 2 | 01110200<br>(0220) |
| 4 | สลักเกลียว M 16 X 250 มม.<br>BOLT, MACHINE, M 16 X 250 mm | 1 | 1 | 01110203<br>(0223) |
| 5 | สลักเกลียว M 16 X 450 มม.<br>BOLT, MACHINE, M 16 X 450 mm | — | 1 | 01110207<br>(0227) |
| 6 | สลักเกลียวห่วงกลม M 16 X 200 มม.<br>BOLT, ROUND EYE M 16 X 200 mm | 1 | 1 | 01140001<br>(0253) |
| 7 | สลักเกลียวห่วงกลม M 16 X 450 มม.<br>BOLT, DOUBLE ARMING, ROUND EYE, M 16 X 450 mm | 3 | 3 | 01130001<br>(0247) |
| 8 | น๊อทรูปห่วง M 16 DIN 582<br>NUT, EYE M 16 DIN 582 | 4 | 4 | 01180001<br>(0345) |
| 9 | แหวนสี่เหลี่ยมแบน 52X52X4.5 มม. รู Ø 18 มม. มอก. 258<br>WASHER, SQUARE, FLAT 52X52X4.5 mm HOLE Ø 18 mm TIS 258 | 15 | 19 | 01180100<br>(0355) |
| 10 | ลูกถ้วยก้านตรง 33 kV มอก. 279 แบบ ค (แบบ 56-3) พร้อมก้าน<br>INSULATOR, PIN TYPE, 33 kV TIS 279 TYPE C (CLASS 56-3) COMP. WITH PIN | 3 | 3 | 03000002<br>03100001 |
| 11 | ลูกถ้วยแขวน มอก. 354 แบบ ง (แบบ 52-4)<br>INSULATOR, SUSPENSION TYPE, TIS 354 TYPE D (CLASS 52-4) | 18 | 18 | 03020002<br>(0415) |
| 12 | สเตรนแคล้มป์ สำหรับสายอะลูมิเนียม อะลูมิเนียมอัลลอย และอะลูมิเนียมแกนเหล็ก ขนาดตามต้องการ<br>CLAMP, STRAIN, FOR Al, Al-ALLOY AND ACSR SIZE AS REQUIRED | 6 | 6 | 03110000<br>03110101 |
| 13 | หลอดต่อสาย ชนิดมีปีกไม่รับแรงดึง ขนาดตามต้องการ<br>CONNECTOR, SPLICE, COMPRESSION TYPE, TENSIONLESS SIZE AS REQUIRED | 3 | 3 | 02410001-5<br>02410100-8 |
| 14 | ยูแคล้มป์ สลัก 1 ตัว M 8 (ไวร์ โร้ป คลิ๊ป)<br>CLAMP, SINGLE U-BOLT, M 8 (WIRE ROPE CLIP) | 6 | 6 | 01230000<br>(0165) |
| 15 | กายทิมเบิ้ลสำหรับสายขนาด 50-95 ต.มม.<br>THIMBLE, GUY, FOR STEEL WIRE 50 – 95 $mm^2$ | 2 | 2 | 01210304<br>(0150) |

หมายเหตุ ในกรณีขาดแคลนหลอดต่อสาย ให้ใช้พีจี คอนเนคเตอร์ 2 อัน แทนได้

NOTE IN CASE OF LACKING TENSIONLESS SPLICE CONNECTOR, PERMIT TO USE 2 P.G. CONNECTORS.

| | | |
|---|---|---|
| กองวิศวกรรมไฟฟ้าและเครื่องกล<br>ฝ่ายวิศวกรรม | การไฟฟ้าส่วนภูมิภาค | ใช้แทนแบบ<br>ถูกแทนโดยแบบ<br>เขียนเสร็จวันที่ 20 ก.พ. 21<br>แก้แบบวันที่<br>มิติเป็น<br>มาตราส่วน |
| ผู้เขียน<br>ผู้สำรวจ<br>วิศวกร<br>หัวหน้าแผนก<br>หัวหน้ากอง<br>ผู้อำนวยการฝ่าย | ผู้ว่าการ | |
| รองผู้ว่าการฝ่ายเทคนิค | การติดตั้งอุปกรณ์ที่เสา เข้าปลายสายสองข้าง ระบบ 33 kV<br>(เสาคอนกรีต 14 ม.)<br><br>33 kV DOUBLE DEADEND INSTALLATION<br>(14 m CONCRETE POLE) | แบบเลขที่ SAI-015/21012<br>แผ่นที่ 2 ของจำนวน 2 แผ่น |