การประกอบเลขที่
ASSEMBLY NO. **5352**

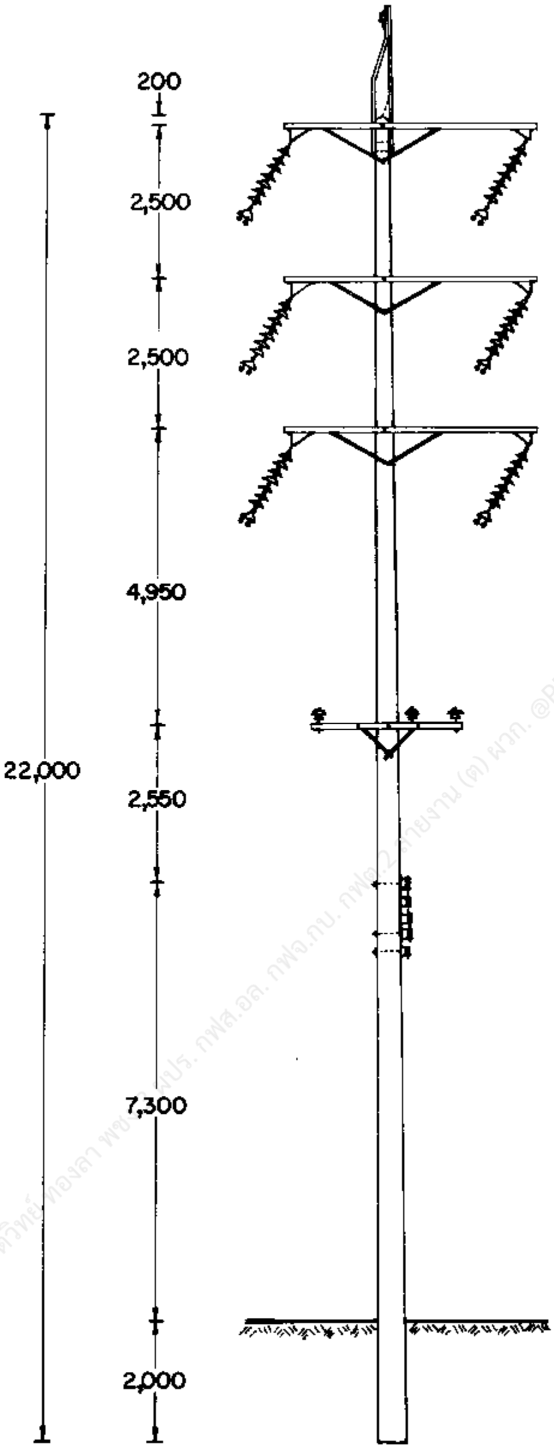

อดิวิทย์ ทองลา พช... หปร. กฟส.อล. กฟจ.กบ. กฟฉ.2 สายงาน (ต) ผวก. @PEA

กองวิศวกรรมไฟฟ้าและเครื่องกล
ฝ่ายวิศวกรรม

ผู้เขียน ....
ผู้ลอก
วิศวกร
หัวหน้าแผนก
หัวหน้ากอง
ผู้อำนวยการฝ่าย
รองผู้ว่าการฝ่ายเทคนิค

การไฟฟ้าส่วนภูมิภาค

ผู้ว่าการ .... 24 มี.ค. 23

115 kV วงจรคู่ สายไฟฟ้าคู่
เสาสำหรับทางโค้ง
แบบ DD-SA-1

23 115 kV DOUBLE CIRCUIT DOUBLE CONDUCTOR
SMALL ANGLE STRUCTURE
TYPE DD-SA-1

ใช้แทนแบบ ....
ถูกแทนโดยแบบ ....
เขียนเสร็จวันที่ 3 มค. 23
แก้แบบวันที่ ....
มิติเป็น มม.
มาตราส่วน 1 : 125
แบบเลขที่ SAI-015/23018
แผ่นที่ 1 ของจำนวน 3 แผ่น

19 มี.ค. 2523

การประกอบเลขที่
ASSEMBLY NO. **5352**

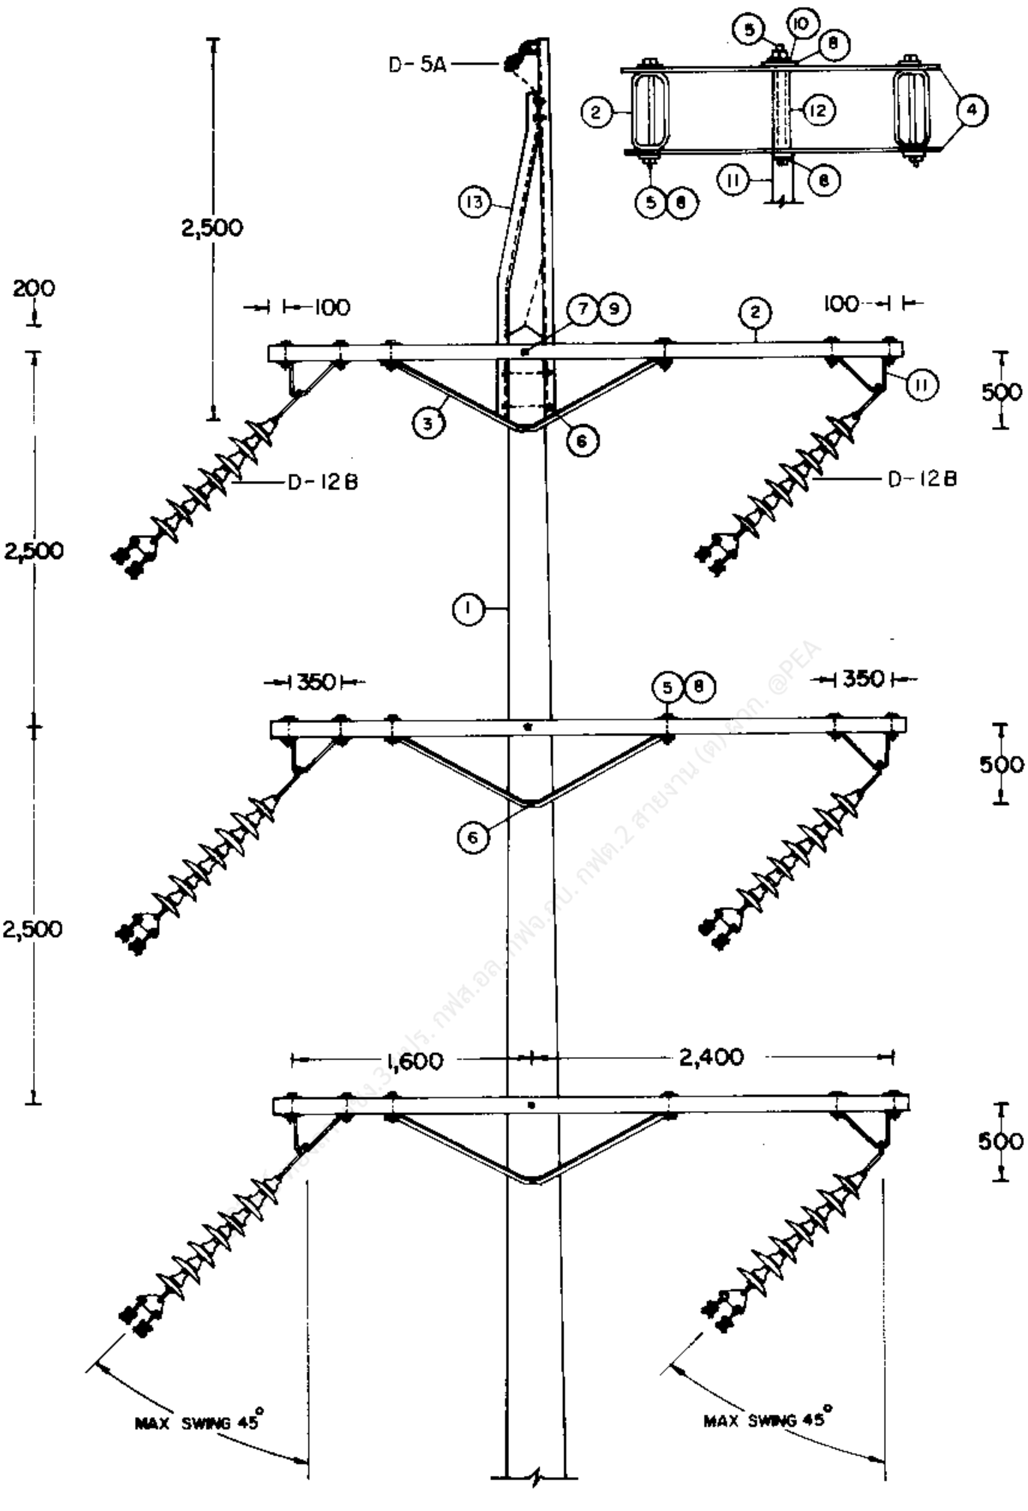

กองวิศวกรรมไฟฟ้าและเครื่องกล ฝ่ายวิศวกรรม	การไฟฟ้าส่วนภูมิภาค	ใช้แทนแบบ ถูกแทนโดยแบบ
ผู้เขียน ผู้ตรวจ วิศวกร หัวหน้าแผนก หัวหน้ากอง ผู้อำนวยการฝ่าย	ผู้ว่าการ 24 มี.ค. 23	เขียนเสร็จวันที่ 3 ม.ค. 23 แก้แบบวันที่ มิติเป็น มม. มาตราส่วน 1 : 50
	115 kV วงจรคู่ สายไฟฟ้าคู่ เสาสำหรับทางโค้ง แบบ DD-SA-1	
รองผู้ว่าการฝ่ายเทคนิค	115 KV DOUBLE CIRCUIT DOUBLE CONDUCTOR SMALL ANGLE STRUCTURE TYPE DD-SA-1	แบบเลขที่ SAI-015/23018 แผ่นที่ 2 ของจำนวน 3 แผ่น

1 มี.ค. 2523

การประกอบเลขที่ ASSEMBLY NO.	5352

บัญชีวัสดุ
BILL OF MATERIAL

ลำดับที่ ITEM	รายละเอียด DESCRIPTION	จำนวน REQ'D	วัสดุเลขที่ MAT. NO.
1	เสาคอนกรีต 22 ม. POLE, CONCRETE 22 m LONG	1	00010011 (0041)
2	คอนสายแบบเหล็ก ขนาด 100 X 50 X 3.2 มม. ยาว 4.20 ม. CROSSARM, STEEL 100 X 50 X 3.2 mm, 4.20 m LONG	6	00120001 (0116)
3	เหล็กฉากรับคอนสาย ขนาด 50 X 50 X 6 มม. ช่วงกว้าง 1,800 มม. ตกดิ่ง 450 มม. BRACE, ANGLE STEEL 50 X 50 X6 mm, 1,800 mm WIDE 450 mm DROP	6	01200007 (0119)
4	แผ่นเหล็ก ขนาด 6 X 100 X 450 มม. PLATE, STEEL 6 X 100 X 450 mm	24	01030002 (0143)
5	สลักเกลียว M 16 X 170 มม. BOLT, MACHINE, M 16 X 170 mm	48	01110201 (0221)
6	สลักเกลียว M 16 X 350 มม. BOLT, MACHINE, M 16 X 350 mm	6	01110205 (0225)
7	สลักเกลียว M 20 X 450 มม. BOLT, MACHINE, M 20 X 450 mm	3	01110302 (0234)
8	แหวนสี่เหลี่ยมแบน 52X52X4.5 มม. รู Ø 18 มม. มอก. 258 WASHER, SQUARE, FLAT 52X52X4.5 mm HOLE Ø 18 mm, TIS 258	84	01180100 (0355)
9	แหวนสี่เหลี่ยมแบน 62 X 62 X 6 มม. รู Ø 22 มม. มอก. 258 WASHER, SQUARE, FLAT 62 X 62 X 6 mm HOLE Ø 22 mm, TIS 258	6	01180101 (0356)
10	แหวนสปริง M 16 มอก. 259 WASHER, LOCK, M 16, TIS 259	12	0118030 (0365)
11	ที่แขวนลูกถ้วยทางโค้ง BRACKET, CORNER SUSPENSION	6	03140012 (0489)
12	ท่อเหล็ก ชื่อขนาด 20 มม. หนา 2.65 มม. ยาว 100 มม. มอก. 277 ประเภท 2 PIPE, IRON DIA. 20 mm I.D., 2.65 mm THICKNESS, 100 mm LONG, TIS 277, TYPE 2	12	0105000 (0905)
13	เหล็กฉากรับสายล่อฟ้าทางโค้ง OVERHEAD GROUND WIRE CORNER BAYONET	1	01010005 (0136)

รายละเอียด
DETAIL

D-12B	การประกอบลูกถ้วยแขวน SUSPENSION INSULATOR ASSEMBLY	6	
D-5A	การต่อสายล่อฟ้า OVERHEAD GROUND WIRE CONNECTION	1	
D-10A	ฐานรากเสา POLE FOUNDATION	1	

กองวิศวกรรมไฟฟ้าและเครื่องกล
ฝ่ายวิศวกรรม

ผู้เขียน ....
ผู้สำรวจ ....
วิศวกร ....
หัวหน้าแผนก ....
หัวหน้ากอง ....
ผู้อำนวยการฝ่าย ....

รองผู้ว่าการฝ่ายเทคนิค
23

๑ มี.ค. ๒๕๒๓

การไฟฟ้าส่วนภูมิภาค

ผู้ว่าการ ....

115 kV วงจรคู่ สายไฟฟ้าคู่
เสาสำหรับทางโค้ง
แบบ DD-SA-1

115 kV DOUBLE CIRCUIT DOUBLE CONDUCTOR
SMALL ANGLE STRUCTURE
TYPE DD-SA-1

ใช้แทนแบบ ....
ถูกแทนโดยแบบ ....
เขียนเสร็จวันที่ 3 ม.ค. 23
แก้แบบครั้งที่ ....
วิศวกร ....
มาตราส่วน ....

แบบเลขที่ SAI-015/23018
แผ่นที่ 3 ของจำนวน 3 แผ่น