



การประกอบเลขที่	2818
ASSEMBLY NO.	3814

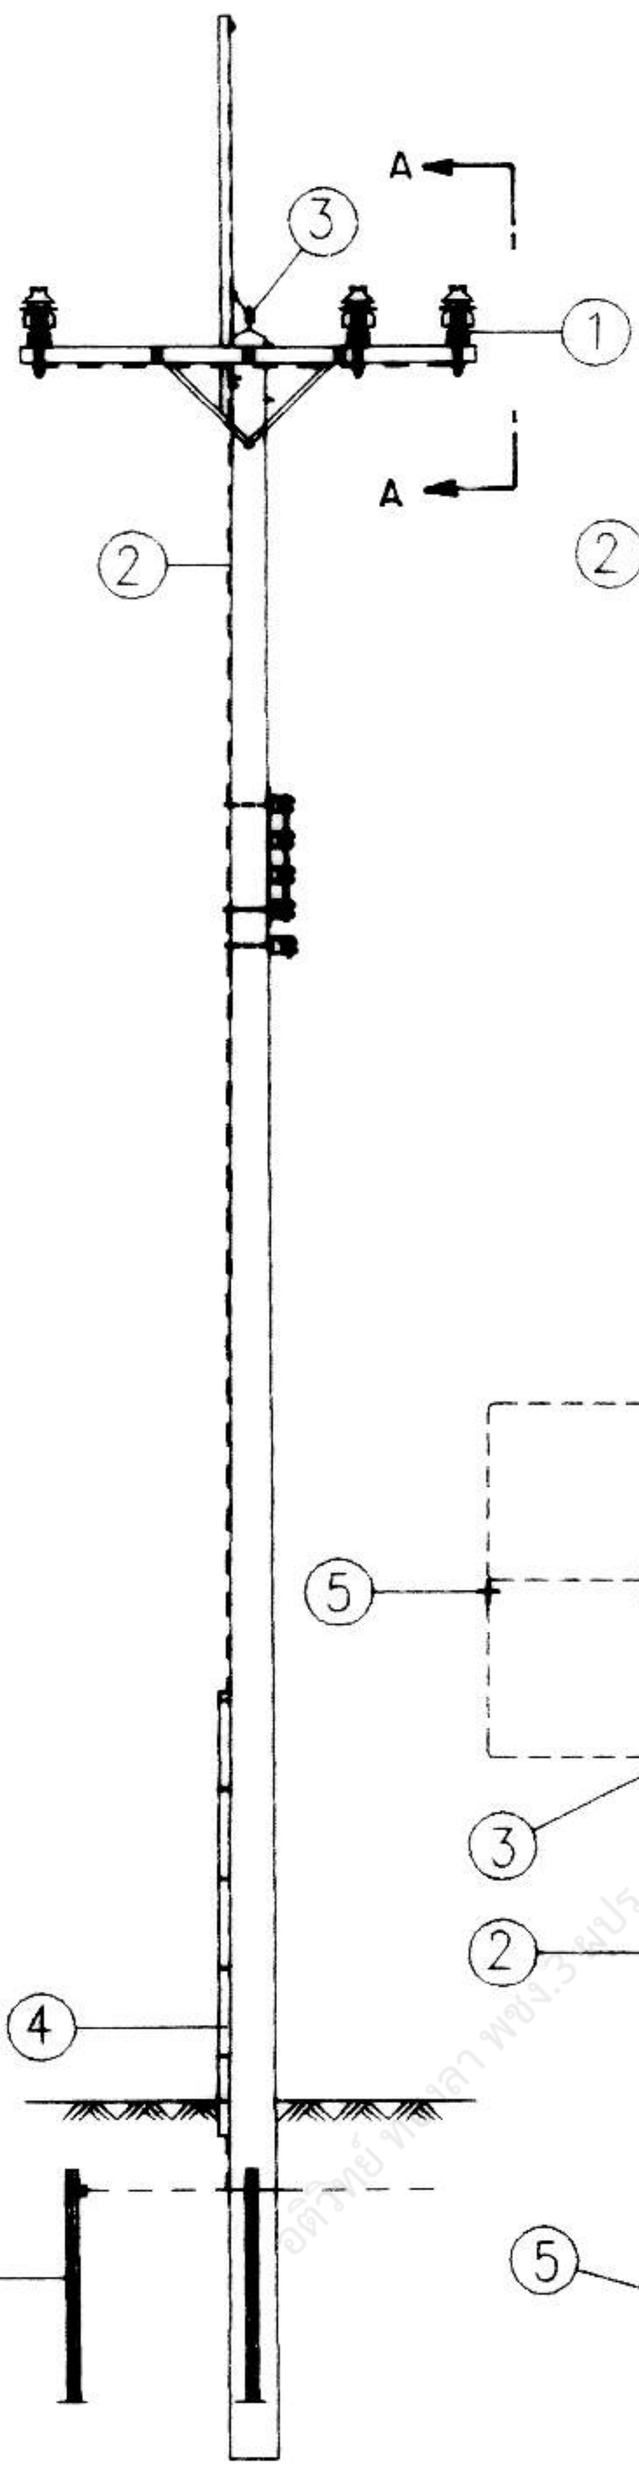

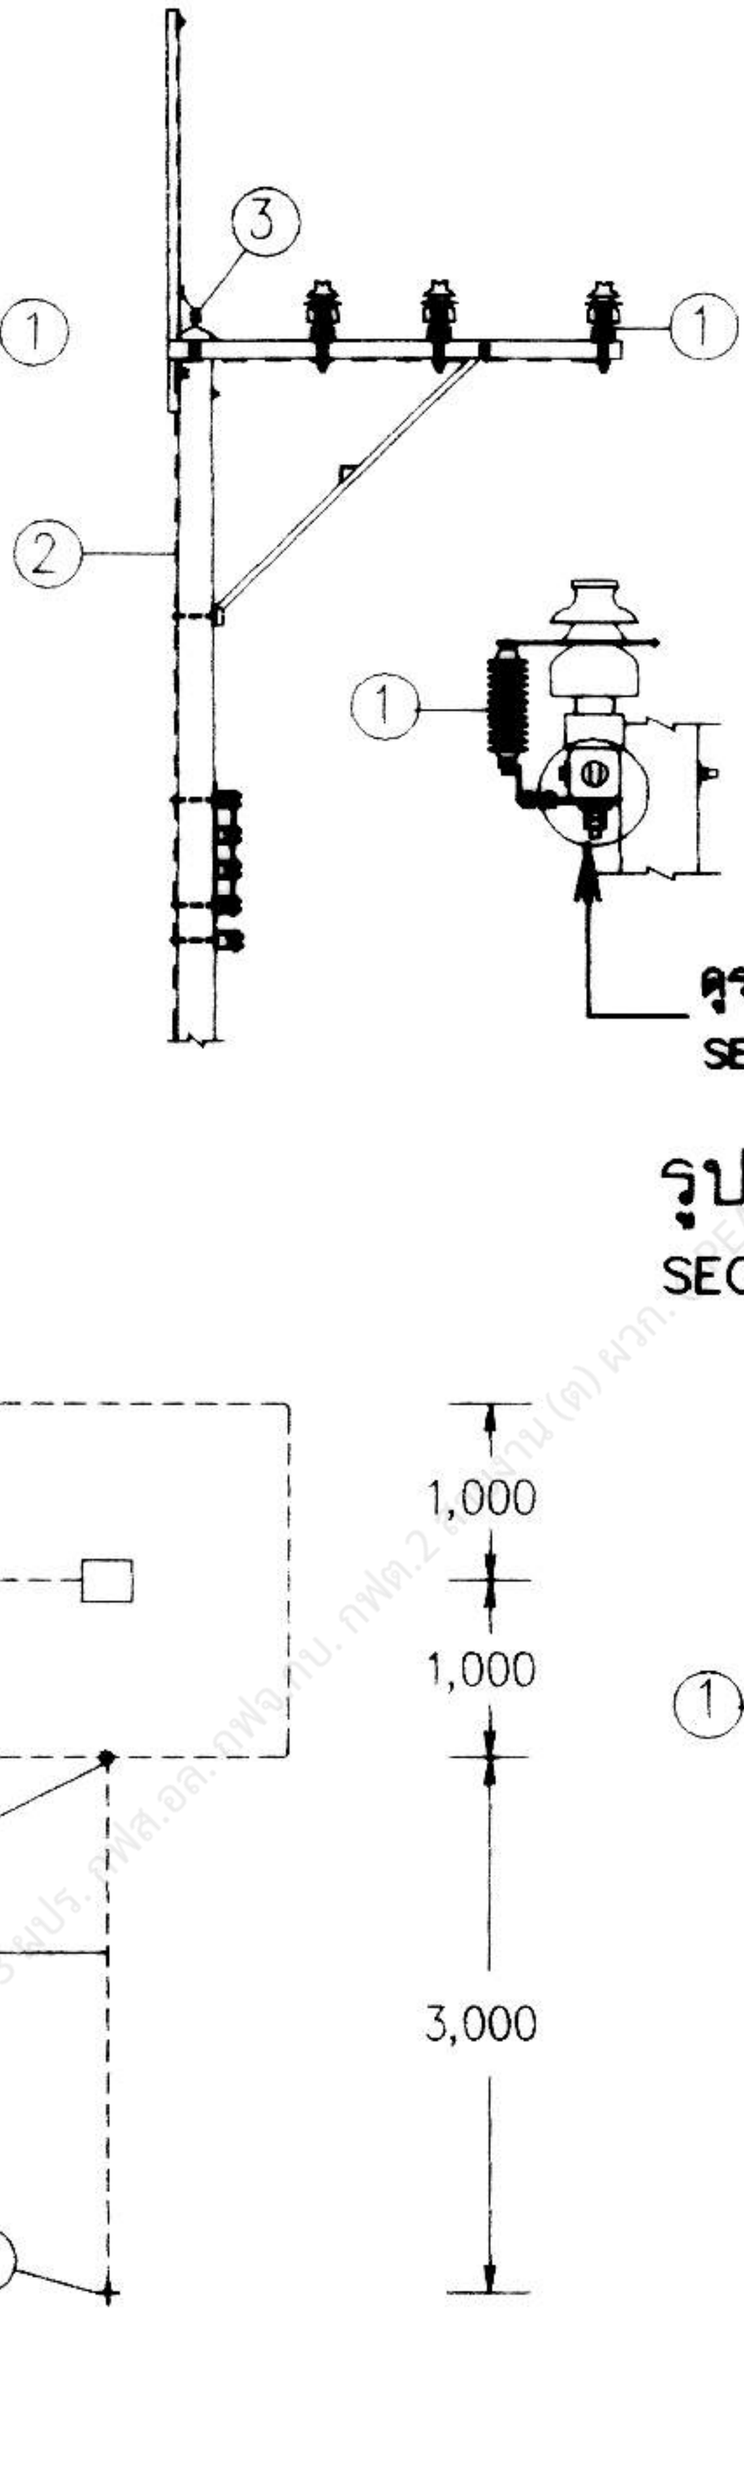

รูปตัด A–A
SECTION

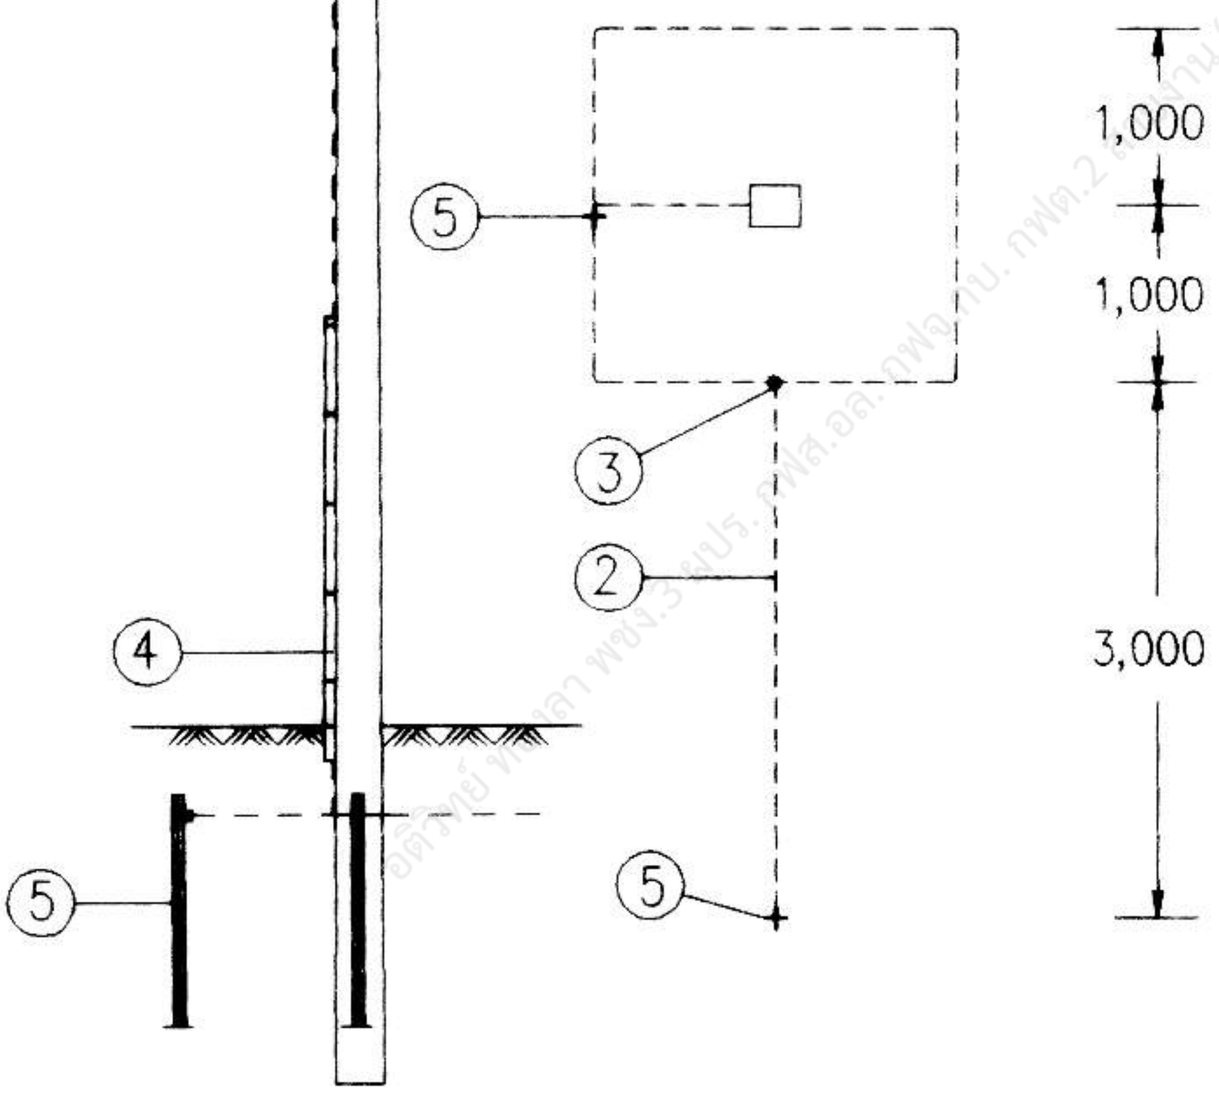

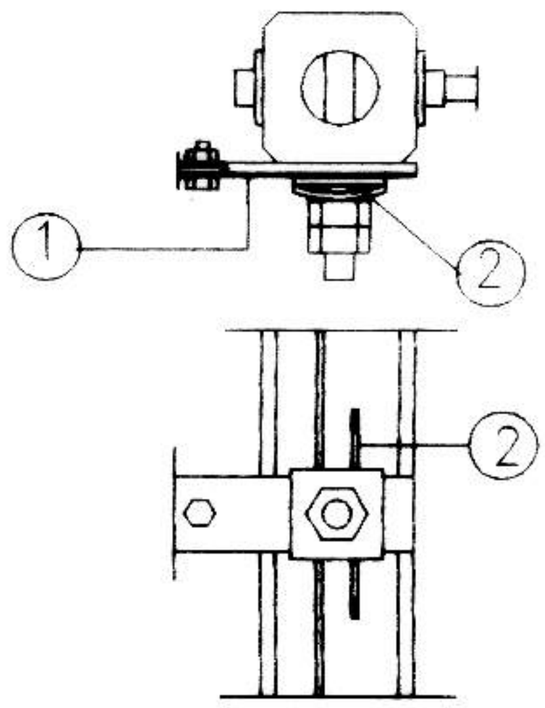



รายละเอียด A
DETAIL

1. สำหรับการติดตั้ง 1 วงจร (PIC)
1. FOR 1–CIRCUIT INSTALLATION (PIC)

กองวิศวกรรมไฟฟ้าและเครื่องกล ฝ่ายวิศวกรรม	การไฟฟ้าส่วนภูมิภาค	ใช้แทนแบบ ..... ถูกแทนโดยแบบ ..... เขียนเสร็จวันที่ 15. ก.ย. 2538. แก้แบบวันที่ ..... มิติเป็น มิลลิเมตร มาตราส่วน 1:75
ผู้เขียน EMD COMP. ผู้สำรวจ ..... วิศวกร ..... หัวหน้าแผนก ..... ผู้อำนวยการกอง ..... ผู้อำนวยการฝ่าย	ผู้ว่าการ ..... 26 ก.ค. 2538 ยงยศ.	
ของผู้ว่าการ	การติดตั้ง CURRENT LIMITING ARCING HORN สำหรับระบบจำหน่าย 22 kV และ 33 kV CURRENT LIMITING ARCING HORN INSTALLATION 22 kV AND 33 kV DISTRIBUTION LINE	แบบเลขที่ SA4–015/38013 แผ่นที่ 1 ของจำนวน 3 แผ่น

การประกอบเลขที่	2816
ASSEMBLY NO.	3814

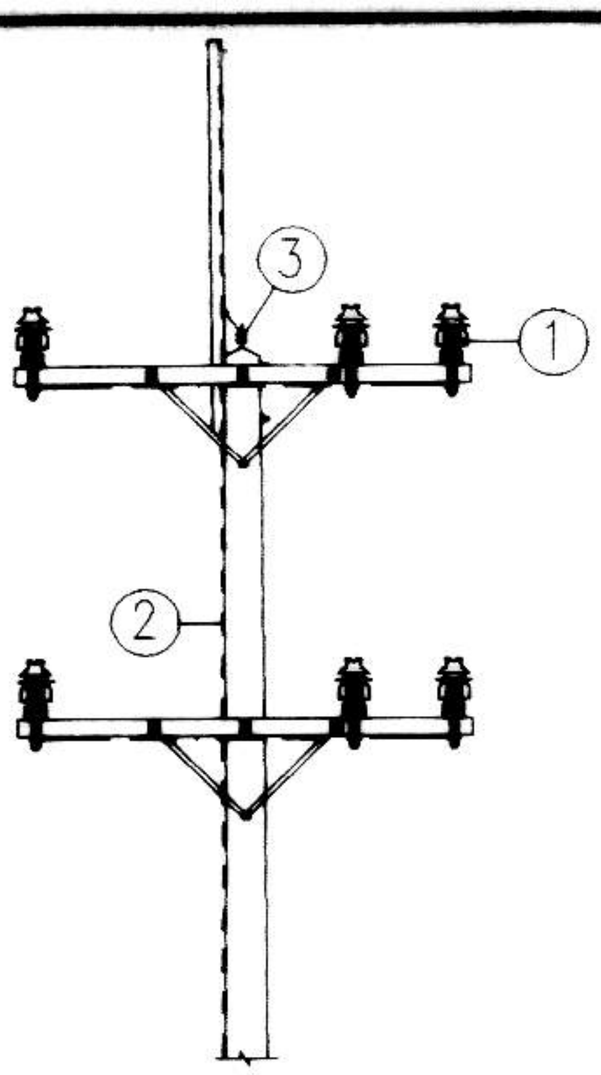

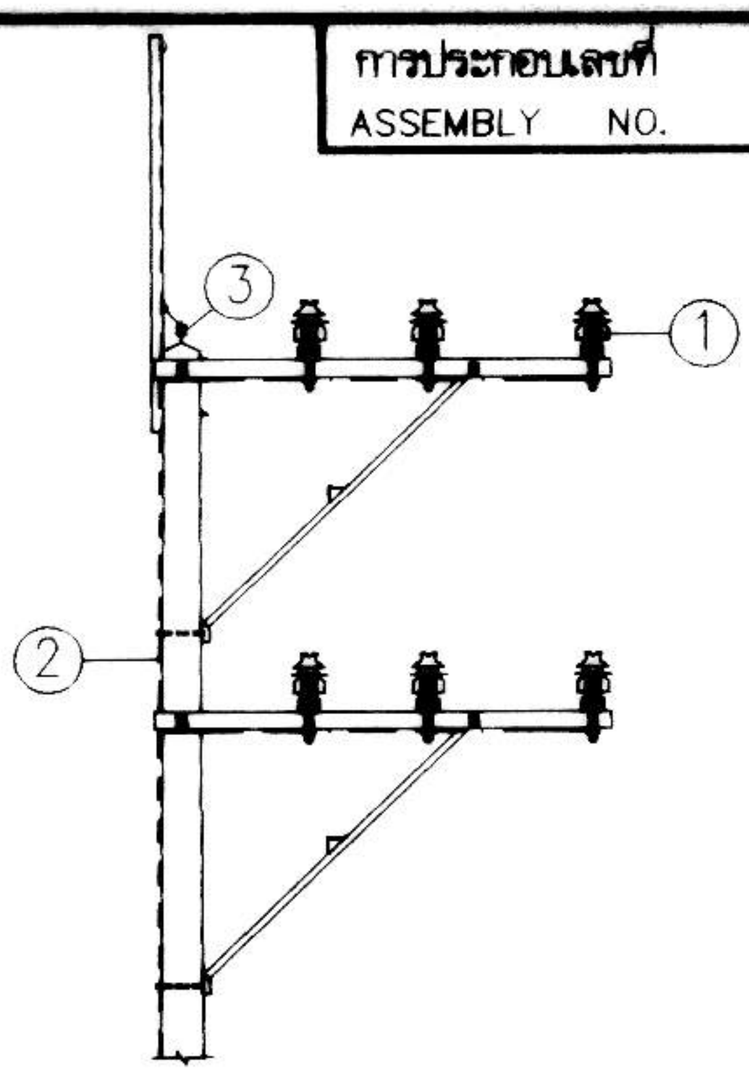

2. สำหรับการติดตั้ง 2 วงจร (PIC)
FOR 2-CIRCUIT INSTALLATION (PIC)

ข้อกำหนดการใช้งาน

ติดตั้งในส่วนของระบบจำหน่าย ดังนี้ :

1. สายเมนที่ใช้สาย PIC ทุกเฟสทุกฟีดเดอร์ในรัศมี 10 กม. ออกจากสถานีไฟฟ้า ทุกระยะ 200-300 เมตร
2. สายระบบจำหน่ายที่ใช้สาย PIC ในบริเวณที่มีฟ้าผ่ารุนแรง ทุกระยะ 200-300 เมตร
3. ระบบจำหน่ายที่ใช้สาย PIC ส่วนที่นอกเหนือจากข้อ 1. และข้อ 2. และอยู่หลังรีโคลสเซอร์หรือดรอพเอาต์ฟิวส์คัตเอาต์ ให้ติดตั้ง ARCING PROTECTION DEVICE (APD) ทุกๆ ระยะ 200-300 เมตร

RECOMMENDATION

INSTALL IN THE FOLLOWING PARTS :

1. EVERY PHASE AND EVERY FEEDER OF MAIN LINES WHICH USE PIC OF 10 km IN RADIUS FROM SUBSTATION AT EVERY 200-300 m .
2. DISTRIBUTION LINES WHICH USE PIC, IN HIGH LIGHTNING HAZARDOUS AREA, AT EVERY 200-300 m .
3. DISTRIBUTION LINES WHICH USE PIC, EXCEPT 1. AND 2. AND RUN AFTER RECLOSER OR DROPOUT FUSE CUT-OUT, SHALL INSTALL ARCING PROTECTION DEVICE (APD) AT EVERY 200-300 m .

หมายเหตุ

1. ค่าความต้านทานดินของสายดินแต่ละจุดควรมีค่าไม่เกิน 5 โอห์ม แต่ในพื้นที่ยากแก่การต่อลงดิน ยอมให้มีค่าไม่เกิน 25 โอห์ม
2. ในบริเวณที่มีต้นไม้สูงอยู่ ให้ตรวจสอบระบบจำหน่ายอย่างน้อย ทุกๆ 2 ปีต่อครั้ง หรือภายหลังจากเกิดพายุรุนแรงทุกครั้ง เพื่อนำกิ่งไม้หรือใบไม้ออก

NOTES

1. THE EARTH ELECTRODE RESISTANCE SHOULD BE NOT EXCEEDED 5 OHMS; BUT IN DIFFICULTY EARTHING AREA, 25 OHMS SHOULD BE ALLOWED .
2. IN AREA WHERE TREES ARE TALL; THE DISTRIBUTION LINES HAVE TO BE INSPECTED AT LEAST EVERY 2 YEARS OR AFTER SEVERE STORMS, IF IT IS LIKELY THAT BRANCHES AND LEAVES OF TREE HAVE TO BE CLEARED.

กองวิศวกรรมไฟฟ้าและเครื่องกล ฝ่ายวิศวกรรม	การไฟฟ้าส่วนภูมิภาค	ใช้แทนแบบ ..... ถูกแทนโดยแบบ ..... เขียนเสร็จวันที่ 18 กย. 2538 แก้แบบวันที่ ..... มิติเป็น มิลลิเมตร มาตราส่วน 1:75
ผู้เขียน EMD COMP. ผู้สำรวจ ..... วิศวกร ..... หัวหน้าแผนก ..... ผู้อำนวยการกอง ..... ผู้อำนวยการฝ่าย ..... รองผู้ว่าการ	ผู้ว่าการ ..... 20 ต.ค. 2538 แทน. การติดตั้ง CURRENT LIMITING ARCING HORN สำหรับระบบจำหน่าย 22 kV และ 33 kV CURRENT LIMITING ARCING HORN INSTALLATION 22 kV AND 33 kV DISTRITRIBUTION LINE	แบบเลขที่ SA4-015/38013 แผ่นที่ 2 ของจำนวน 3 แผ่น

การประกอบแบบที่ 2818
ASSEMBLY NO. 3814

บัญชีวัสดุ
BILL OF MATERIAL

ลำดับที่ ITEM	รายละเอียด DESCRIPTION	จำนวน REQ'D 1	จำนวน REQ'D 2	วัสดุแบบที่ MAT. NO.
1	ลูกถ้วยพินไพสเท่าไทพ์ 22 kV หรือ 33kV ชนิดทนแพ้วอร์อาร์ก พร้อมCURRENT LIMITING ARCING HORN และ อุปกรณ์ยึดสายดิน INSULATOR,PIN–POST TYPE,22 kV OR 33 kV,POWER ARC TEST; COMPLETE WITH CURRENT LIMITING ARCING HORN AND GROUND WIRE FIXING	3	6	
2	ลวดเหล็กสี่เกลียว 50/7 ตร.มม. มอก. 404 WIRE,STEEL STRAND,50/7 mm^2, TIS 404	28m	33m	01100004
3	ยูแคล้มป์ สลัก 1 ตัว M8 CLAMP,SINGLE U–BOLT,M8	4	6	01230000
4	ท่อ PVC แข็ง ขนาด ø 20X2,500–4,000 มม. มอก 216 พร้อมอุปกรณ์ยึด CONDUIT,PVC. RIGID,ø 20X2,500–4,000 mm,TIS 216; COMP. WITH FIXING	1	1	01220002
5	หลักดิน ขนาด 60X60X5 มม. ยาว 2 ม. ROD,GROUND,60X60X5 mm, 2 m LONG	2	2	08040001–2

หมายเหตุ

บัญชีวัสดุนี้ใช้สำหรับ การติดตั้ง CURRENT LIMITING ARCING HORN

NOTE

THIS BILL OF MATERIAL IS USED FOR CURRENT LIMITING ARCING HORN INSTALLATION.

ลำดับที่ ITEM	การประกอบแบบที่ ASSEMBLY NO.	การประกอบแบบที่ ASSEMBLY NO.	การประกอบแบบที่ ASSEMBLY NO.
1	การประกอบสายลงดิน วิธียึดลวดเหล็ก GROUND LEAD ASSEMBLY, STEEL WIRE ASSEMBLY	S02–015/19166 SA1–015/31012	9703 9703A
2	การประกอบที่ยึดท่อ สำหรับสายดิน PVC PIPE ASSEMBLY, FOR GROUND WIRE	S02–015/19128 SA1–015/31013	9704 9704A

อดิวัฒย์ ทองดา พชง.3 ผปร. กฟภ.2 สำนัก (ค) ผวก.@PEA

กองวิศวกรรมไฟฟ้าและเครื่องกล
ฝ่ายวิศวกรรม

ผู้เขียน EMD. COMP.
ผู้สำรวจ .....
วิศวกร .....
หัวหน้าแผนก .....
ผู้อำนวยการกอง .....
ผู้อำนวยการฝ่าย .....

รองผู้ว่าการ
.....

การไฟฟ้าส่วนภูมิภาค

ผู้ว่าการ ..... 20 ก.ค. 2538

การติดตั้ง CURRENT LIMITING ARCING HORN
สำหรับระบบจำหน่าย 22 kV และ 33 kV

CURRENT LIMITING ARCING HORN INSTALLATION
22 kV AND 33 kV DISTRIBUTION LINE

ใช้แทนแบบ .....
ถูกแทนโดยแบบ .....
เขียนเสร็จวันที่ 18 กรกฎ. 2538
แก้แบบวันที่ .....
มิติเป็น .....
มาตราส่วน .....

แบบเลขที่ SA4–015/38013
แผ่นที่ 3 ของจำนวน 3 แผ่น