การประกอบเลขที่
ASSEMBLY NO. 5256

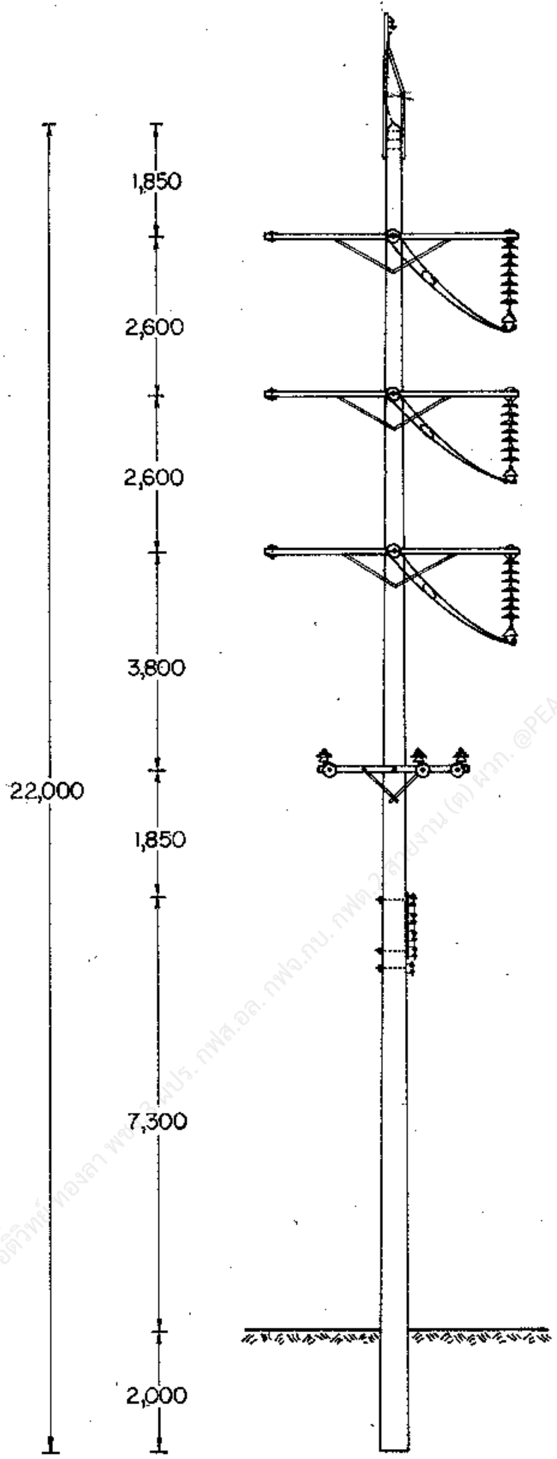

อดิวิทย์ ทองลา พชง.3 ฝปร. กฟส.อล. กฟจ.กบ. กฟต.2 สายงาน (ต) ผวก. @PEA

กองวิศวกรรมไฟฟ้าและเครื่องกล
ฝ่ายวิศวกรรม

ผู้เขียน
ผู้ตรวจ
วิศวกร
หัวหน้าแผนก
หัวหน้ากอง
ผู้อำนวยการฝ่าย 23
รองผู้ว่าการฝ่ายเทคนิค

การไฟฟ้าส่วนภูมิภาค

ผู้ว่าการ 24 ม.ค. 23

115 kV วงจรเดี่ยว สายไฟฟ้าคู่
เสาสำหรับทางโค้ง (ช่วงไม่รับแรงดึง)
แบบ SD-AS-1

115 kV SINGLE CIRCUIT DOUBLE CONDUCTOR
ANGLE STRUCTURE (SLACK SPAN)
TYPE SD-AS-1

ใช้แทนแบบ
ถูกแทนโดยแบบ
เขียนเสร็จวันที่ 2 ม.ค.23
แก้แบบวันที่
มิติเป็น มม.
มาตราส่วน 1:125
แบบเลขที่ SAI-015/23010
แผ่นที่ 1 ของจำนวน 4 แผ่น

การประกอบเลขที่ ASSEMBLY NO. 5256

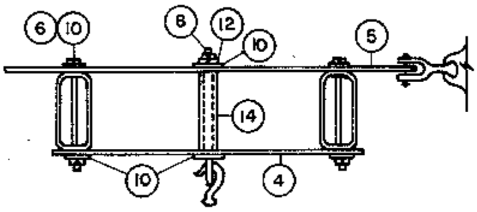

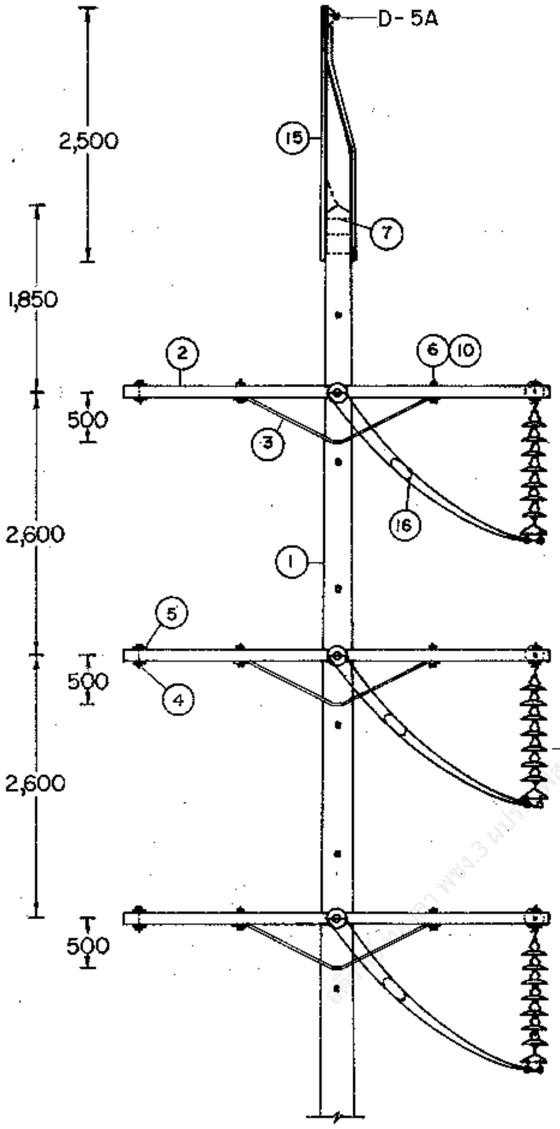

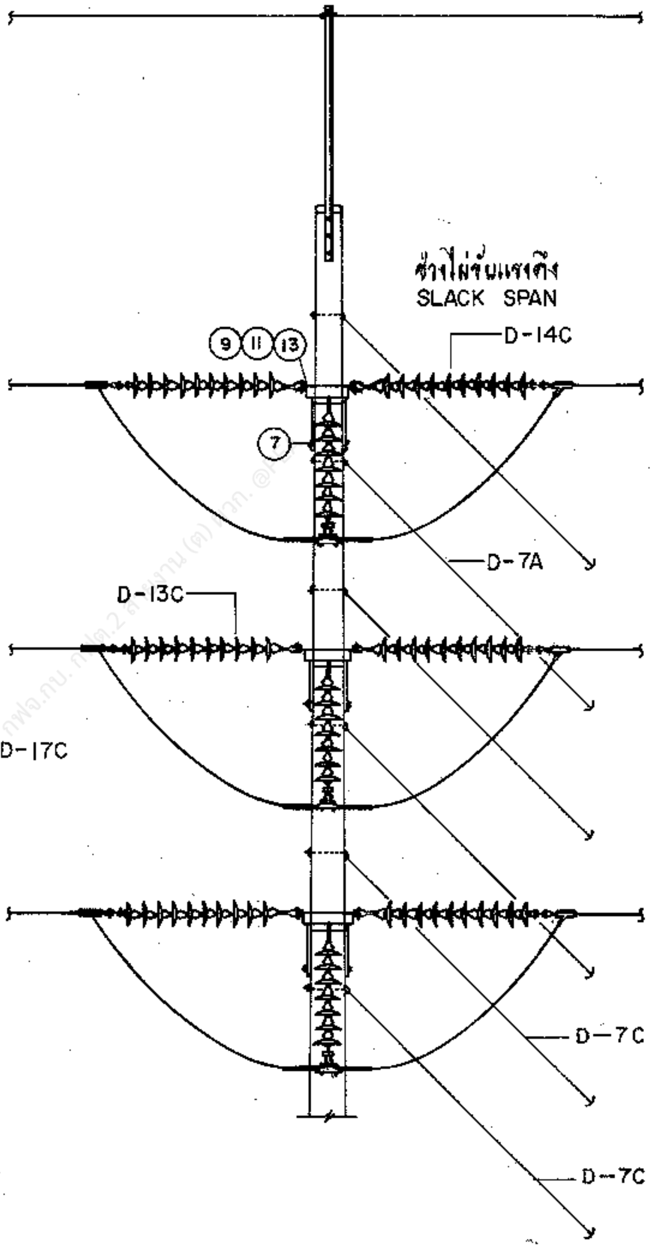

กองวิศวกรรมไฟฟ้าและเครื่องกล ฝ่ายวิศวกรรม	การไฟฟ้าส่วนภูมิภาค	ใช้แทนแบบ ถูกแทนโดยแบบ
ผู้เขียน ผู้สำรวจ วิศวกร หัวหน้าแผนก หัวหน้ากอง ผู้อำนวยการฝ่าย	ผู้ว่าการ 24 มิ.ย.23 115 kV วงจรเดี่ยว สายไฟฟ้าคู่ เสาสำหรับทางโค้ง (ช่วงไม่รับแรงดึง) แบบ SD-AS-1	เขียนเสร็จวันที่ 2 ม.ค.23 แก้แบบวันที่ 15 ก.ย.40 มิติเป็น มม. มาตราส่วน 1:75
รองผู้ว่าการฝ่ายเทคนิค	115 kV SINGLE CIRCUIT DOUBLE CONDUCTOR ANGLE STRUCTURE (SLACK SPAN) TYPE SD-AS-1	แบบเลขที่ SAI-015/23010 แผ่นที่ 2 ของจำนวน 4 แผ่น

19 ส.ค. 2523

การประกอบเลขที่
ASSEMBLY NO. 5256

บัญชีวัสดุ
BILL OF MATERIAL

ลำดับที่ ITEM	รายละเอียด DESCRIPTION	จำนวน REQ'D	วัสดุเลขที่ MAT. NO.
1	เสาคอนกรีต 22 ม. POLE, CONCRETE 22 m LONG	1	00010011 (0041)
2	คอนสายแบบเหล็ก 100X50X3.2 มม. ยาว 4.20 ม. CROSSARM, STEEL 100X50X3.2 mm, 4.20 m LONG	6	00120001 (0116)
3	เหล็กฉากรับคอนสาย ขนาด 50X50X6 มม. ช่วงกว้าง 1,800 มม. ดรอพ 450 มม. BRACE, ANGLE STEEL, 50X50X6 mm 1,800 mm WIDE 450 mm DROP	6	01200007 (0119)
4	เหล็กแผ่น ขนาด 6X100X450 มม. PLATE, STEEL 6X100X450 mm	6	01030002 (0143)
5	แผ่นเหล็กยึดต่อปลาย ขนาด 12X100X650 มม. PLATE, STEEL, DOUBLE ARMING 12X100X650 mm	6	01030100 (0145)
6	สลักเกลียว M 16X170 มม. BOLT, MACHINE, M 16 X 170 mm	24	01110201 (0221)
7	สลักเกลียว M 16X350 มม. BOLT, MACHINE, M 16 X 350 mm	6	01110205 (0225)
8	สลักห่วงโอแวล M 16X150 มม. BOLT, OVAL EYE M 16 X 150 mm	3	01150000 (0257)
9	สลักห่วงโอแวล M 20X450 มม. BOLT, OVAL EYE M 20 X 450 mm	3	01150101 (0261)
10	แหวนสี่เหลี่ยมแบน 52X52X4.5 มม. รู Ø 18 มม. มอก. 258 WASHER, SQUARE, FLAT 52X52X4.5 mm, HOLE Ø 18 mm, TIS 258	42	01180100 (0355)
11	แหวนสี่เหลี่ยมแบน 62X62X6 มม. รู Ø 22 มม. มอก. 258 WASHER, SQUARE, FLAT 62X62X6 mm, HOLE Ø 22 mm, TIS 258	6	01180101 (0356)
12	แหวนสปริง M 16 มอก. 259 WASHER, LOCK, M 16, TIS 259	3	01180301 (0365)
13	แหวนสปริง M 20 มอก. 259 WASHER, LOCK, M 20, TIS 259	3	01180302 (0366)
14	ท่อเหล็ก ชื่อขนาด 20 มม. หนา 2.65 มม. ยาว 100 มม. มอก. 277 ประเภท 2 PIPE, IRON, DIA. 20 mm I.D., 2.65 mm THICKNESS, 100 mm LONG, TIS 277, TYPE 2	3	01050000 (0905)
15	เหล็กฉากรับสายล่อฟ้าทางโค้ง OVERHEAD GROUND WIRE CORNER BAYONET	1	01010005 (0136)
16	ปรีฟอร์มแยกสาย SPACER, HELICAL ROD, PREFORMED	6	02240000 (0918)

กองวิศวกรรมไฟฟ้าและเครื่องกล
ฝ่ายวิศวกรรม
ผู้เขียน........
ผู้สำรวจ........
วิศวกร........
หัวหน้าแผนก........
หัวหน้ากอง........
ผู้อำนวยการฝ่าย........
รองผู้ว่าการฝ่ายเทคนิค

การไฟฟ้าส่วนภูมิภาค

ผู้ว่าการ........ 24 มี.ค. 23

115 kV วงจรเดี่ยว สายไฟฟ้าคู่
เสาสำหรับทางโค้ง (ช่วงไม่รับแรงดึง)
แบบ SD-AS-1

115 kV SINGLE CIRCUIT DOUBLE CONDUCTOR
ANGLE STRUCTURE (SLACK SPAN)
TYPE SD-AS-1

ใช้แทนแบบ........
ถูกแทนโดยแบบ........
เขียนเสร็จวันที่ 2 มี.ค. 23
แก้แบบวันที่........
มิติเป็น........
มาตราส่วน........
แผ่นเลขที่ SAI-015/23010
แผ่นที่ 3 ของจำนวน 4 แผ่น

19 มี.ค. 2523

การประกอบเลขที่ 5256
ASSEMBLY NO. 5256

	รายละเอียด DETAIL		
D-13C	การประกอบลูกถ้วยแขวน SUSPENSION INSULATOR ASSEMBLY	3	
D-14C	การประกอบลูกถ้วยแขวน SUSPENSION INSULATOR ASSEMBLY	3	
D-17C	การประกอบลูกถ้วยแขวน SUSPENSION INSULATOR ASSEMBLY	3	
D-5A	การต่อสายล่อฟ้า OVERHEAD GROUND WIRE CONNECTION	1	
D-7A	การประกอบสายยึดโยงลวดเหล็กตีเกลียว 95 ต.มม. STEEL STRANDED WIRE 95 mm² GUY ASSEMBLY	4	
D-7C	การประกอบสายยึดโยงลวดเหล็กตีเกลียว 95 ต.มม. STEEL STRANDED WIRE 95 mm² GUY ASSEMBLY	2	
D-9B	สมอบกคอนกรีต CONCRETE ANCHOR	1	
D-10A	ฐานรากเสา POLE FOUNDATION	1	

อดิวิทย์ ทองลา พชง.3 ผปร. กฟส.อล. กฟจ.กบ. กฟต.2 สายงาน (ต) ผวก. @PEA

กองวิศวกรรมไฟฟ้าและเครื่องกล ฝ่ายวิศวกรรม	**การไฟฟ้าส่วนภูมิภาค**	ใช้แทนแบบ ถูกแทนโดยแบบ เขียนเสร็จวันที่ 2 ม.ค.23 แก้แบบวันที่ 15 ก.ย.40 มิติเป็น มาตราส่วน
ผู้เขียน ผู้สำรวจ วิศวกร หัวหน้าแผนก หัวหน้ากอง ผู้อำนวยการฝ่าย	ผู้ว่าการ 24 มี.ค. 23	
	115 kV วงจรเดี่ยว สายไฟฟ้าคู่ เสาสำหรับทางโค้ง (ช่วงไม่รับแรงดึง) แบบ SD-AS-1	
รองผู้ว่าการฝ่ายเทคนิค	115 kV SINGLE CIRCUIT DOUBLE CONDUCTOR ANGLE STRUCTURE (SLACK SPAN) TYPE SD-AS-1	แบบเลขที่ SAI-015/23010 แผ่นที่ 4 ของจำนวน 4 แผ่น

19 มี.ค. 2523