การประกอบเลขที่
ASSEMBLY NO. 5210

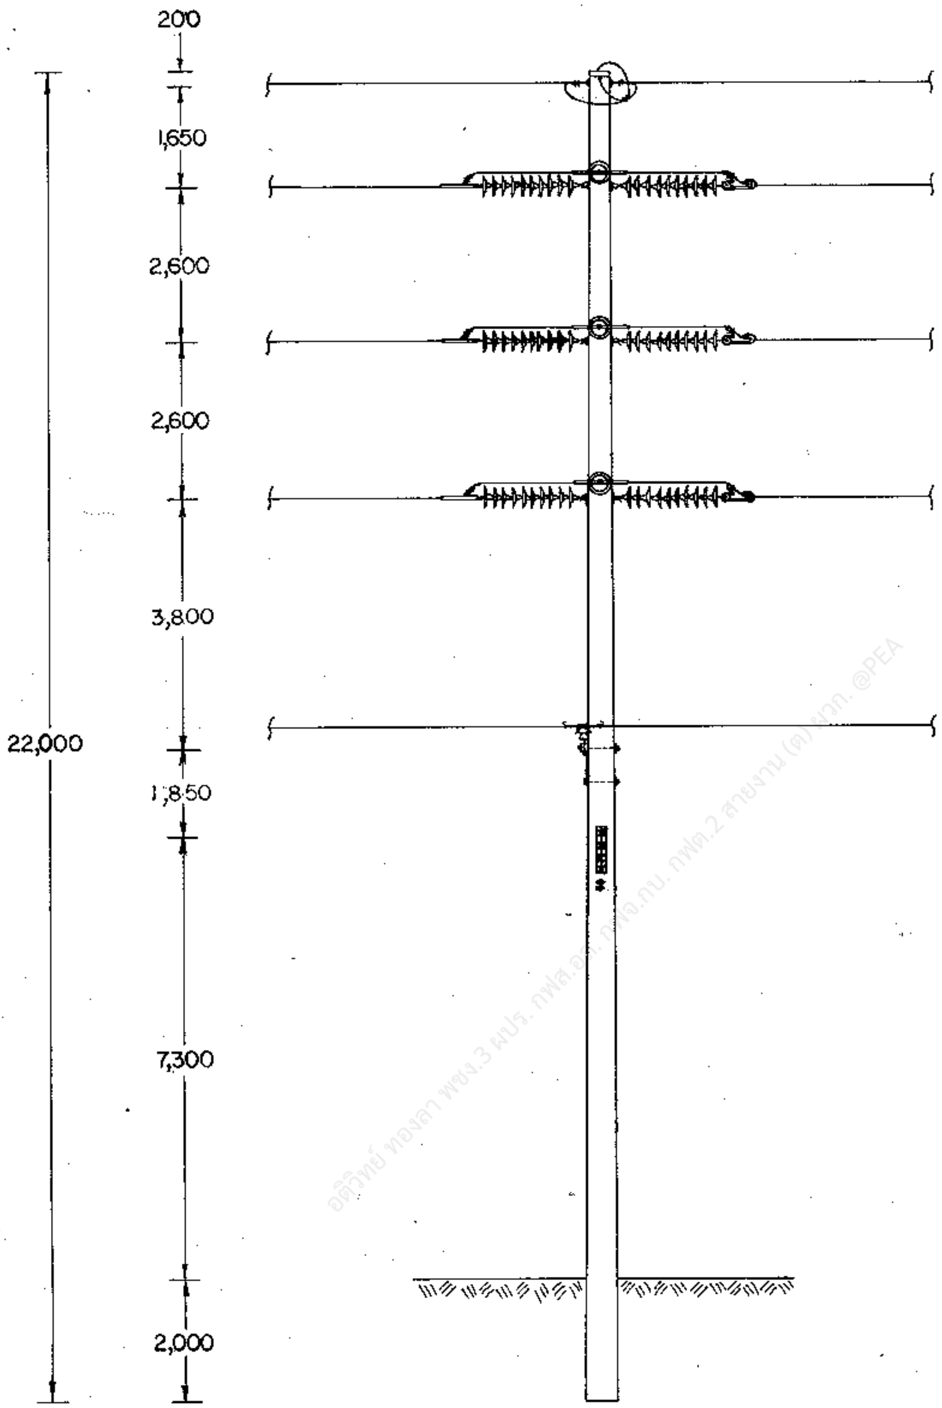

กองวิศวกรรมไฟฟ้าและเครื่องกล ฝ่ายวิศวกรรม	# การไฟฟ้าส่วนภูมิภาค	ใช้แทนแบบ ถูกแทนโดยแบบ
ผู้เขียน ผู้ตรวจ วิศวกร หัวหน้าแผนก ชัยรัฐ หัวหน้ากอง ผู้อำนวยการฝ่าย	ผู้ว่าการ 24 มี.ค. 23 115 kV วงจรเดี่ยว สายไฟฟ้าเดี่ยว เสาเดี่ยวสำหรับแยกสาย แบบ SS-TL-1	เขียนเสร็จวันที่ 2 ม.ค. 23 แก้แบบวันที่ มิติเป็น มม. มาตราส่วน 1 : 125
รองผู้ว่าการฝ่ายเทคนิค	115 kV SINGLE CIRCUIT SINGLE CONDUCTOR SINGLE POLE, TAP LINE STRUCTURE TYPE SS—TL—1	แบบเลขที่ SAI-015/23003 แผ่นที่ 1 ของจำนวน 3 แผ่น

19 มี.ค. 2523

อดิวิทย์ ทองลา พชง.3 ผปร. กฟส.อล. กฟจ.กบ. กฟต.2 สายงาน (ต) ผวก. @PEA

การประกอบเลขที่
ASSEMBLY NO. **5210**

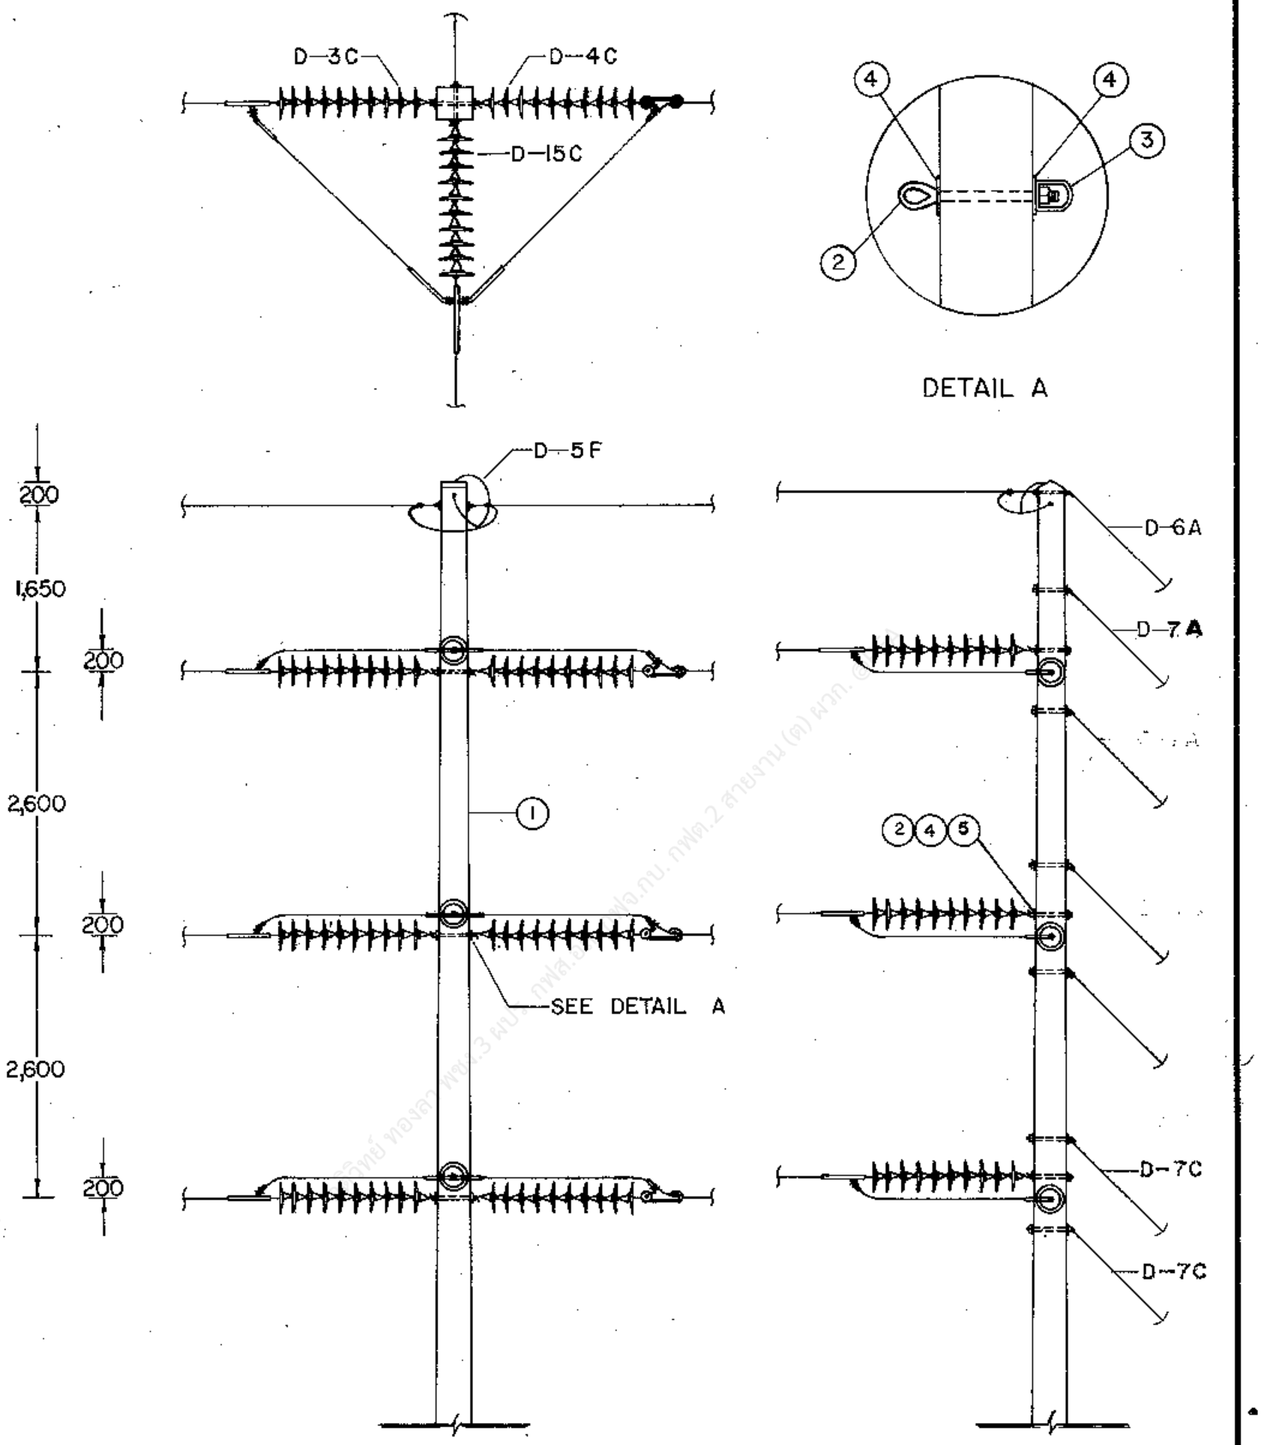

กองวิศวกรรมไฟฟ้าและเครื่องกล ฝ่ายวิศวกรรม	**การไฟฟ้าส่วนภูมิภาค**	ใช้แทนแบบ........ ถูกแทนโดยแบบ........
ผู้เขียน........ ผู้ตรวจ........ วิศวกร........ หัวหน้าแผนก........ หัวหน้ากอง........ ผู้อำนวยการฝ่าย........	ผู้ว่าการ........	เขียนเสร็จวันที่ 2 ม.ค. 23 แก้แบบวันที่ 15 ก.ย. 40 มิติเป็น มม. มาตราส่วน 1 : 75
	115 kV วงจรเดี่ยว สายไฟฟ้าเดี่ยว เสาเดี่ยวสำหรับแยกสาย แบบ SS-TL-1	
รองผู้ว่าการฝ่ายเทคนิค	115 kV SINGLE CIRCUIT SINGLE CONDUCTOR SINGLE POLE, TAP LINE STRUCTURE TYPE SS-TL-1	แบบเลขที่ SAI-015/23003 แผ่นที่ 2 ของจำนวน 3 แผ่น

การประกอบเลขที่ ASSEMBLY NO.	5210

บัญชีวัสดุ
BILL OF MATERIAL

ลำดับที่ ITEM	รายละเอียด DESCRIPTION	จำนวน REQ'D	วัสดุเลขที่ MAT. NO.
1	เสาคอนกรีต 22 ม. POLE, CONCRETE 22 m. LONG	1	00010011 (0041)
2	สลักห่วงโอแวล M 20 X 350 มม. BOLT, OVAL EYE M 20 X 350 mm.	6	01150100 (0260)
3	อายเล็ต สำหรับสลักเกลียว M 20 EYELET, FOR BOLT M 20	3	01180002 (0346)
4	แหวนสี่เหลี่ยมแบน 62X62X6 มม. รู Ø 22 มม. มอก. 258 WASHER, SQUARE, FLAT 62X62X6 mm HOLE Ø 22 mm TIS 258	12	01180101 (0356)
5	แหวนสปริง M 20 มอก. 259 WASHER, LOCK, M 20, TIS 259	3	01180302 (0366)
	รายละเอียด DETAIL		
D-3C	การประกอบลูกถ้วยแขวน SUSPENSION INSULATOR ASSEMBLY	3	
D-4C	การประกอบลูกถ้วยแขวน SUSPENSION INSULATOR ASSEMBLY	3	
D-15C	การประกอบลูกถ้วยแขวน SUSPENSION INSULATOR ASSEMBLY	3	
D-5F	การต่อสายล่อฟ้า OVERHEAD GROUND WIRE CONNECTION	1	
D-6A	การประกอบสายยึดโยงลวดเหล็กตีเกลียว 50 ต.มม. STEEL STRANDED WIRE 50 mm² GUY ASSEMBLY	1	
D-6C	การประกอบสายยึดโยงลวดเหล็กตีเกลียว 50 ต.มม. STEEL STRANDED WIRE 50 mm² GUY ASSEMBLY	1	
D-7A	การประกอบสายยึดโยงลวดเหล็กตีเกลียว 95 ต.มม. STEEL STRANDED WIRE 95 mm² GUY ASSEMBLY	4	
D-7C	การประกอบสายยึดโยงลวดเหล็กตีเกลียว 95 ต.มม. STEEL STRANDED WIRE 95 mm² GUY ASSEMBLY	2	
D-9A	สมอบกคอนกรีต CONCRETE ANCHOR	1	
D-10A	ฐานรากเสา POLE FOUNDATION	1	

กองวิศวกรรมไฟฟ้าและเครื่องกล ฝ่ายวิศวกรรม	การไฟฟ้าส่วนภูมิภาค	ใช้แทนแบบ...... ถูกแทนโดยแบบ......
ผู้เขียน...... ผู้สำรวจ...... วิศวกร...... หัวหน้าแผนก...... หัวหน้ากอง...... ผู้อำนวยการฝ่าย......	ผู้ว่าการ...... 24 มี.ค. 23 115 kV วงจรเดี่ยว สายไฟฟ้าเดี่ยว เสาเดี่ยวสำหรับแยกสาย แบบ SS-TL-1	เขียนเสร็จวันที่ 2 ม.ค. 23 แก้แบบวันที่ 15 ก.ย. 40 มิติเป็น...... มาตราส่วน......
รองผู้ว่าการฝ่ายเทคนิค	115 kV SINGLE CIRCUIT SINGLE CONDUCTOR SINGLE POLE, TAP LINE STRUCTURE TYPE SS—TL—1	แบบเลขที่ SAI-015/23003 แผ่นที่ 3 ของจำนวน 3 แผ่น

1 9 มี.ค. 2523