การประกอบเลขที่ 5218
ASSEMBLY NO.

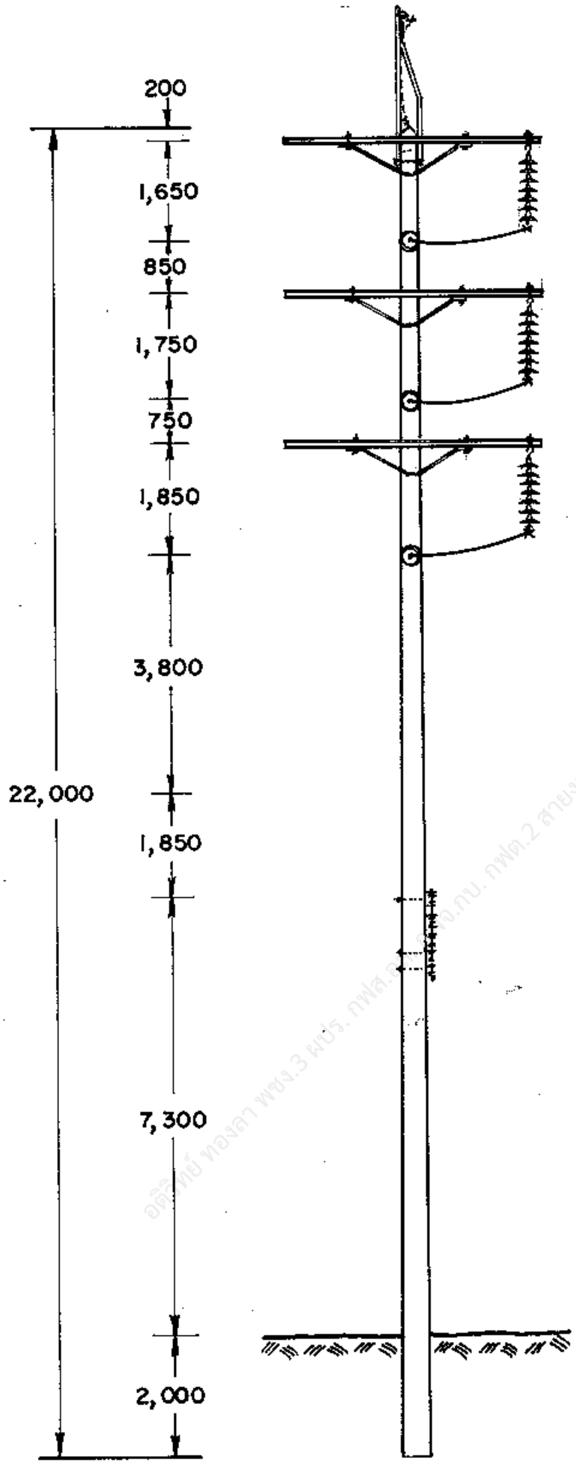

อติวิทย์ ทองลา พชง.3 ผปร. กฟส.[illegible] กบ. กฟต.2 สายงาน (ต) ผวภ. @PEA

กองวิศวกรรมไฟฟ้าและเครื่องกล
ฝ่ายวิศวกรรม

ผู้เขียน สมพง.
ผู้สำรวจ
วิศวกร
หัวหน้าแผนก
ผู้อำนวยการกอง
ผู้อำนวยการฝ่าย

รองผู้ว่าการฝ่ายเทคนิค

การไฟฟ้าส่วนภูมิภาค

ผู้ว่าการ
5 มี.ค. 2537

115 kV วงจรเดี่ยว สายไฟฟ้าเดี่ยว
เสาสำหรับเข้าปลายสายสองข้าง
แบบ SS–DD–2

115 kV SINGLE CIRCUIT SINGLE CONDUCTOR
DOUBLE DEADEND STRUCTURE
TYPE SS–DD–2

ใช้แทนแบบ
ถูกแทนโดยแบบ
เขียนเสร็จวันที่ 15 ธค. 2536
แก้แบบวันที่
มิติเป็น
มาตราส่วน 1 : 125

แบบเลขที่ SAI–015/36009
แผ่นที่ 1 ของจำนวน 3 แผ่น

การประกอบเลขที่
ASSEMBLY NO. 5218

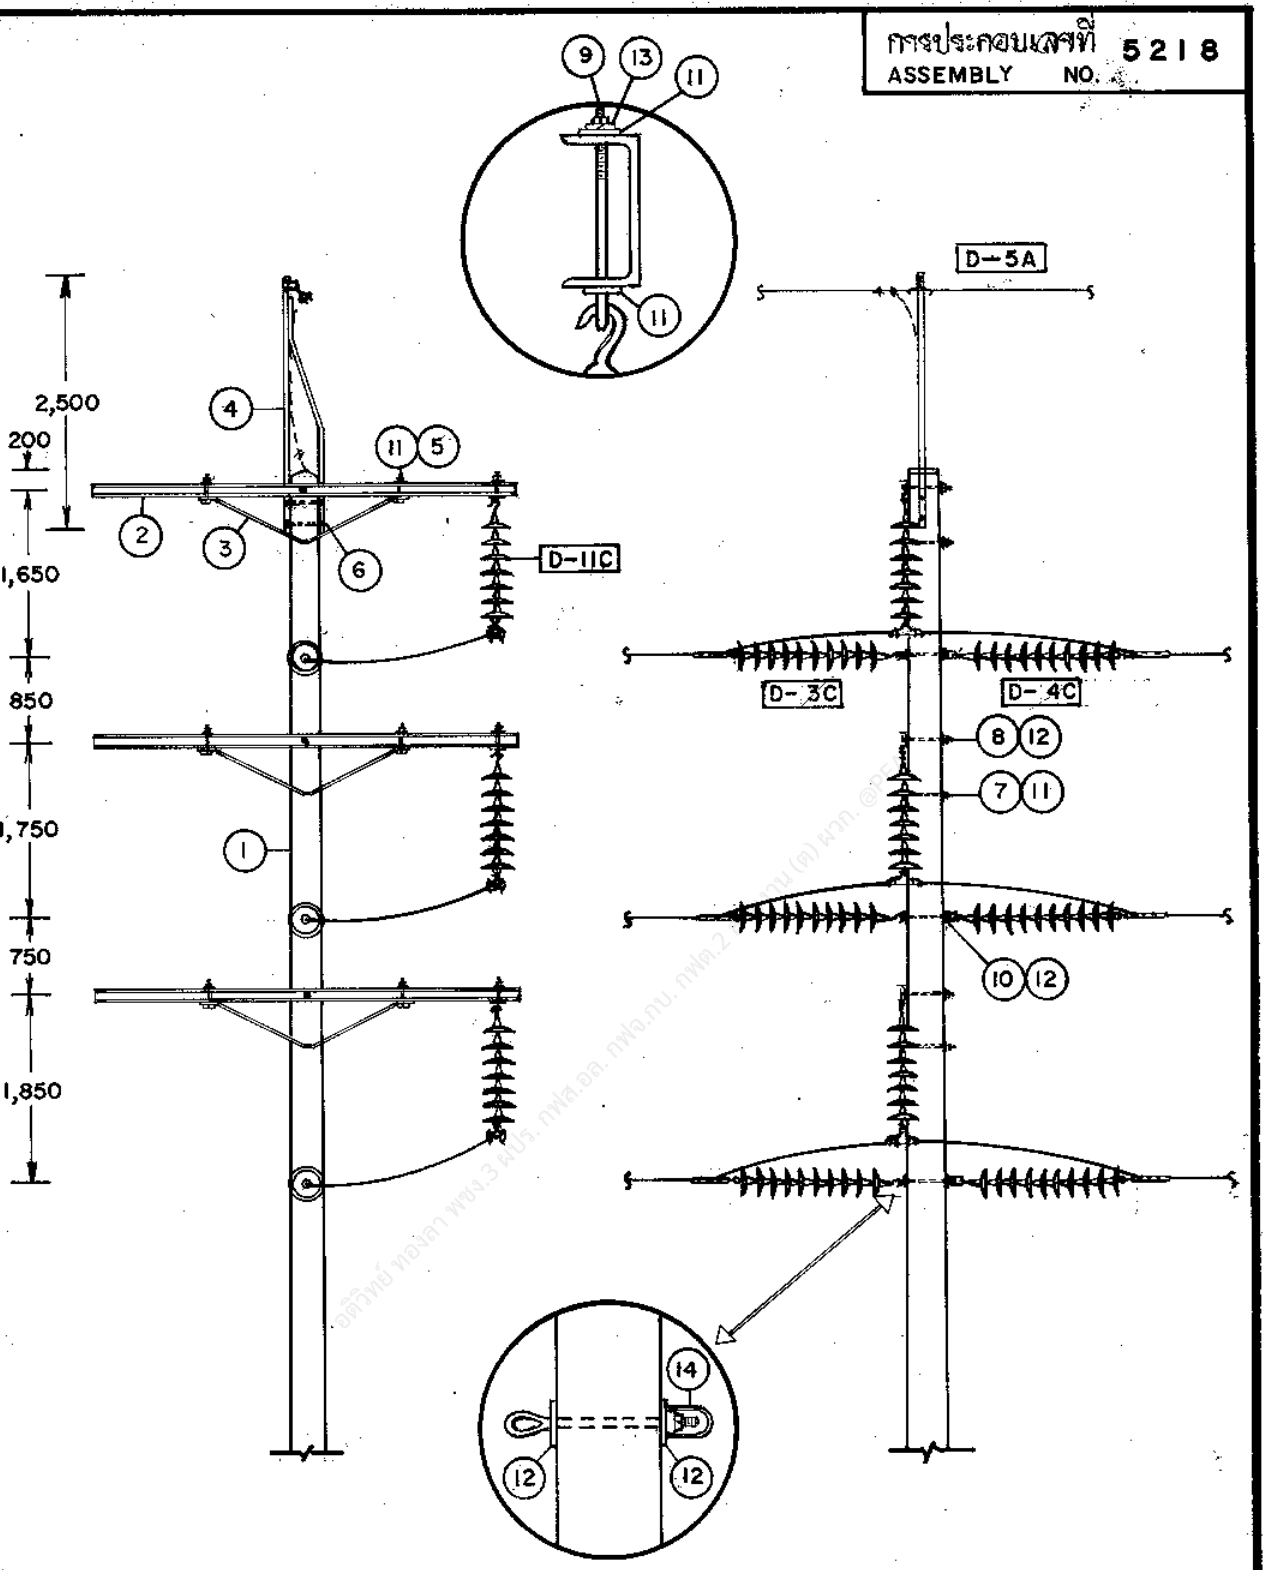

กองวิศวกรรมไฟฟ้าและเครื่องกล ฝ่ายวิศวกรรม	**การไฟฟ้าส่วนภูมิภาค**	ใช้แทนแบบ ถูกแทนโดยแบบ
ผู้เขียน ผู้สำรวจ วิศวกร หัวหน้าแผนก ผู้อำนวยการกอง ผู้อำนวยการฝ่าย	ผู้ว่าการ	เขียนเสร็จวันที่ 15 ธค. 2536 แก้แบบวันที่
	115 kV วงจรเดี่ยว สายไฟฟ้าเดี่ยว เสาสำหรับเข้าปลายสายสองข้าง แบบ SS-DD-2	มิติเป็น มิลลิเมตร มาตราส่วน 1 : 75
รองผู้ว่าการฝ่ายเทคนิค	115 kV SINGLE CIRCUIT SINGLE CONDUCTOR DOUBLE DEADEND STRUCTURE TYPE SS-DD-2	แบบเลขที่ SAI-015/36009 แผ่นที่ 2 ของจำนวน 3 แผ่น

การประกอบเลขที่
ASSEMBLY NO. **5218**

บัญชีวัสดุ
BILL OF MATERIAL

ลำดับที่ ITEM	รายละเอียด DESCRIPTION	จำนวน REQ'D	วัสดุเลขที่ MAT. NO.
1	เสาคอนกรีต 22 ม. POLE, CONCRETE 22 m LONG	1	00010011 (0041)
2	คอนสายแบบเหล็กรูปรางน้ำ ขนาด 100X50X5 มม. ยาว 4.20 ม. มอก. 116 CROSSARM, STEEL, CHANNEL 100X50X5 mm, 4.20 m LONG TIS 116	3	
3	เหล็กฉากรับคอนสาย ขนาด 50X50X6 มม. ช่วงกว้าง 1,800 มม. ดรอพ 450 มม. BRACE, ANGLE STEEL 50X50X6 mm, 1,800 mm WIDE 450 mm DROP	3	00120007 (0119)
4	เหล็กฉากรับสายล่อฟ้าทางโค้ง OVERHEAD GROUND WIRE BAYONET	1	01010005 (0136)
5	สลักเกลียว M 16X130 มม. BOLT, MACHINE, M 16X130 mm	6	01110200 (0220)
6	สลักเกลียว M 16X300 มม. BOLT, MACHINE, M 16X300 mm	3	01110204 (0224)
7	สลักเกลียว M 16X350 มม. BOLT, MACHINE, M 16X350 mm	3	01110205 (0225)
8	สลักเกลียว M 20X350 มม. BOLT, MACHINE, M 20X350 mm	3	01110300
9	สลักห่วงโอแวล M 16X150 มม. BOLT, OVAL EYE M 16X150 mm	3	01150000 (0257)
10	สลักห่วงโอแวล M 20X350 มม. BOLT, OVAL EYE M 20X350 mm	3	01150100 (0260)
11	แหวนสี่เหลี่ยมแบน 52X52X4.5 มม. รู ø 18 มม. มอก. 258 WASHER, SQUARE, FLAT 52X52X4.5 mm HOLE ø 18 mm TIS 258	15	01180100 (0355)
12	แหวนสี่เหลี่ยมแบน 62X62X6 มม. รู ø 22 มม. มอก. 258 WASHER, SQUARE, FLAT 62X62X6 mm HOLE ø 22 mm TIS 258	12	01180101 (0356)
13	แหวนสปริง M 16 มอก. 259 WASHER, LOCK M 16 TIS 259	3	01180301 (0365)
14	อายเล็ท สำหรับสลักเกลียว M 20 EYELET FOR BOLT, M 20	3	01180002 (0346)
D-3C	การประกอบลูกถ้วยแขวน SUSPENSION INSULATOR ASSEMBLY	3	
D-4C	การประกอบลูกถ้วยแขวน SUSPENSION INSULATOR ASSEMBLY	3	
D-11C	การประกอบลูกถ้วยแขวน SUSPENSION INSULATOR ASSEMBLY	3	
D-5A	การต่อสายล่อฟ้า OVERHEAD GROUND WIRE CONNECTION	1	
D-10A	ฐานรากเสา POLE FOUNDATION	1	

กองวิศวกรรมไฟฟ้าและเครื่องกล
ฝ่ายวิศวกรรม

ผู้เขียน ______
ผู้สำรวจ ______
วิศวกร ______
หัวหน้าแผนก ______
ผู้อำนวยการกอง ______
ผู้อำนวยการฝ่าย ______

รองผู้ว่าการฝ่ายเทคนิค

การไฟฟ้าส่วนภูมิภาค

ผู้ว่าการ ______ 5 มี.ค. 2537

115 kV วงจรเดี่ยว สายไฟฟ้าเดี่ยว
เสาสำหรับเข้าปลายสายสองข้าง
แบบ SS-DD-2

115 kV SINGLE CIRCUIT SINGLE CONDUCTOR
DOUBLE DEADEND STRUCTURE
TYPE SS-DD-2

ใช้แทนแบบ ______
ถูกแทนโดยแบบ ______
เขียนเสร็จวันที่ 15 ธค. 2536
แก้แบบวันที่ ______
มิติเป็น ______
มาตราส่วน ______

แบบเลขที่ SAI-015/36009
แผ่นที่ 3 ของจำนวน 3 แผ่น