

การประกอบเลขที่
ASSEMBLY NO. 3217

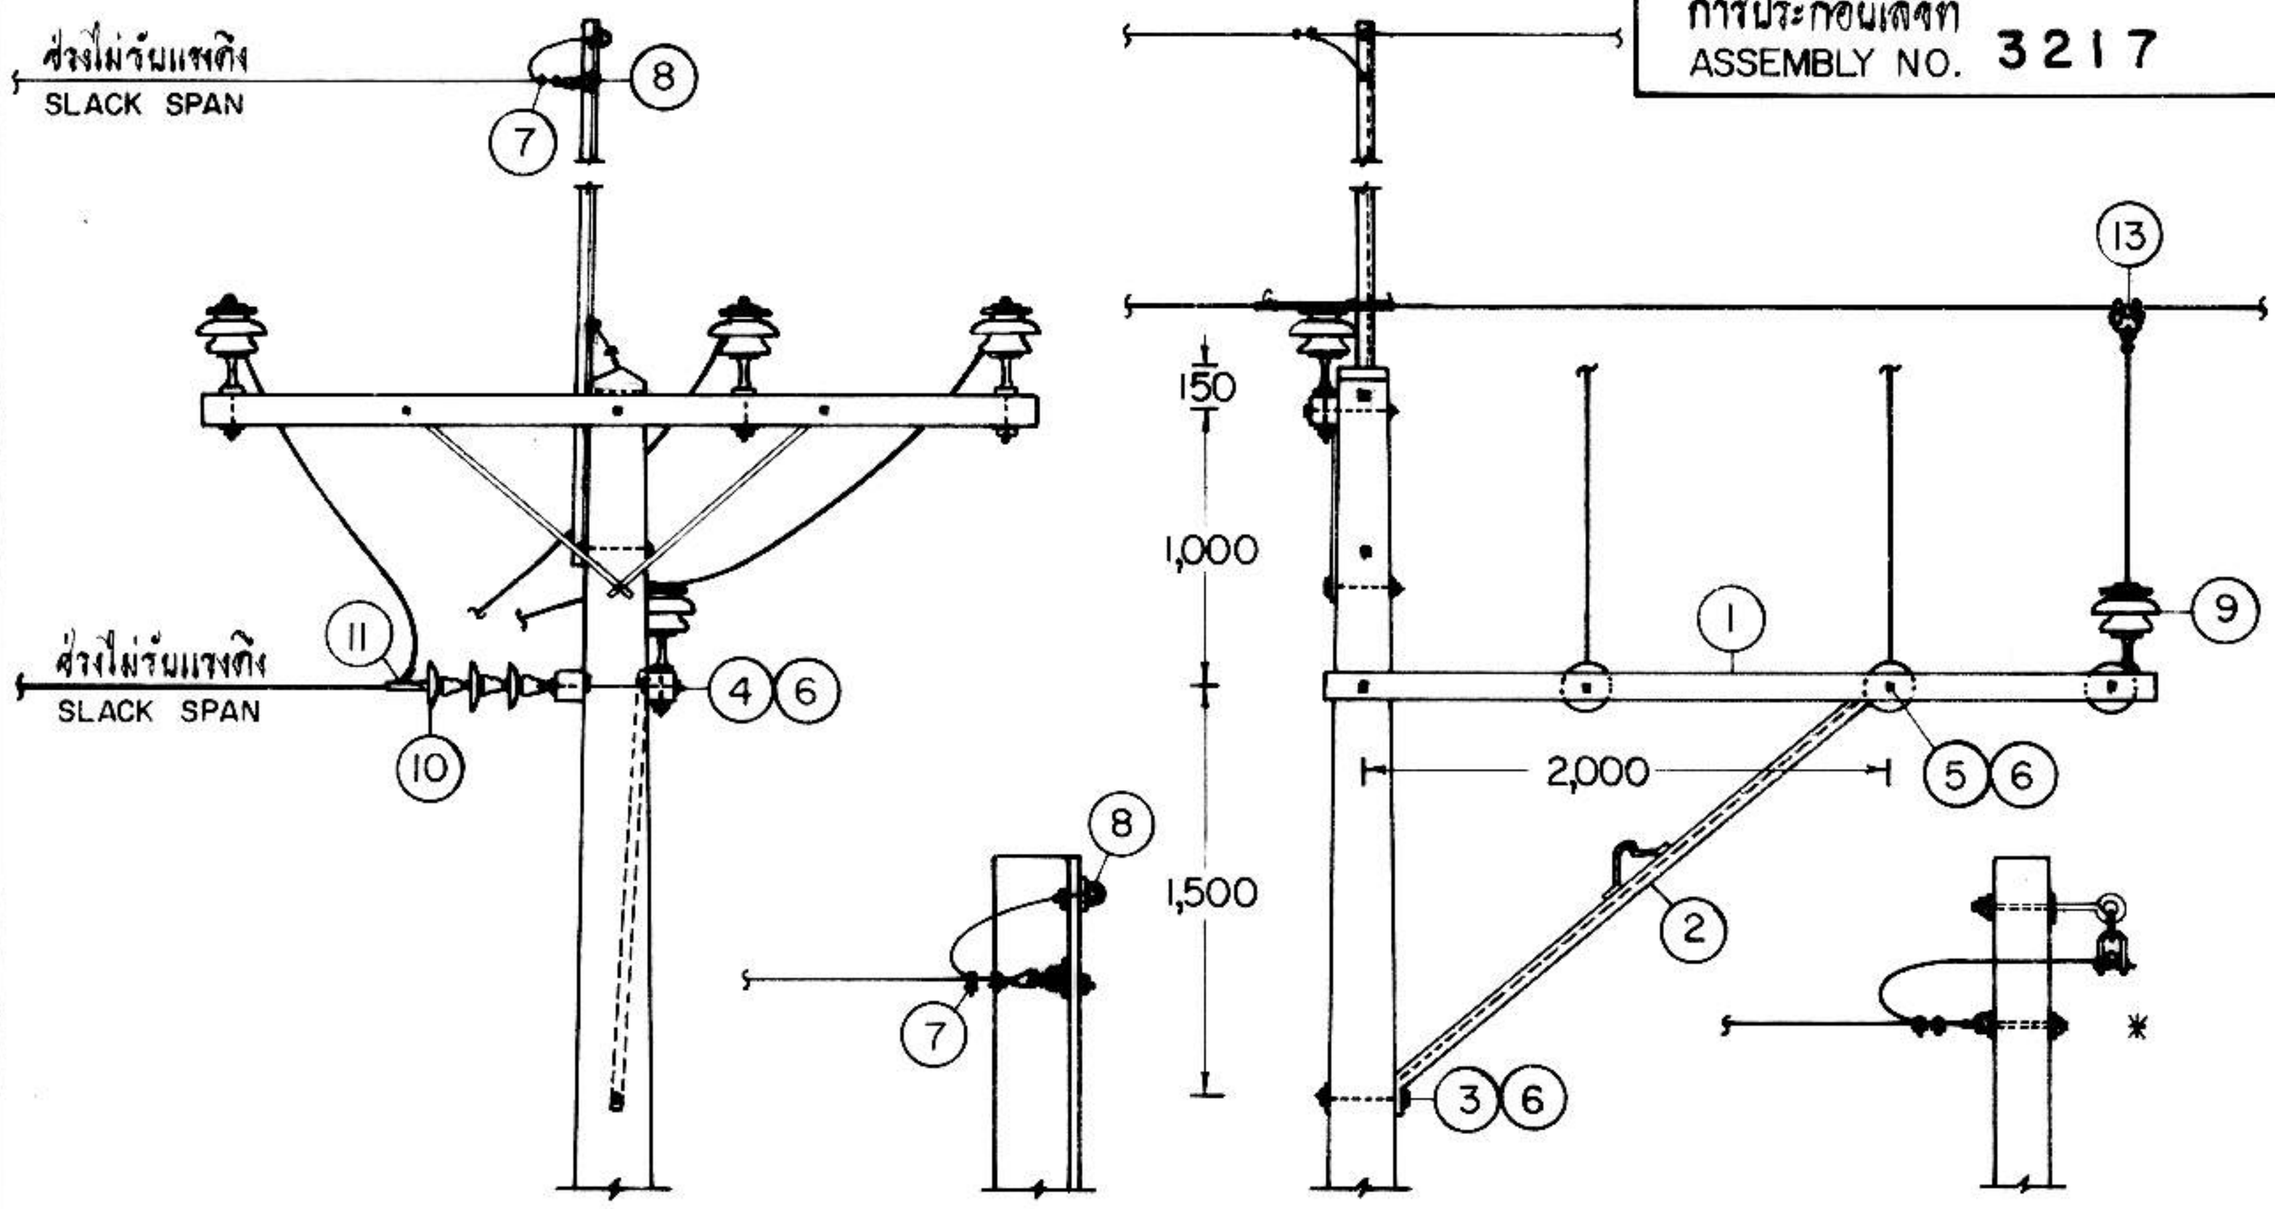

แบบที่ I สำหรับการต่อตรง
TYPE I FOR DIRECT CONNECTION

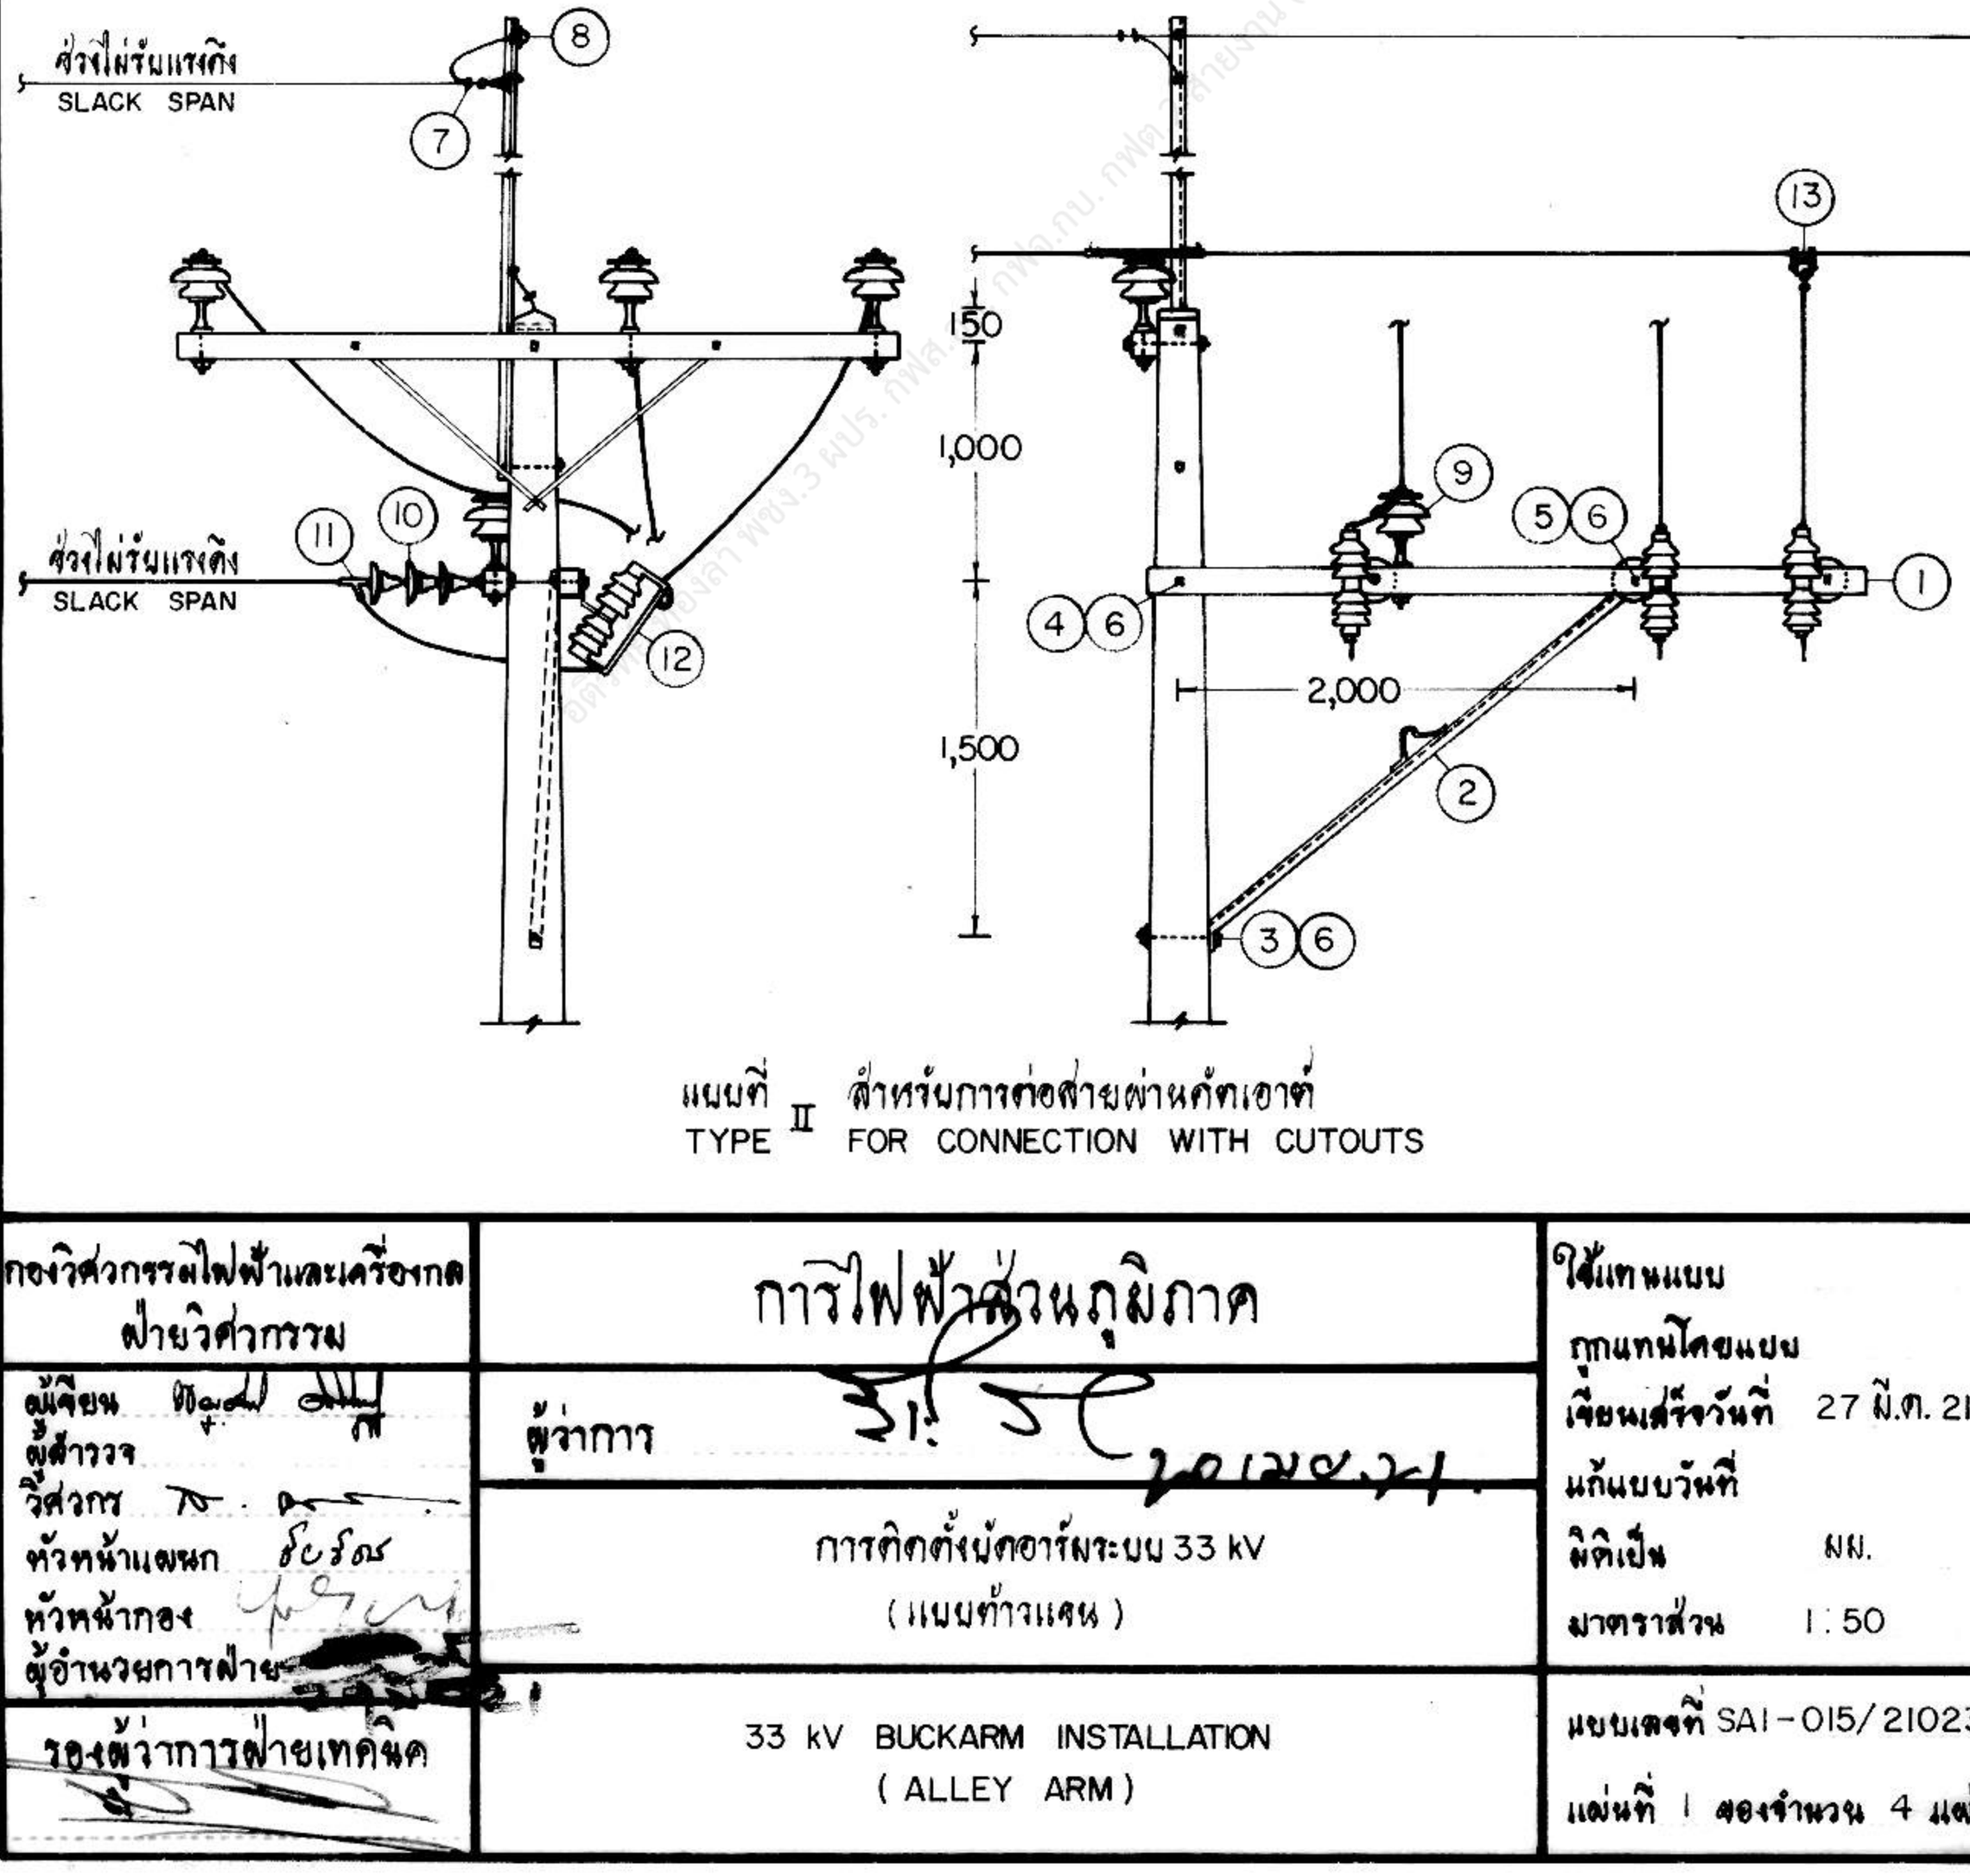


แบบที่ II สำหรับการต่อสายผ่านคัตเอาต์
TYPE II FOR CONNECTION WITH CUTOUTS


กองวิศวกรรมไฟฟ้าและเครื่องกล ฝ่ายวิศวกรรม	การไฟฟ้าส่วนภูมิภาค	ใช้แทนแบบ ถูกแทนโดยแบบ เขียนเสร็จวันที่ 27 มี.ค. 21 แก้แบบวันที่ มิติเป็น มม. มาตราส่วน 1 : 50
ผู้เขียน ผู้สำรวจ วิศวกร หัวหน้าแผนก หัวหน้ากอง ผู้อำนวยการฝ่าย	ผู้ว่าการ การติดตั้งบัคอาร์มระบบ 33 kV (แบบท้าวแสน)	
รองผู้ว่าการฝ่ายเทคนิค	33 kV BUCKARM INSTALLATION (ALLEY ARM)	แบบเลขที่ SAI-015/21023 แผ่นที่ 1 ของจำนวน 4 แผ่น

แผนแนะนำการติดตั้งบัคอาร์ม (แผนท้าวแสน)
APPLICATION OF BUCKARM (ALLEY ARM) INSTALLATION


การประกอบเลขที่ ASSEMBLY NO. 3217

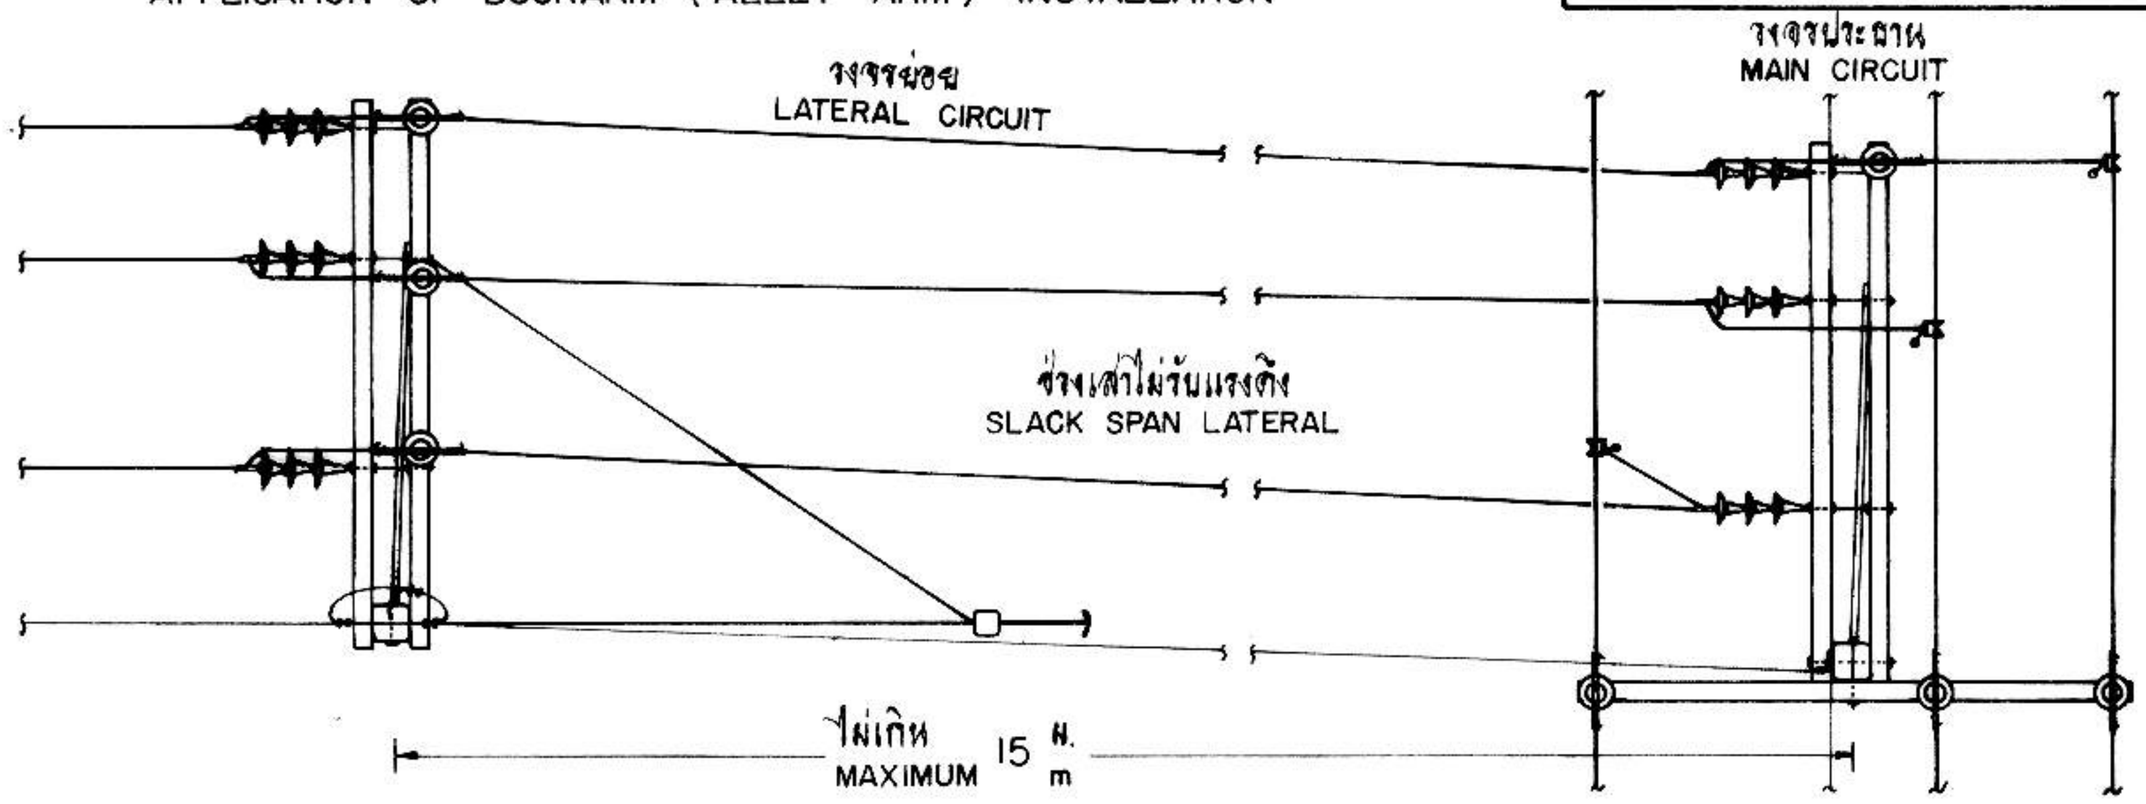

ลักษณะที่ 1
FEATURE

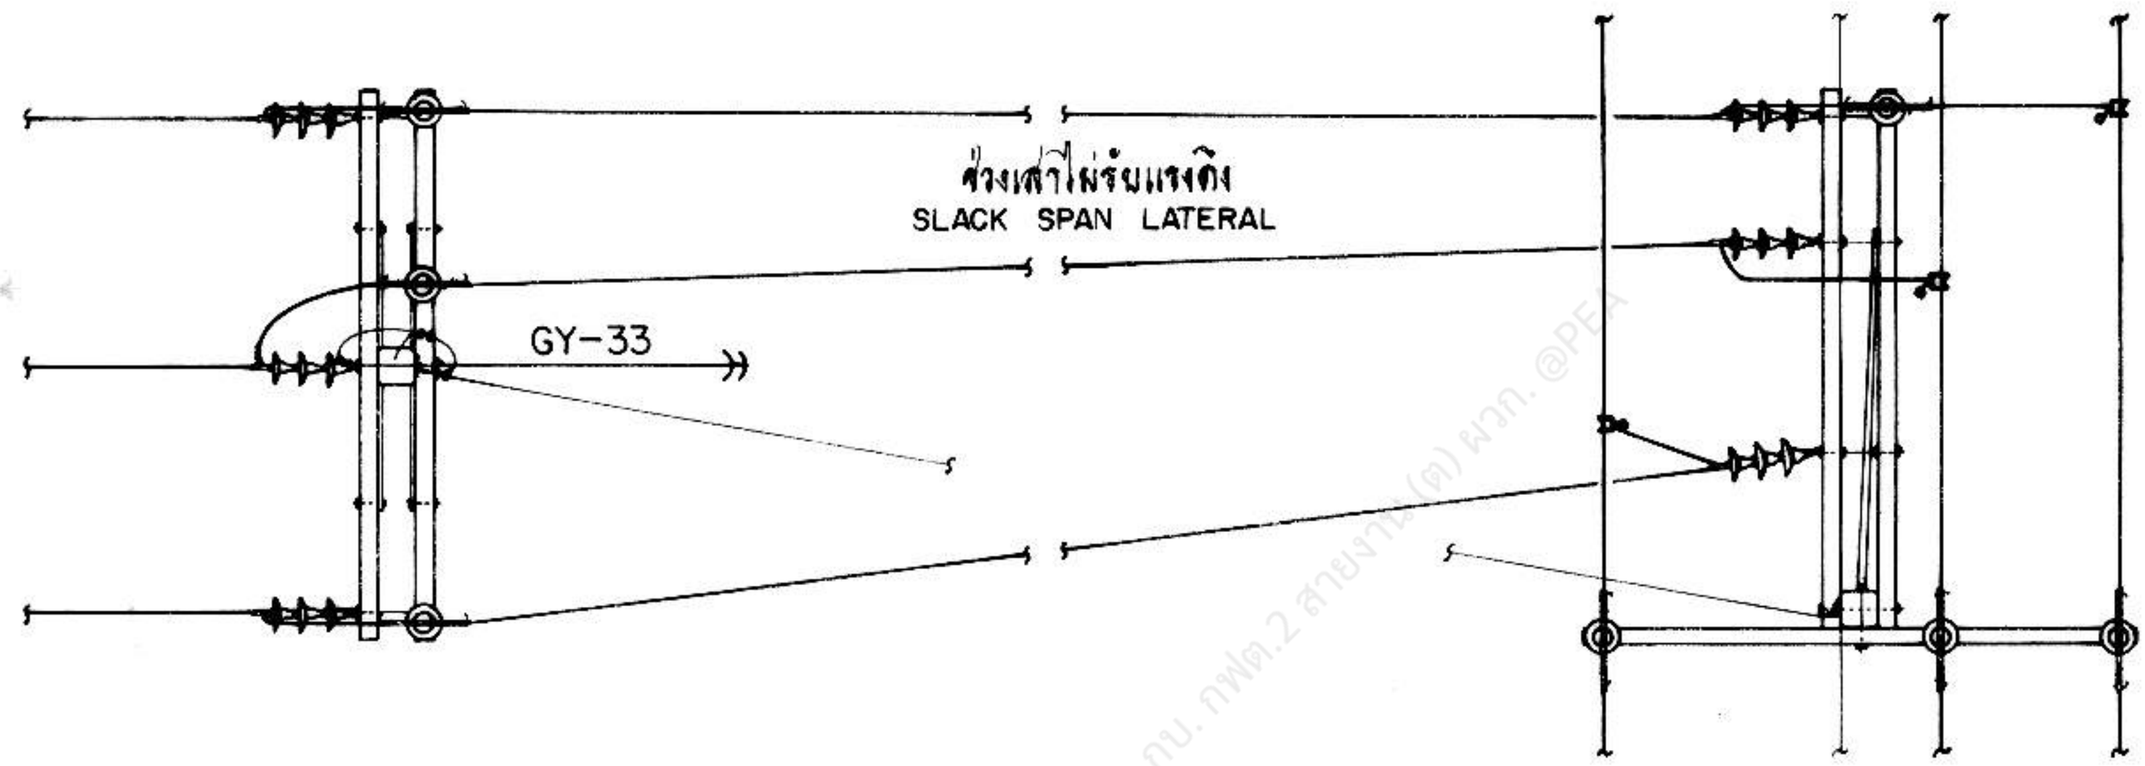

ลักษณะที่ 2
FEATURE

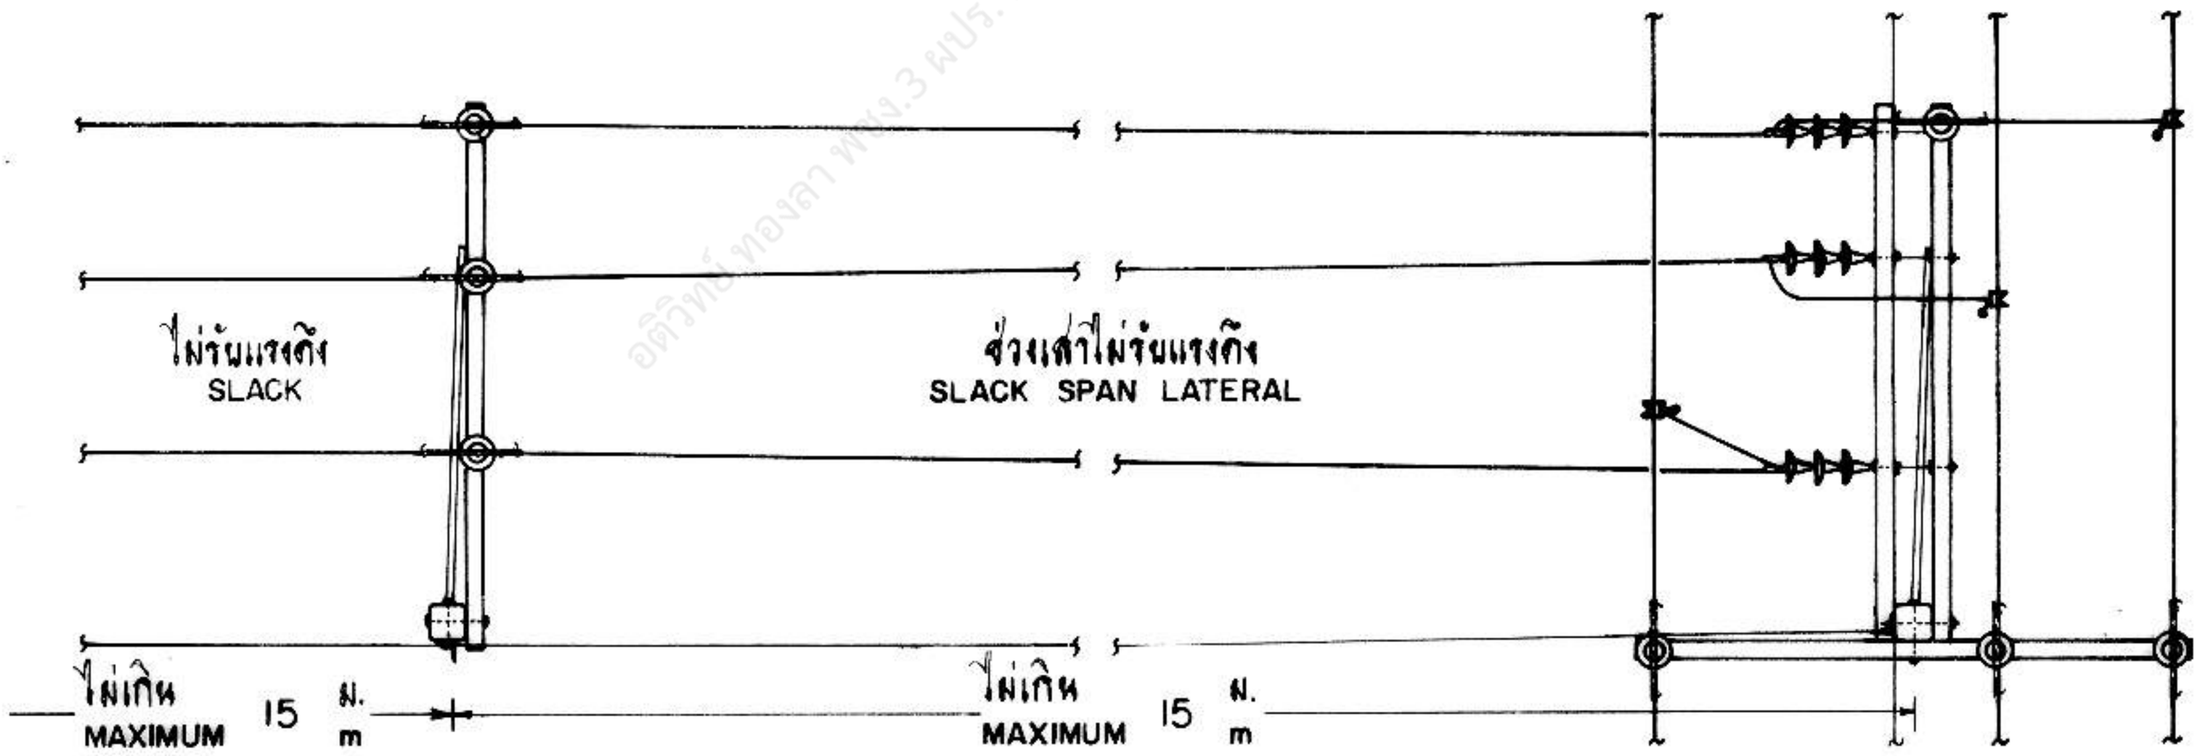

ลักษณะที่ 3
FEATURE

กองวิศวกรรมไฟฟ้าและเครื่องกล ฝ่ายวิศวกรรม	การไฟฟ้าส่วนภูมิภาค	ใช้แทนแบบ ถูกแทนโดยแบบ เขียนเสร็จวันที่ 27 มี.ค. 21 แก้แบบวันที่ มิติเป็น มาตราส่วน 1:75
ผู้เขียน ผู้สำรวจ วิศวกร หัวหน้าแผนก หัวหน้ากอง ผู้อำนวยการฝ่าย	ผู้ว่าการ 20 เม.ย. 21	
รองผู้ว่าการฝ่ายเทคนิค	การติดตั้งบัคอาร์มระพน 33 kV (แผนท้าวแสน) 33 kV BUCKARM INSTALLATION (ALLEY ARM)	แบบเลขที่ SAI-015/21023 แผ่นที่ 2 ของจำนวน 4 แผ่น

การประกอบเลขที่ ASSEMBLY NO. 3217

บัญชีวัสดุ
BILL OF MATERIAL

ลำดับที่ ITEM	รายละเอียด DESCRIPTION	จำนวน REQ'D I	จำนวน REQ'D II	วัสดุเลขที่ MAT. NO.
1	ไม้คอนสายแรงสูง 100 X 120 X 3,000 มม. CROSSARM, WOOD, H.T. 100 X 120 X 3,000 mm	2	2	00100003 (0101)
2	เหล็กประกับไม้คอนแบบท้าวแขน 50 X 50 X 5 มม. ยาว 2,350 มม. BRACE, ALLEY ARM 50 X 50 X 5 mm 2,350 mm LONG	1	1	01200005 (0125)
3	สลักเกลียว M 16 X 200 มม. BOLT, MACHINE, M 16 X 200 mm	1	1	01110202 (0222)
4	สลักเกลียว M 16 X 450 มม. BOLT, MACHINE, M 16 X 450 mm	1	1	01110207 (0227)
5	สลักเกลียวห่วงกลม M 16 X 450 มม. BOLT, DOUBLE ARMING, ROUND EYE M 16 X 450 mm	3	3	01130001 (0247)
6	แหวนสี่เหลี่ยมแบน 52X52X4.5 มม.รู Ø 18 มม. มอก. 258 WASHER, SQUARE FLAT 52X52X4.5 mm HOLE Ø 18 mm TIS 258	14	14	01180100 (0355)
7	ยูแคล้มป์ สลัก 1 ตัว M 8 (ไวร์โรป คลิพ) CLAMP, SINGLE U-BOLT, M 8 (WIRE ROPE CLIP)	4	4	01230000 (0165)
8*	กราวด์ไวร์แคล้มป์ แบบ J 1152 GROUND WIRE CLAMP J 1152	1	1	01230205 (0296)
9	ลูกถ้วยก้านตรง 33 kV มอก. 279 แบบ ค (แบบ 56-3) พร้อมก้าน INSULATOR, PIN TYPE 33 kV TIS 279 TYPE C (CLASS 56-3) COMP. WITH PIN	1	1	03000002 03100001
10	ลูกถ้วยแขวน มอก. 354 แบบ ง (แบบ 52-4) INSULATOR, SUSPENSION TYPE TIS 354 TYPE D (CLASS 52-4)	9	9	03020002 (0415)
11	สเตรนแคล้มป์ สำหรับสายอะลูมิเนียม อะลูมิเนียมแกนเหล็ก และอะลูมิเนียมอัลลอย CLAMP, STRAIN FOR AI, ACSR AND AI-ALLOY CONDUCTOR	3	3	03110000 - 03110101
12	ครอพเอาต์ ฟิวส์คัตเอาต์ หนึ่งอินซูเลเตอร์ 33 kV, 100 แอมป์ CUT-OUT, FUSE, OPEN TYPE, SINGLE INSULATOR DROP-OUT 33 kV 100A	-	3	04010101 (1426)
13	สเตอร์รัพแคล้มป์ หรือเบลแคล้มป์ และฮอทไลน์แคล้มป์ ขนาดตามต้องการ CLAMP, STIRRUP OR BAIL CLAMP, HOT LINE, SIZE AS REQUIRED	3	3	02330000-1 02330100-1

อติวิทย์ ทองลา พง.3 ... @PEA

กองวิศวกรรมไฟฟ้าและเครื่องกล ฝ่ายวิศวกรรม	การไฟฟ้าส่วนภูมิภาค	ใช้แทนแบบ ถูกแทนโดยแบบ เขียนเสร็จวันที่ 27 มิ.ค. 21 แก้แบบวันที่ มิติเป็น มาตราส่วน
ผู้เขียน ผู้สำรวจ วิศวกร หัวหน้าแผนก หัวหน้ากอง ผู้อำนวยการฝ่าย ของผู้ว่าการฝ่ายเทคนิค	ผู้ว่าการ 20 มิ.ย. 21 การติดตั้งผัคอาร์มระบบ 33 kV (แบบท้าวแขน) 21 33 kV BUCKARM INSTALLATION (ALLEY ARM)	แบบเลขที่ SAI-015/21023 แผ่นที่ 3 ของจำนวน 4 แผ่น

การประกอบเลขที่ ASSEMBLY NO.	3217

หมายเหตุ
1. ระยะระหว่างช่วงเสาไม่รับแรงดึง ไม่เกิน 15 ม. ระยะหย่อนยานของสายไฟฟ้า และสายล่อฟ้า ประมาณ 0.70 ม.
2. สำหรับการยึดโยงแบบสมัย เสาต้นปลายสายแบบท้าวแขน ดูแบบเลขที่ SAI-015/20023 แผ่นที่ 11
3. * ในกรณีใช้ไม้คอนรับสายล่อฟ้า ให้ใช้สลักห่วงกลม M 16 X 200 มม. กายทิมเบิ้ลอย่างละ 1 ตัว และแหวนสี่เหลี่ยมแบน 2 อัน แทน
4. การติดตั้งบัคอาร์ม (แบบท้าวแขน) ปกติให้ติดตั้งตามลักษณะที่ 1 และที่ 2 สำหรับการติดตั้งตามลักษณะที่ 3 ให้ใช้ในกรณีไม่สามารถทำการยึดโยงเสาแยกต้นแรกได้ (ถ้าขนาดสายไฟฟ้าของวงจรย่อยไม่เกิน 50 ต.มม. ระยะระหว่างเสาของวงจรย่อยสามารถเพิ่มเป็น 20 ม. ได้)

NOTES
1. MAXIMUM SLACK SPAN LATERAL 15 m SAG OF CONDUCTORS AND OVERHEAD GROUND WIRE ARE APPROX 0.70 m.
2. FOR DEADEND ALLEY ARM STUB GUY SEE DWG. NO. SAI-015/20023 SHEET 11
3. * FOR WOOD BAYONET, ONE ROUND EYE BOLT M 16 X 200 mm, ONE GUY THIMBLE AND TWO SQUARE WASHERS SHALL BE USED INSTEAD.
4. BUCKARM (ALLEY ARM) INSTALLATION FEATURE 1 AND 2 ARE PREFERABLE. IN CASE OF FIRST LATERAL LINE POLE CAN NOT BE GUYED, INSTALLATION FEATURE 3 MAY BE APPLIED. (LATERAL SPAN LENGTH CAN BE EXPANDED TO 20 m IF CONDUCTOR SIZE OF LATERAL LINES ARE NOT LARGER THAN 50 mm^2)

กองวิศวกรรมไฟฟ้าและเครื่องกล ฝ่ายวิศวกรรม	การไฟฟ้าส่วนภูมิภาค	ใช้แทนแบบ ถูกแทนโดยแบบ เขียนเสร็จวันที่ 27 มี.ค. 21 แก้แบบวันที่ มิติเป็น มาตราส่วน
ผู้เขียน ผู้สำรวจ วิศวกร หัวหน้าแผนก หัวหน้ากอง ผู้อำนวยการฝ่าย	ผู้ว่าการ 20/มี.ค./21	
รองผู้ว่าการฝ่ายเทคนิค	การติดตั้งบัคอาร์มระบบ 33 kV (แบบท้าวแขน) 33 kV BUCKARM INSTALLATION (ALLEY ARM)	แบบเลขที่ SAI-015/21023 แผ่นที่ 4 ของจำนวน 4 แผ่น