การประกอบเลขที่ ASSEMBLY NO.	5686

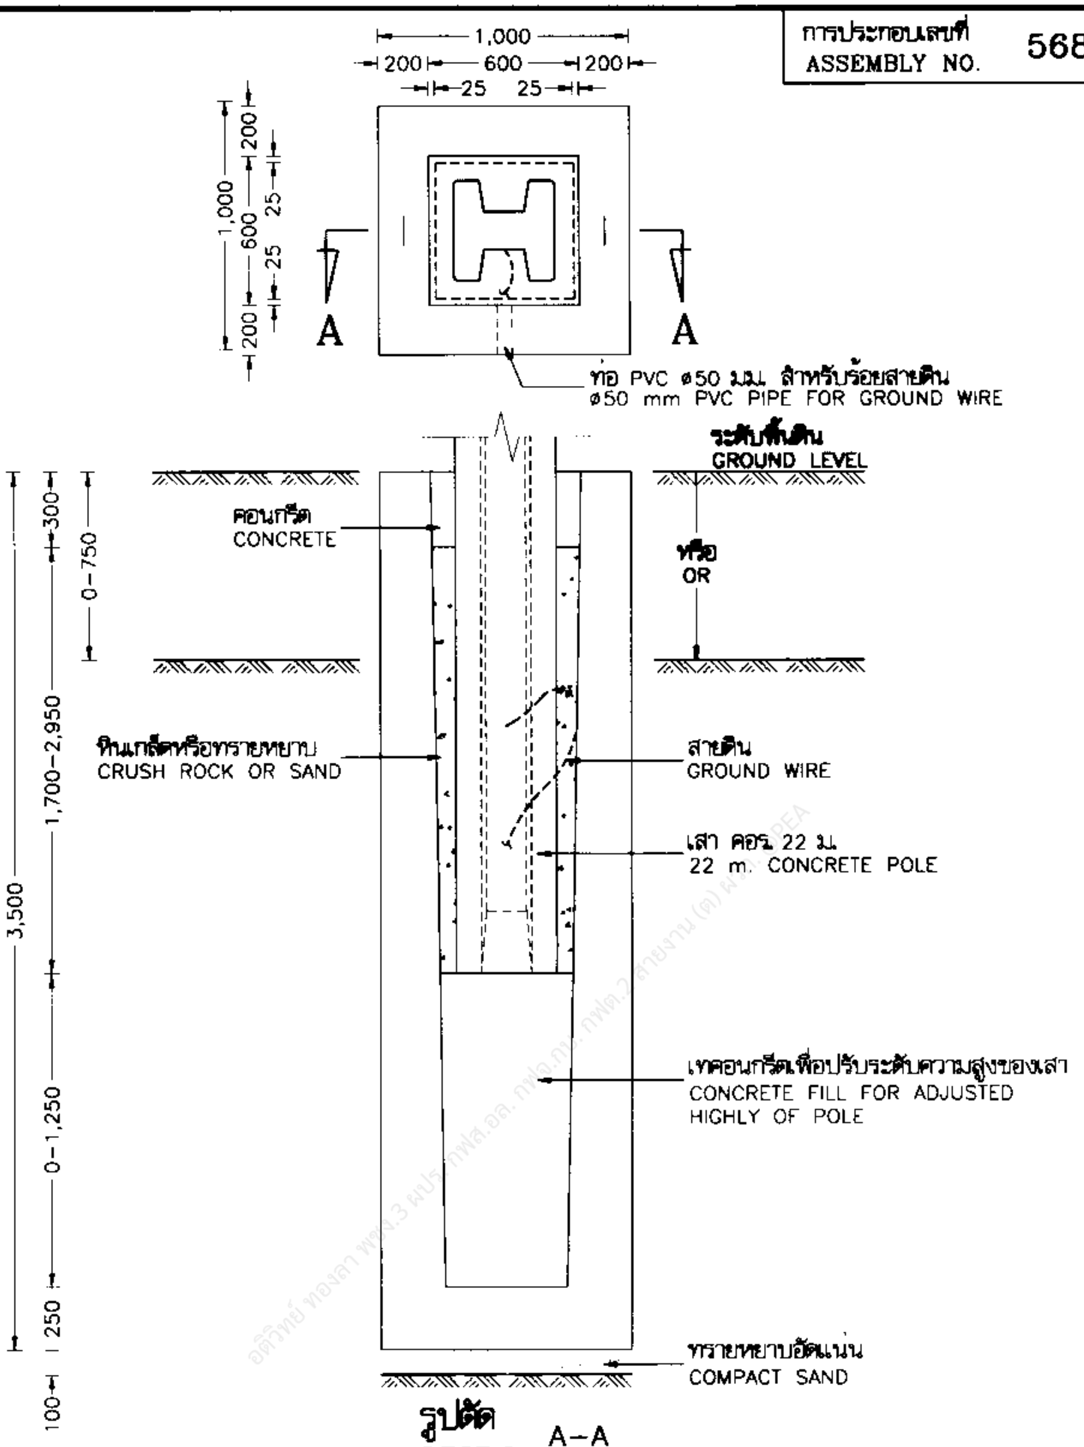

รูปตัด
SECTION A–A

อดิวิทย์ ทองลา พชง.3 ผปร. กฟส.อล. กฟจ.กพ. กฟต.2 สายงาน (ต) ผปร.PEA

หมายเหตุ

1. ฐานรากเสานี้ใช้ในกรณีดินสามารถรับน้ำหนักปลอดภัยได้ตั้งแต่ 10 ตัน/ตารางเมตรขึ้นไป
2. ฐานรากนี้เป็นแบบที่ทำสำเร็จรูปแล้วจึงนำไปติดตั้ง
3. ดูรายละเอียดเพิ่มเติมแบบเลขที่ IB2-018/39016

NOTES

1. THIS FOUNDATION USE ONLY IN CASE ALLOWABLE SOIL BEARING CAPACITY OF 10 TON/m^2 OR MORE.
2. THIS FOUNDATION IS PRECAST TYPE.
3. SEE ADDITIONAL DETAIL, DWG.NO. IB2-018/39016.

กองวิศวกรรมไฟฟ้าและเครื่องกล ฝ่ายวิศวกรรม	การไฟฟ้าส่วนภูมิภาค	ใช้แทนแบบ.............. ถูกแทนโดยแบบ..........
ผู้เขียน B. Suppl... ผู้สำรวจ.................... วิศวกร.................... หัวหน้าแผนก.................... ผู้อำนวยการกอง.................... ผู้อำนวยการฝ่าย....................	ผู้ว่าการ .... 2540 รายละเอียดที่ 10F ฐานรากเสา (แบบที่ 1 ชนิดสำเร็จรูป)	เขียนเสร็จวันที่.......... แก้แบบวันที่ .... มิติเป็น.............. มาตราส่วน.....1 : 30.....
รองผู้ว่าการ	DETAIL 10F POLE FOUNDATION (TYPE 1, PRECAST TYPE)	แบบเลขที่ SA1-015/40010 แผ่นที่ 1 ของจำนวน 3 แผ่น

2540

การประกอบเลขที่ ASSEMBLY NO.	5686

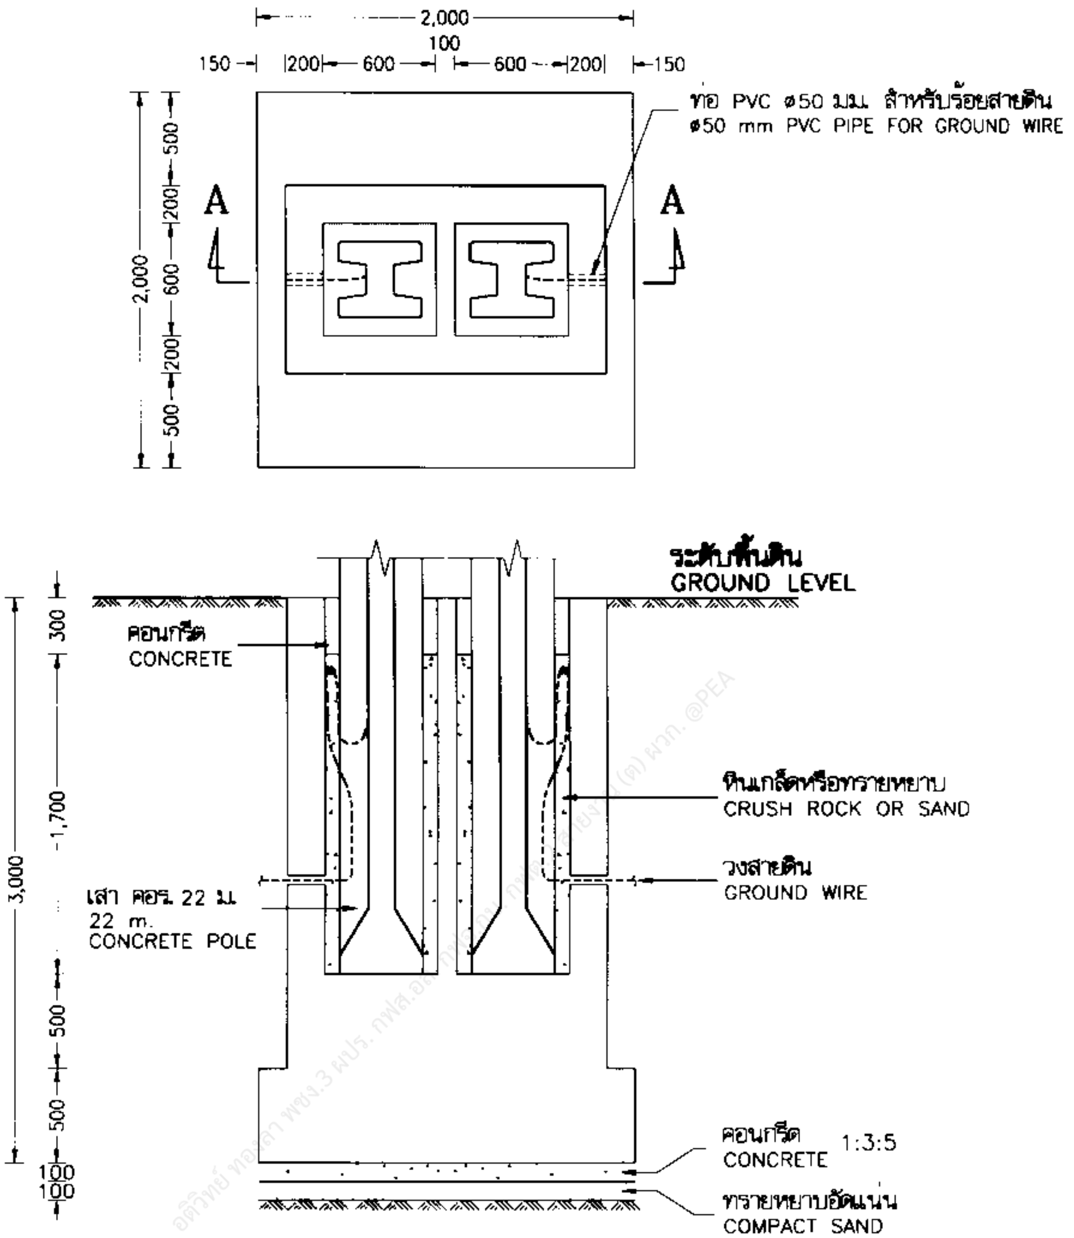

รูปตัด A–A
SECTION A–A

อดิวิทย์ ทองสา พชง.3 ผปร. กฟส.อ... (ต) ผวก. @PEA

หมายเหตุ

1. ฐานรากเสานี้ใช้ในกรณีดินสามารถรับน้ำหนักปลอดภัยได้ตั้งแต่ ๑๐ ตัน/ตารางเมตรขึ้นไป
2. ดูรายละเอียดเพิ่มเติมแบบเลขที่ IB2–018/39018

NOTES

1. THIS FOUNDATION USE ONLY IN CASE ALLOWABLE SOIL BEARING CAPACITY OF 10 TON/m^2 OR MORE.
2. SEE ADDITIONAL DETAIL, DWG.NO. IB2–018/39018.

กองวิศวกรรมไฟฟ้าและเครื่องกล ฝ่ายวิศวกรรม	การไฟฟ้าส่วนภูมิภาค	ใช้แทนแบบ.......... ถูกแทนโดยแบบ..........
ผู้เขียน B. Sup... ผู้สำรวจ.......... วิศวกร.......... หัวหน้าแผนก.......... ผู้อำนวยการกอง.......... ผู้อำนวยการฝ่าย..........	ผู้ว่าการ ... ... เม.ย. 2540 รายละเอียดที่ 10F ฐานรากเสา (แบบที่ 2)	เขียนเสร็จวันที่.......... แก้แบบวันที่.......... มิติเป็น.......... มาตราส่วน 1 : 40
รองผู้ว่าการ	DETAIL 10F POLE FOUNDATION (TYPE 2)	แบบเลขที่ SA1–015/40010 แผ่นที่ 2 ของจำนวน 3 แผ่น

0 ... 2540

การประกอบเลขที่ ASSEMBLY NO.	5686

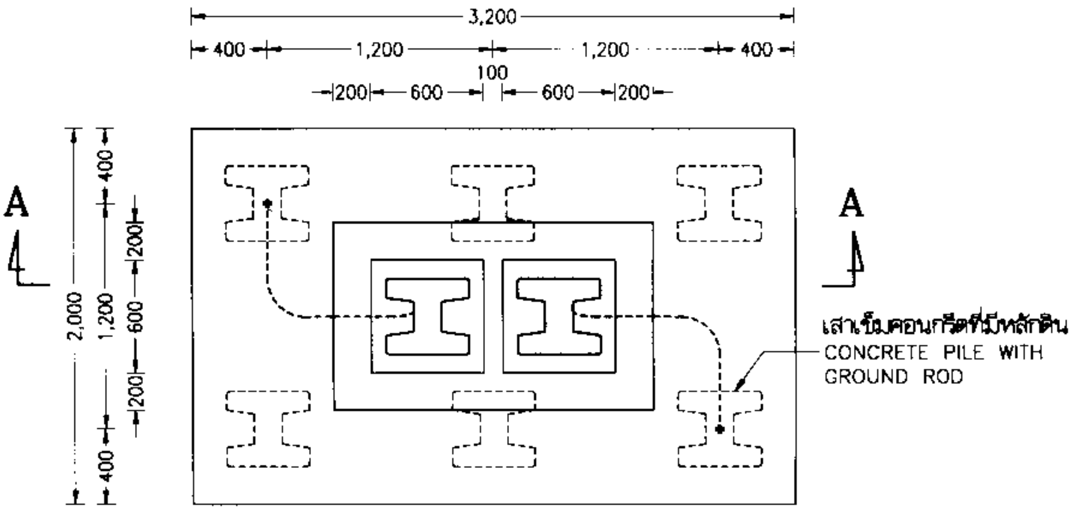

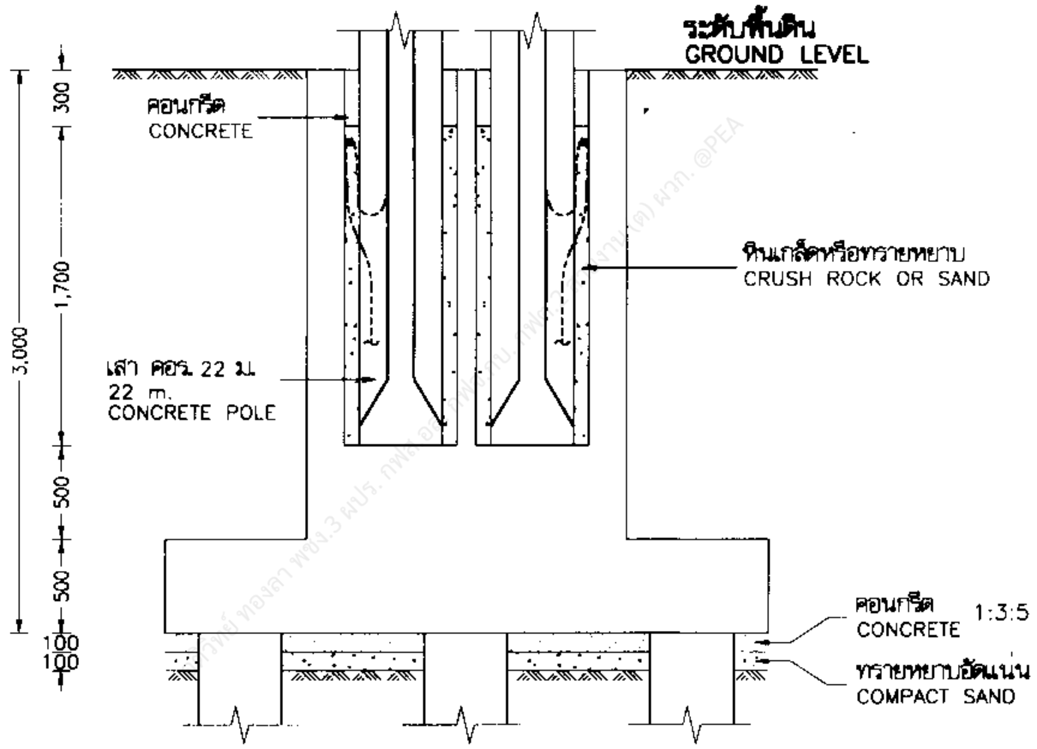

รูปตัด A–A
SECTION

หมายเหตุ

1. ดูรายละเอียดเพิ่มเติมแบบเลขที่ IB2–018/39019

NOTES

1. SEE ADDITIONAL DETAIL, DWG.NO. IB2–018/39019.

กองวิศวกรรมไฟฟ้าและเครื่องกล ฝ่ายวิศวกรรม	การไฟฟ้าส่วนภูมิภาค	ใช้แทนแบบ............... ถูกแทนโดยแบบ............
ผู้เขียน B. S............... ผู้สำรวจ............... วิศวกร............... หัวหน้าแผนก............... ผู้อำนวยการกอง............... ผู้อำนวยการฝ่าย...............	ผู้ว่าการ............... [illegible] 2540 รายละเอียดที่ 10F ฐานรากเสา (แบบที่ 3)	เขียนเสร็จวันที่............... แก้แบบวันที่............... มิติเป็น............... มาตราส่วน.....1 : 40.....
รองผู้ว่าการ	DETAIL 10F POLE FOUNDATION (TYPE 3)	แบบเลขที่ SA1–015/40010 แผ่นที่ 3 ของจำนวน 3 แผ่น

2540