การประกอบเลขที่ **5 2 3 2**
ASSEMBLY NO.

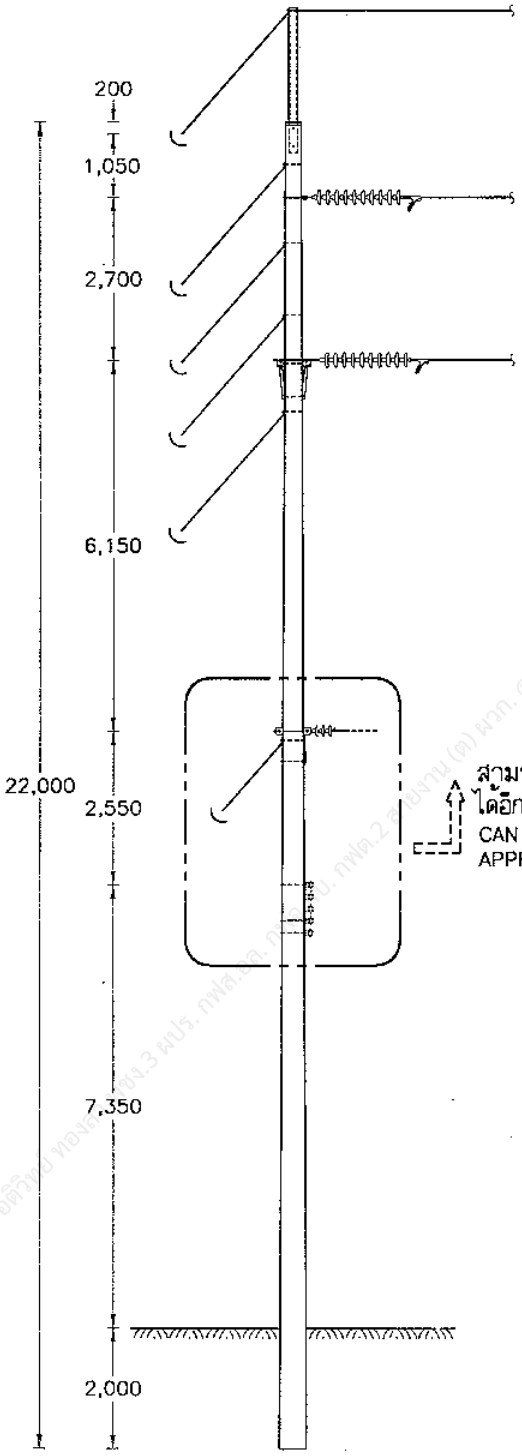

สามารถปรับระดับขึ้น
ได้อีกประมาณ 2.00 ม.
CAN RISE UP THE LEVEL
APPROXIMATELY 2.00 m

อธิวัฒน์ ทอง[illegible] ชง.3 ผปร. กฟส.อล. กฟ[illegible] กฟต.2 สายงาน (ต) ผวก. @PEA

กองวิศวกรรมไฟฟ้าและเครื่องกล
ฝ่ายวิศวกรรม

การไฟฟ้าส่วนภูมิภาค

ใช้แทนแบบ ....
ถูกแทนโดยแบบ ....

ผู้เขียน Supphalit Boonrueng
ผู้สำรวจ...................
วิศวกร...............
หัวหน้าแผนก............(ผทพ)
ผู้อำนวยการกอง..........
ผู้อำนวยการฝ่าย..........

ผู้ว่าการ - 3 ส.ค. 2542

เขียนเสร็จวันที่ 22 ก.พ. 2542
แก้แบบวันที่ ....
มิติเป็น มิลลิเมตร
มาตราส่วน 1 : 125

115 kV วงจรเดี่ยว สายไฟฟ้าเดี่ยว
เสาสำหรับเข้าปลายสาย
แบบ SS-DE--2

รองผู้ว่าการเทคนิคและบริการ
....

115 kV SINGLE CIRCUIT, SINGLE CONDUCTOR
DEADEND STRUCTURE
TYPE SS-DE-2

แบบเลขที่ SA1-015/42005
แผ่นที่ 1 ของจำนวน 4 แผ่น

- 3 ส.ค. 2542

การประกอบเลขที่
ASSEMBLY NO. **5232**

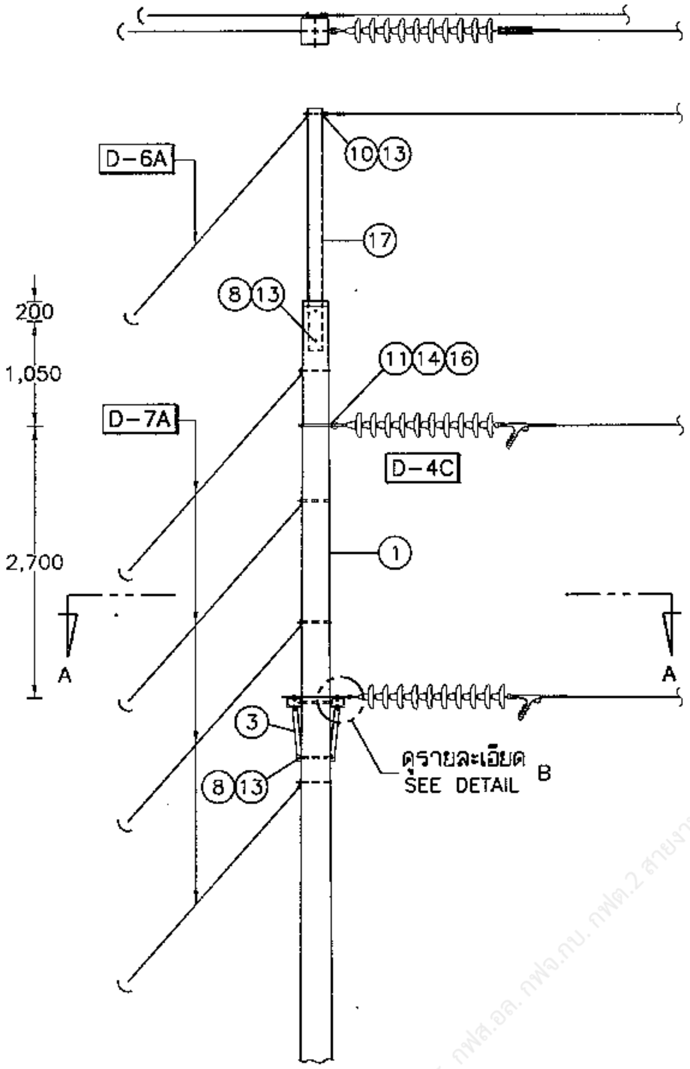

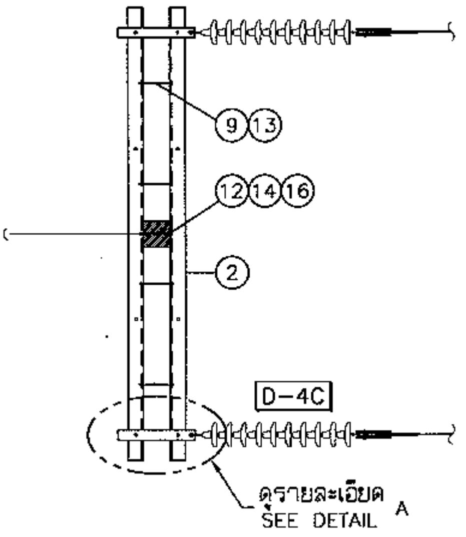

รูปตัด SECTION A–A

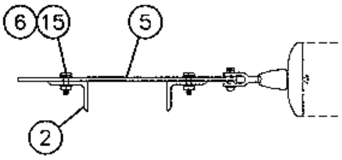

รายละเอียด
DETAIL A

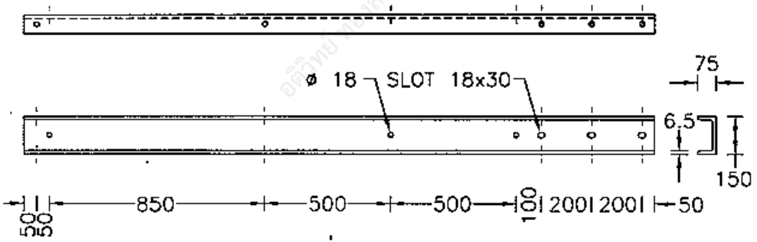

วัสดุลำดับที่
MATERIAL ITEM ⑰

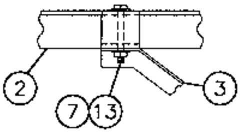

รายละเอียด
DETAIL B

พชง.3 ผปร. กฟส.อล. กฟจ.กบ. กฟต.2 สายงาน (ต) ผวก. @PEA

กองวิศวกรรมไฟฟ้าและเครื่องกล
ฝ่ายวิศวกรรม

ผู้เขียน
ผู้สำรวจ
วิศวกร
หัวหน้าแผนก
ผู้อำนวยการกอง
ผู้อำนวยการฝ่าย
รองผู้ว่าการเทคนิคและบริการ

การไฟฟ้าส่วนภูมิภาค

ผู้ว่าการ — 3 ส.ค. 2542

115 kV วงจรเดี่ยว สายไฟฟ้าเดี่ยว
เสาสำหรับเข้าปลายสาย
แบบ SS–DE–2

115 kV SINGLE CIRCUIT, SINGLE CONDUCTOR
DEADEND STRUCTURE
TYPE SS–DE–2

ใช้แทนแบบ ....
ถูกแทนโดยแบบ ....
เขียนเสร็จวันที่ 22 ก.พ. 2542
แก้แบบวันที่ ....
มิติเป็น มิลลิเมตร
มาตราส่วน 1 : 75
แบบเลขที่ SA1–015/42005
แผ่นที่ 2 ของจำนวน 4 แผ่น

– 3 ส.ค. 2542

การประกอบเลขที่ 5232
ASSEMBLY NO.

บัญชีวัสดุ
BILL OF MATERIAL

ลำดับที่ ITEM	รายละเอียด DESCRIPTION	จำนวน REQ'D	วัสดุเลขที่ MAT. NO.
1	เสาคอนกรีต 22 ม. POLE, CONCRETE 22 m LONG	1	00010011
2	คอนสายแบบเหล็กฉาก ขนาด 150x100x12 มม. ยาว 4.50 ม. CROSSARM, STEEL ANGLE 150x100x12 mm, 4.50 m LONG	2	00120001
3	เหล็กฉากรับคอนสายขนาด 50x50x6 มม. ช่วงกว้าง 1,800 มม. ดรอพ 450 มม. BRACE, ANGLE STEEL 50x50x6 mm, 1,800 mm WIDE, 450 mm DROP	2	00120007
4	ท่อเหล็ก ขนาด 100x50x3.2 มม. ยาว 100 มม. ADAPTER, TUBE, RECTANGULAR STEEL, 100x50x3.2 mm, 100 mm LONG	–	01050200
5	แผ่นเหล็กยึนสองปลาย ขนาด 12x100x760 มม. PLATE, STEEL, DOUBLE ARMING 12x100x760 mm	2	01030102
6	สลักเกลียว M 16x75 มม. พร้อมแหวนกลม 2 อัน BOLT, MACHINE M 16x75 mm ; COMPLETE WITH 2 ROUND WASHER	4	01110400
7	สลักเกลียว M 16x170 มม. BOLT, MACHINE M 16x170 mm	4	01110201
8	สลักเกลียว M 16x350 มม. BOLT, MACHINE M 16x350 mm	4	01110205
9	สลักเกลียวตลอด M 16x400 มม. BOLT, DOUBLE ARMING, M 16x400 mm	4	01120000
10	สลักห่วงโอแวล M 16x200 มม. BOLT, OVAL EYE M 16x200 mm	1	01150001
11	สลักห่วงโอแวล M 20x350 มม. BOLT, OVAL EYE M 20x350 mm	1	01150100
12	สลักเกลียว M 20x350 มม. BOLT, MACHINE M 20x350 mm	1	01110300
13	แหวนสี่เหลี่ยมแบน 52x52x4.5 มม. รู ø18 มม. มอก. 258 WASHER, SQUARE FLAT 52x52x4.5 mm HOLE ø18 mm TIS 258	27	01180100
14	แหวนสี่เหลี่ยมแบน 62x62x6 มม. รู ø22 มม. มอก. 258 WASHER, SQUARE FLAT 62x62x6 mm HOLE ø22 mm TIS 258	2	01180101
15	แหวนสปริง M 16 มอก. 259 WASHER, LOCK M 16 TIS 259	4	01180301
16	แหวนสปริง M 20 มอก. 259 WASHER, LOCK M 20 TIS 259	2	01180301
17	เหล็กรูปรางน้ำรับสายล่อฟ้า 150x75x6.5 มม. ยาว 2.50 ม. OVER HEAD GROUND WIRE, STEEL CHANNEL 150x150x6.5 mm, 2.50 m LONG	1	–

กองวิศวกรรมไฟฟ้าและเครื่องกล
ฝ่ายวิศวกรรม

ผู้เขียน Sypholat Jonung
ผู้สำรวจ..................
วิศวกร..................
หัวหน้าแผนก.......... (มนต์)
ผู้อำนวยการกอง..................
ผู้อำนวยการฝ่าย..................

รองผู้ว่าการเทคนิคและบริการ
....

การไฟฟ้าส่วนภูมิภาค

ผู้ว่าการ..................

- 3 ส.ค. 2542

115 kV วงจรเดี่ยว สายไฟฟ้าเดี่ยว
เสาสำหรับเข้าปลายสาย
แบบ SS–DE–2

115 kV SINGLE CIRCUIT, SINGLE CONDUCTOR
DEADEND STRUCTURE
TYPE SS–DE–2

ใช้แทนแบบ ....
ถูกแทนโดยแบบ ....
เขียนเสร็จวันที่ 22 ก.พ. 2542
แก้แบบวันที่ ....
มิติเป็น..................
มาตราส่วน..................

แบบเลขที่ SA1–015/42005
แผ่นที่ 3 ของจำนวน 4 แผ่น

- 3 ส.ค. 2542

การประกอบเลขที่ ASSEMBLY NO. **5 2 3 2**

รายละเอียด DETAIL			
D-4C	การประกอบลูกถ้วยแขวน SUSPENSION INSULATOR ASSEMBLY	3	
D-6A	การประกอบสายยึดโยงลวดเหล็กตีเกลียว 50 ต.มม. STEEL STRANDED WIRE 50 mm^2 GUY ASSEMBLY	1	
D-7A	การประกอบสายยึดโยงลวดเหล็กตีเกลียว 95 ต.มม. STEEL STRANDED WIRE 95 mm^2 GUY ASSEMBLY	4	
D-9A*	สมอบกคอนกรีต CONCRETE ANCHOR	1	
D-10A*	ฐานรากเสา POLE FOUNDATION	1	

* สามารถเปลี่ยนได้ตามความเหมาะสม
CAN BE CHANGEDTO BE SUITABLE

อดิวิทย์ ทองลา พชง.3 ผปร. กฟส.ฉล. กฟจ.กบ. กฟต.2 สายงาน (ต) ผวก. @PEA

กองวิศวกรรมไฟฟ้าและเครื่องกล
ฝ่ายวิศวกรรม

การไฟฟ้าส่วนภูมิภาค

ผู้เขียน
ผู้สำรวจ
วิศวกร
หัวหน้าแผนก
ผู้อำนวยการกอง
ผู้อำนวยการฝ่าย

รองผู้ว่าการเทคนิคและบริการ

ผู้ว่าการ - 3 ส.ค. 2542

115 kV วงจรเดี่ยว สายไฟฟ้าเดี่ยว
เสาสำหรับเข้าปลายสาย
แบบ SS-DE-2

115 kV SINGLE CIRCUIT, SINGLE CONDUCTOR
DEADEND STRUCTURE
TYPE SS-DE-2

ใช้แทนแบบ
ถูกแทนโดยแบบ
เขียนเสร็จวันที่ 22 ก.พ. 2542
แก้แบบวันที่
มิติเป็น
มาตราส่วน

แบบเลขที่ SA1-015/42005
แผ่นที่ 4 ของจำนวน 4 แผ่น

- 3 ส.ค. 2542