การประกอบเลขที่ ASSEMBLY NO. 0810

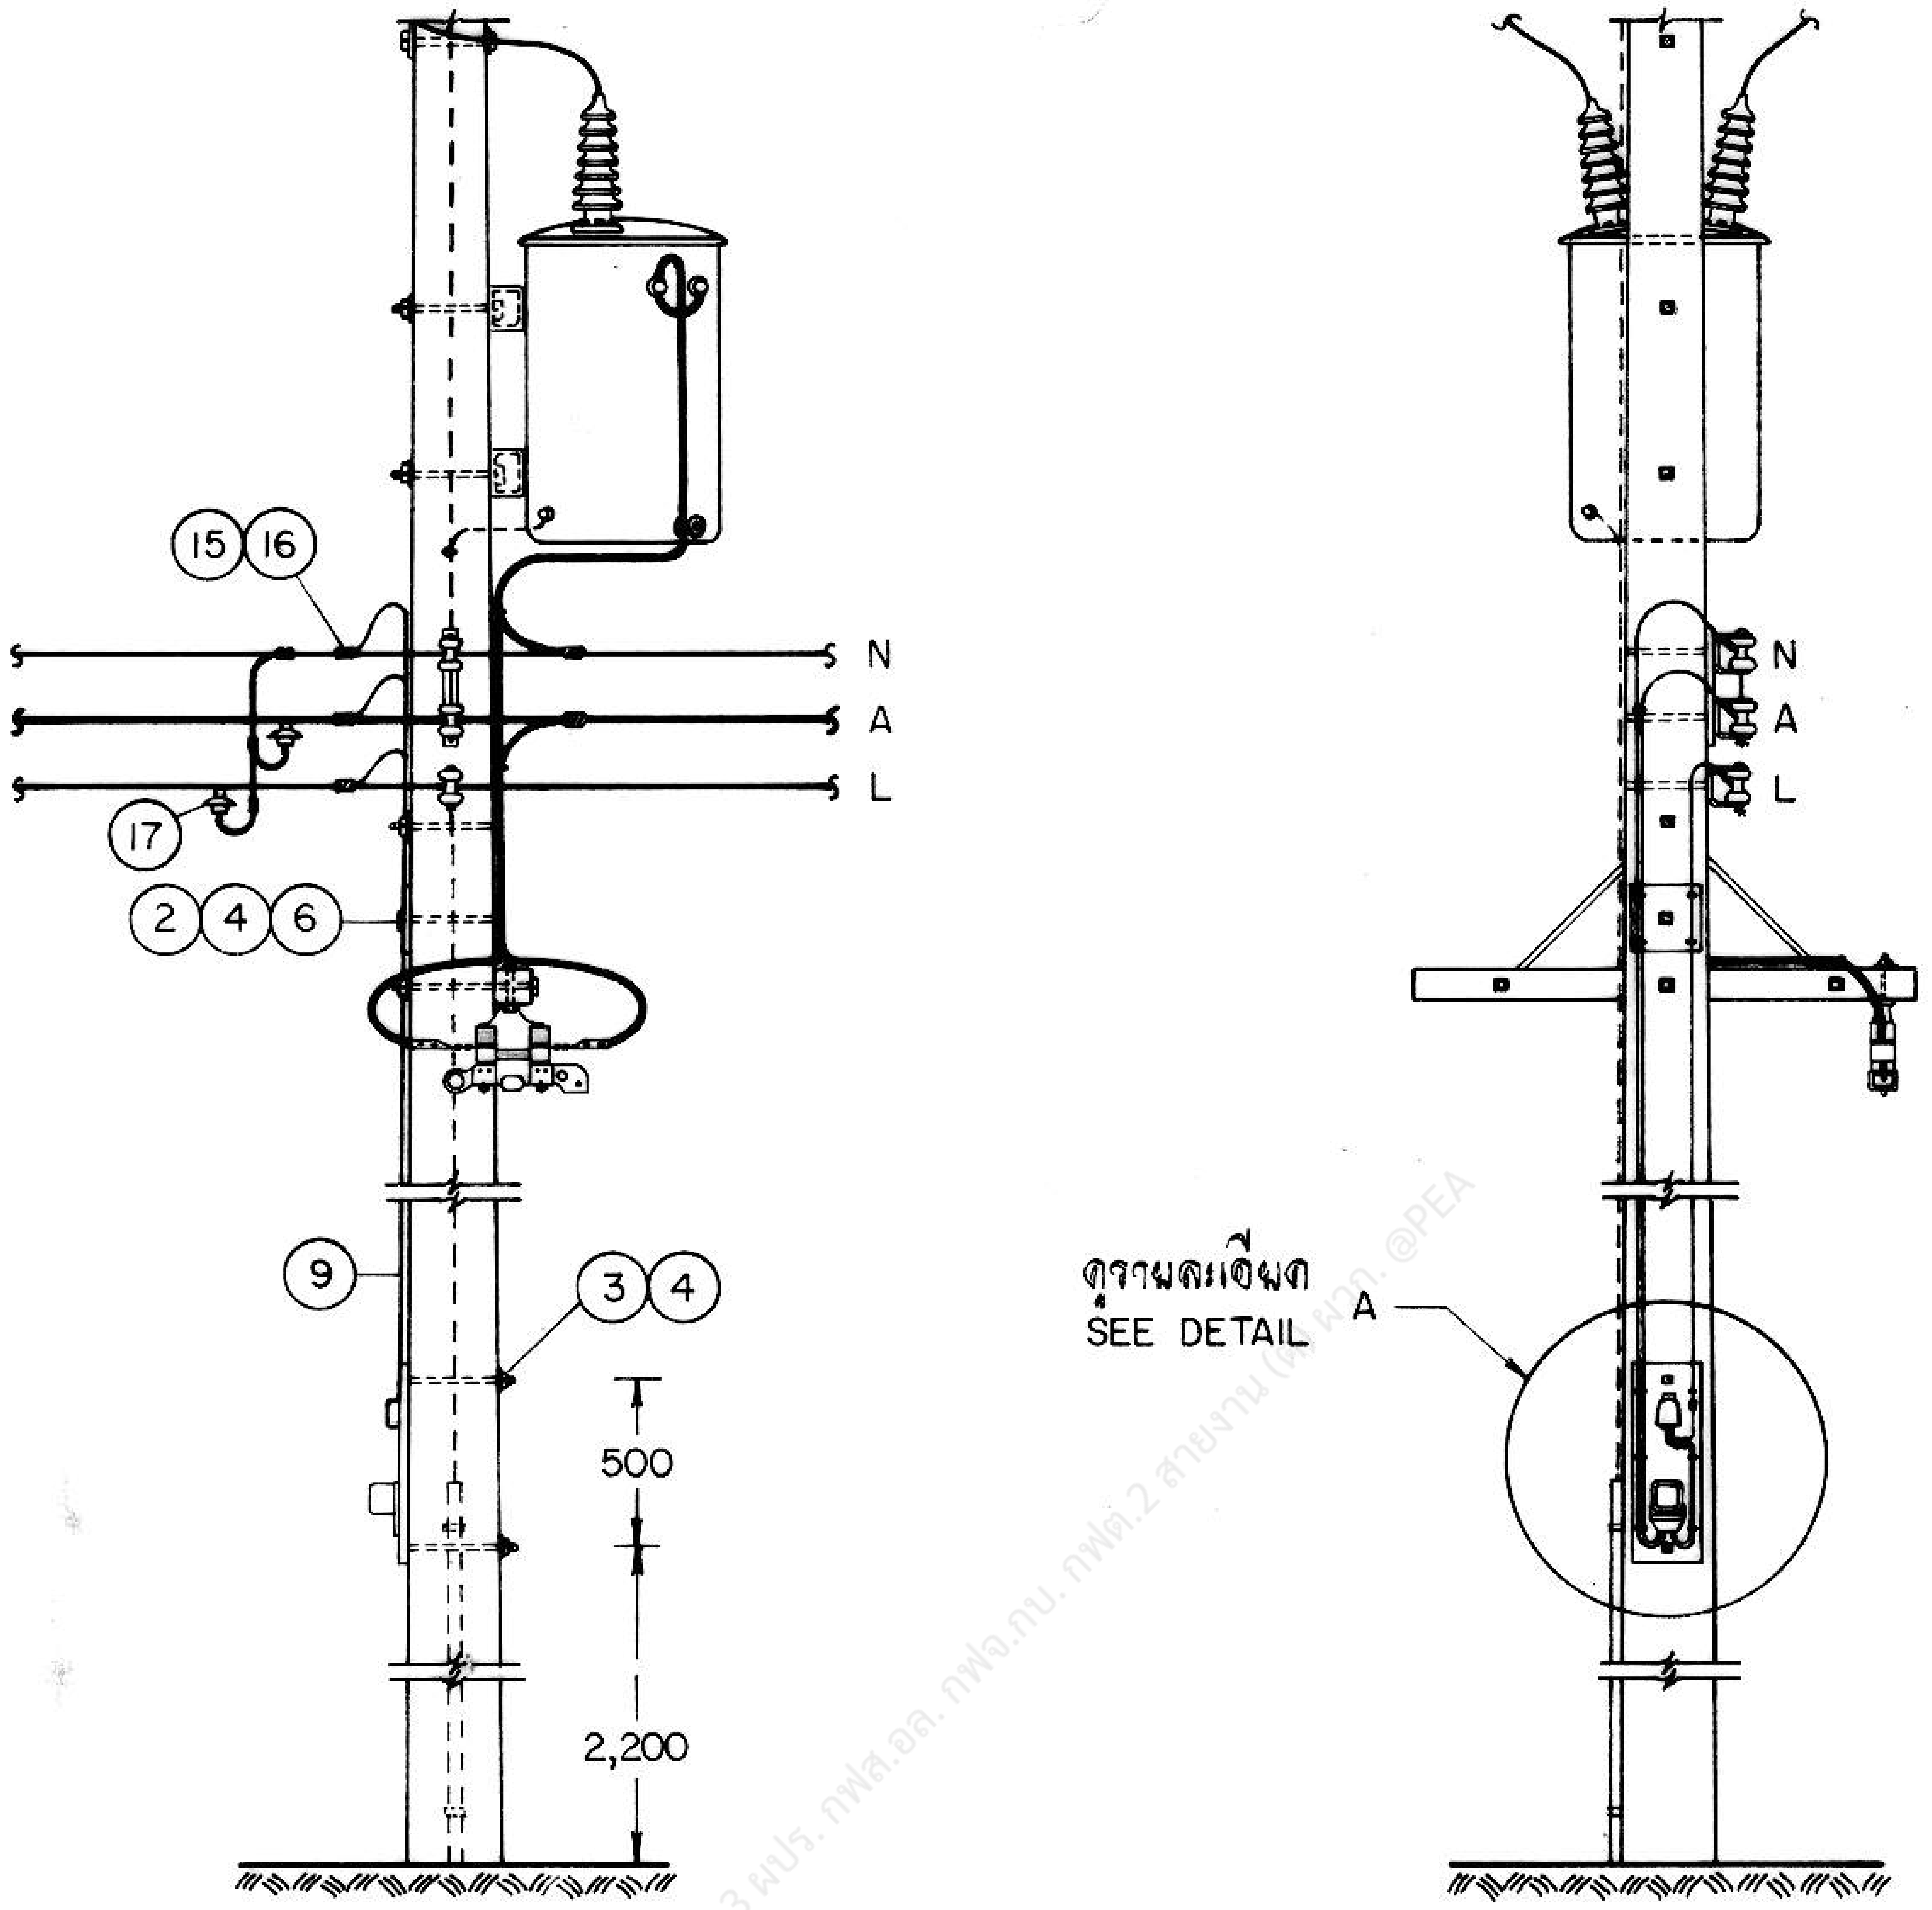

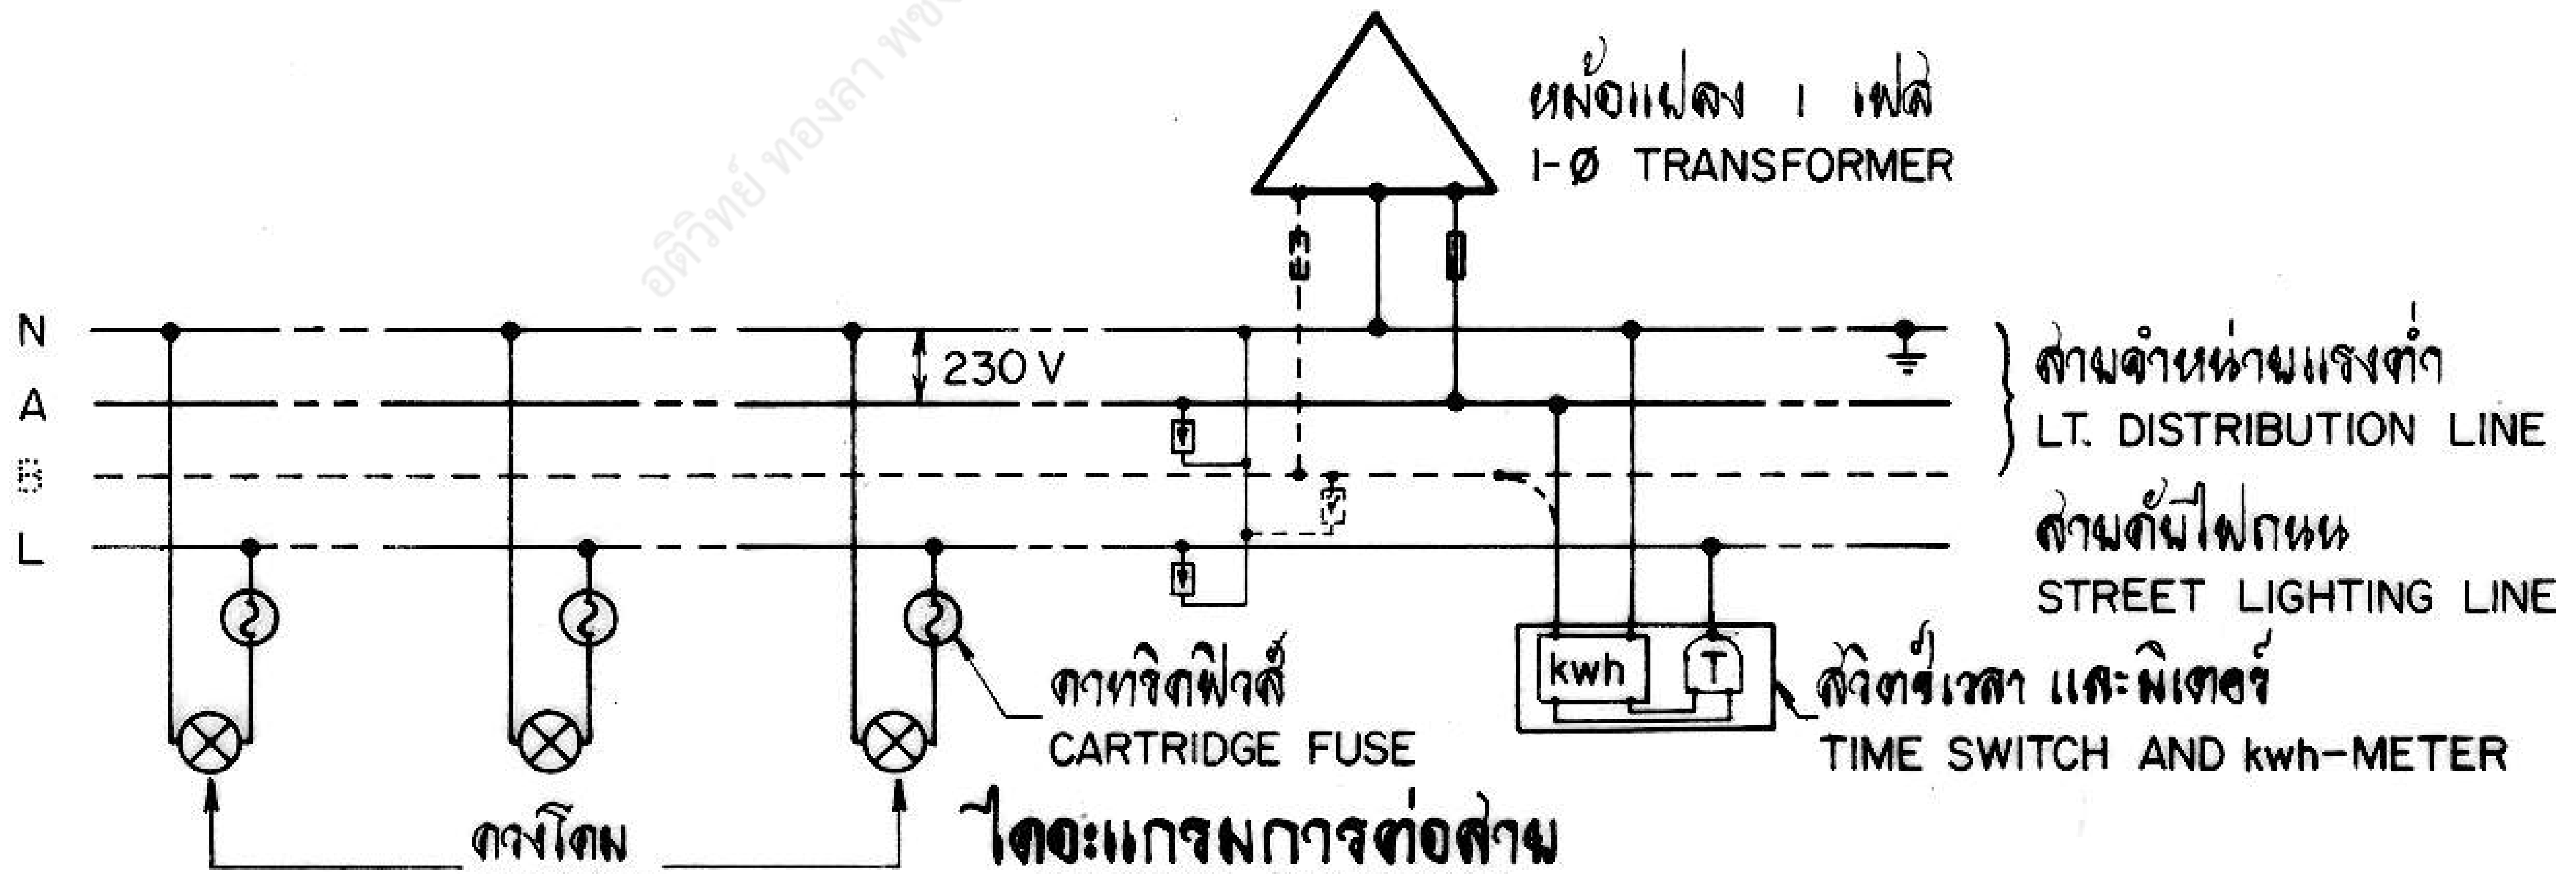

ไดอะแกรมการต่อสาย
WIRING DIAGRAM

กองวิศวกรรมไฟฟ้าและเครื่องกล
ฝ่ายวิศวกรรม

ผู้เขียน
ผู้สำรวจ
วิศวกร
หัวหน้าแผนก
ผู้อำนวยการกอง
ผู้อำนวยการฝ่าย

รองผู้ว่าการฝ่ายเทคนิค

การไฟฟ้าส่วนภูมิภาค

ผู้ว่าการ . 11 ธ.ค. 26

การติดตั้งสวิตช์เวลา
ก ที่เสาต้นติดตั้งหม้อแปลงแบบแขวน

TIME SWITCH INSTALLATION
A ON SINGLE-PHASE TRANSFORMER POLE

ใช้แทนแบบ
ถูกแทนโดยแบบ
เขียนเสร็จวันที่ 3 มี.ค. 26
แก้แบบวันที่
มิติเป็น มม.
มาตราส่วน 1 : 40

แบบเลขที่ SAI-015/26009
แผ่นที่ 1 ของจำนวน 6 แผ่น

- 5 ส.ค. 2526

อดิวิทย์ ทองลา พชง.3 ผปร. กฟส.อล. กฟจ.กบ. กฟต.2 สายงาน (ต) ผวก. @PEA

การประกอบเลขที่
ASSEMBLY NO. 0810

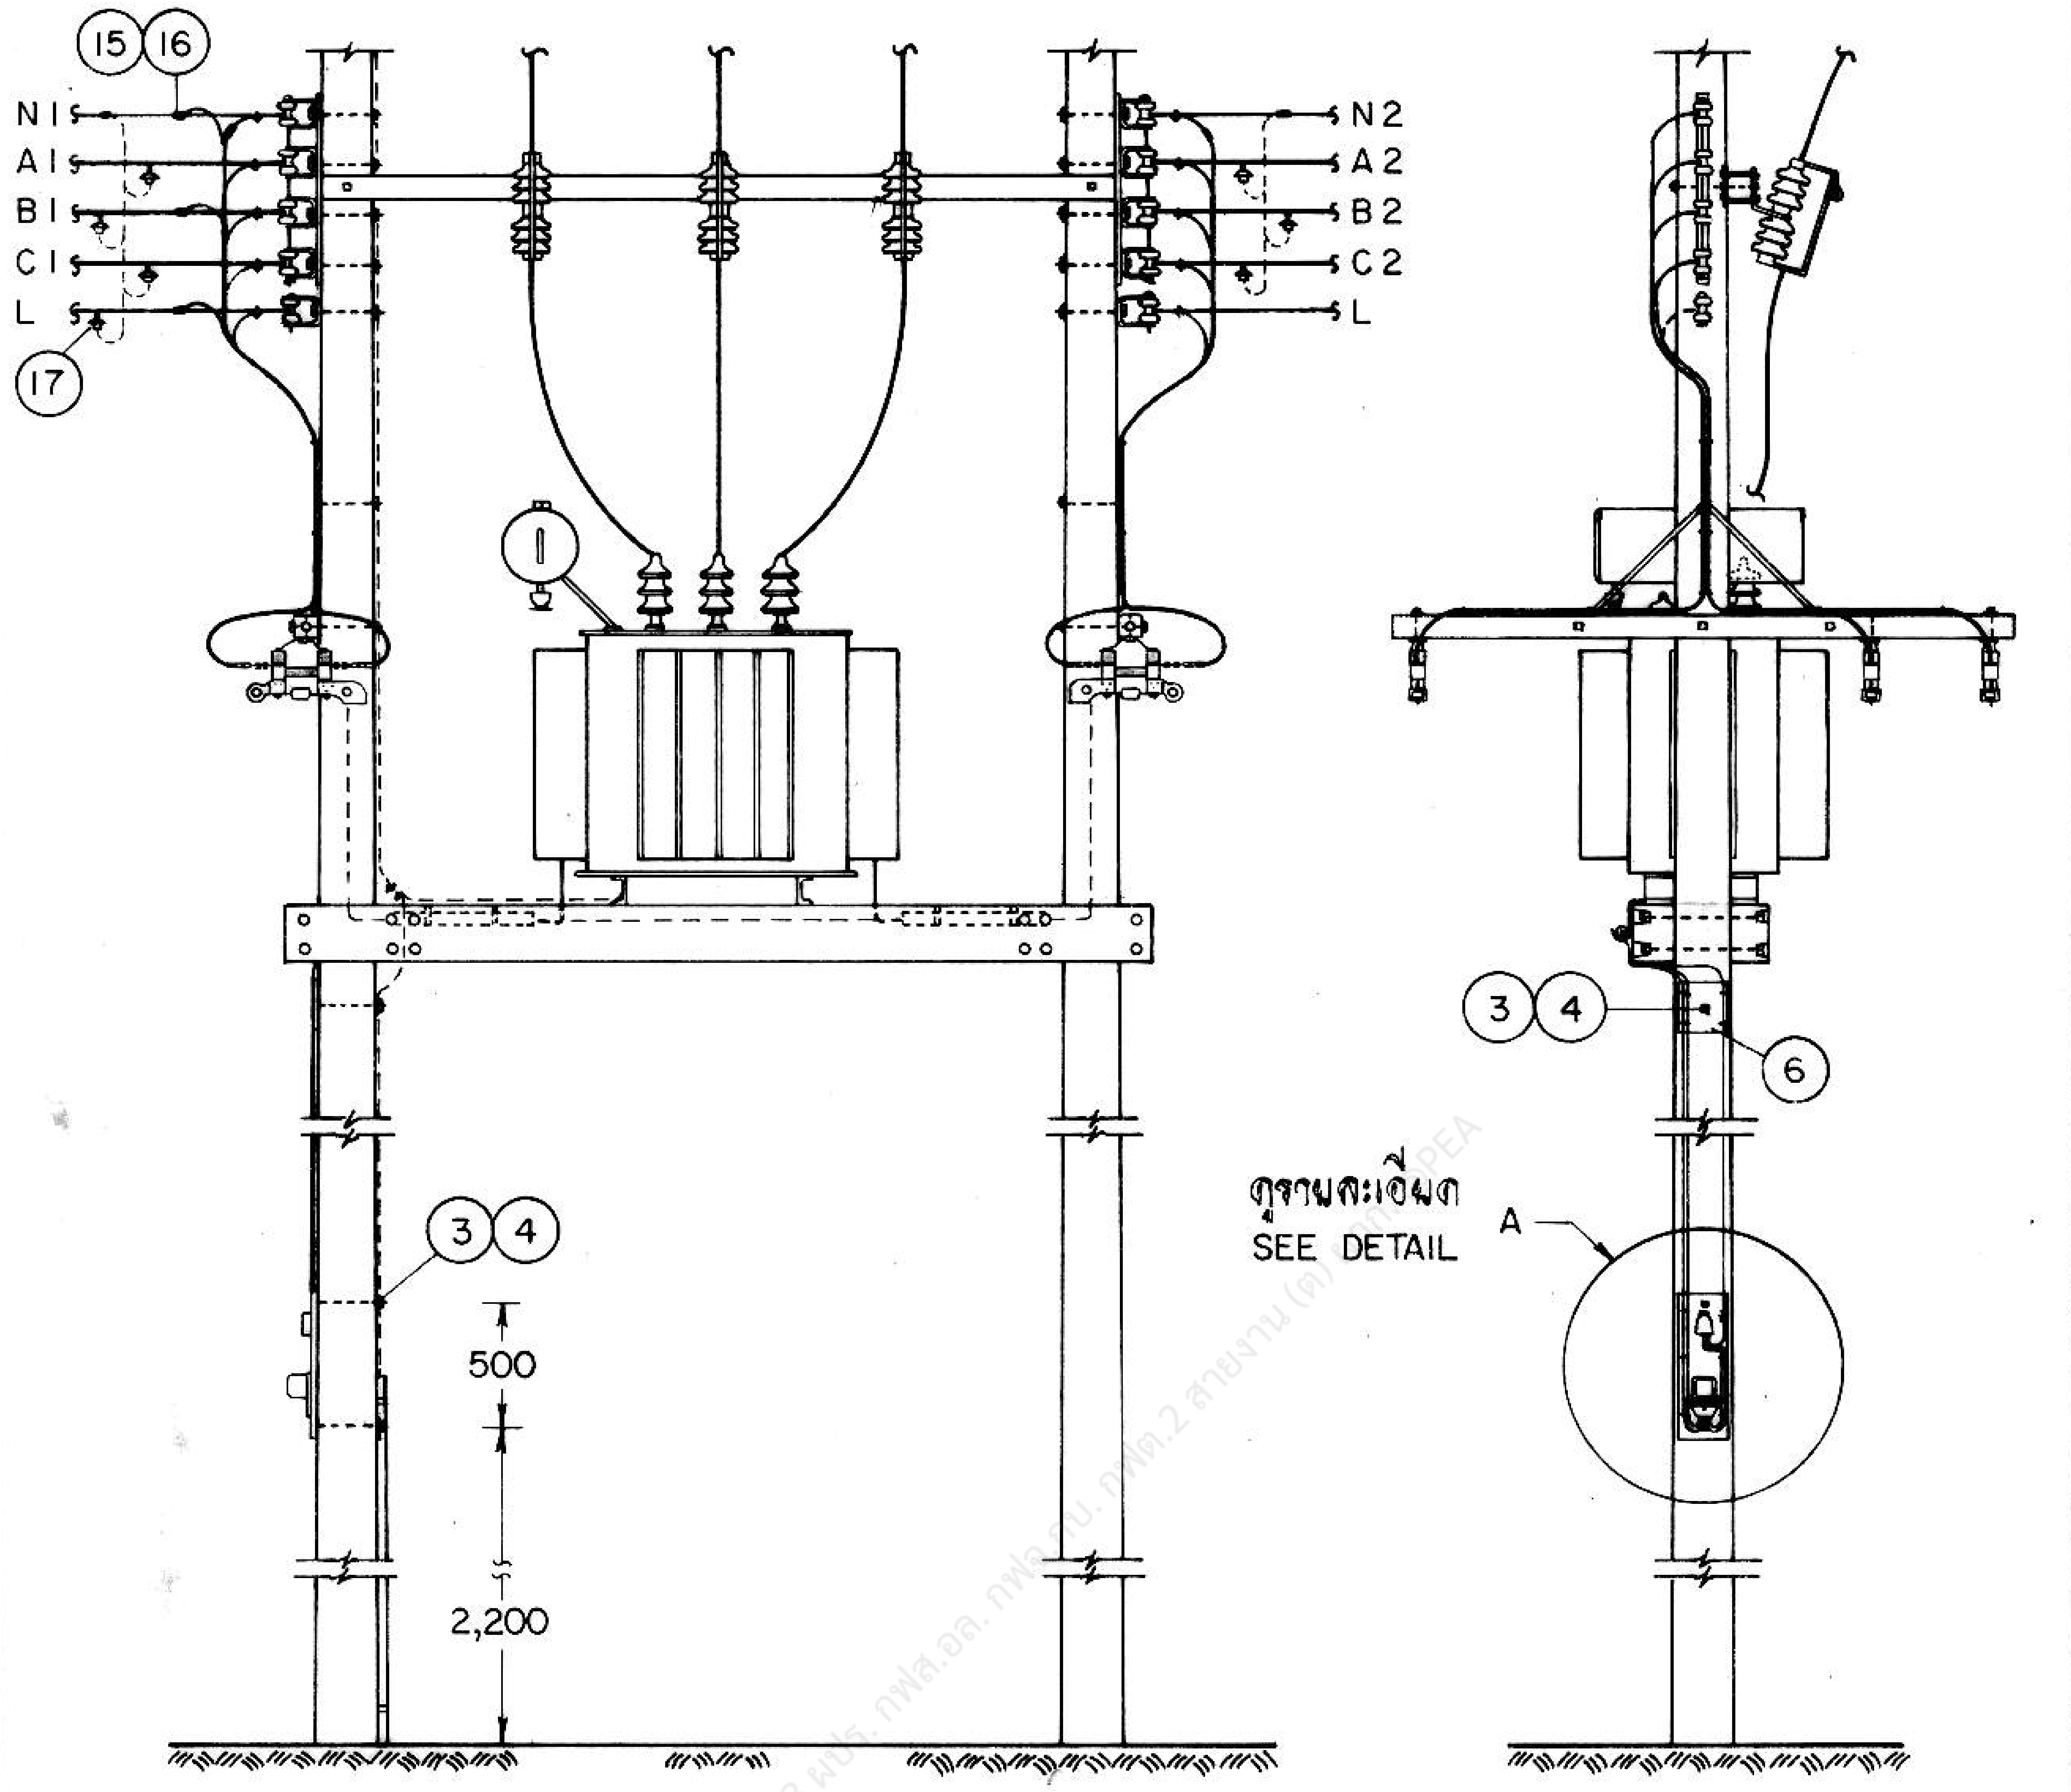

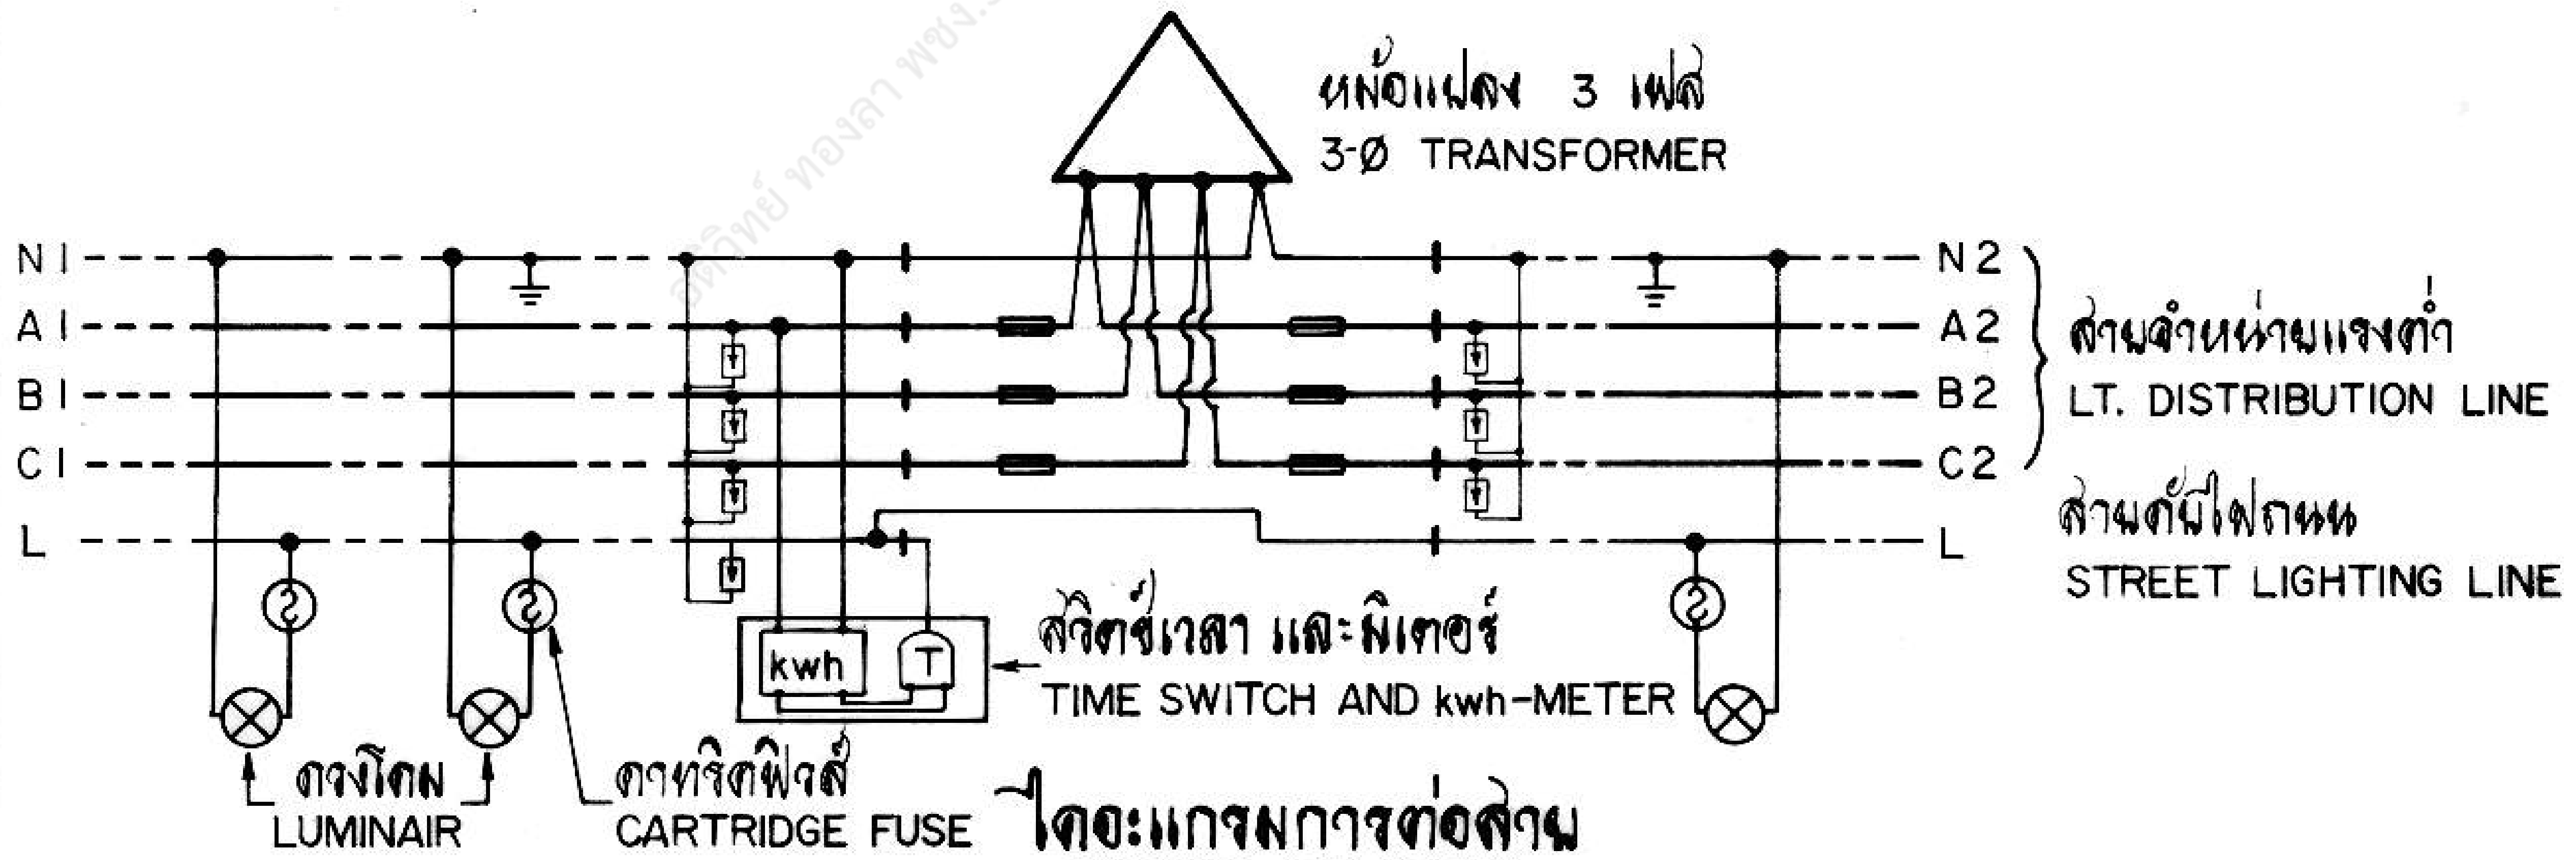

ไดอะแกรมการต่อสาย
WIRING DIAGRAM

กองวิศวกรรมไฟฟ้าและเครื่องกล ฝ่ายวิศวกรรม	การไฟฟ้าส่วนภูมิภาค	ใช้แทนแผน
ผู้เขียน ผู้สำรวจ วิศวกร หัวหน้าแผนก ผู้อำนวยการกอง ผู้อำนวยการฝ่าย	ผู้ว่าการ : 11 ม.ค. ๒๖	ถูกแทนโดยแผน เขียนเสร็จวันที่ 3 มี.ค. 26 แก้แผนวันที่ ลิขิตเป็น ผผ. มาตราส่วน 1 : 50
	การติดตั้งสวิตช์เวลา ข ที่เสาต้นนั่งร้านหม้อแปลง	
รองผู้ว่าการฝ่ายเทคนิค	TIME SWITCH INSTALLATION B ON THREE-PHASE TRANSFORMER POLE (PLATFORM MOUNTING)	แผนเลขที่ SAI-015/26009 แผ่นที่ 2 ของจำนวน 6 แผ่น

การประกอบเลขที่
ASSEMBLY NO. 0810

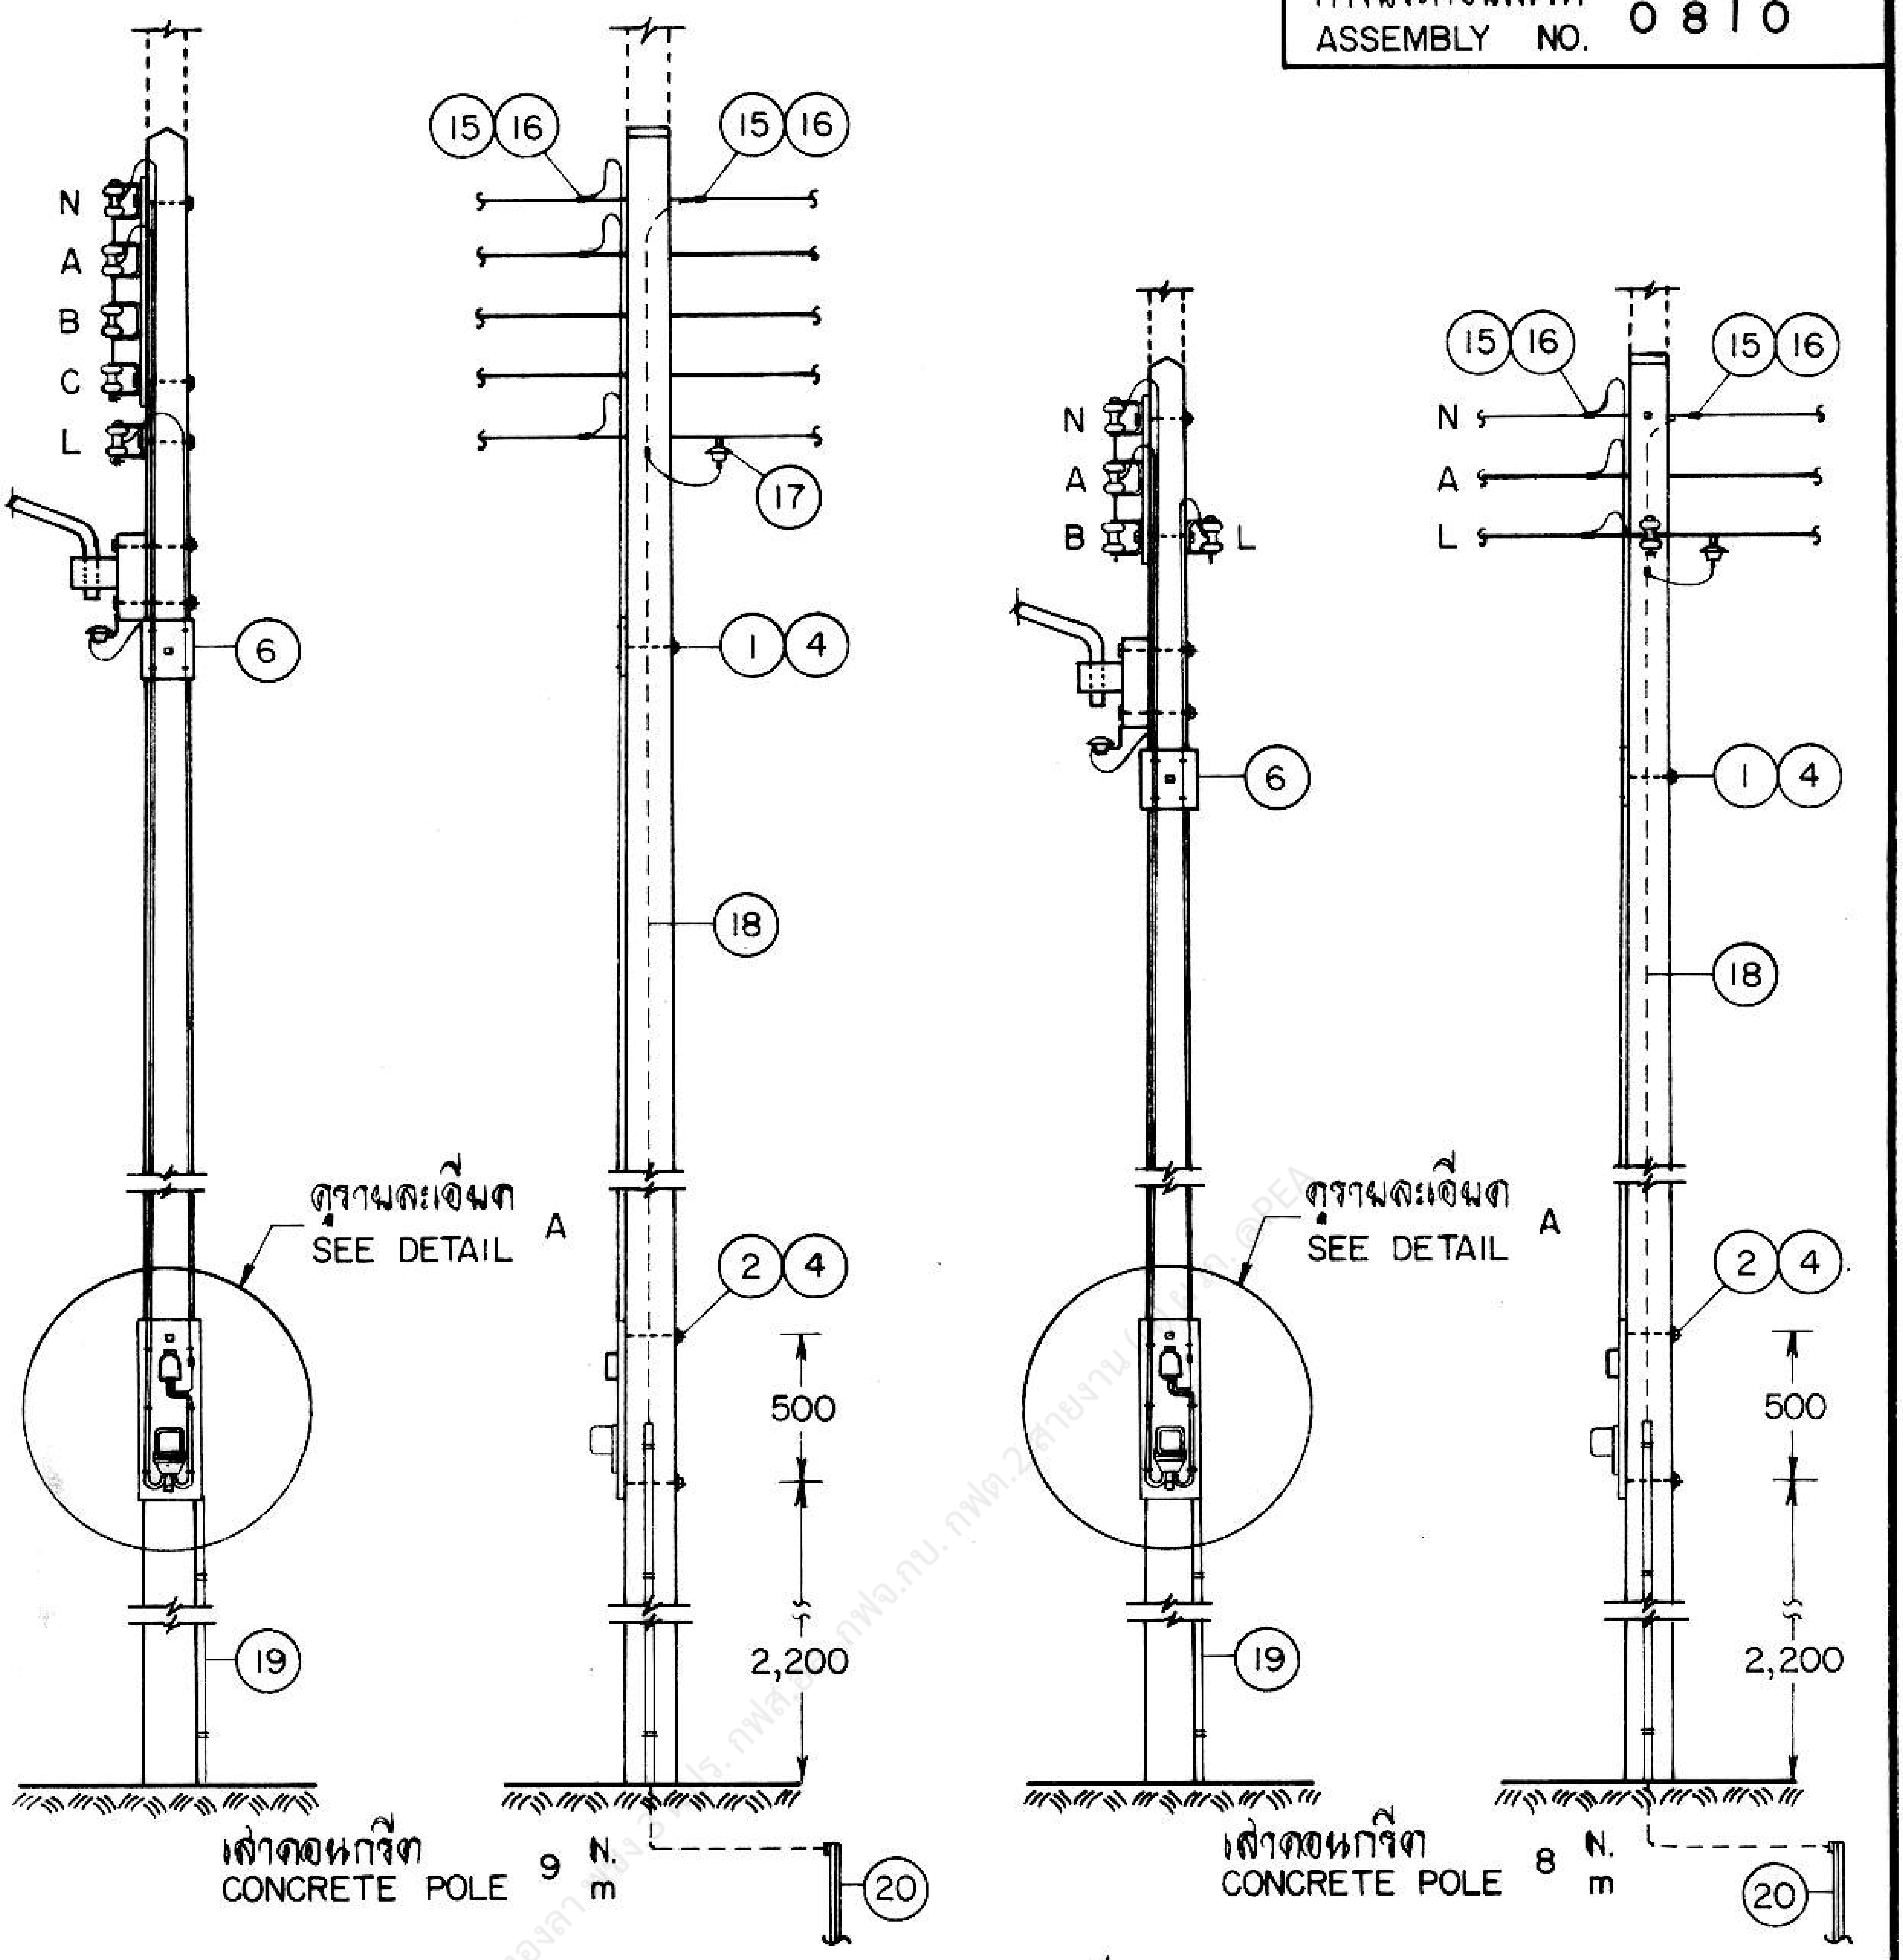

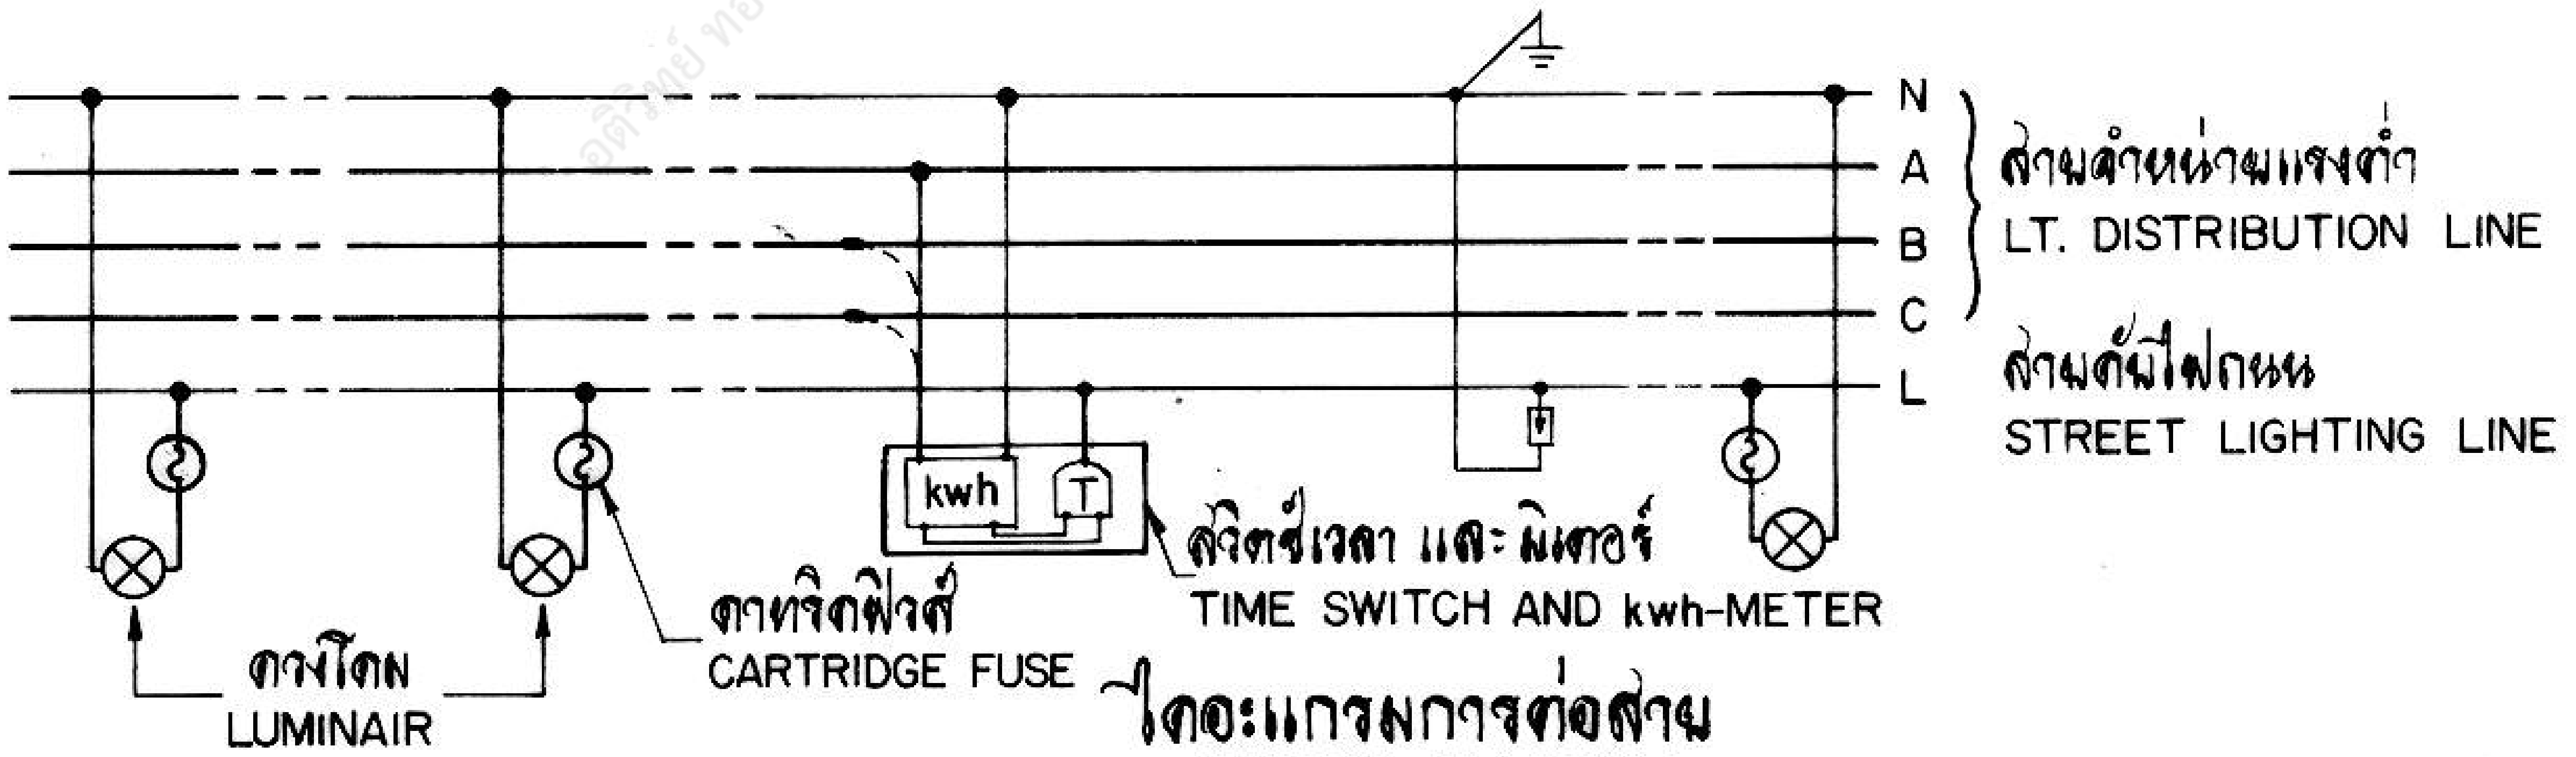

ไดอะแกรมการต่อสาย
WIRING DIAGRAM

กองวิศวกรรมไฟฟ้าและเครื่องกล ฝ่ายวิศวกรรม	การไฟฟ้าส่วนภูมิภาค	ใช้แทนแบบ ถูกแทนโดยแบบ เขียนเสร็จวันที่ 3 มี.ค. 26 แก้แบบวันที่ ลิขิตเป็น ผผ. มาตราส่วน 1 : 40
ผู้เขียน ผู้สำรวจ วิศวกร หัวหน้าแผนก ผู้อำนวยการกอง ผู้อำนวยการฝ่าย	ผู้ว่าการ . 11 ธ.ค. 26 การติดตั้งสวิตช์เวลา ค ที่เสาต้นใดในไลน์ระบบจำหน่ายแรงต่ำ	
รองผู้ว่าการฝ่ายเทคนิค	TIME SWITCH INSTALLATION C ON THE POLE IN LT. DISTRIBUTION LINE	แบบเลขที่ SAI-015/26009 แผ่นที่ 3 ของจำนวน 6 แผ่น

การประกอบเลขที่
ASSEMBLY NO. 0810

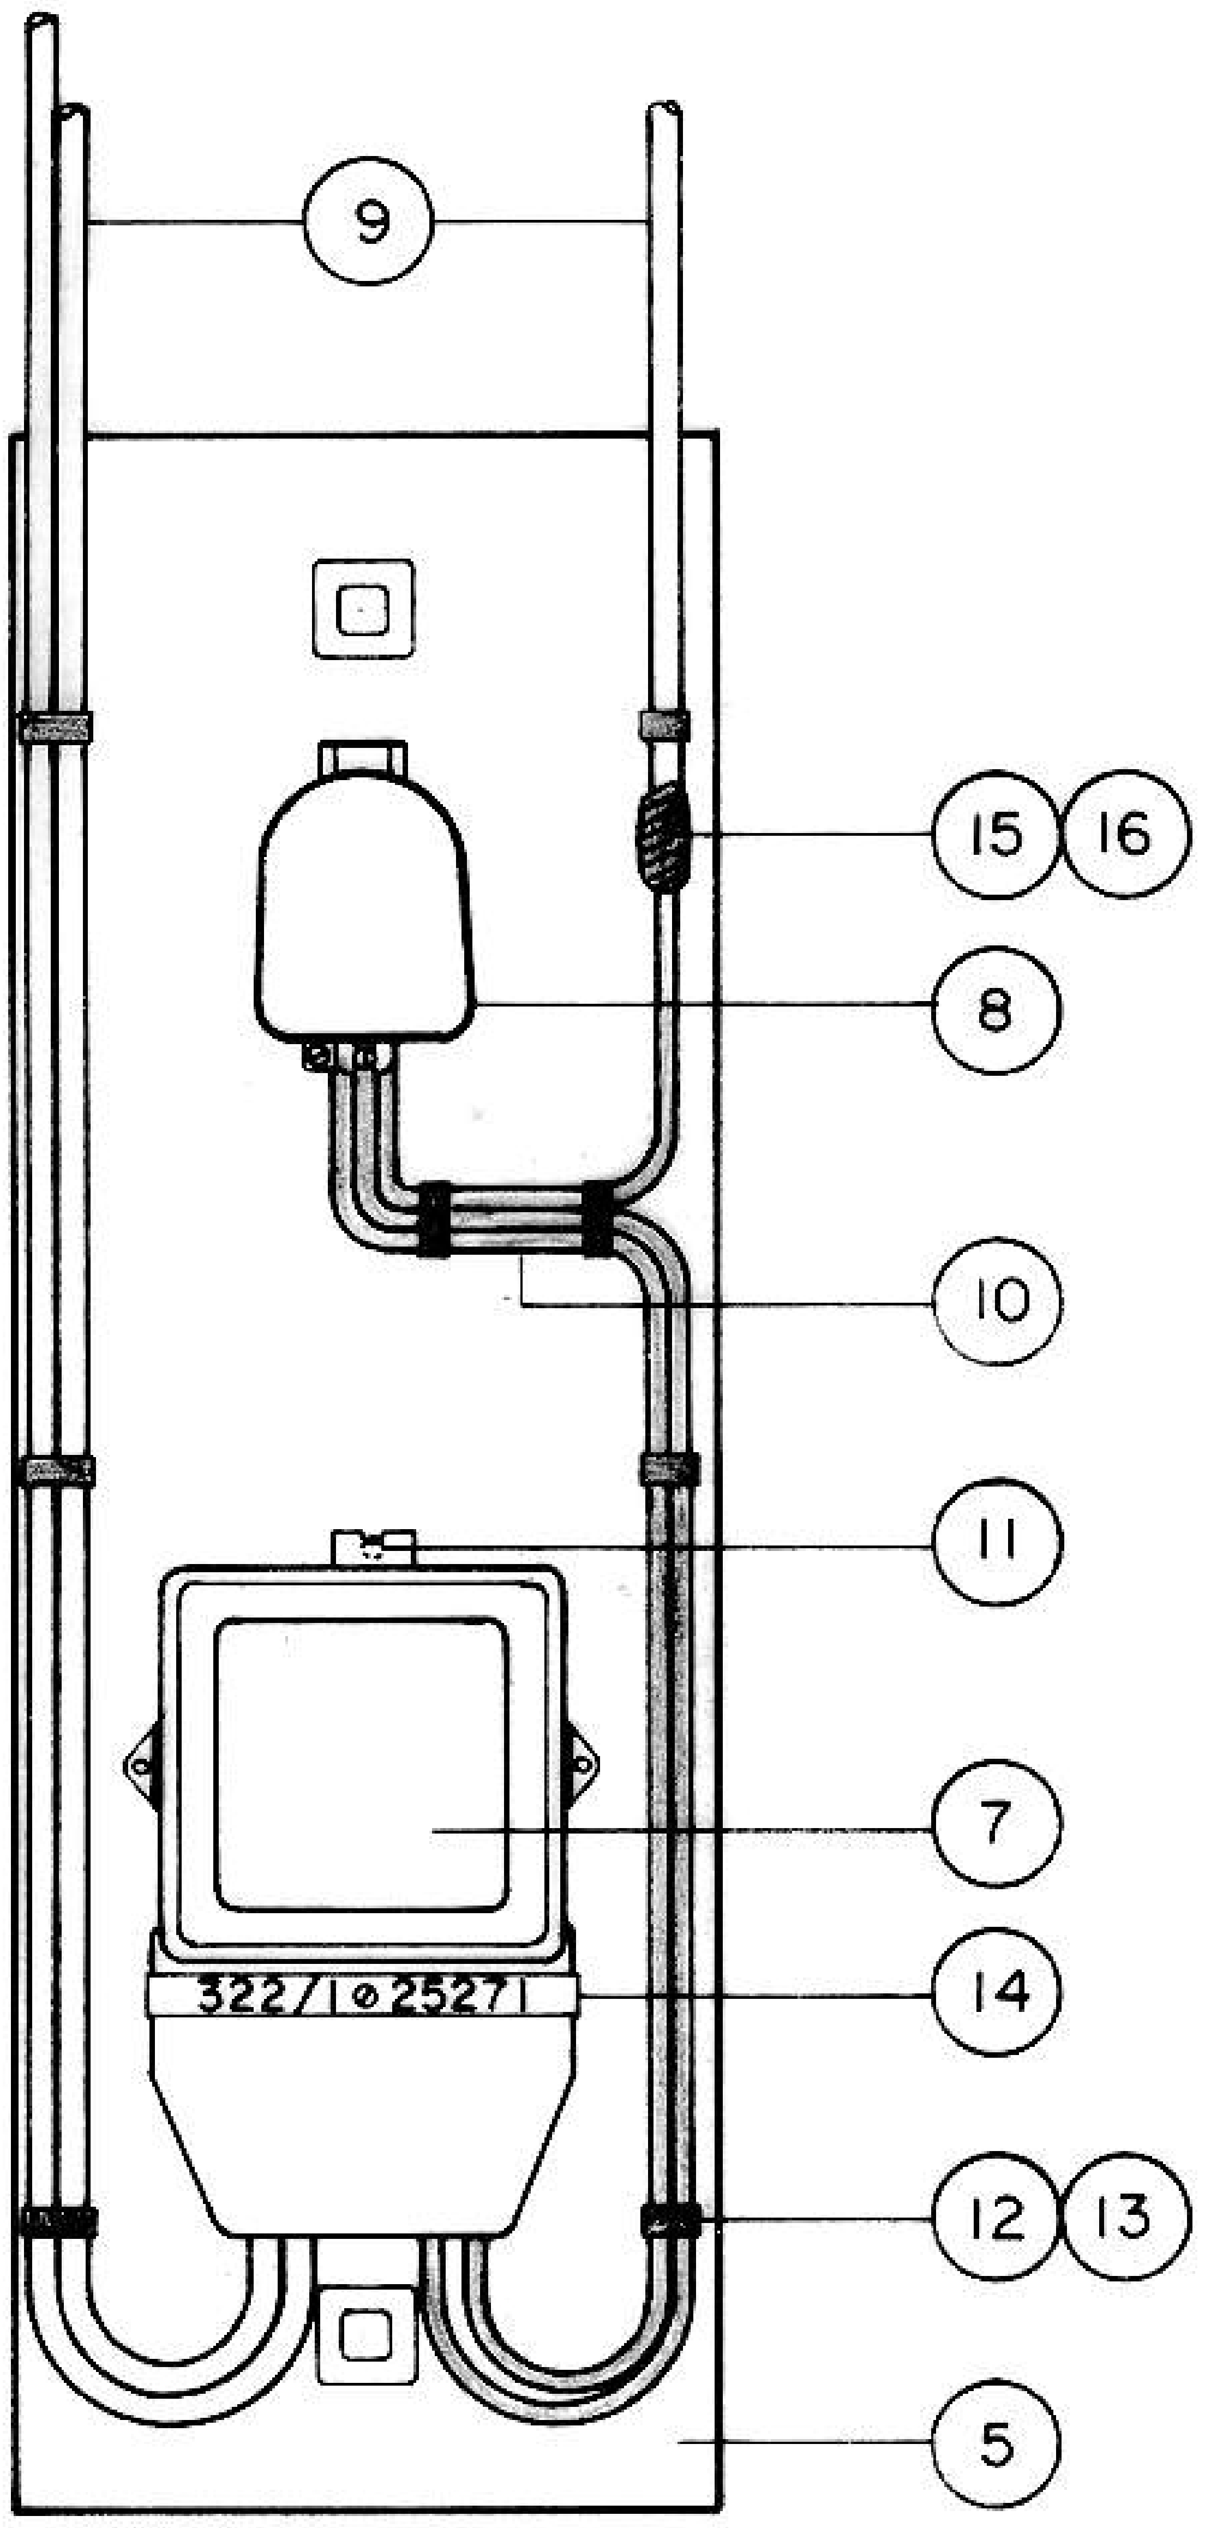

รายละเอียด A
DETAIL A

การติดตั้งนี้ สำหรับสวิตช์เวลาแบบติดตั้งภายนอก เช่น ผลิตภัณฑ์ HORSTMANN (30A) และผลิตภัณฑ์ TORK (40A) ขนาดสายไฟเข้าออกสวิตช์เวลา ให้ดูตาม ตาราง ①

THIS INSTALLATION IS FOR OUTDOOR TYPE TIME SWITCH, SUCH AS HORSTMANN (30 A) AND TORK (40 A). THE SIZE OF CABLE ENTRANCE TO TIME SWITCH SEE TABLE ①

ตาราง ①
TABLE

ขนาดของสวิตช์เวลา SIZE OF TIME SWITCH	ขนาดของสายไฟ SIZE OF CONDUCTOR	หมายเหตุ REMARK
30 A	10 – 16 ตร.มม. mm^2	1. ใช้สายทองแดงหุ้มฉนวน พีวีซี. 750 โวลต์ 75°C และควรเป็นสายตัวนำเส้นเดียว 2. ที่ขั้วต่อสายของสวิตช์เวลา ผลิตภัณฑ์ TORK ให้เข้าปลายสายด้วยหางปลาสำหรับสายทองแดง (ต้องจัดหาเพิ่มใหม่)
40 A	16 – 25 ตร.มม. mm^2	1. USE COPPER CONDUCTOR PVC INSULATED 750 VOLT, 75° C, AND SHOULD BE SOLID CONDUCTOR. 2. FOR TORK'S TIME SWITCH, AT TERMINAL, USE COPPER CABLE LUG IN CONNECTION.

กองวิศวกรรมไฟฟ้าและเครื่องกล
ฝ่ายวิศวกรรม

ผู้เขียน
ผู้สำรวจ
วิศวกร
หัวหน้าแผนก
ผู้อำนวยการกอง
ผู้อำนวยการฝ่าย

รองผู้ว่าการฝ่ายเทคนิค

การไฟฟ้าส่วนภูมิภาค

ผู้ว่าการ 11 ส.ค. 26

การติดตั้งสวิตช์เวลา

TIME SWITCH INSTALLATION

ใช้แทนแบบ
ถูกแทนโดยแบบ
เขียนเสร็จวันที่ 3 มี.ค. 26
แก้แบบวันที่
มิติเป็น มม.
มาตราส่วน 1 : 15

แบบเลขที่ SAI-015/26009
แผ่นที่ 4 ของจำนวน 6 แผ่น

5 ส.ค. 2526

อดิวิทย์ ทองลา พชง. [illegible] ผจ.กบ. กฟต.2 สายงาน (ต) ผวก. @PEA

การประกอบเลขที่
ASSEMBLY NO. 0810

บัญชีวัสดุ
BILL OF MATERIAL

ลำดับที่ ITEM	รายละเอียด DESCRIPTION	จำนวน REQ'D ก/A	 ข/B	 ค/C	วัสดุเลขที่ MAT. NO.
1	สลักเกลียว M 16 X 200 มม. BOLT, MACHINE, M 16 X 200 mm	–	–	1	01110202
2	สลักเกลียว M 16 X 250 มม. BOLT, MACHINE, M 16 X 250 mm	1	–	2	01110203
3	สลักเกลียว M 16 X 300 มม. BOLT, MACHINE, M 16 X 300 mm	2	2	–	01110204
4	แหวนสี่เหลี่ยมแบน ขนาด 52 X 52 X 4.5 มม. รู Ø 18 มม. มอก. 258 WASHER, SQUARE, FLAT 52 X 52 X 4.5 mm HOLE Ø 18 mm, TIS 258	6	4	6	01180100
5	แป้นไม้รองมิเตอร์ไสแล้ว ขนาด 60 X 20 X 2 ซม. METER, PLATE (HARD WOOD) SURFACE FINISHED SIZE 60 X 20 X 2 cm	1	1	1	
6	แป้นไม้สำหรับยึดสายเข้าและออกจากมิเตอร์ไสแล้ว ขนาด 20 X 20 X 2 ซม. CABLE, PLATE (HARD WOOD) SURFACE FINISHED SIZE 20 X 20 X 2 cm	1	1	1	–
7	วัตต์อาวร์มิเตอร์ 1 เฟส 2 สาย 220 โวลต์ 20(40) แอมป์ ใช้ภายนอก METER, WATTHOUR, SINGLE-PHASE, 2-WIRE, 220 VOLT, 20(40) A WEATHER PROOF	1	1	1	06000003
8	สวิตช์เวลาวงจรเดี่ยว สำหรับระบบ 220 โวลต์ ขนาด 30–40 แอมป์ (แบบใช้ภายนอก) TIME SWITCH, SINGLE CIRCUIT, FOR 220 V, 30–40 A (OUTDOOR TYPE)	1	1	1	07030802-3
9	สายอะลูมิเนียมหุ้มฉนวน PVC 750 โวลต์ 75°ซ. 25 ต.มม. มอก. 293 CABLE, AL PVC INSULATED, 750 V, 75°C, 25 mm^2 TIS 293	18 ม. m	18 ม. m	18 ม. m	02070000
10	สายทองแดงหุ้มฉนวน PVC 750 โวลต์ 75°ซ. มอก. 11 ขนาดตามต้องการ CABLE, COPPERS CONDUCTOR, PVC INSULATED, 750 V, 75°C, TIS 11 SIZE AS REQ'D.	1.5 ม. m	1.5 ม. m	1.5 ม. m	–
11	ตะปูเกลียวชุบโครเมียม ขนาด 15–20 มม. SCREW, CHROME PLATED, SIZE 15–20 mm	6	6	6	
12	ตะปูหัวกลมแบน ยาว 15–20 มม. Ø 1.00 มม. มอก. 113 NAIL, ROUND, MILD STEEL WIRE 15–20 mm LONG Ø 1.00 mm TIS 113	12	12	12	
13	เข็มขัดรัดสาย (ทำด้วยลวดอะลูมิเนียมแบน 1 X 10 มม.) CABLE STRAP (MADE OF ARMOUR TAPE 1 X 10 mm)				
14	หมายเลขผู้ใช้ไฟ (ทำด้วยแผ่นอะลูมิเนียม 15 X 100 มม. หนา 0.5 มม.) NUMBER OF CUSTOMER (MADE OF ALUMINIUM PLATE 15 X 100 mm, 0.5 mm THICKNESS)	1	1	1	
15	คอนเนคเตอร์ชนิดบีบแบบ H สำหรับสายอะลูมิเนียม ขนาดตามต้องการ CONNECTOR, COMPRESSION, H–TYPE, FOR AL CONDUCTOR SIZE AS REQUIRED	4	4	5	02320003-2
16	PVC เทป กว้าง 19 มม. (ใช้ความยาว 2 ม. ต่อ 1 จุด) มอก. 386 PVC TAPE, 19 mm WIDE (2 m LONG PER POINT) TIS 386				02180001 or 02180002
17	ล่อฟ้า 250–500 โวลต์ 2.5–5 กิโลแอมป์ LIGHTNING ARRESTER 250–500 VOLT, 2.5–5 kA	1	1	1	04000300
18	ลวดเหล็กตีเกลียว 50/7 ต.มม. มอก. 404 WIRE, STEEL STRANDED 50/7 mm^2, TIS 404	–	–	20 ม. m	01100004
19	ท่อ PVC แข็ง ขนาด 20 X 2,500 มม. พร้อมอุปกรณ์ยึด CONDUIT, PVC RIGID 20 X 2,500 mm COMPLETE WITH FIXING ACCESSORY	–	–	1	08040001
20	หลักดิน 60 X 60 X 5 มม. ยาว 2 ม. ROD, GROUND 60 X 60 X 5 mm 2 m LONG	–	–	1	01220002

กองวิศวกรรมไฟฟ้าและเครื่องกล
ฝ่ายวิศวกรรม

ผู้เขียน
ผู้สำรวจ
วิศวกร
หัวหน้าแผนก
ผู้อำนวยการกอง
ผู้อำนวยการฝ่าย

รองผู้จัดการฝ่ายเทคนิค

การไฟฟ้าส่วนภูมิภาค

ผู้จัดการ 11 ส.ค. 26

การติดตั้งสวิตช์เวลา

TIME SWITCH INSTALLATION

ใช้แทนแบบ
ถูกแทนโดยแบบ
เขียนเสร็จวันที่ 3 มี.ค. 26
แก้แบบวันที่
มิติเป็น
มาตราส่วน

แบบเลขที่ SAI–015/26009
แผ่นที่ 5 ของจำนวน 6 แผ่น

5 ส.ค. 2526

การประกอบเลขที่ 0810
ASSEMBLY NO. 0810

หมายเหตุ

1. ในกรณีติดตั้งหม้อแปลงเฉพาะเพื่อจ่ายไฟให้กับวงจรไฟถนน ให้ติดตั้งฟิวส์สวิตช์แรงต่ำป้องกันวงจรไฟถนนที่เสาต้นหม้อแปลง
2. จำนวนดวงโคม ขนาดสวิตช์เวลา และขนาด ดี-คาทริดฟิวส์ ให้ดูรายละเอียดตามแผนเลขที่ SAI-015/23039 (การประกอบเลขที่ 0807)

NOTES

1. IN CASE OF TRANSFORMER INSTALLATION FOR STREET LIGHTING CIRCUIT ONLY, L.T. FUSE SWITCH SHALL BE INSTALLED AT TRANSFORMER POLE FOR PROTECTION STREET LIGHTING CIRCUIT.
2. NUMBER OF LUMINAIRS, SIZE OF TIME SWITCH AND SIZE OF D-CARTRIDGE FUSE SEE DETAIL IN DRAWING NO. SAI-015/23039 (ASSEMBLY NO. 0807)

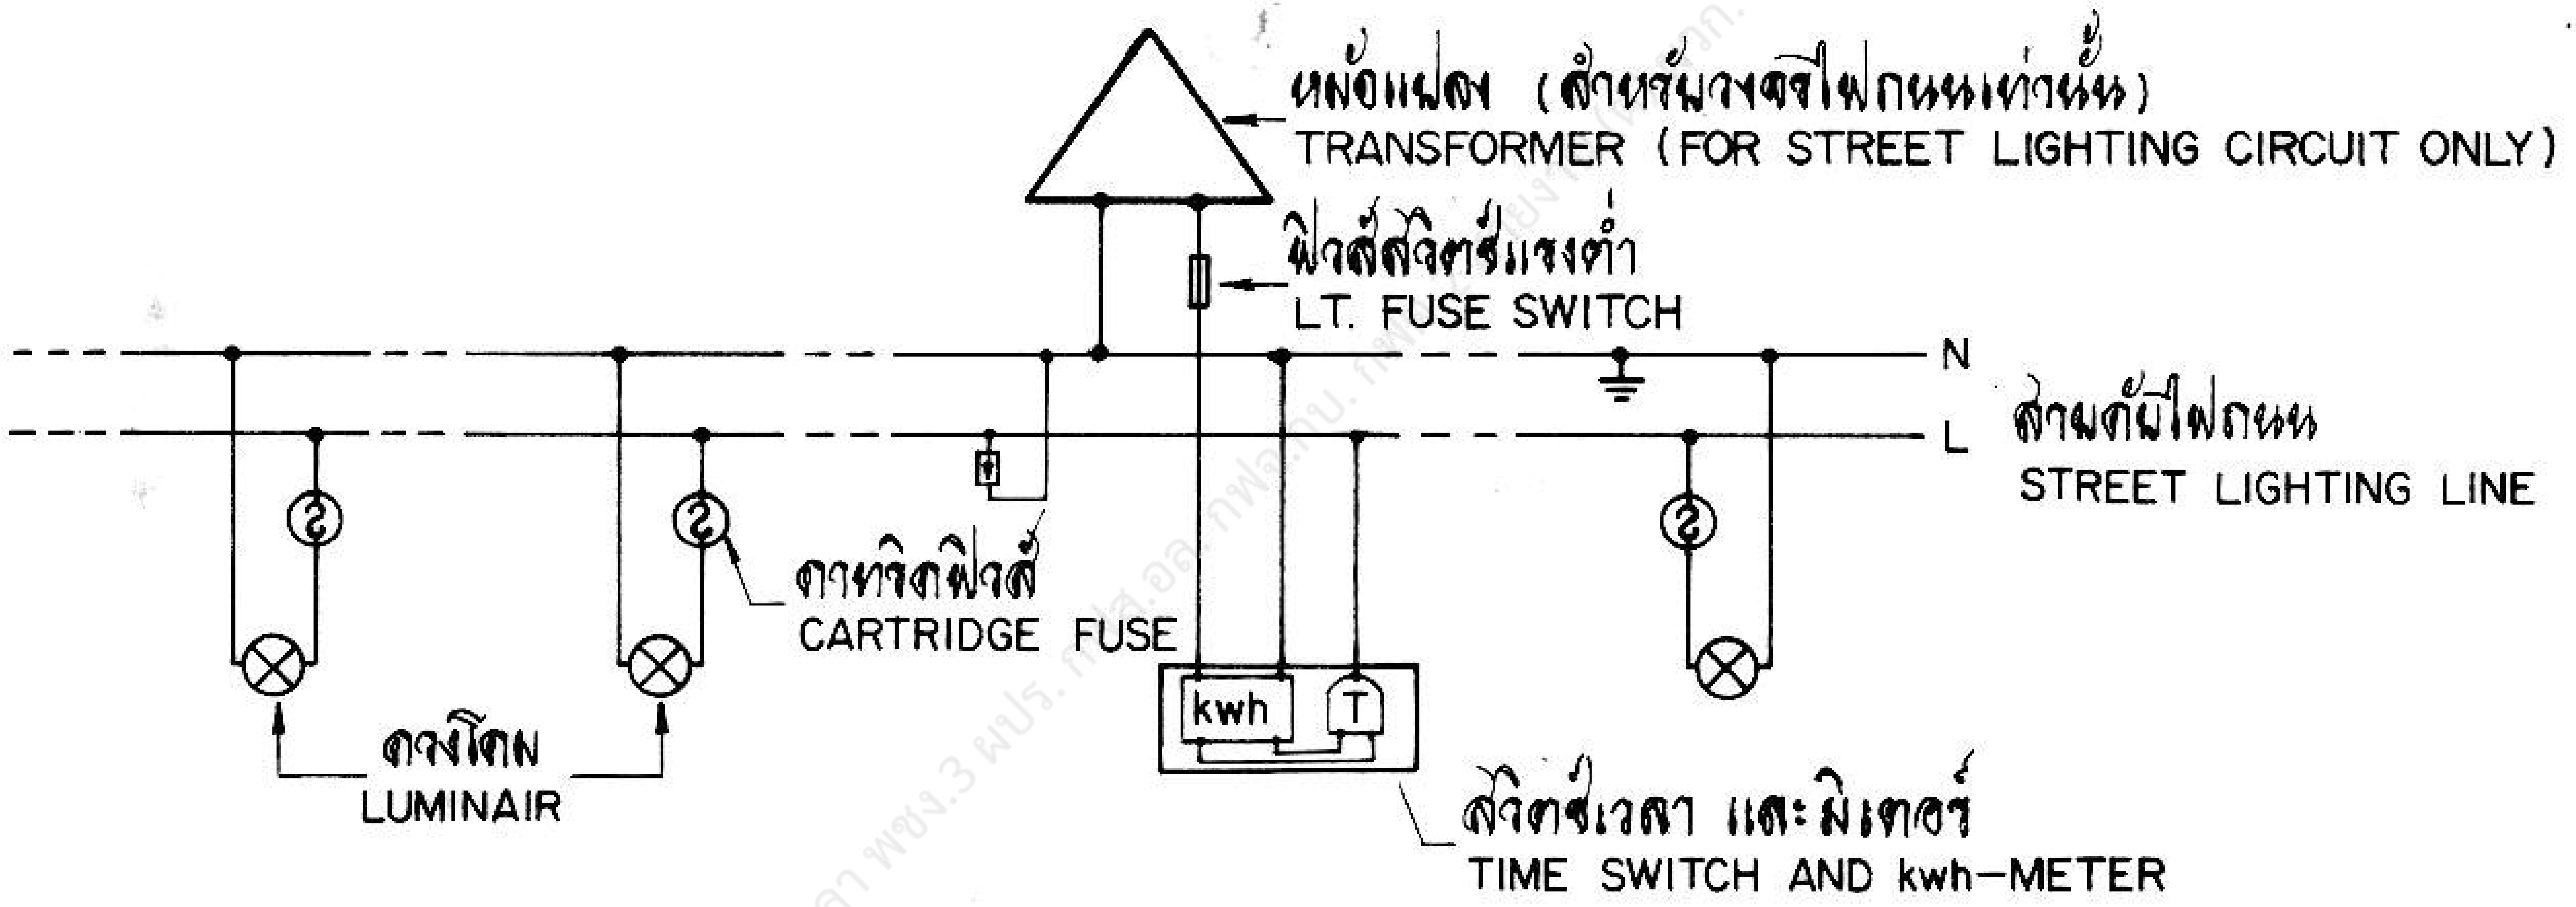

ไดอะแกรมการต่อสาย
WIRING DIAGRAM

กองวิศวกรรมไฟฟ้าและเครื่องกล ฝ่ายวิศวกรรม	การไฟฟ้าส่วนภูมิภาค	ใช้แทนแผน ถูกแทนโดยแผน เขียนเสร็จวันที่ 3 มี.ค. 26 แก้แผนวันที่ มิติเป็น มาตราส่วน
ผู้เขียน ผู้สำรวจ วิศวกร หัวหน้าแผนก ผู้อำนวยการกอง ผู้อำนวยการฝ่าย	ผู้ว่าการ ๑๑ ส.ค. ๒๖	
	การติดตั้งสวิตช์เวลา	
รองผู้ว่าการฝ่ายเทคนิค	TIME SWITCH INSTALLATION	แผนเลขที่ SAI-015/26009 แผ่นที่ 6 ของจำนวน 6 แผ่น