การประกอบเลขที่ **5270**
ASSEMBLY NO.

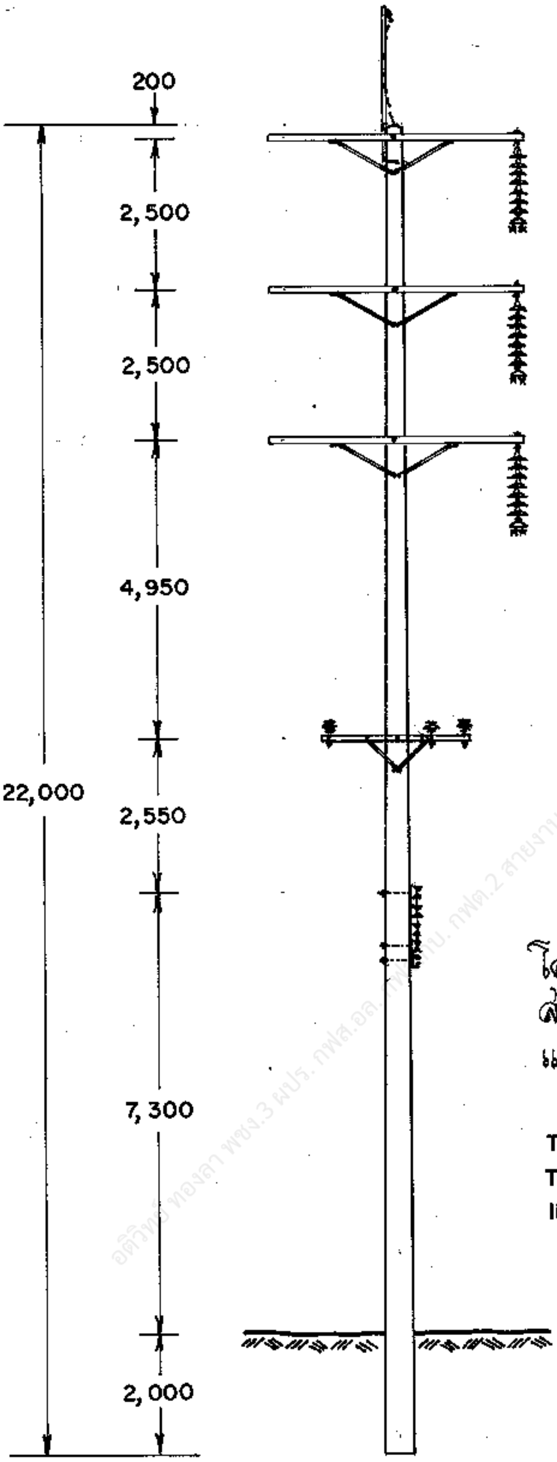

โครงสร้างนี้ ใช้งานได้เช่นเดียวกับโครงสร้าง แบบ SD-TG-1 (โครงสร้างแตกต่างกันที่วัสดุรายการที่ ② และ ⑦)

THIS STRUCTURE IS USED AS SD-TG-1 TYPE STRUCTURE (MATERIAL DIFFERENCE IN ITEM ② AND ⑦ FOR EACH STRUCTURE)

อดิวิทย์ ทองลา พชง.3 ผปร. กฟส.อล. [illegible] กฟต.2 สายงาน (ต) ผวก. @PEA

กองวิศวกรรมไฟฟ้าและเครื่องกล
ฝ่ายวิศวกรรม

ผู้เขียน
ผู้ตรวจ
วิศวกร
หัวหน้าแผนก
ผู้อำนวยการกอง
ผู้อำนวยการฝ่าย

รองผู้ว่าการฝ่ายเทคนิค

การไฟฟ้าส่วนภูมิภาค

ผู้ว่าการ 16 กค 35

115 kV วงจรเดี่ยว สายไฟฟ้าคู่
เสาสำหรับทางตรง
แบบ SD-TG-5

115 kV SINGLE CIRCUIT DOUBLE CONDUCTOR
TANGENT STRUCTURE
TYPE SD-TG-5

ใช้แทนแบบ
ถูกแทนโดยแบบ
เขียนเสร็จวันที่ 30 มิ.ย. 35
แก้แบบวันที่
มิติเป็น มิลลิเมตร
มาตราส่วน 1 : 125

แบบเลขที่ SAI-015/35023
แผ่นที่ 1 ของจำนวน 3 แผ่น

13 ก.ค. 2535

การประกอบเลขที่
ASSEMBLY NO. 5270

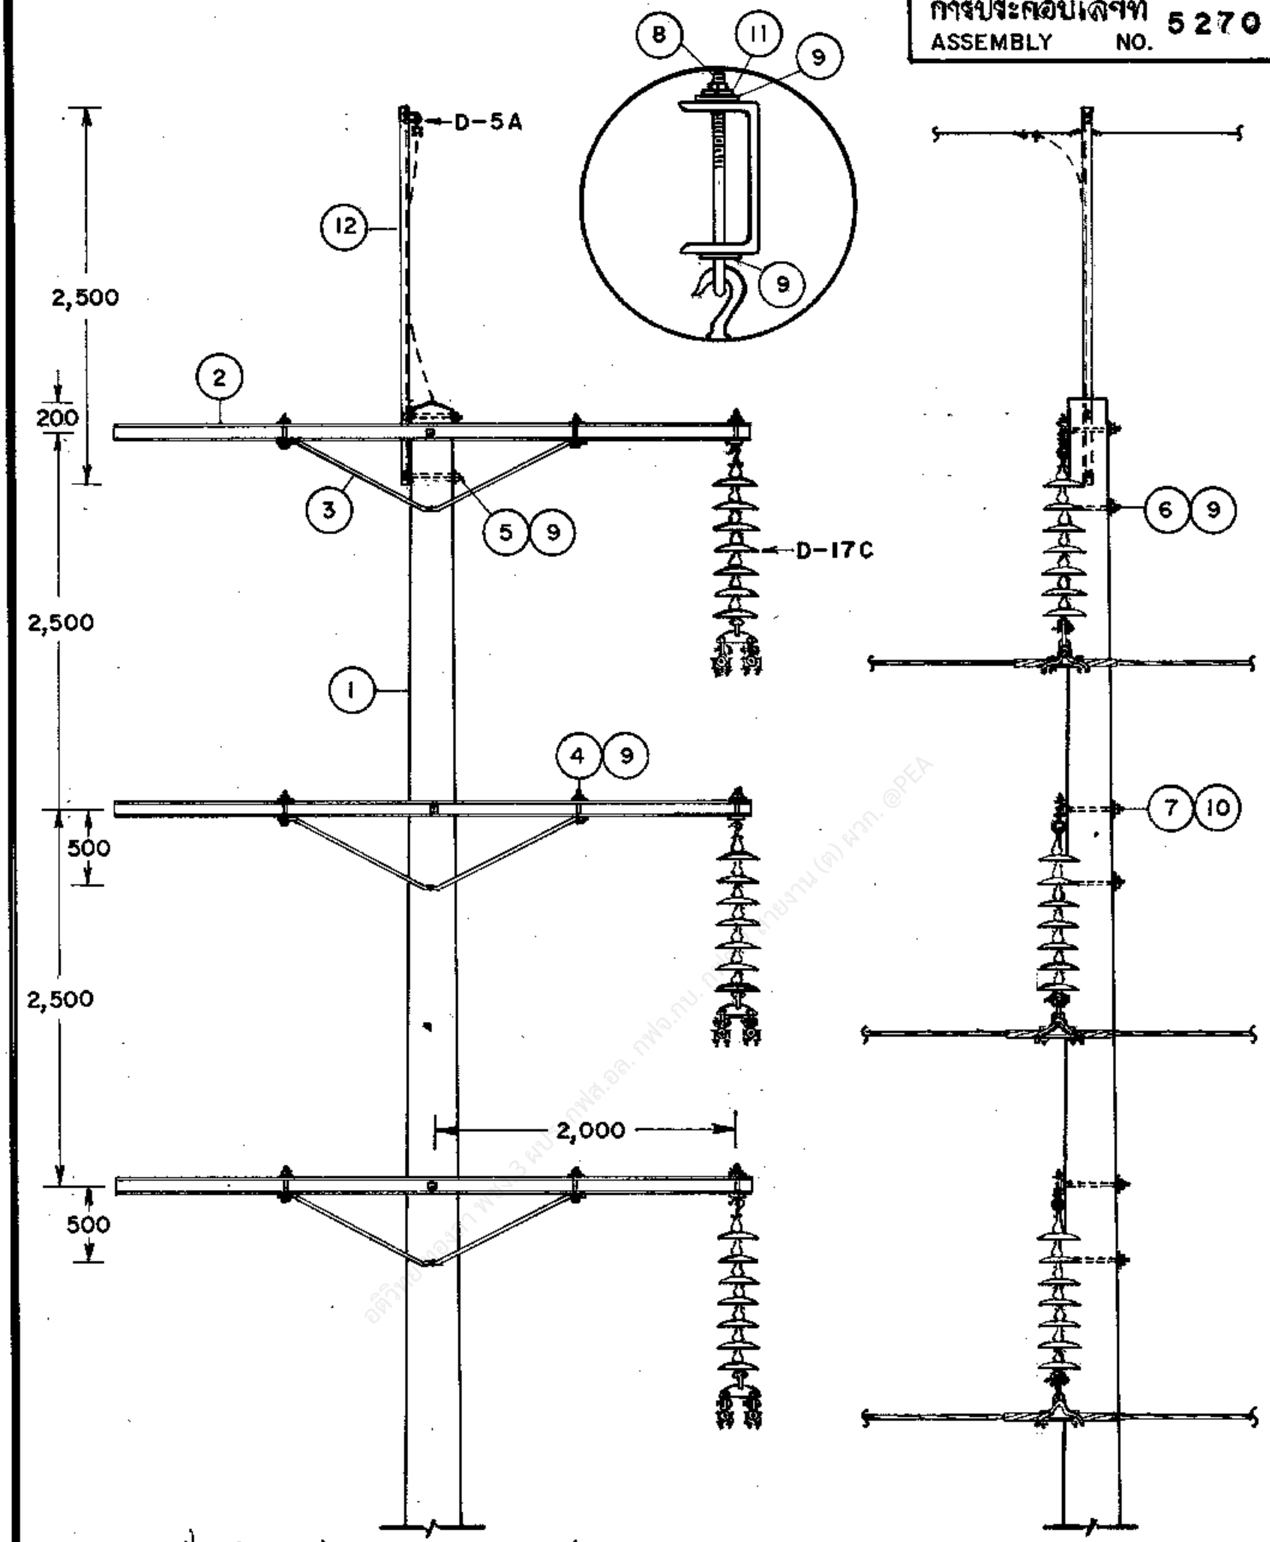

โครงสร้างนี้ใช้งานได้เช่นเดียวกับโครงสร้าง แบบ SD-TG-1
THIS STRUCTURE IS USED AS SD-TG-1 TYPE STRUCTURE

กองวิศวกรรมไฟฟ้าและเครื่องกล ฝ่ายวิศวกรรม	# การไฟฟ้าส่วนภูมิภาค	ใช้แทนแบบ ถูกแทนโดยแบบ เขียนเสร็จวันที่ 30 มิ.ย.35 แก้แบบวันที่ มิติเป็น มิลลิเมตร มาตราส่วน 1 : 5, 1 : 50
ผู้เขียน ผู้ตรวจ วิศวกร หัวหน้าแผนก ผู้อำนวยการกอง ผู้อำนวยการฝ่าย	ผู้ว่าการ 16 กค35 115 kV วงจรเดี่ยว สายไฟฟ้าคู่ เสาสำหรับทางตรง แบบ SD-TG-5	
รองผู้ว่าการฝ่ายเทคนิค	115 kV SINGLE CIRCUIT DOUBLE CONDUCTOR TANGENT STRUCTURE TYPE SD-TG-5	แบบเลขที่ SAI-015/35023 แผ่นที่ 2 ของจำนวน 3 แผ่

13 ก.ค. 2535

อดิวิทย์ ทองงาก พพง.3 ผปร. กฟส.อล. กฟจ.กบ. ฝ่ายงาน (ต) ผวก. @PEA

การประกอบเลขที่ ASSEMBLY NO. **5270**

บัญชีวัสดุ
BILL OF MATERIAL

ลำดับที่ ITEM	รายละเอียด DESCRIPTION	จำนวน REQ'D	วัสดุเลขที่ MAT. NO.
1	เสาคอนกรีต 22 ม. POLE, CONCRETE 22 m LONG	1	00010011 (0041)
2	คอนสายแบบเหล็กขนาด [100X50X5 มม. ยาว 4.20 ม. มอก. 116 CROSSARM, STEEL [100X50X5 mm, 4.20 m LONG, TIS 116	3	
3	เหล็กฉากรับคอนสาย ขนาด 50X50X6 มม. ช่วงกว้าง 1,800 มม. ดรอพ 450 มม. BRACE, ANGLE STEEL, 50X50X6 mm, 1,800 mm, WIDE 450 mm, DROP	3	01200007 (0119)
4	สลักเกลียว M 16X130 มม. BOLT, MACHINE, M 16X130 mm	6	01110200 (0220)
5	สลักเกลียว M 16X300 มม. BOLT, MACHINE, M 16X300 mm	3	01110204 (0224)
6	สลักเกลียว M 16X350 มม. BOLT, MACHINE, M 16X350 mm	2	01110205 (0225)
7	สลักเกลียว M 20X350 มม. BOLT, MACHINE, M 20X350 mm	3	01110300 (0232)
8	สลักห่วงโอแวล M 16X150 มม. BOLT, OVAL EYE M 16X150 mm	3	01150000 (0257)
9	แหวนสี่เหลี่ยมแบน 52X52X4.5 มม. รู Ø 18 มม. มอก. 258 WASHER, SQUARE FLAT 52X52X4.5 mm, HOLE Ø 18 mm, TIS 258	17	01180100 (0355)
10	แหวนสี่เหลี่ยมแบน 62X62X6 มม. รู Ø 22 มม. มอก. 258 WASHER, SQUARE FLAT 62X62X6 mm, HOLE Ø 22 mm, TIS 258	6	01180101 (0356)
11	แหวนสปริง M 16 มอก. 259 WASHER, LOCK, M 16, TIS 259	3	01180301 (0365)
12	เหล็กฉากรับสายล่อฟ้าทางตรง ยาว 2.50 ม. OVERHEAD GROUND WIRE BAYONET 2.50 m LONG	1	01010004 (0135)

รายละเอียด
DETAIL

D-17C	การประกอบลูกถ้วยแขวน SUSPENSION INSULATOR ASSEMBLY	3	
D-5A	การต่อสายล่อฟ้า OVERHEAD GROUND WIRE CONNECTION	1	
D-10A	ฐานรากเสา POLE FOUNDATION	1	

วัสดุลำดับที่ ②
MAT. ITEM

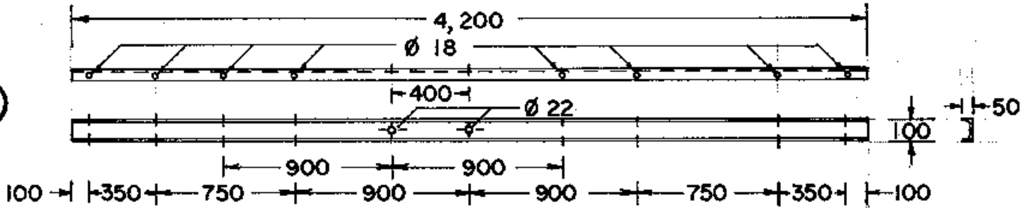

กองวิศวกรรมไฟฟ้าและเครื่องก ฝ่ายวิศวกรรม	**การไฟฟ้าส่วนภูมิภาค**	ใช้แทนแบบ ถูกแทนโดยแบบ เขียนเสร็จวันที่ 30 มิ.ย.35 แก้แบบวันที่ มิติเป็น มิลลิเมตร มาตราส่วน 1 : 40
ผู้เขียน ผู้สำรวจ วิศวกร หัวหน้าแผนก ผู้อำนวยการกอง ผู้อำนวยการฝ่าย	ผู้ว่าการ 16 กค35 115 kV วงจรเดี่ยว สายไฟฟ้าคู่ เสาสำหรับทางตรง แบบ SD-TG-5	
รองผู้ว่าการฝ่ายเทคนิค	115 kV SINGLE CIRCUIT DOUBLE CONDUCTOR TANGENT STRUCTURE TYPE SD-TG-5	แบบเลขที่ SAI-015/35023 แผ่นที่ 3 ของจำนวน 3 แผ่น

3 ก.ค. 25