การประกอบเลขที่
ASSEMBLY NO. 0707

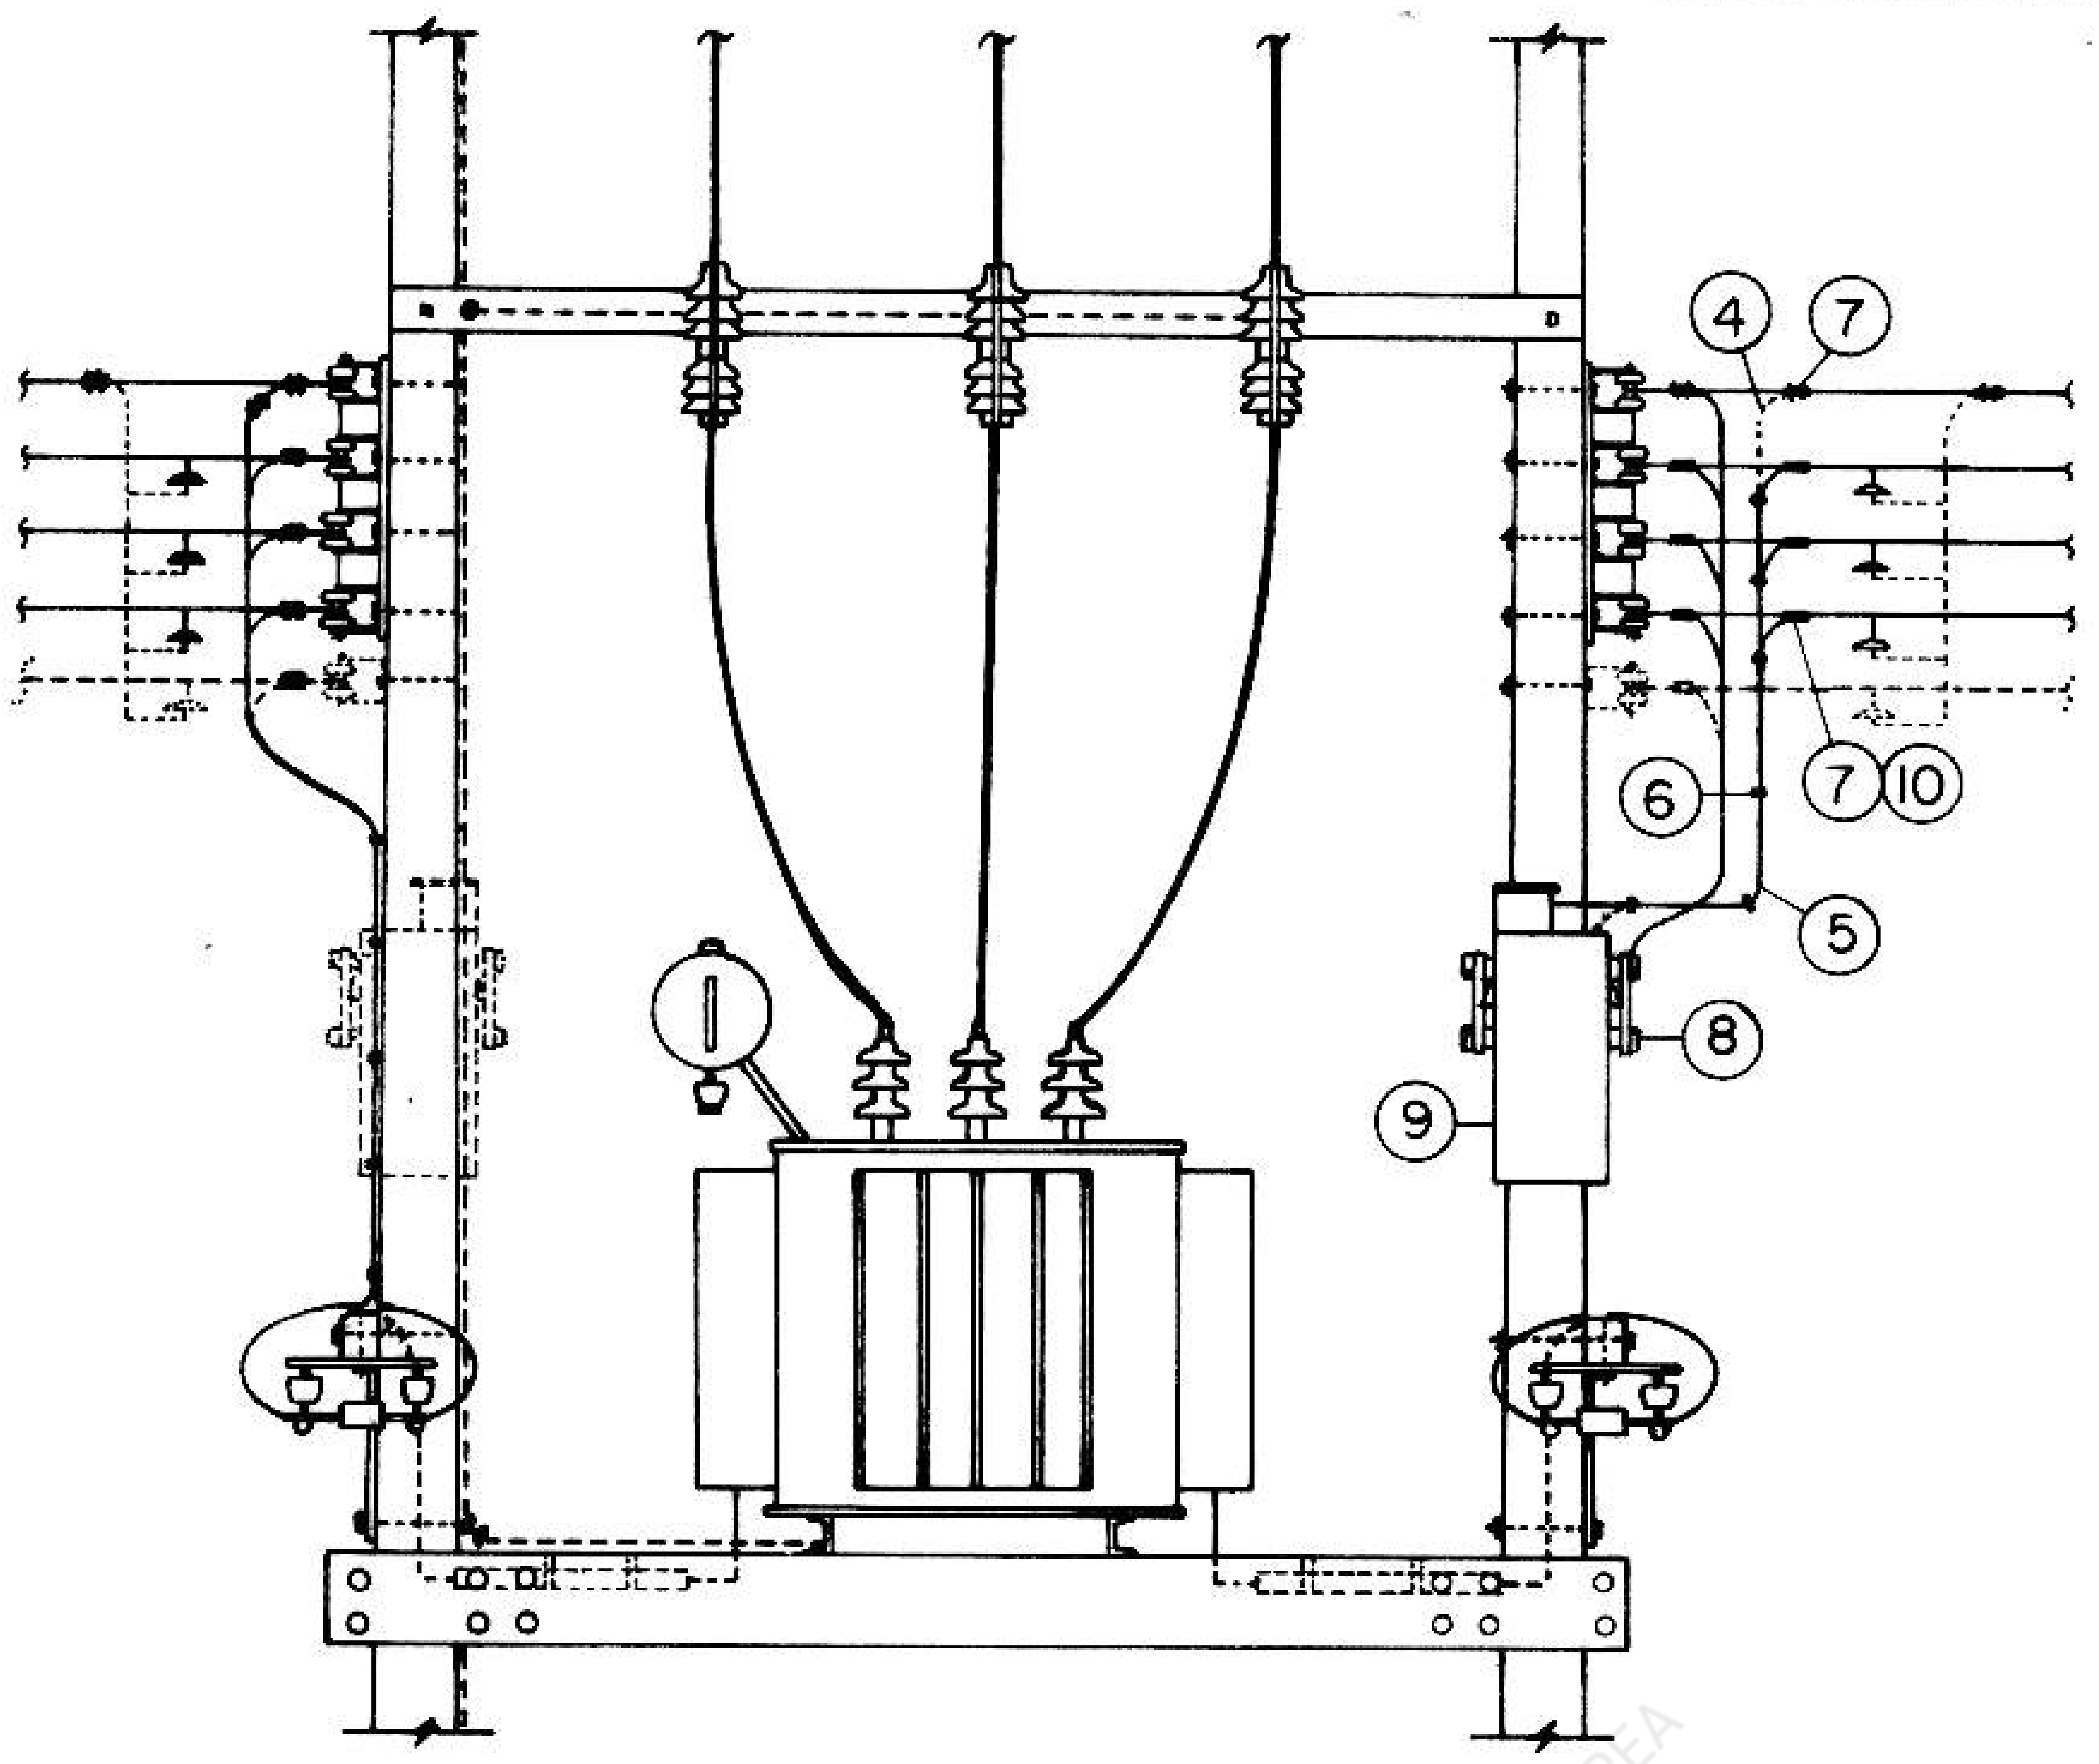

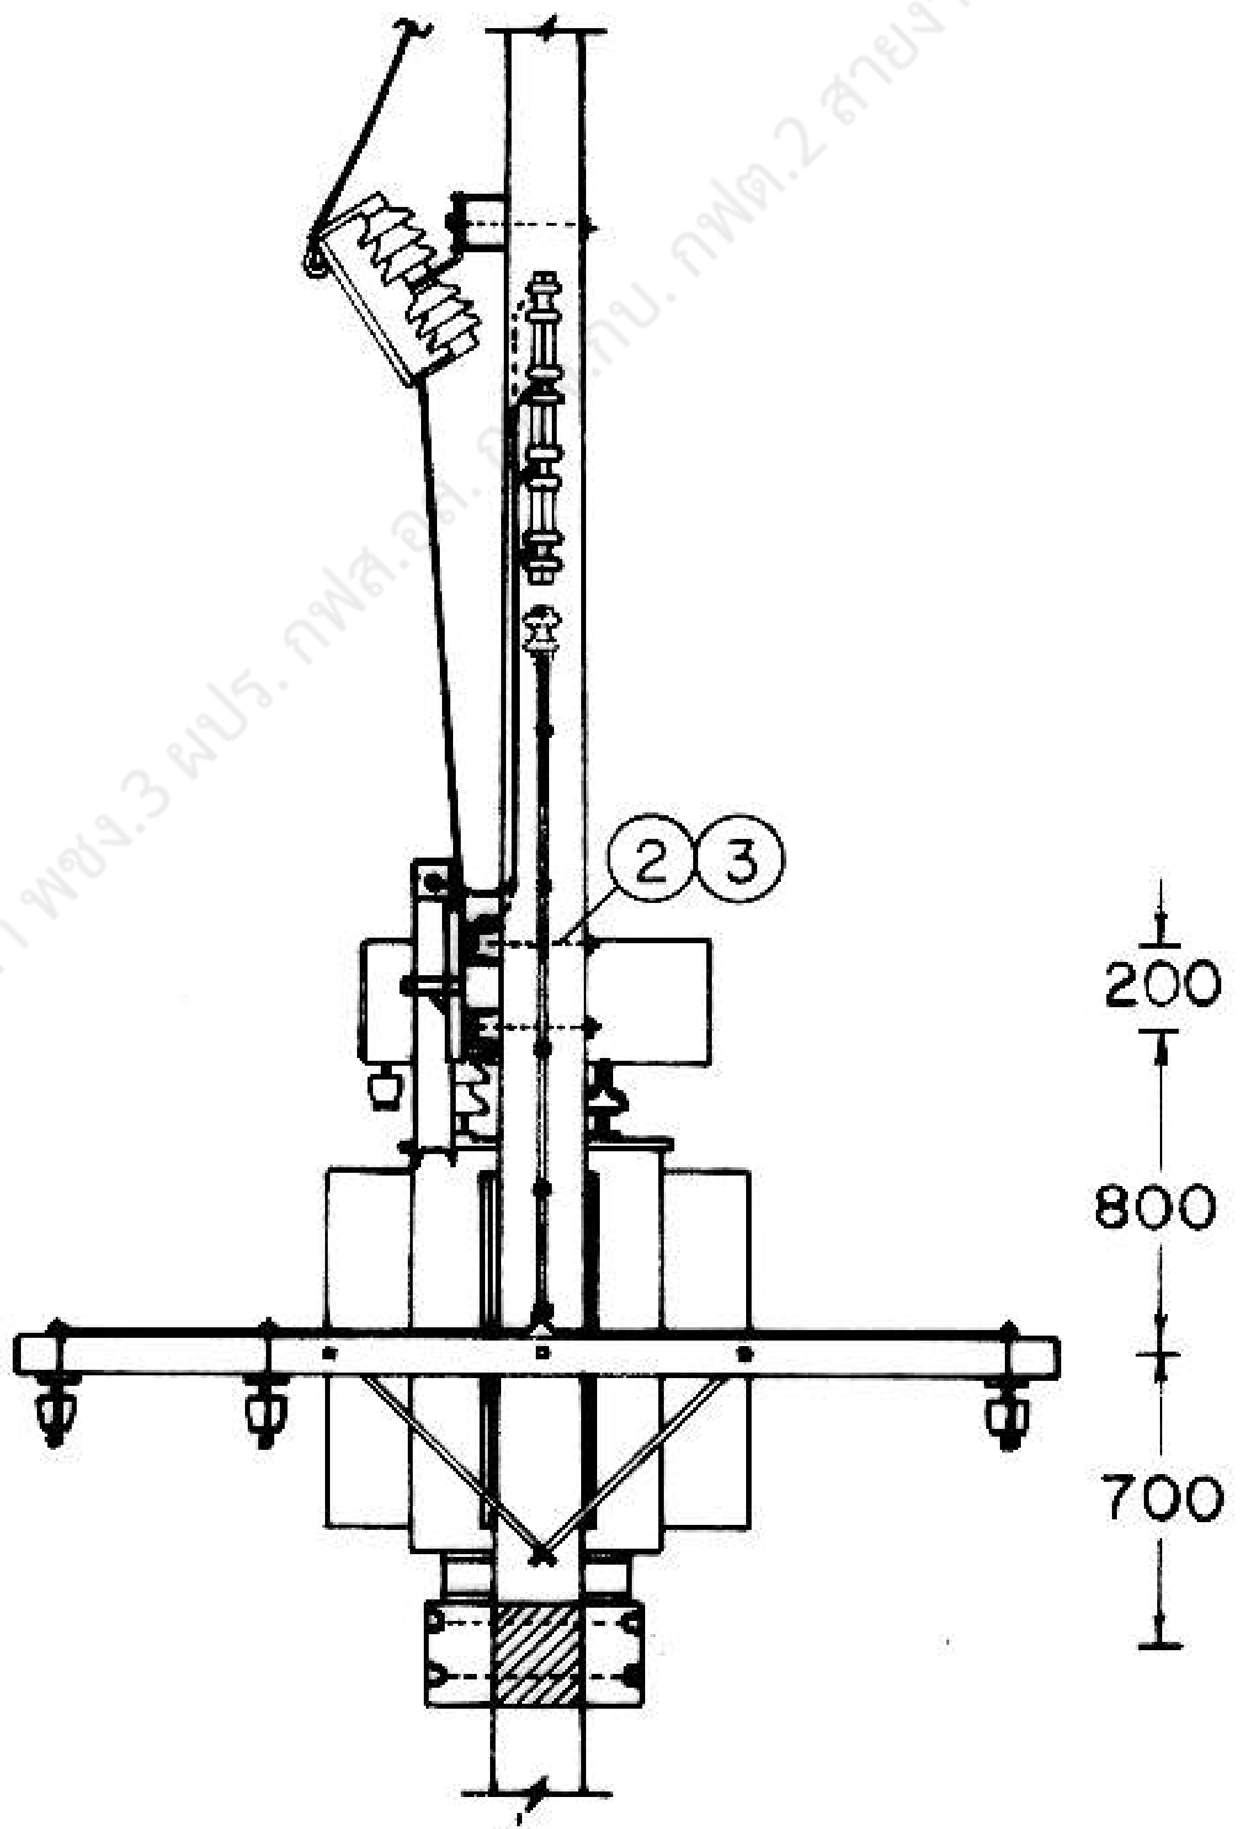

แบบที่
TYPE I

อติวิทย์ ทองลา พชง.3 ผปร. กฟส.อ[illegible] กฟต.2 สายงาน (ต) ผวก. @PEA

กองวิศวกรรมไฟฟ้าและเครื่องกล
ฝ่ายวิศวกรรม

ผู้เขียน
ผู้สำรวจ
วิศวกร
หัวหน้าแผนก
หัวหน้ากอง
ผู้อำนวยการฝ่าย
รองผู้ว่าการฝ่ายเทคนิค

การไฟฟ้าส่วนภูมิภาค

ผู้ว่าการ

การติดตั้งคะแปซิเตอร์ 3 เฟส 400 โวลต์
ที่เสาต้นหั่งร้านหม้อแปลง

3-Ø 400 V CAPACITOR INSTALLATION
AT TRANSFORMER STATION

ใช้แทนแบบ
ถูกแทนโดยแบบ
เขียนเสร็จวันที่ 30 พ.ย. 21
แก้แบบวันที่
มิติเป็น มม.
มาตราส่วน 1 : 50

แบบเลขที่ SA1-015/21077
แผ่นที่ 1 ของจำนวน 3 แผ่น

การประกอบเลขที่
ASSEMBLY NO. 0707

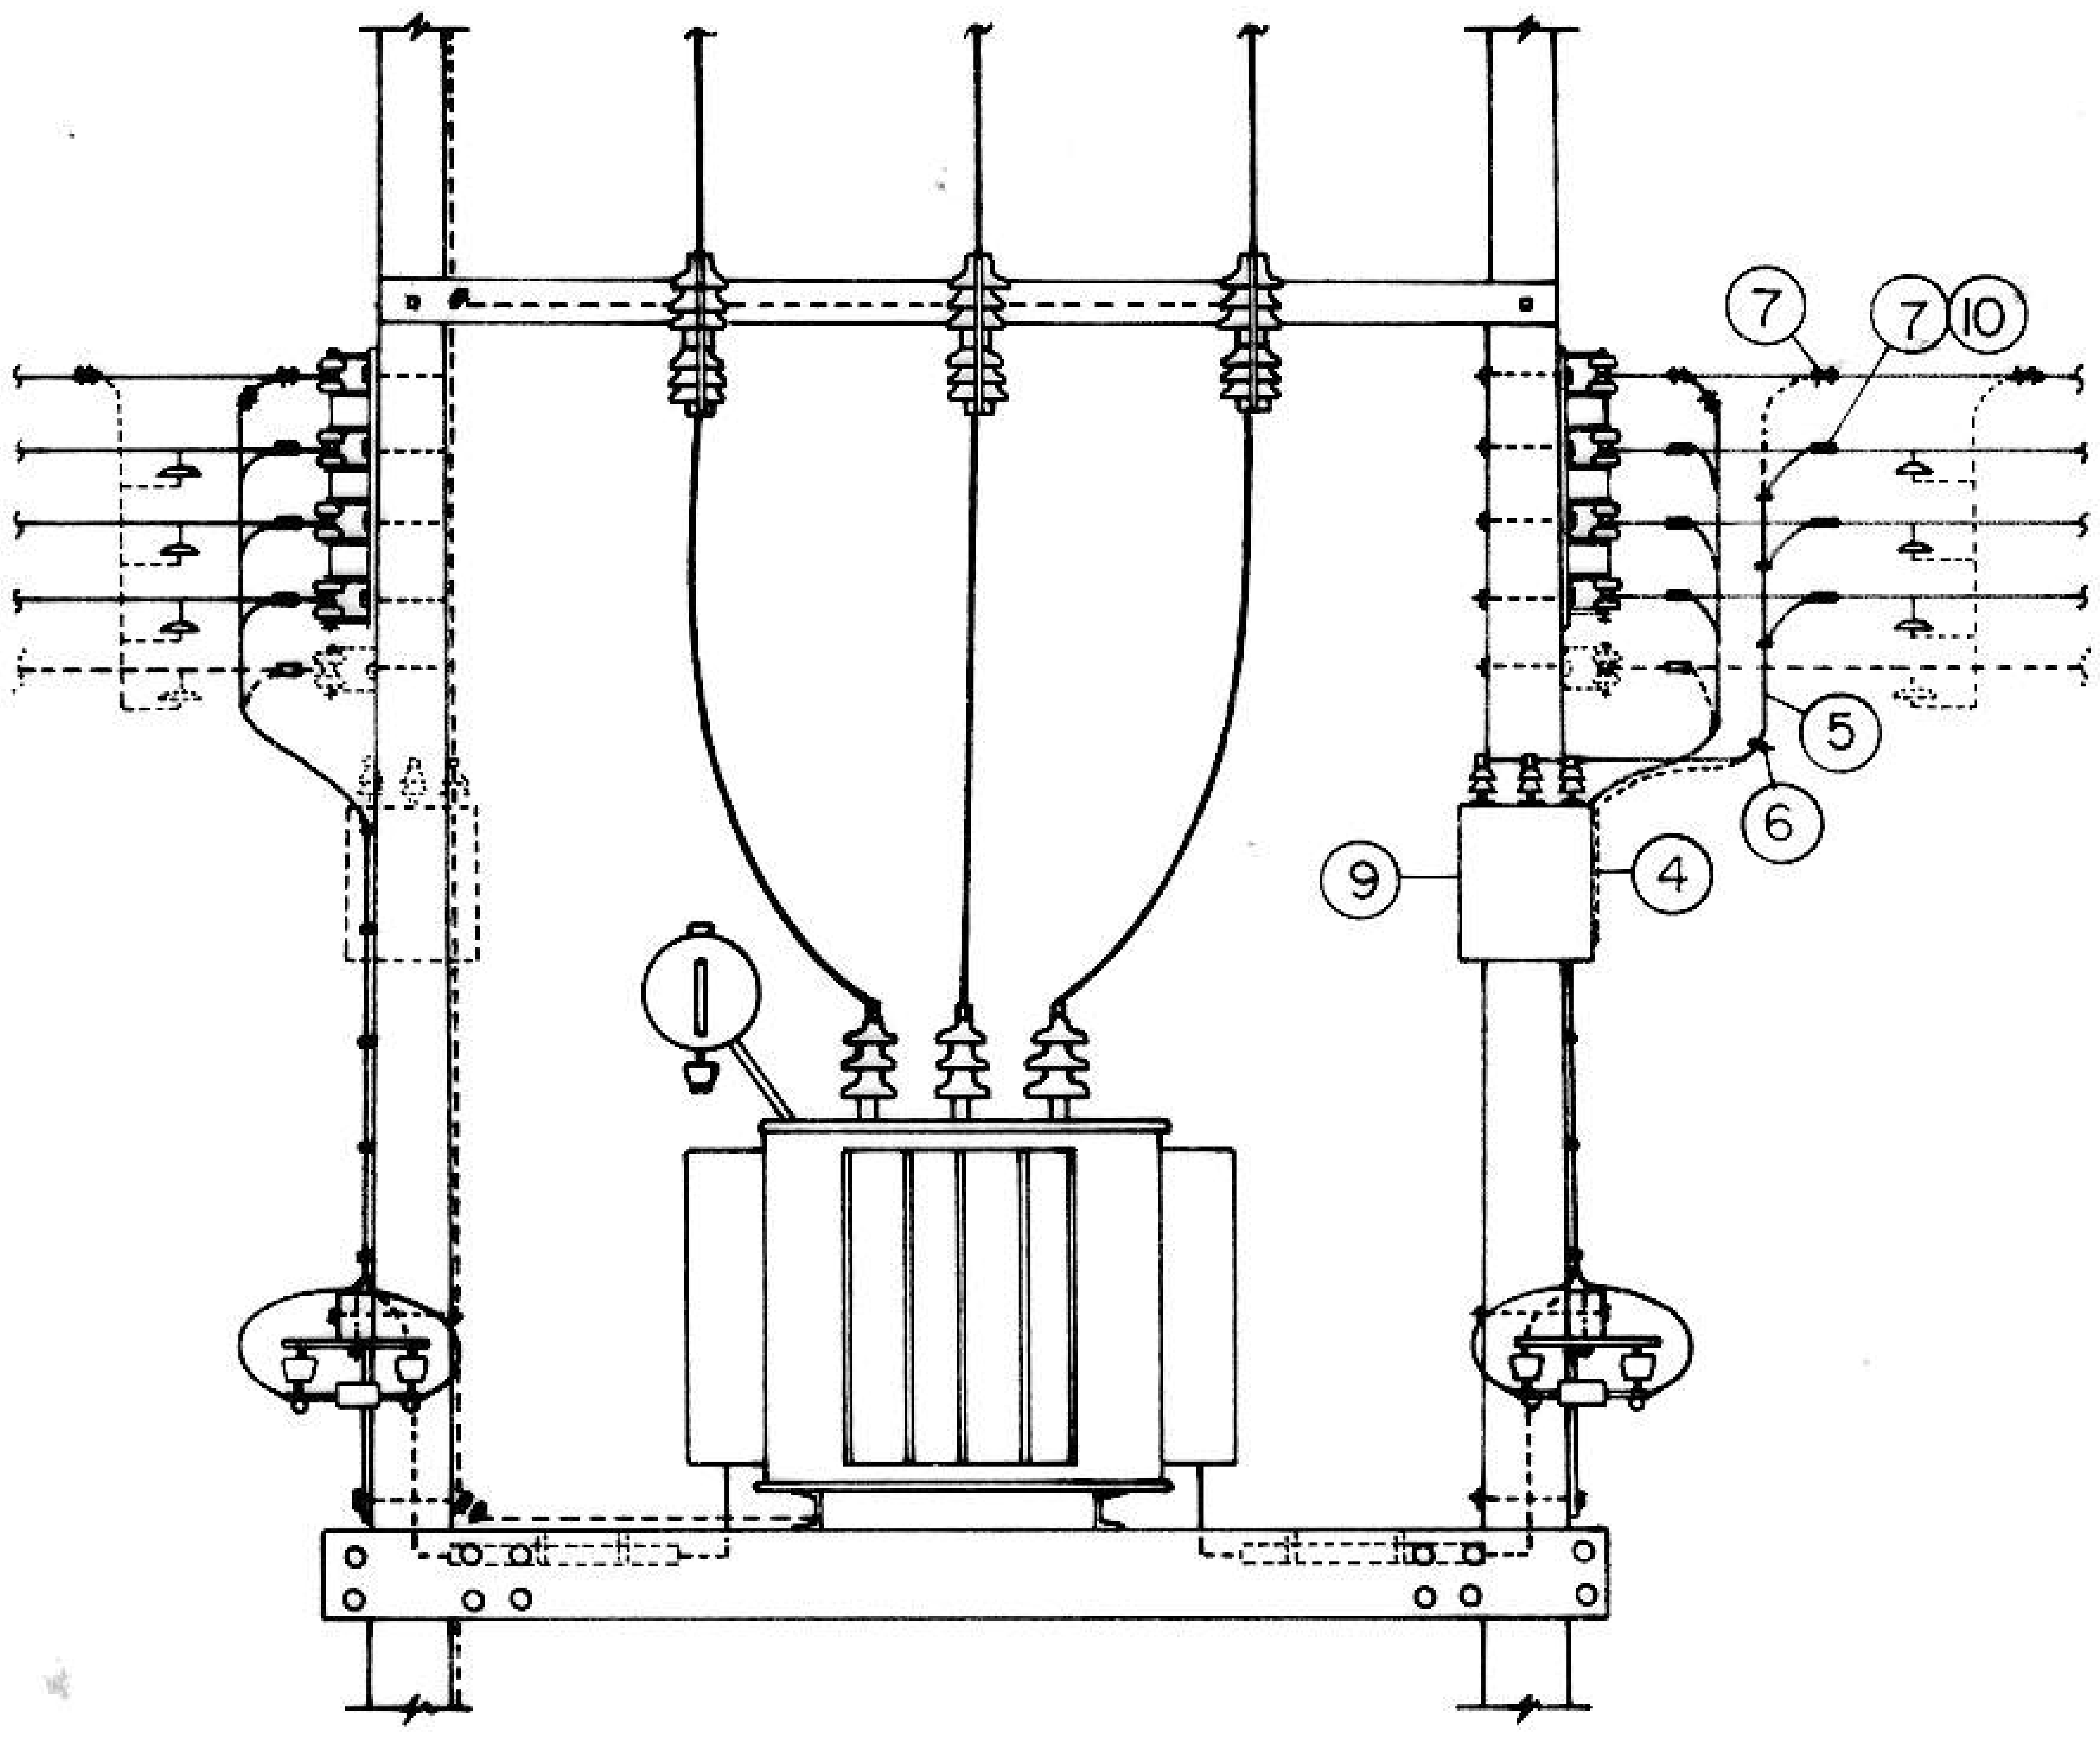

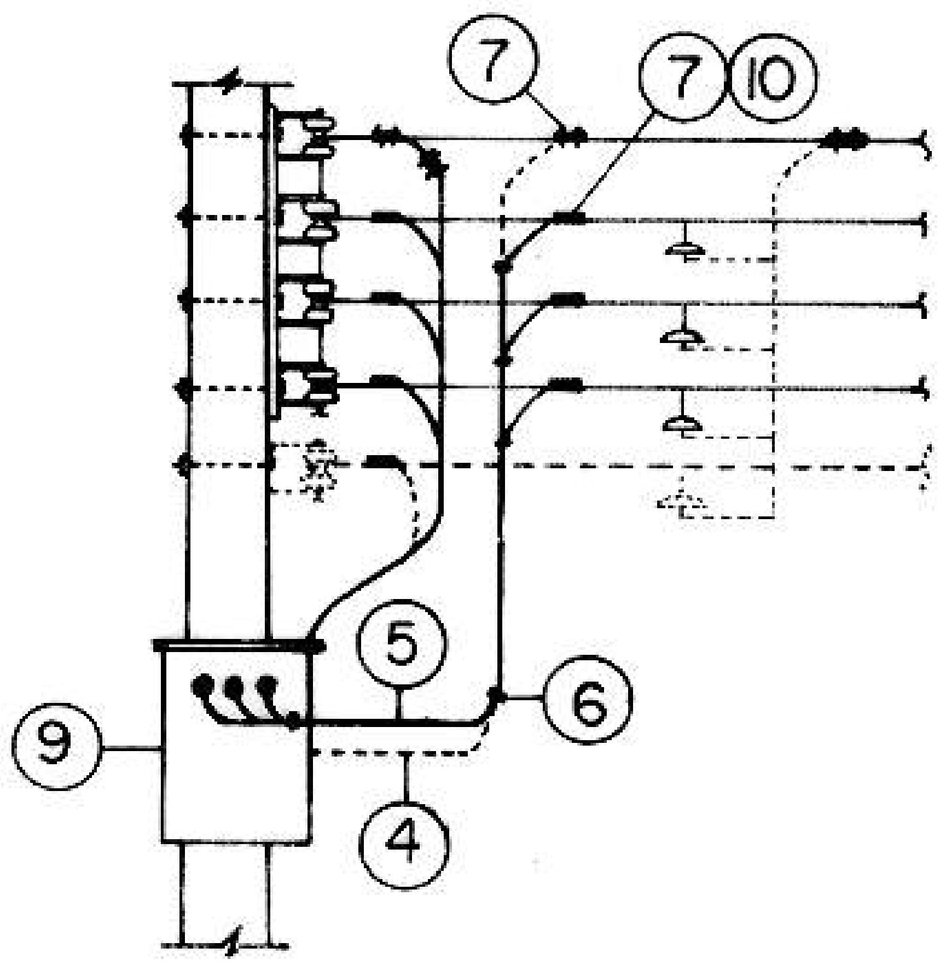

แบบเผื่อเลือก
ALTERNATIVE

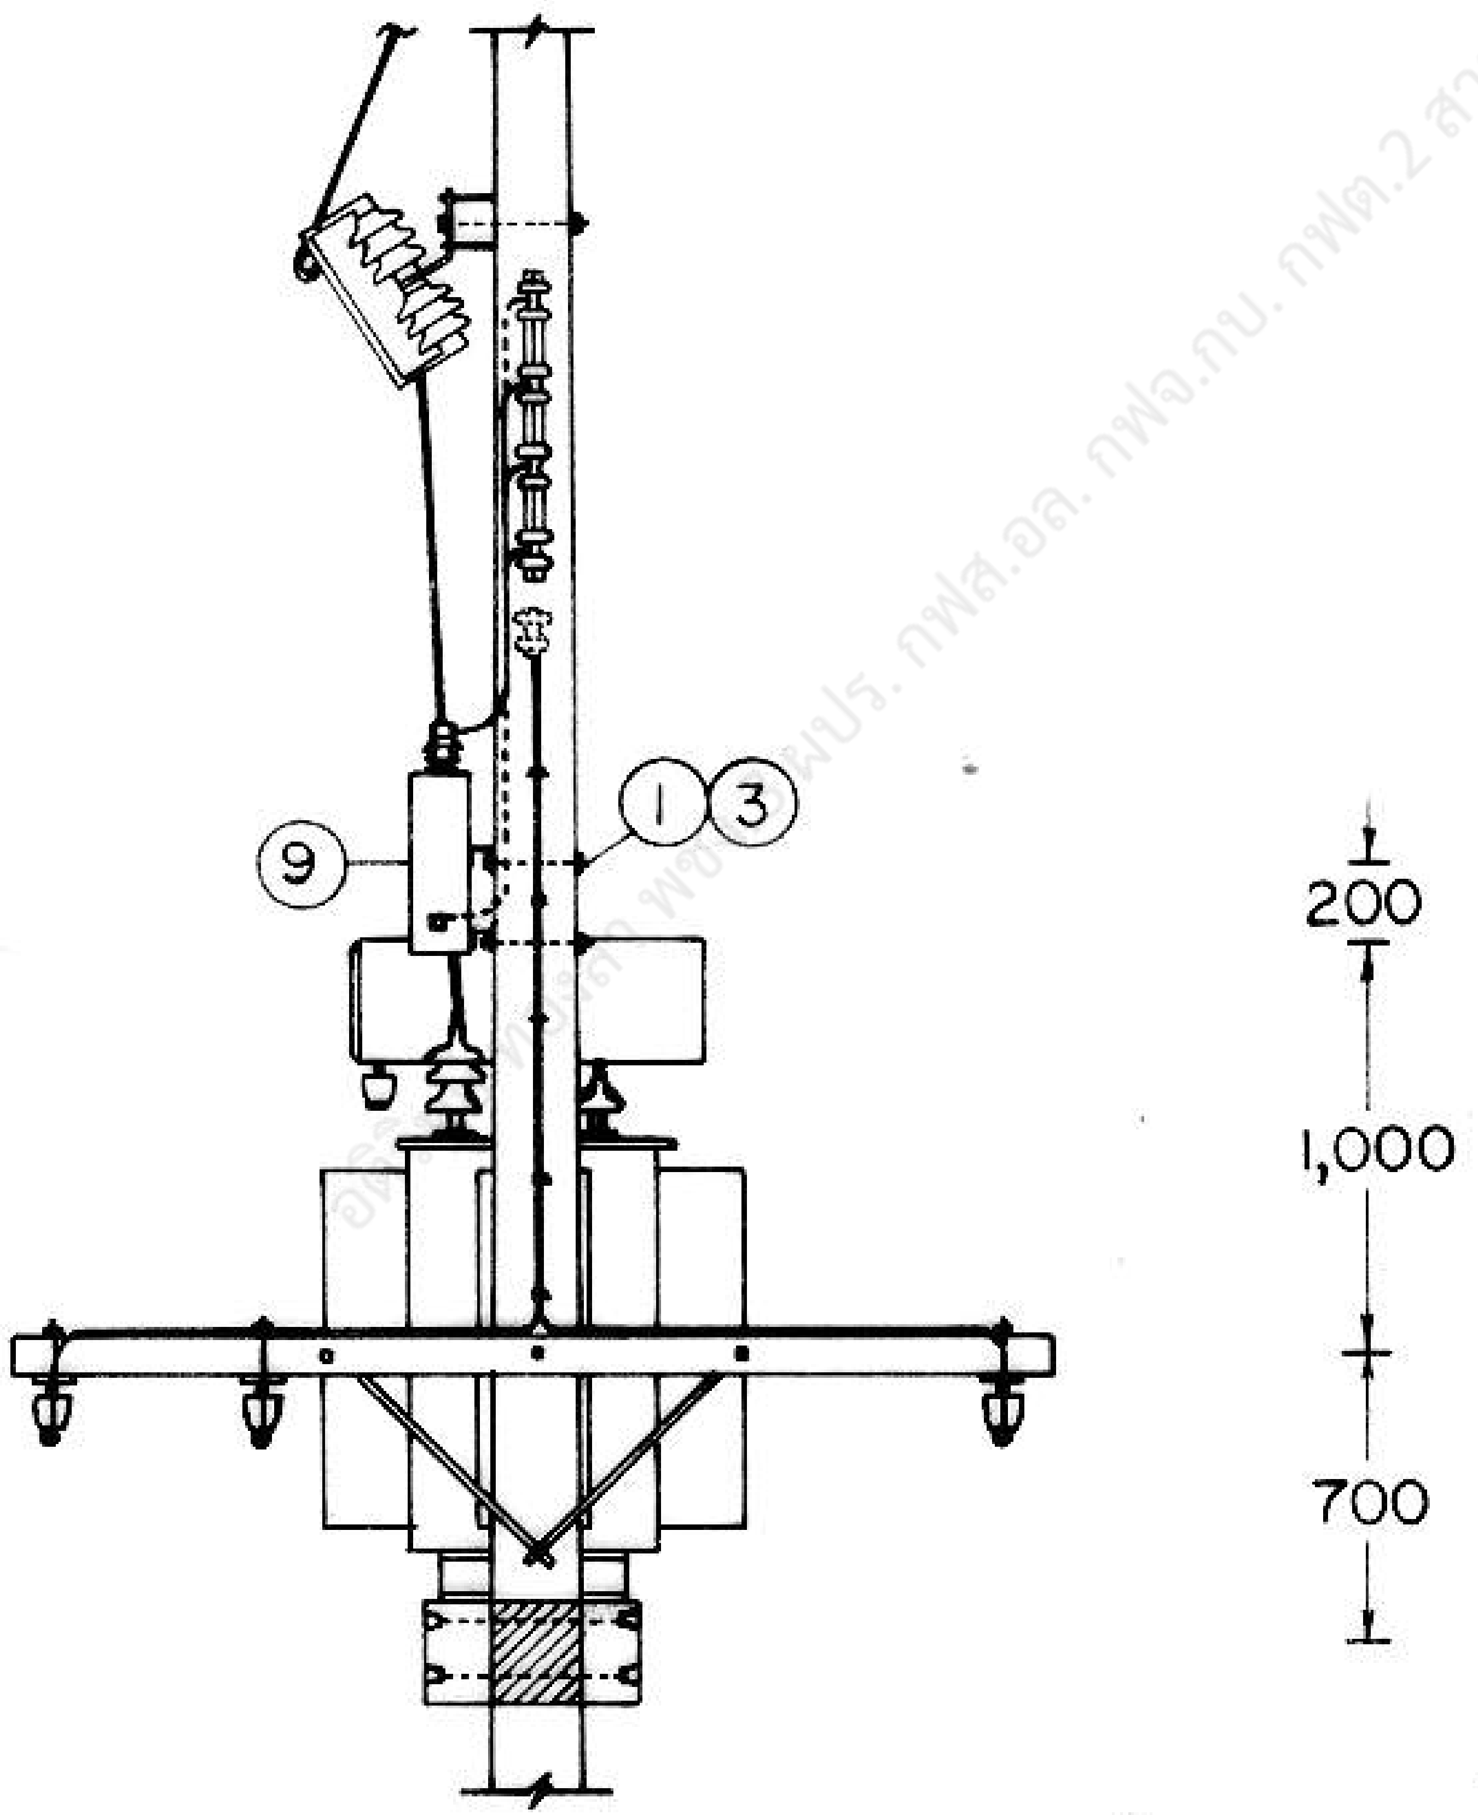

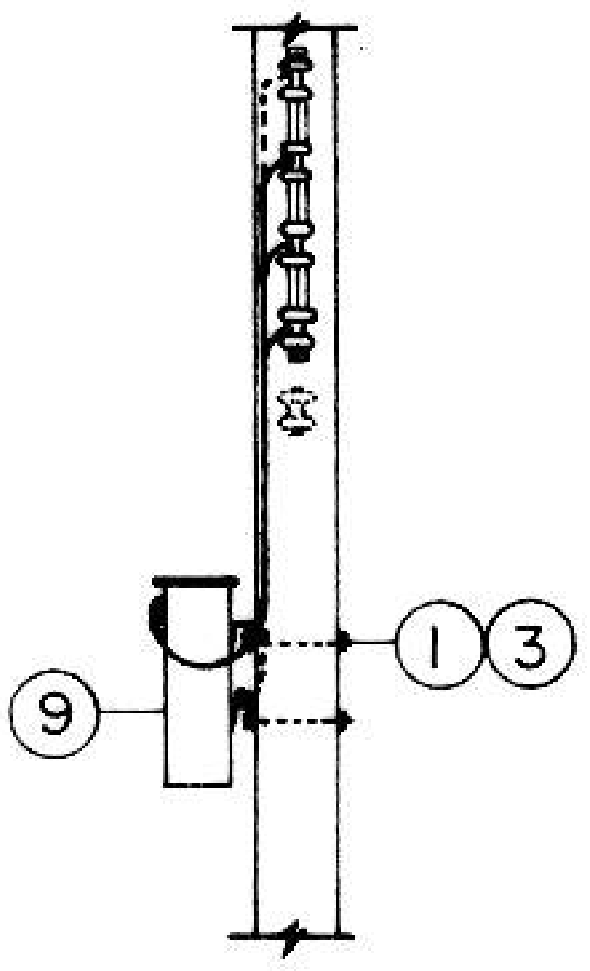

แบบเผื่อเลือก
ALTERNATIVE

แบบที่
TYPE II

กฟปร. กฟส.อล. กฟจ.กบ. กฟต.2 สายงาน (ต) ผวก. @PEA

กองวิศวกรรมไฟฟ้าและเครื่องกล
ฝ่ายวิศวกรรม

ผู้เขียน
ผู้ตรวจ
วิศวกร สิทธิพงษ์
หัวหน้าแผนก
หัวหน้ากอง
ผู้อำนวยการฝ่าย
รองผู้ว่าการฝ่ายเทคนิค

การไฟฟ้าส่วนภูมิภาค

ผู้ว่าการ

การติดตั้งคะแปซิเตอร์ 3 เฟส 400 โวลต์
ที่เสาต้นนั่งร้านหม้อแปลง

3-Ø 400 V CAPACITOR INSTALLATION
AT TRANSFORMER STATION

ใช้แทนแบบ
ถูกแทนโดยแบบ
เขียนเสร็จวันที่ 30 พ.ย. 21
แก้แบบวันที่
มิติเป็น มม.
มาตราส่วน 1 : 50

แบบเลขที่ SA1-015/21077
แผ่นที่ 2 ของจำนวน 3 แผ่น

การประกอบเลขที่
ASSEMBLY NO. 0707

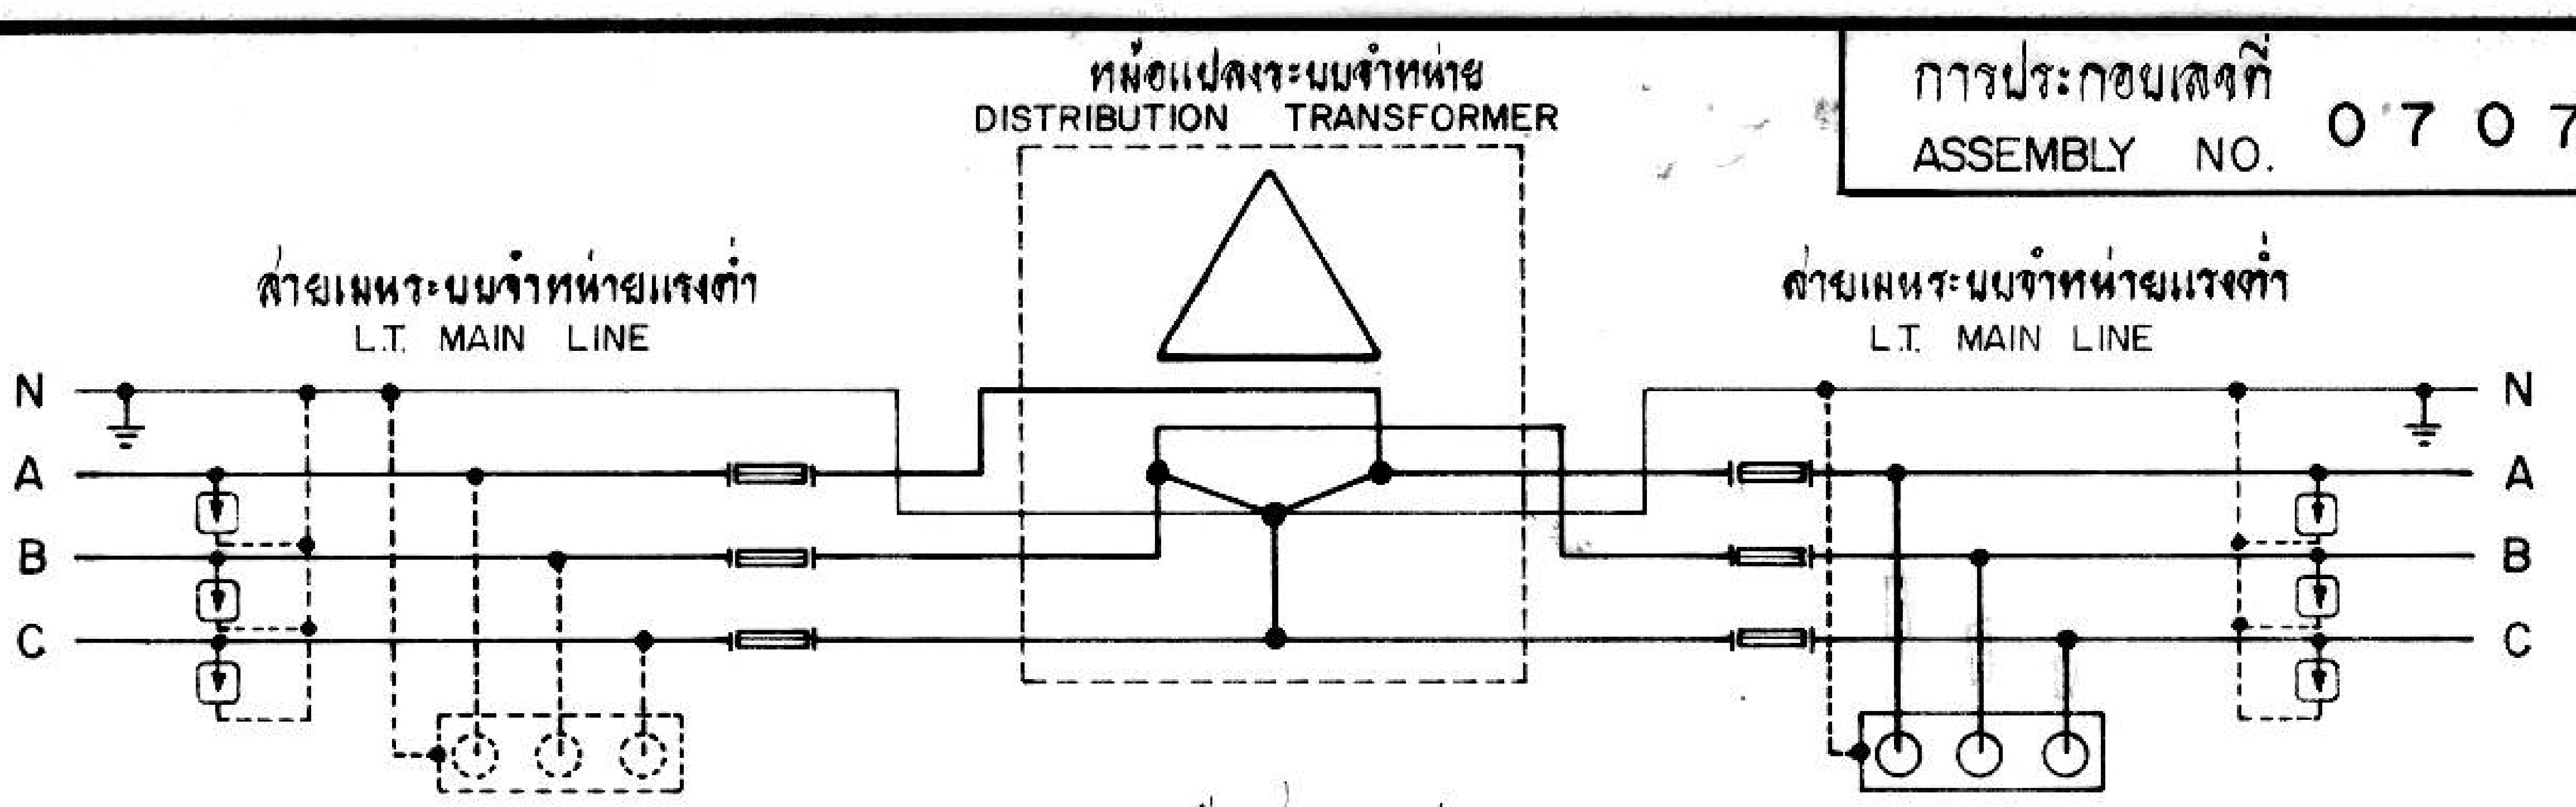

แผนผังแสดงการต่อ
CONNECTION DIAGRAM

บัญชีวัสดุ
BILL OF MATERIAL

ลำดับที่ ITEM	รายละเอียด DESCRIPTION	จำนวน REQ'D		วัสดุเลขที่ MAT. NO.
		I	II	
1	สลักเกลียว M 16 X 250 มม. BOLT, MACHINE, M 16 X 250 mm	–	2	01110203
2	สลักเกลียว M 16 X 300 มม. BOLT, MACHINE, M 16 X 300 mm	2	–	01110204
3	แหวนสี่เหลี่ยมแบน 52 X 52 X 4.5 มม. รู Ø 18 มม. **มอก.** 258 WASHER, SQUARE, FLAT, 52 X 52 X 4.5 mm, HOLE Ø 18 mm, TIS 258	4	6	01180100
4	ลวดเหล็กตีเกลียว 50/7 ต.มม. **มอก.** 404 WIRE, STEEL STRANDED, 50/7 mm², TIS 404	2 ม. m	2.5 ม. m	01100004
5	สายอะลูมิเนียมหุ้มฉนวน PVC 25-70 ต.มม. มอก. 293 CABLE, Al STRANDED, PVC-INSULATED, 25-70 mm², TIS 293	5 ม. m	5 ม. m	02070000-3
6	ลวดอะลูมิเนียมแบน ขนาด 1 X 10 มม. ความยาวตามต้องการ TAPE, ARMOUR, Al, 1 X 10 mm, LENGTH AS REQUIRED			02200000
7	**คอนเนคเตอร์ ชนิดบีบ แบบ H สำหรับสายอะลูมิเนียมขนาดตามต้องการ** CONNECTOR, COMPRESSION, H-TYPE, FOR Al CONDUCTOR, SIZE AS REQUIRED	4	4	02320003 02320002
8	ที่แขวนคะแปซิเตอร์แรงต่ำ แบบเลขที่ SAI-015/21003 L.T. CAPACITOR HANGER DWG. NO. SAI-015/21003	1	–	—
9	คะแปซิเตอร์ 3 เฟส ใช้นอกอาคาร 400 โวลต์ 5-75 กิโลวาร์ CAPACITOR, POWER, THREE-PHASE, OUTDOOR 400 V, 5-75 kvar	1	1	05040200-5
10	PVC เทป กว้าง 19 มม. (ใช้ความยาว 2 ม. ต่อ จุด) มอก. 386 PVC TAPE, 19 mm WIDE (2 m LONG PER POINT) TIS 386	6 ม. m	6 ม. m	02180001 or 02180002

หมายเหตุ
1. บัญชีวัสดุใช้สำหรับการติดตั้งคะแปซิเตอร์ 3 เฟส 400 โวลต์ เท่านั้น
2. แบบที่ I ใช้สำหรับคะแปซิเตอร์รุ่นเก่า ต้องใช้ที่แขวนคะแปซิเตอร์เพื่อประกอบยึดกับเสา
   แบบที่ II ใช้สำหรับคะแปซิเตอร์ที่จัดซื้อรุ่นใหม่ ซึ่งมีห่วงแขวนยึดกับเสาแล้ว

NOTES
1. BILL OF MATERIAL USED FOR 3-Ø 400 V CAPACITOR INSTALLATION ONLY.
2. TYPE I FOR PREVIOUS PURCHASING, THE CAPACITOR MUST BE USED WITH MOUNTING HANGER.
   TYPE II FOR NEW PURCHASING, THE CAPACITOR SHALL BE COMPLETED WITH MOUNTING LUGS.

กองวิศวกรรมไฟฟ้าและเครื่องกล ฝ่ายวิศวกรรม	**การไฟฟ้าส่วนภูมิภาค**	ใช้แทนแบบ ถูกแทนโดยแบบ
ผู้เขียน ผู้สำรวจ วิศวกร หัวหน้าแผนก หัวหน้ากอง ผู้อำนวยการฝ่าย	ผู้ว่าการ 20 ธ.ค. 21	เขียนเสร็จวันที่ 30 พ.ย. 21 แก้แบบวันที่ 1 ก.พ. 31
	การติดตั้งคะแปซิเตอร์ 3 เฟส 400 โวลต์ ที่เสาต้นนั่งร้านหม้อแปลง	มิติเป็น มาตราส่วน
รองผู้ว่าการฝ่ายเทคนิค	3-Ø 400 V CAPACITOR INSTALLATION AT TRANSFORMER STATION	แบบเลขที่ SAI-015/21077 แผ่นที่ 3 ของจำนวน 3 แผ่น