* ให้ดัดโค้งสายขึ้น เพื่อป้องกันน้ำฝนไหลย้อนเข้าจุดที่ต่อปลายสาย

การประกอบเลขที่
ASSEMBLY NO. **0539**

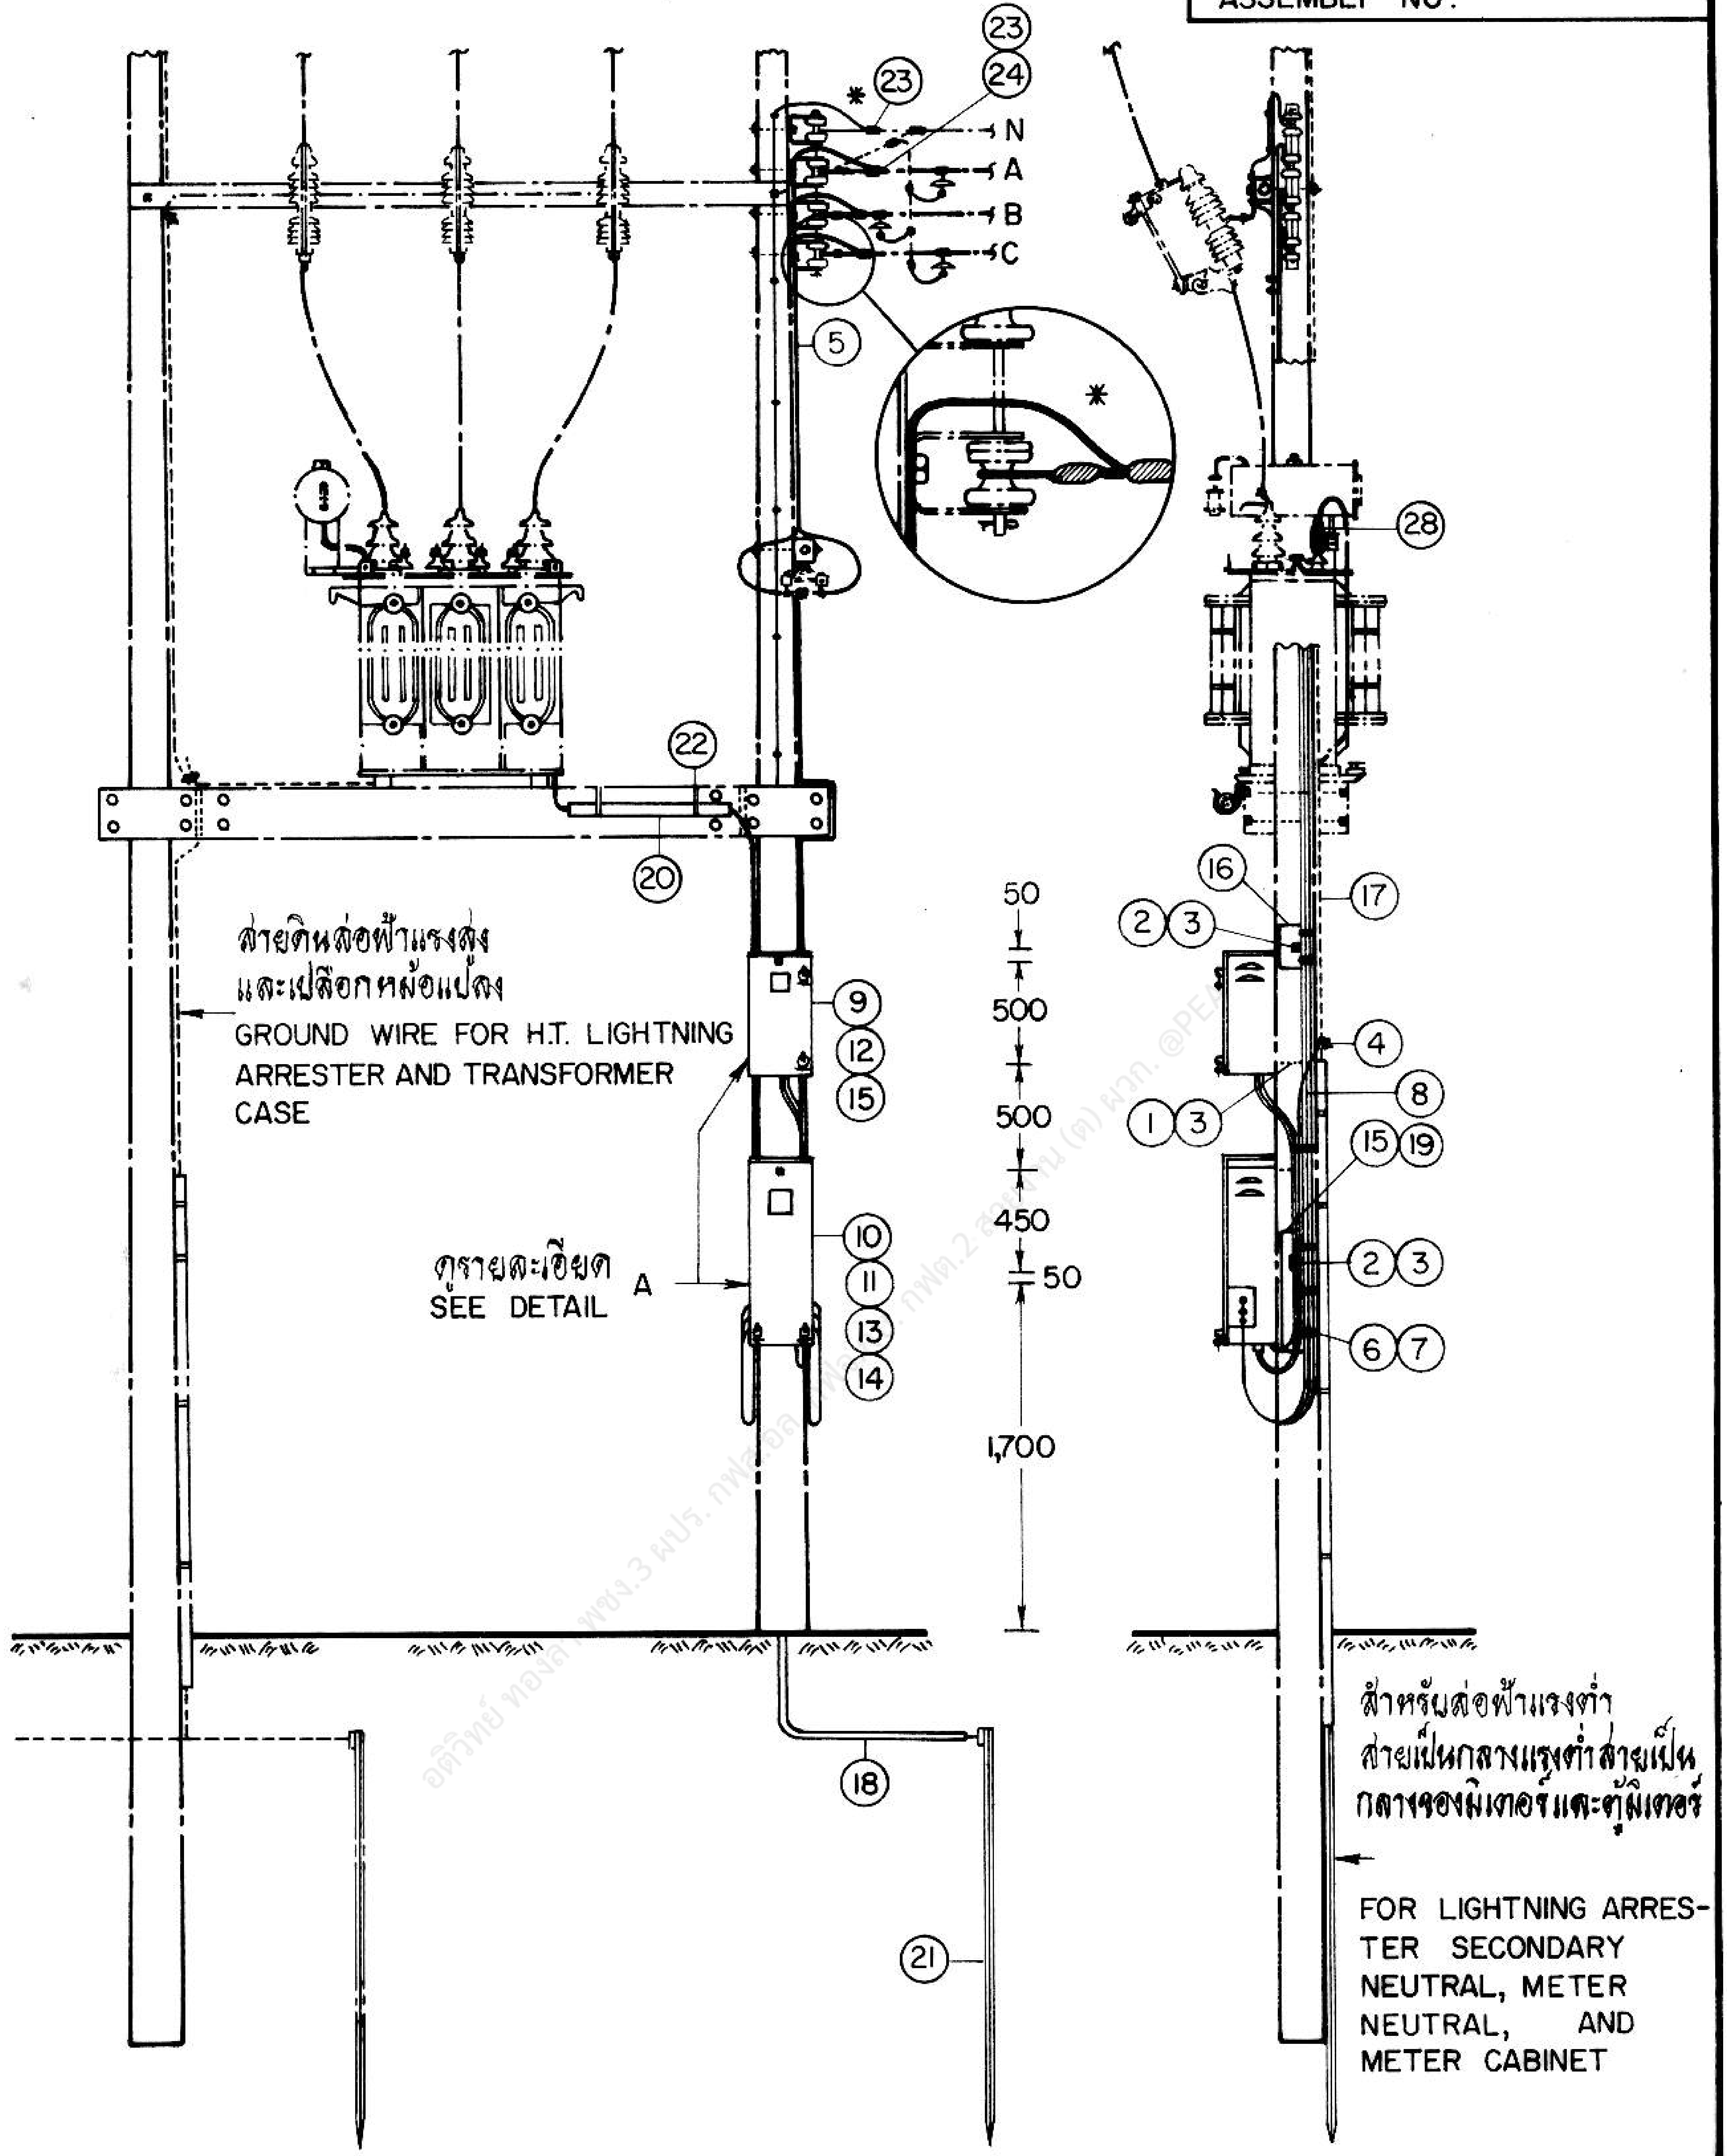

㉓
*
㉓
㉔
N
A
B
C
⑤
*
㉘
㉒
⑳
⑯
⑰
② ③
④
① ③
⑧
⑮ ⑲
② ③
⑥ ⑦
⑨
⑫
⑮
⑩
⑪
⑬
⑭
50
500
500
450
50
1,700
สายดินล่อฟ้าแรงสูง
และเปลือกหม้อแปลง
GROUND WIRE FOR H.T. LIGHTNING ARRESTER AND TRANSFORMER CASE
ดูรายละเอียด A
SEE DETAIL
⑱
㉑
สำหรับล่อฟ้าแรงต่ำ
สายเป็นกลางแรงต่ำสายเป็นกลางของมิเตอร์และตู้มิเตอร์
FOR LIGHTNING ARRESTER SECONDARY NEUTRAL, METER NEUTRAL, AND METER CABINET

กองวิศวกรรมไฟฟ้าและเครื่องกล
ฝ่ายวิศวกรรม

ผู้เขียน ....
ผู้สำรวจ ....
วิศวกร ลิตพงษ์
หัวหน้าแผนก ....
ผู้อำนวยการกอง ....
ผู้อำนวยการฝ่าย ....

รองผู้ว่าการฝ่ายเทคนิค

การไฟฟ้าส่วนภูมิภาค

ผู้ว่าการ ....

8 ต.ค. 2528

การติดตั้งมิเตอร์ 3 เฟส 4 สาย ประกอบซี.ที. แรงต่ำ
กรณีติดตั้งกิโลวัตต์ - ชั่วโมงมิเตอร์ ร่วมกับกิโลวาร์ - ชั่วโมงมิเตอร์
I ที่เสาต้นหิ้งร้านหม้อแปลง

INSTALLATION OF 3-Ø, 4-W METER WITH L.T. - C.T.
kWh AND kVarh METERS COMBINATION
I AT TRANSFORMER STATION

ใช้แทนแบบ ....
ถูกแทนโดยแบบ ....
เขียนเสร็จวันที่ 16 ส.ค. 28
แก้แบบวันที่ 8 ก.ค. 31
มิติเป็น มม.
มาตราส่วน 1 : 50

แบบเลขที่ SAI-015/28019
แผ่นที่ 1 ของจำนวน 6 แผ่น

-8 ต.ค. 2528

การประกอบเลขที่
ASSEMBLY NO. 0539

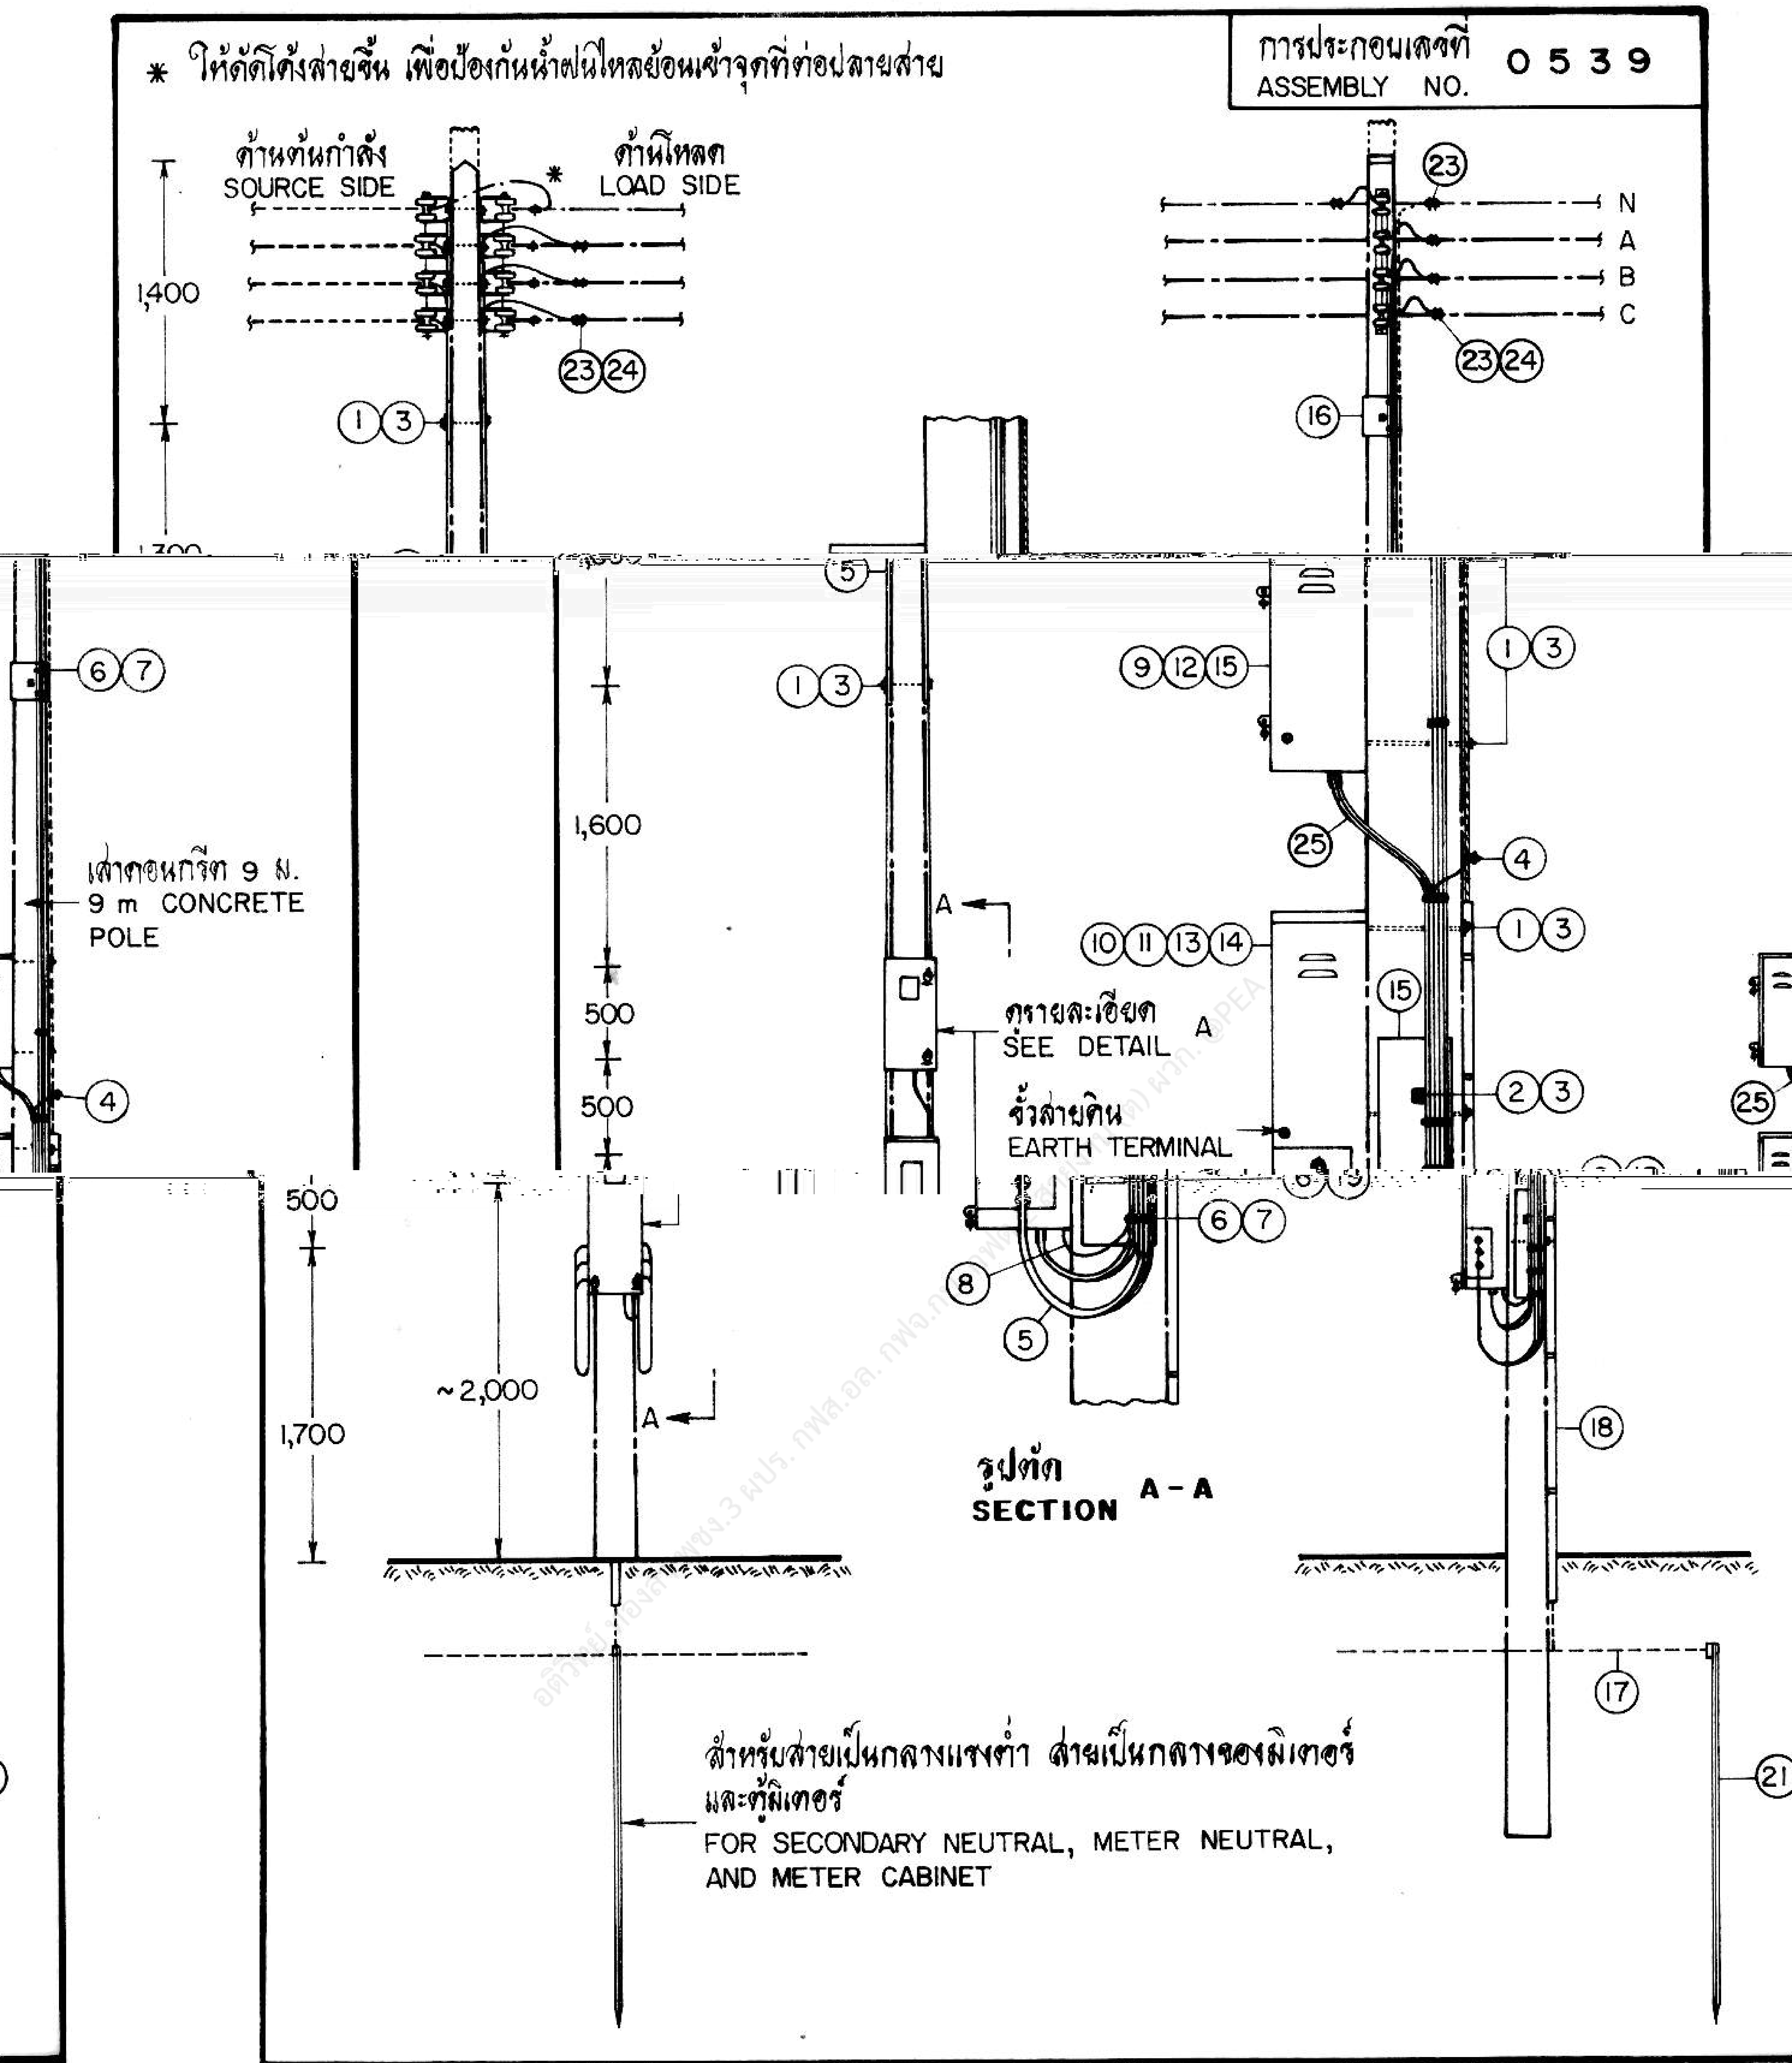

28
31
19
แผ่น

กองวิศวกรรมไฟฟ้า และเครื่องกล
ฝ่ายวิศวกรรม

ผู้เขียน ....
ผู้สำรวจ ....
วิศวกร ....
หัวหน้าแผนก ....
ผู้อำนวยการกอง ....
ผู้อำนวยการฝ่าย ....

รองผู้ว่าการฝ่ายเทคนิค ....

การไฟฟ้าส่วนภูมิภาค

ผู้ว่าการ ....

8 ก.ค. 2528

การติดตั้งมิเตอร์ 3 เฟส 4 สาย ประกอบซีที. แรงต่ำ
กรณีติดตั้งกิโลวัตต์-ชั่วโมงมิเตอร์ ร่วมกับกิโลวาร์-ชั่วโมงมิเตอร์
II ที่เสาระบบจำหน่ายแรงต่ำ

INSTALLATION OF 3-Ø, 4-W METER WITH L.T. – C.T.
kWh AND kVarh METERS COMBINATION
II AT L.T. DISTRIBUTION POLE

ใช้แทนแบบ ....
ถูกแทนโดยแบบ ....
เขียนเสร็จวันที่ 16 ส.ค. 2
แก้แบบวันที่ 8 ก.ค. 3
มิติเป็น มม.
มาตราส่วน 1 : 50
แบบเลขที่ SAI-015/280
แผ่นที่ 2 ของจำนวน 6

- ๕ ต.ค. 2528

* ทำความสะอาดสาย และทาคอมเปาด์ช่วยสัมผัสทางไฟฟ้าก่อนต่อสาย และพันหุ้มจุดต่อด้วย PVC เทป

การประกอบเลขที่ ASSEMBLY NO. 0539

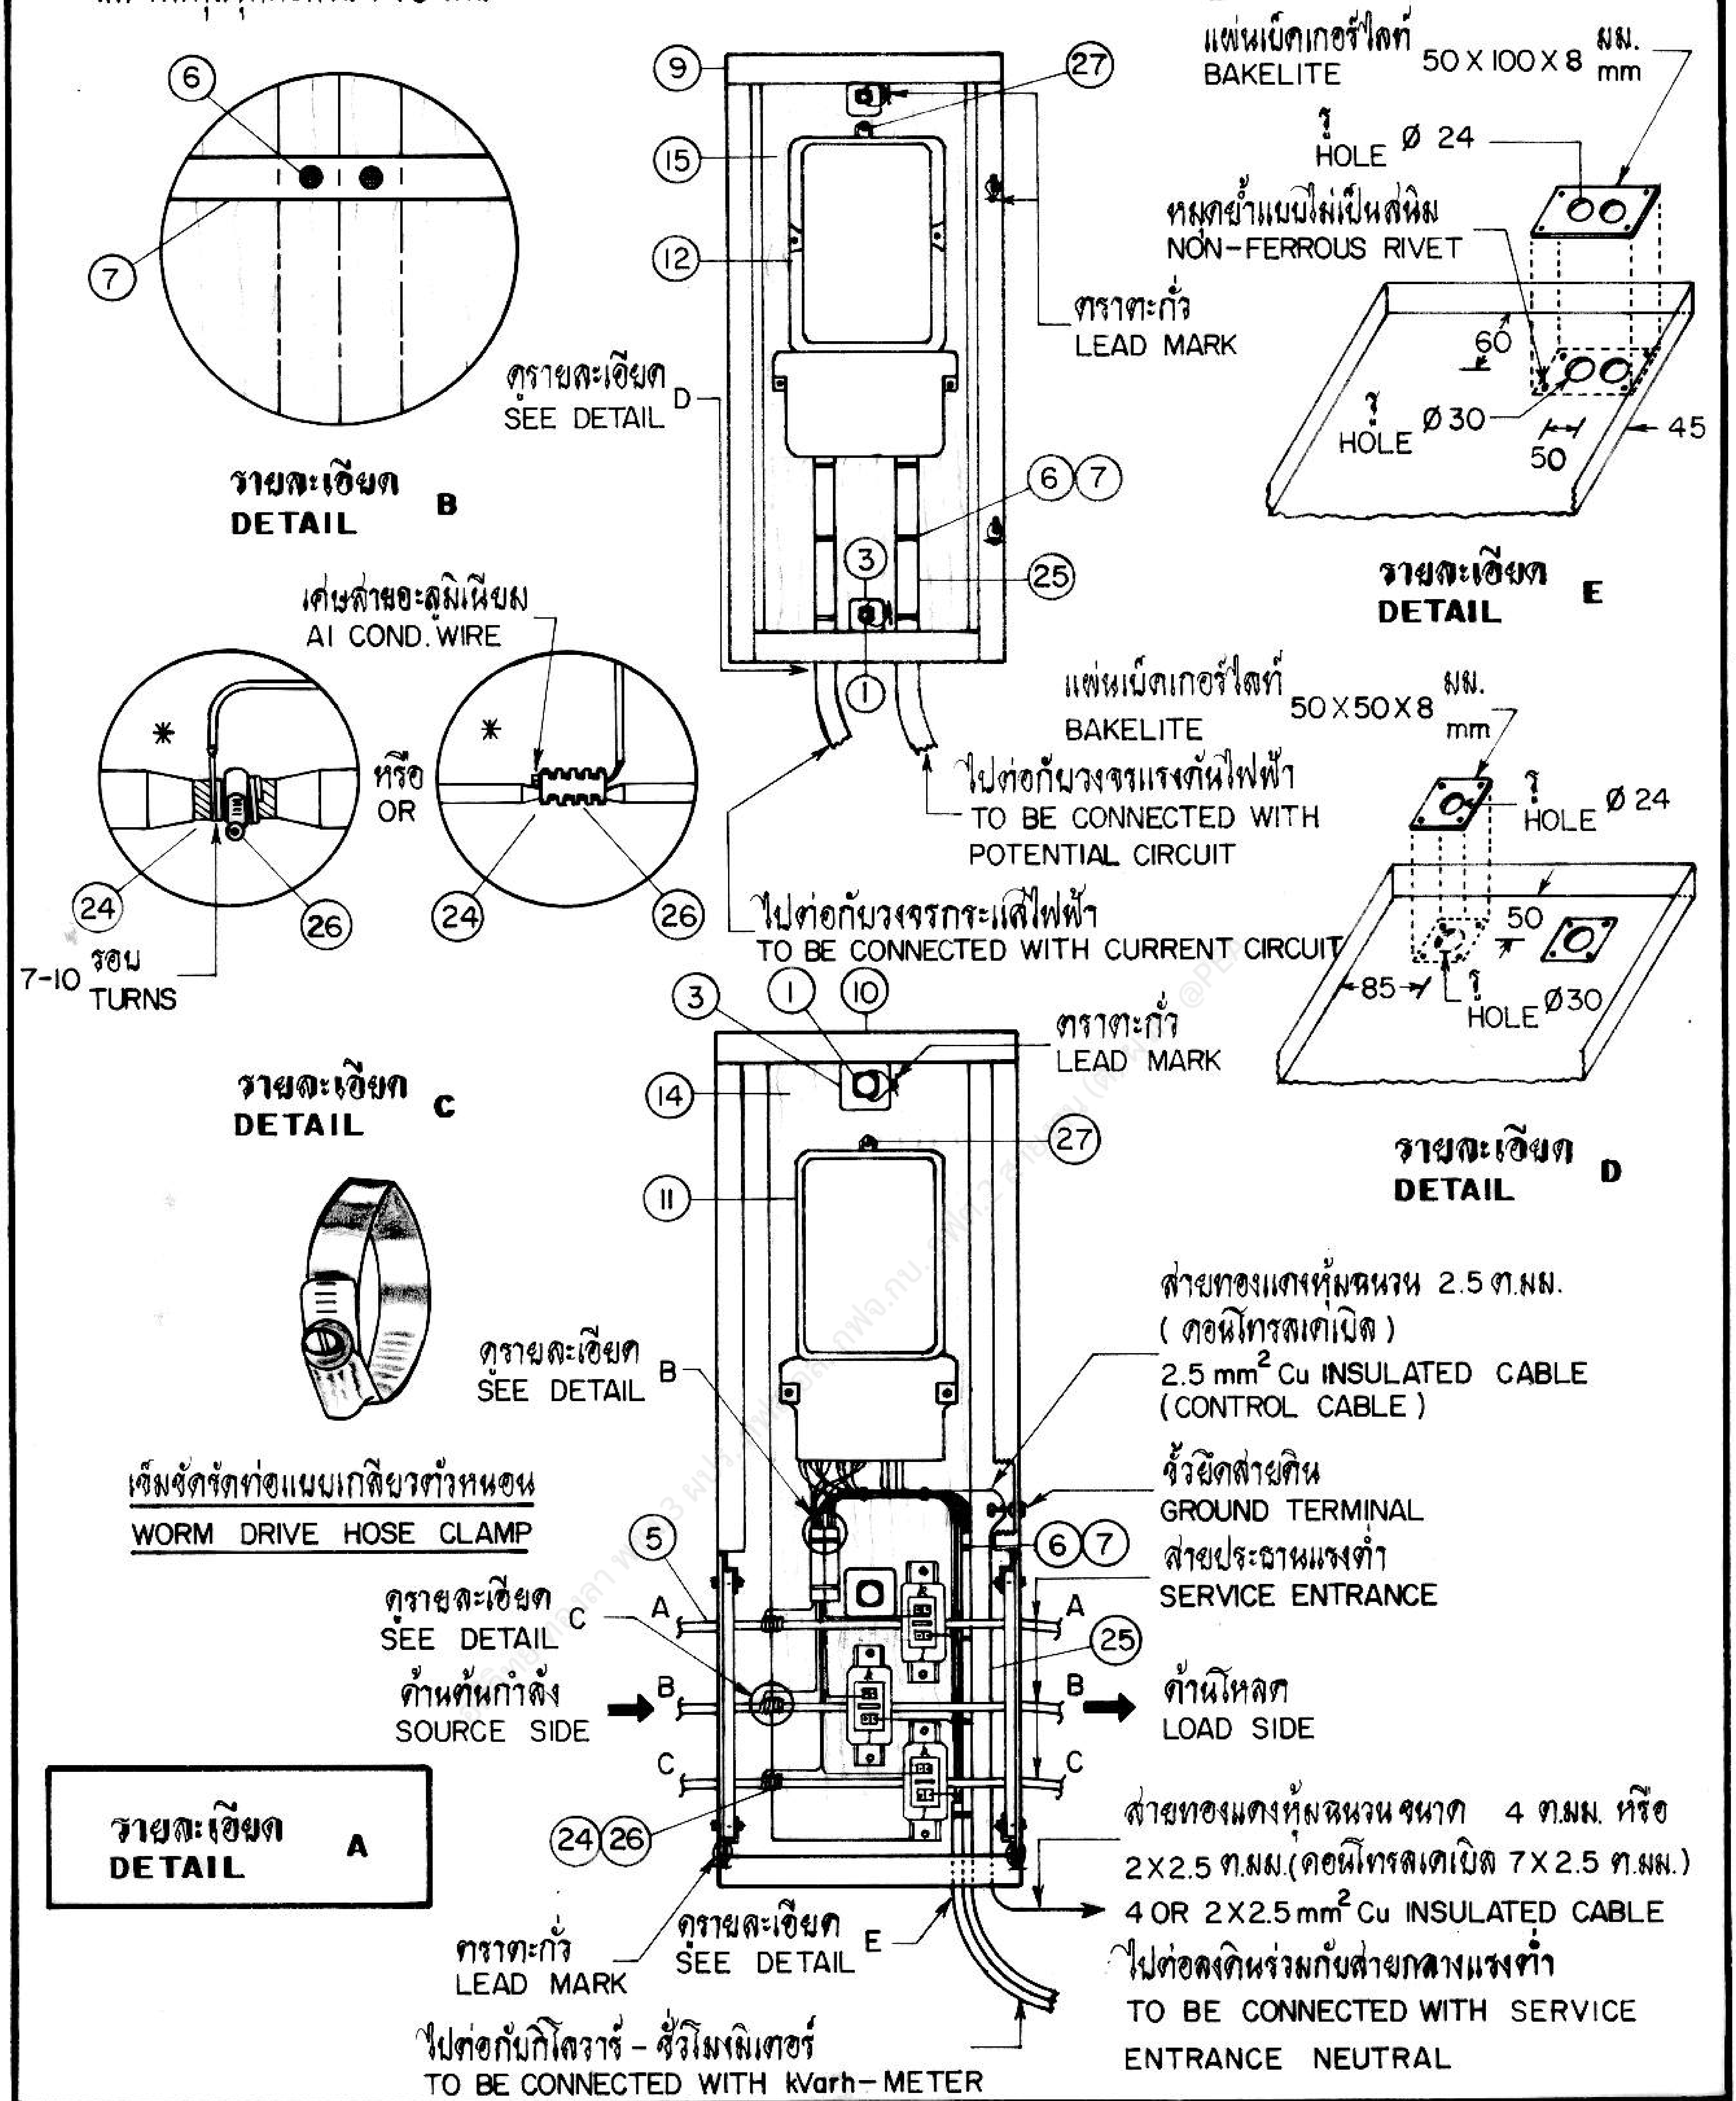
6
7
รายละเอียด DETAIL B
9
27
15
12
ตราตะกั่ว LEAD MARK
ดูรายละเอียด SEE DETAIL D
6 7
3
25
1
แผ่นเบ็คเกอร์ไลท์ BAKELITE 50 X 100 X 8 มม. mm
รู HOLE Ø 24
หมุดย้ำแบบไม่เป็นสนิม NON-FERROUS RIVET
60
รู HOLE Ø 30
50
45
รายละเอียด DETAIL E
เส้นสายอะลูมิเนียม AI COND. WIRE
*
หรือ OR
24
26
7-10 รอบ TURNS
รายละเอียด DETAIL C
แผ่นเบ็คเกอร์ไลท์ BAKELITE 50X50X8 มม. mm
รู HOLE Ø 24
ไปต่อกับวงจรแรงดันไฟฟ้า TO BE CONNECTED WITH POTENTIAL CIRCUIT
ไปต่อกับวงจรกระแสไฟฟ้า TO BE CONNECTED WITH CURRENT CIRCUIT
50
85
รู HOLE Ø30
รายละเอียด DETAIL D
3
1
10
ตราตะกั่ว LEAD MARK
14
27
11
เข็มขัดรัดท่อแบบเกลียวตัวหนอน WORM DRIVE HOSE CLAMP
ดูรายละเอียด SEE DETAIL B
สายทองแดงหุ้มฉนวน 2.5 ต.มม. (คอนโทรลเคเบิ้ล) 2.5 mm² Cu INSULATED CABLE (CONTROL CABLE)
ขั้วยึดสายดิน GROUND TERMINAL
6 7
สายประธานแรงต่ำ SERVICE ENTRANCE
5
ดูรายละเอียด SEE DETAIL C
A
ด้านต้นกำลัง SOURCE SIDE
B
C
25
A
B
C
ด้านโหลด LOAD SIDE
24 26
รายละเอียด DETAIL A
ตราตะกั่ว LEAD MARK
ดูรายละเอียด SEE DETAIL E
สายทองแดงหุ้มฉนวนขนาด 4 ต.มม. หรือ 2X2.5 ต.มม. (คอนโทรลเคเบิ้ล 7X2.5 ต.มม.) 4 OR 2X2.5 mm² Cu INSULATED CABLE
ไปต่อลงดินร่วมกับสายกลางแรงต่ำ TO BE CONNECTED WITH SERVICE ENTRANCE NEUTRAL
ไปต่อกับกิโลวาร์-ชั่วโมงมิเตอร์ TO BE CONNECTED WITH kVarh-METER

กองวิศวกรรมไฟฟ้าและเครื่องกล
ฝ่ายวิศวกรรม

ผู้เขียน
ผู้สำรวจ
วิศวกร
หัวหน้าแผนก
ผู้อำนวยการกอง
ผู้อำนวยการฝ่าย
รองผู้ว่าการฝ่ายเทคนิค

การไฟฟ้าส่วนภูมิภาค

ผู้ว่าการ

8 ต.ค. 2528

การติดตั้งมิเตอร์ 3 เฟส 4 สาย ประกอบซีที. แรงต่ำ
กรณีติดตั้งกิโลวัตต์-ชั่วโมงมิเตอร์ ร่วมกับกิโลวาร์-ชั่วโมงมิเตอร์

INSTALLATION OF 3-Ø, 4-W METER WITH L.T. - CT.
kWh AND kVarh METERS COMBINATION

ใช้แทนแบบ
ถูกแทนโดยแบบ
เขียนเสร็จวันที่ 16 ส.ค. 28
แก้แบบวันที่ 8 ก.ค. 31
มิติเป็น มม.
มาตราส่วน
แบบเลขที่ SAI-015/28019
แผ่นที่ 3 จากจำนวน 6 แผ่น

-8 ต.ค. 2528

105

การประกอบเลขที่ **0539**
ASSEMBLY NO.

บัญชีวัสดุ
BILL OF MATERIAL

ลำดับที่ ITEM	รายละเอียด DESCRIPTION	จำนวน REQ'D I	 II	วัสดุเลขที่ MAT. NO.
1	สลักเกลียว M 16 X 250 มม. BOLT, MACHINE, M 16 X 250 mm	–	6	01110203
	สลักเกลียว M 16 X 300 มม. สำหรับเสาคอนกรีต 12 ม. BOLT, MACHINE, M 16 X 300 mm FOR 12 m CONCRETE POLE	4	6	01110204
2	สลักเกลียว M 16 X 250 มม. BOLT, MACHINE, M 16 X 250 mm	–	1	01110203
	สลักเกลียว M 16 X 350 มม. สำหรับเสาคอนกรีต 12 ม. BOLT, MACHINE, M 16 X 350 mm FOR 12 m CONCRETE POLE	2	1	01110205
3	แหวนสี่เหลี่ยมแบน 52 X 52 X 4.5 มม. รู Ø 18 มม. มอก. 258 WASHER, SQUARE, FLAT 52 X 52 X 4.5 mm HOLE Ø 18 mm TIS 258	12	14	01180100
4	ยูแคล้มป์ สลักเดี่ยว M 8 CLAMP, SINGLE U-BOLT, M 8	1	1	01230000
5	สายอะลูมิเนียม หรือทองแดงหุ้ม PVC 750 โวลต์ ขนาดตามต้องการ CABLE, Al OR Cu, PVC INSULATED, 750 V, SIZE AS REQUIRED	55 ม. m	35 ม. m	02070002-8
6	ตะปูหัวกลมแบน ยาว 15-20 มม. Ø 1.00 มม. มอก. 113 NAIL, ROUND MILD STEEL WIRE 15-20 mm LONG Ø 1.00 mm TIS 113	37	45	
7	เข็มขัดรัดสาย (ทำด้วยลวดอะลูมิเนียมแบน 1 X 10 มม.) ช่วงระยะ 50 ซม. CABLE STRAP (MADE OF ARMOUR TAPE 1 X 10 mm) AT 50 cm INTERVAL	กก. kg	กก. kg	02200000
8	สายทองแดงหุ้มฉนวนใช้ภายนอก ขนาด 4 ต.มม. หรือ 2 X 2.5 ต.มม. (คอนโทรลเคเบิล) CONDUCTOR, INSULATED, WEATHER-PROOF Cu 4 mm^2 OR 2 X 2.5 mm^2 (CONTROL CABLE)	ม. m	ม. m	
9	ตู้สำหรับดีมานด์มิเตอร์ CABINET, ALUMINIUM, FOR DEMAND METER	1	1	06100007
10	ตู้สำหรับมิเตอร์ พร้อมซีที. แรงต่ำ CABINET, STEEL, FOR WATTHOUR METER WITH L.T.-CURRENT TRANSFORMER	1	1	06100008
11	กิโลวัตต์ - ชั่วโมงมิเตอร์ ชนิดดีมานด์สะสม 3 เฟส 4 สาย 380/220 โวลต์ 5 แอมป์ kWh-METER, CUMULATIVE DEMAND, 3-PHASE, 4-WIRE, 380/220 V, 5 A	1	1	06000301
12	กิโลวาร์ - ชั่วโมงมิเตอร์ ชนิดดีมานด์สะสม 3 เฟส 4 สาย 380/220 โวลต์ 5 แอมป์ kVarh-METER, CUMULATIVE DEMAND, 3-PHASE, 4-WIRE, 380/220 V, 5 A	1	1	06000401
13	ซีที. แรงต่ำ 500 โวลต์ เรโชตามต้องการ คลาส 0.5, 5VA TRANSFORMER, CURRENT, L.T. 500 V RATIO AS REQUIRED CLASS 0.5, 5 VA	3	3	06030000-5
14	แป้นไม้รองรับมิเตอร์ ไสแล้ว ขนาด 80 X 20 X 2 ซม. METER PLATE (HARD WOOD) SURFACE FINISHED, SIZE 80 X 20 X 2 cm	1	1	
15	แป้นไม้รองรับมิเตอร์ ไสแล้ว ขนาด 60 X 20 X 2 ซม. METER PLATE (HARD WOOD) SURFACE FINISHED, SIZE 60 X 20 X 2 cm	3	3	
16	แป้นไม้ยึดสายไฟฟ้า ไสแล้ว ขนาด 20 X 20 X 2 ซม. CABLE PLATE (HARD WOOD) SURFACE FINISHED, SIZE 20 X 20 X 2 cm	2	4	
17	ลวดเหล็กตีเกลียว 50/7 ต.มม. มอก. 404 WIRE, STEEL STRANDED 50/7 mm^2, TIS 404	9 ม. m	17 ม. m	01100004
18	ท่อ พีวีซี. แข็ง ขนาด Ø 20 X 4,000 มม. พร้อมอุปกรณ์ยึด CONDUIT, PVC RIGID, Ø 20 X 4,000 mm WITH FIXING ACCESSORIES	1	1	08040002

กองวิศวกรรมไฟฟ้า และเครื่องกล
ฝ่ายวิศวกรรม

ผู้เขียน
ผู้สำรวจ
วิศวกร
หัวหน้าแผนก
ผู้อำนวยการกอง
ผู้อำนวยการฝ่าย

รองผู้ว่าการฝ่ายเทคนิค

การไฟฟ้าส่วนภูมิภาค

ผู้ว่าการ

8 ต.ค. 2528

การติดตั้งมิเตอร์ 3 เฟส 4 สาย ประกอบซีที. แรงต่ำ
กรณีติดตั้งกิโลวัตต์ - ชั่วโมงมิเตอร์ ร่วมกับกิโลวาร์ - ชั่วโมงมิเตอร์

INSTALLATION OF 3-Ø, 4-W METER WITH L.T. - CT.
kWh AND kVarh METERS COMBINATION

ใช้แทนแบบ
ถูกแทนโดยแบบ
เขียนเสร็จวันที่ 16 ส.ค. 28
แก้แบบวันที่
มิติเป็น
มาตราส่วน
แบบเลขที่ SAI-015/28019
แผ่นที่ 4 ของจำนวน 6 แผ่น

8 ต.ค. 2528

การประกอบเลขที่ ASSEMBLY NO. **0539**

บัญชีวัสดุ
BILL OF MATERIAL

ลำดับที่ ITEM	รายละเอียด DESCRIPTION	จำนวน REQ'D		วัสดุเลขที่ MAT. NO
		I	II	
19	หมายเลขผู้ใช้ไฟ (ดูตัวอย่างข้างล่าง) NUMBER OF CUSTOMER	1	1	
20	ท่อ PVC แข็ง ขนาด Ø 65 X 800 มม. มอก. 216 CONDUIT, PVC RIGID Ø 65 X 800 mm TIS 216	1	–	
21	**หลักดิน** 60 X 60 X 5 มม. ยาว 2 ม. ROD, GROUND 60 X 60 X 5 mm, 2 m LONG	1	1	01220002
22	เหล็กแขวนท่อ PVC (เหล็กแบน 30 X 4 มม. มอก. 55) STEEL BRACKET (FLAT IRON 30 X 4 mm TIS 55)	2	–	05100002
23	พี.จี. คอนเนคเตอร์ หรือ คอนเนคเตอร์ชนิดบีบ แบบ H สำหรับสายอลูมิเนียมหรือทองแดง ขนาดตามต้องการ CONNECTOR, PARALLEL GROOVE OR H-TYPE COMPRESSION, Al OR Cu SIZE AS REQ'D	4	8	02300101-3 02320003
24	PVC เทป กว้าง 19 มม. (ใช้ความยาว 2 ม. ต่อ 1 จุด) มอก. 386 PVC TAPE, 19 mm WIDE (2 m LONG PER POINT) TIS 386			02180001 or 02180002
25	คอนโทรลเคเบิล ขนาด 7 X 2.5 ต.มม. CONTROL CABLE, SIZE 7 X 2.5 mm^2	8 ม. m	8 ม. m	02080402
26	เข็มขัดรัดท่อ แบบเกลียวตัวหนอน ขนาด 1/2" - 1" หรือ คอนเนคเตอร์ชนิดบีบ แบบ H CLAMP, WORM DRIVE HOSE SIZE Ø 1/2" - 1" OR H-TYPE COMPRESSION CONNECTOR	3	3	02210001 02210003
27	ตะปูเกลียวชุบโครเมี่ยม ขนาด 15-20 มม. SCREW, CHROME PLATED, SIZE 15-20 mm	12	12	
28	เทปพันเคเบิลอากาศแรงสูง ขนาด 3/4" X 30' ELECTRICAL SPLICING TAPE, FOR H.T. AERIAL CABLE, SIZE 3/4" X 30'	ม้วน roll	–	02180003

	แบบอ้างอิง REFERENCE DRAWING	แบบเลขที่ DWG. NO.	การประกอบเลขที่ ASSEMBLY NO.
1	**การติดตั้งฟิวส์สวิตช์แรงต่ำบนคอน** คอร. สปัน 100 X 100 X 2,500 มม. L.T. FUSE-SWITCH INSTALL. ON SPUN PRESTRESSED CONCRETE CROSSARM	SAI-015/25004	**0407**
2	แผนผังการต่อมิเตอร์ CONNECTION DIAGRAM OF METER	SAI-015/28017	**0537**
3	ขนาดของสายไฟฟ้าแรงต่ำที่ออกจากหม้อแปลง แผ่นที่ 6 และ 7 THE SIZE OF L.T. CABLE FROM TRANSFORMER, SHEET NO. 6 AND 7	SAI-015/22034	**0601**
	การกำหนดขนาด HRC ฟิวส์ แรงต่ำ สำหรับหม้อแปลง แผ่นที่ 3 และ 4	SOI-015/18006	**0602**

[redacted]

การประกอบเลขที่
ASSEMBLY NO. 0539

หมายเหตุ

1. ตำแหน่งติดตั้งตู้มิเตอร์ เปลี่ยนได้ตามความเหมาะสม
2. แบบนี้ใช้ในกรณีที่ติดตั้งร่วมกับกิโลวาร์-ชั่วโมงมิเตอร์ ผลิตภัณฑ์ของ AEG เท่านั้น

NOTES

1. SUITABLE HEIGHT FOR METER CABINET INSTALLATION.
2. THIS CONSTRUCTION DRAWING ARE ONLY FOR COMBINATION WITH kVarh-METER MANUFACTURED BY AEG.

คำเตือน

ในการติดตั้งตู้ใส่มิเตอร์ ให้ดำเนินการตามมาตรการ และวิธีปฏิบัติเกี่ยวกับการละเมิดสิทธิการใช้ไฟฟ้า โดยการเอียงมิเตอร์ ตามบันทึกที่ มต. 2145 ลว. 31 พ.ค. 2528 (อนุมัติ ผวก. ลว. 28 พ.ค. 2528) ดังนี้

1. การยึดแป้นไม้รองมิเตอร์ และตู้ใส่มิเตอร์ที่เสาไฟฟ้า ให้ยึดด้วยสลักเกลียว และนัท 2 จุด โดยให้นัทของสลักเกลียว อยู่ในตู้
2. ให้เจาะรูร้อยลวดตีตราตะกั่วที่ปลายสลักเกลียว ตามข้อ 1. ทั้ง 2 จุด
3. ให้ร้อยลวดตีตราตะกั่วที่ฝาตู้ใส่มิเตอร์ทั้ง 2 จุด

อดิวิทย์ ทองลา พชง.3 ผปร. กฟส.อล. กฟจ.กน. [illegible] 2 สายงาน [illegible] © PEA

กองวิศวกรรมไฟฟ้า และเครื่องกล ฝ่ายวิศวกรรม	การไฟฟ้าส่วนภูมิภาค	ใช้แทนแบบ ถูกแทนโดยแบบ
ผู้เขียน ผู้สำรวจ วิศวกร หัวหน้าแผนก ผู้อำนวยการกอง ผู้อำนวยการฝ่าย	ผู้ว่าการ 8 ต.ค. 2528 การติดตั้งมิเตอร์ 3 เฟส 4 สาย ประกอบซีที. แรงต่ำ กรณีติดตั้งกิโลวัตต์-ชั่วโมงมิเตอร์ ร่วมกับกิโลวาร์-ชั่วโมงมิเตอร์	เขียนเสร็จวันที่ 16 ส.ค. 28 แก้แบบวันที่ มิติเป็น มาตราส่วน
รองผู้ว่าการฝ่ายเทคนิค	INSTALLATION OF 3-Ø, 4-W METER WITH L.T. - CT. kWh AND kVarh METERS COMBINATION	แบบเลขที่ SA1-015/28019 แผ่นที่ 6 ของจำนวน 6 แผ่น

-8 ต.ค. 2528