

การประกอบเลขที่ ASSEMBLY NO. 52544 A

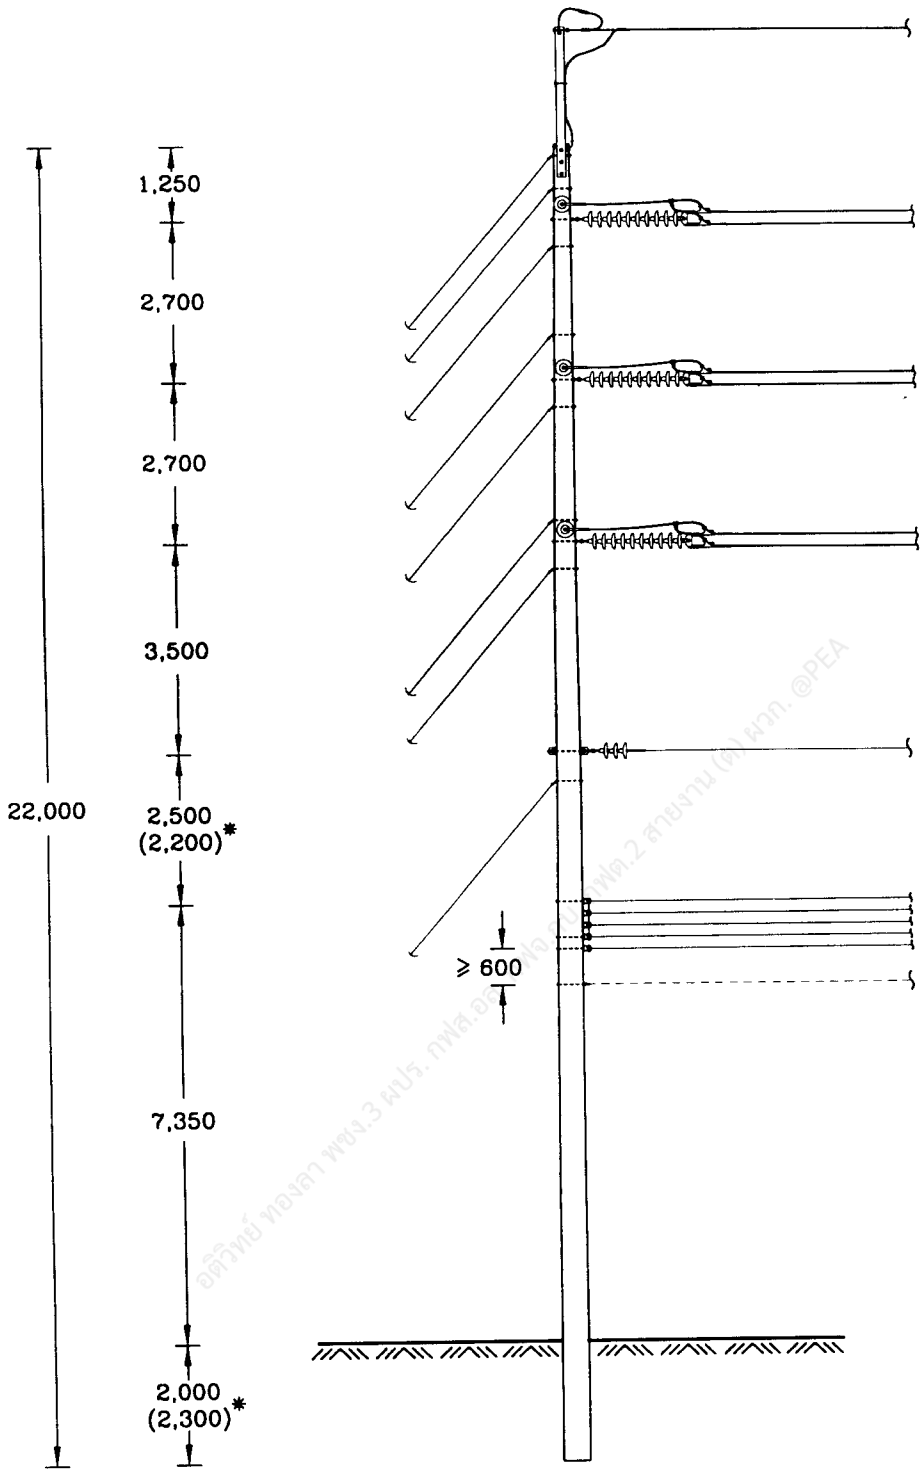

* ดูหมายเหตุ SEE NOTE 1

กองมาตรฐานระบบไฟฟ้า ฝ่ายมาตรฐานและความปลอดภัย	การไฟฟ้าส่วนภูมิภาค	ใช้แทนแบบ ..... ถูกแทนโดยแบบ ..... เขียนเสร็จวันที่ 2 มิ.ย. 2547
ผู้เขียน สมชาย ..... ผู้สำรวจ ..... วิศวกร ..... หัวหน้าแผนก ..... ผู้อำนวยการกอง ..... ผู้อำนวยการฝ่าย	ผู้ว่าการ ..... 115 kV วงจรเดี่ยว สายไฟฟ้า 3 เฟส เสาเดี่ยว (ชนิดมีกราวด์เพลทในเสา) สำหรับทางโค้ง 90° แบบ SD-LA-1	แก้แบบวันที่ ..... มิติเป็น มิลลิเมตร มาตราส่วน 1:125
รองผู้ว่าการฝ่ายวางแผนและพัฒนาระบบไฟฟ้า	115 kV SINGLE CIRCUIT DOUBLE CONDUCTOR SINGLE POLE (WITH GROUND PLATE IN POLE), 90° ANGLE STRUCTURE TYPE SD-LA-1	แบบเลขที่ SA1-015/47011 แผ่นที่ 1 ของจำนวน 3 แผ่น

การประกอบเลขที่ ASSEMBLY NO. 5 2 5 4 A

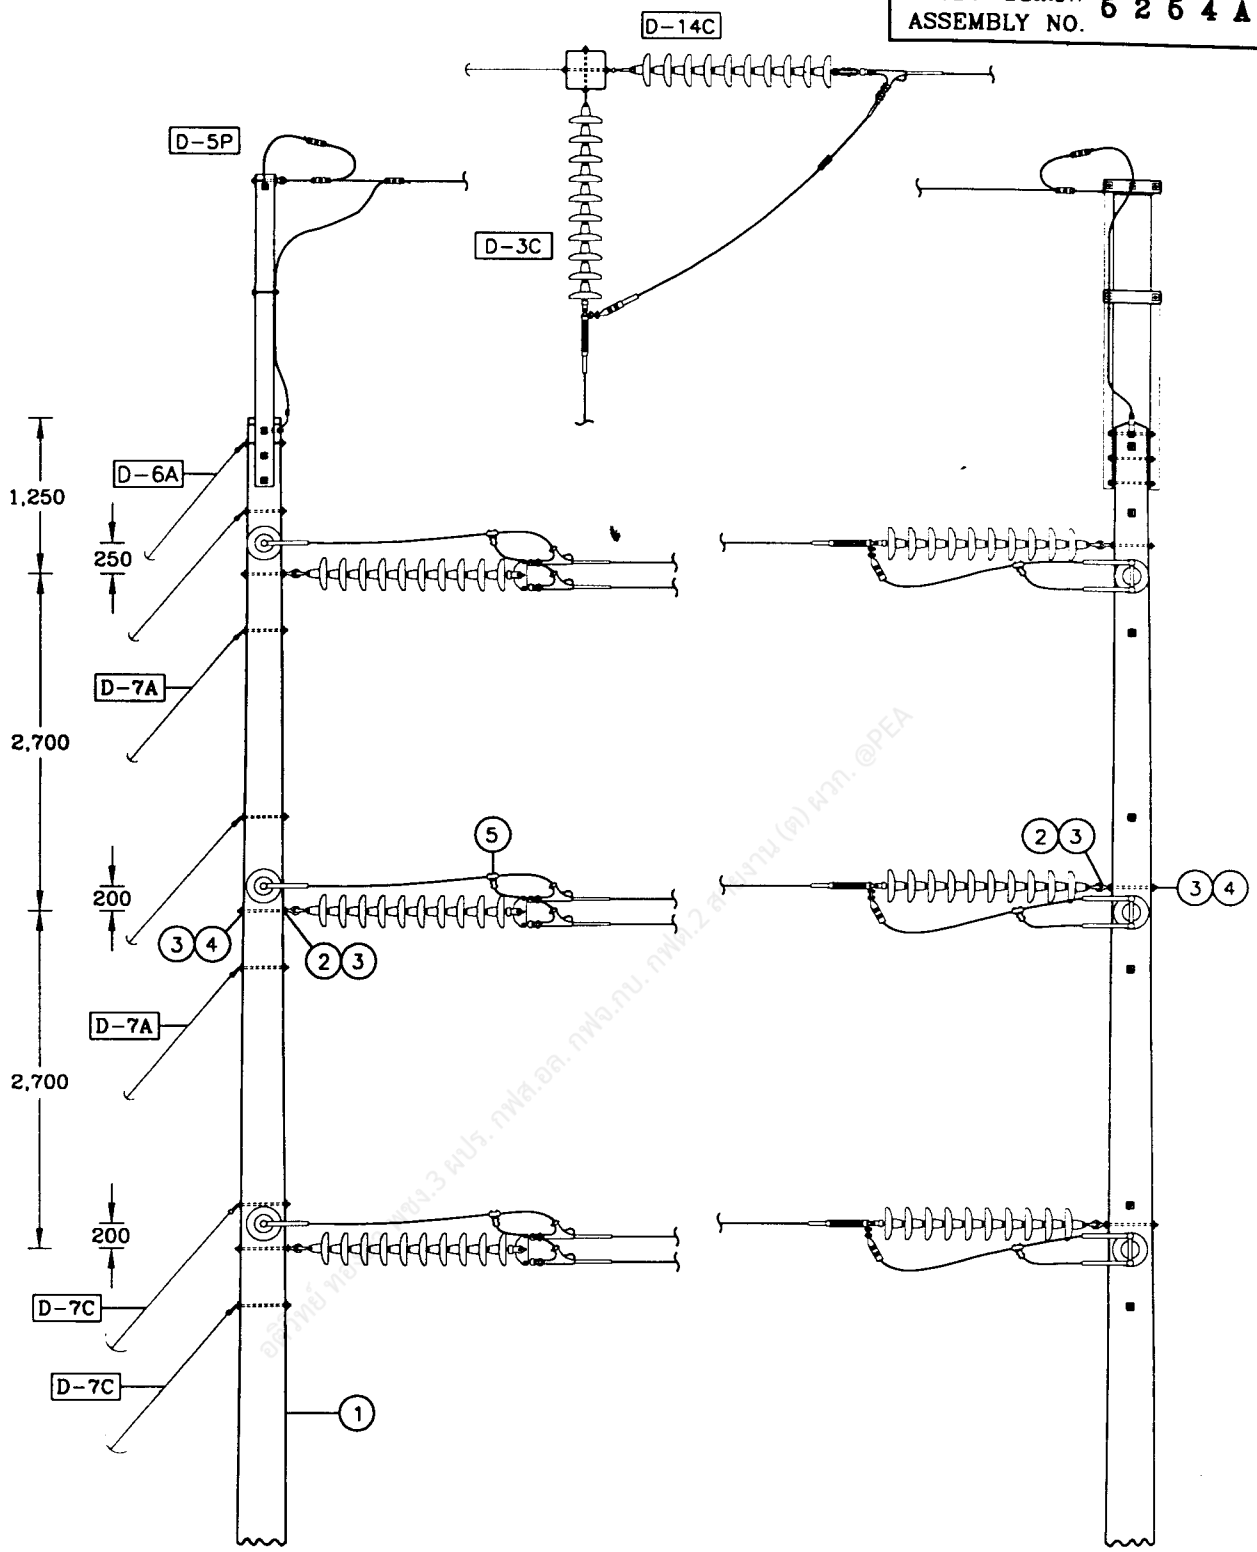

กองมาตรฐานระบบไฟฟ้า ฝ่ายมาตรฐานและความปลอดภัย	การไฟฟ้าส่วนภูมิภาค	ใช้แทนแบบ ..... ถูกแทนโดยแบบ .....
ผู้เขียน ...สมชาย..... ผู้สำรวจ ..... วิศวกร ..... หัวหน้าแผนก ..... ผู้อำนวยการกอง ..... ผู้อำนวยการฝ่าย	ผู้ว่าการ	เขียนเสร็จวันที่ 2 มิ.ย. 2547 แก้แบบวันที่ ..... มิติเป็น ..มิลลิเมตร..... มาตราส่วน ..1:60.....
รองผู้ว่าการฝ่ายวางแผนและพัฒนาระบบไฟฟ้า	115 kV วงจรเดี่ยว สายไฟฟ้า 27 ก.ค. 2547 เสาเดี่ยว (ชนิดมีกราวด์เพลทในเสา) สำหรับทางโค้ง 90° แบบ SD-LA-1	
	115 kV SINGLE CIRCUIT DOUBLE CONDUCTOR SINGLE POLE (WITH GROUND PLATE IN POLE), 90° ANGLE STRUCTURE TYPE SD-LA-1	แบบเลขที่ SA1-015/47011 แผ่นที่ 2 ของจำนวน 3 แผ่น

27 ก.ค. 2547

การประกอบเลขที่ ASSEMBLY NO. 5254A

บัญชีวัสดุ
BILL OF MATERIAL

ลำดับที่ ITEM	รายละเอียด DESCRIPTION	จำนวน REQ.D	วัสดุเลขที่ MAT. NO.
1	เสา คอร. ยาว 22.00 ม. ชนิดมีกราวด์เพลทในเสา POLE, CONCRETE, 22.00 m LONG, WITH GROUND PLATE IN POLE	1	00010015
2	สลักหวงโอแวล M 20x350 มม. BOLT, OVAL EYE, M 20x350 mm	6	01150100
3	แหวนสี่เหลี่ยมแบน 62x62x6 มม. รู ø22 มม. มอก.258 WASHER, SQUARE, FLAT, 62x62x6 mm, HOLE ø22 mm, TIS 258	12	01180101
4	แหวนสปริง M 20 มอก. 259 WASHER, LOCK, M 20, TIS 259	6	01180302
5	คอนเนคเตอร์แบบที สำหรับอะลูมิเนียมสายเมน 400 ต.มม. สายแยก 400 ต.มม. CONNECTOR, T-TYPE, FOR AL, MAIN 400 mm^2, TAP OFF 400 mm^2	3	02500006
	รายละเอียด DETAIL		
D-3C	การประกอบลูกถ้วยแขวน SUSPENSION INSULATOR ASSEMBLY	3	
D-14C	การประกอบลูกถ้วยแขวน SUSPENSION INSULATOR ASSEMBLY	3	
D-5P**	การประกอบสายลอฟ้า OVERHEAD GROUND WIRE ASSEMBLY	1	
D-6A	การประกอบสายยึดโยงลวดเหล็กตีเกลียว 50 ต.มม. STEEL STRANDED WIRE 50 mm^2 GUY ASSEMBLY	1	
D-7A	การประกอบสายยึดโยงลวดเหล็กตีเกลียว 95 ต.มม. STEEL STRANDED WIRE 95 mm^2 GUY ASSEMBLY	4	
D-7C	การประกอบสายยึดโยงลวดเหล็กตีเกลียว 95 ต.มม. STEEL STRANDED WIRE 95 mm^2 GUY ASSEMBLY	2	
D-9A	สมอบกคอนกรีต CONCRETE ANCHOR	1	
D-10A	ฐานรากเสา POLE FOUNDATION	1	
D-25	การต่อลงดิน GROUNDING	1	

หมายเหตุ

1.* กรณีก่อสร้างในพื้นที่เขตทางหลวง ให้ใช้ค่าระยะห่างตามแนวดิ่งในวงเล็บ โดยดูรายละเอียดเพิ่มเติมในแบบเลขที่ SA1-015/43012 (การประกอบเลขที่ 5687)

2.** กรณีไม่มีสายยึดโยง ให้ใช้การประกอบสายลอฟ้า แบบ D-5Q แทน

3. ระยะห่างระหว่างช่วงเสาของโครงสร้างสายส่ง 115 kV โครงสร้างเสาสำหรับทางโค้ง 90° ให้ดูแบบเลขที่ SA1-015/47009 (การประกอบเลขที่ 5161)

NOTES

1.* IN CASE OF CONSTRUCTION IN HIGHWAY AREA, USE A VERTICAL CLEARANCE VALUE IN THE PARENTHESIS, FOR ADDITIONAL DETAIL, SEE DWG NO. SA1-015/43012 (ASSEMBLY NO. 5687) .

2.** IN CASE OF NO GUY, USE OVERHEAD GROUND WIRE ASSEMBLY TYPE D-5Q .

3. SPAN LENGTHS FOR 115 kV CONSTRUCTION STRUCTURE, 90° ANGLE STRUCTURE, SEE DWG. NO. SA1-015/47009 (ASSEMBLY NO. 5161) .

กองมาตรฐานระบบไฟฟ้า
ฝ่ายมาตรฐานและความปลอดภัย

ผู้เขียน ...สมชาย.....
ผู้สำรวจ.....
วิศวกร.....
หัวหน้าแผนก.....
ผู้อำนวยการกอง.....
ผู้อำนวยการฝ่าย.....

รองผู้ว่าการฝ่ายวางแผนและพัฒนาระบบไฟฟ้า
.....

การไฟฟ้าส่วนภูมิภาค

ผู้ว่าการ.....

27 ส.ค. 2547

115 kV วงจรเดี่ยว สายไฟฟ้า
เสาเดี่ยว (ชนิดมีกราวด์เพลทในเสา) สำหรับทางโค้ง 90°
แบบ SD-LA-1

115 kV SINGLE CIRCUIT DOUBLE CONDUCTOR
SINGLE POLE (WITH GROUND PLATE IN POLE), 90° ANGLE STRUCTURE
TYPE SD-LA-1

ใช้แทนแบบ .....
ถูกแทนโดยแบบ .....
เขียนเสร็จวันที่ 2 มิ.ย. 2547
แก้แบบวันที่ .....
มิติเป็น.....
มาตราส่วน.....

แบบเลขที่ SA1-015/47011
แผนที่ 3 ของจำนวน 3 แผ่น

27 ส.ค. 2547