การประกอบเลขที่
ASSEMBLY NO. 5687 G

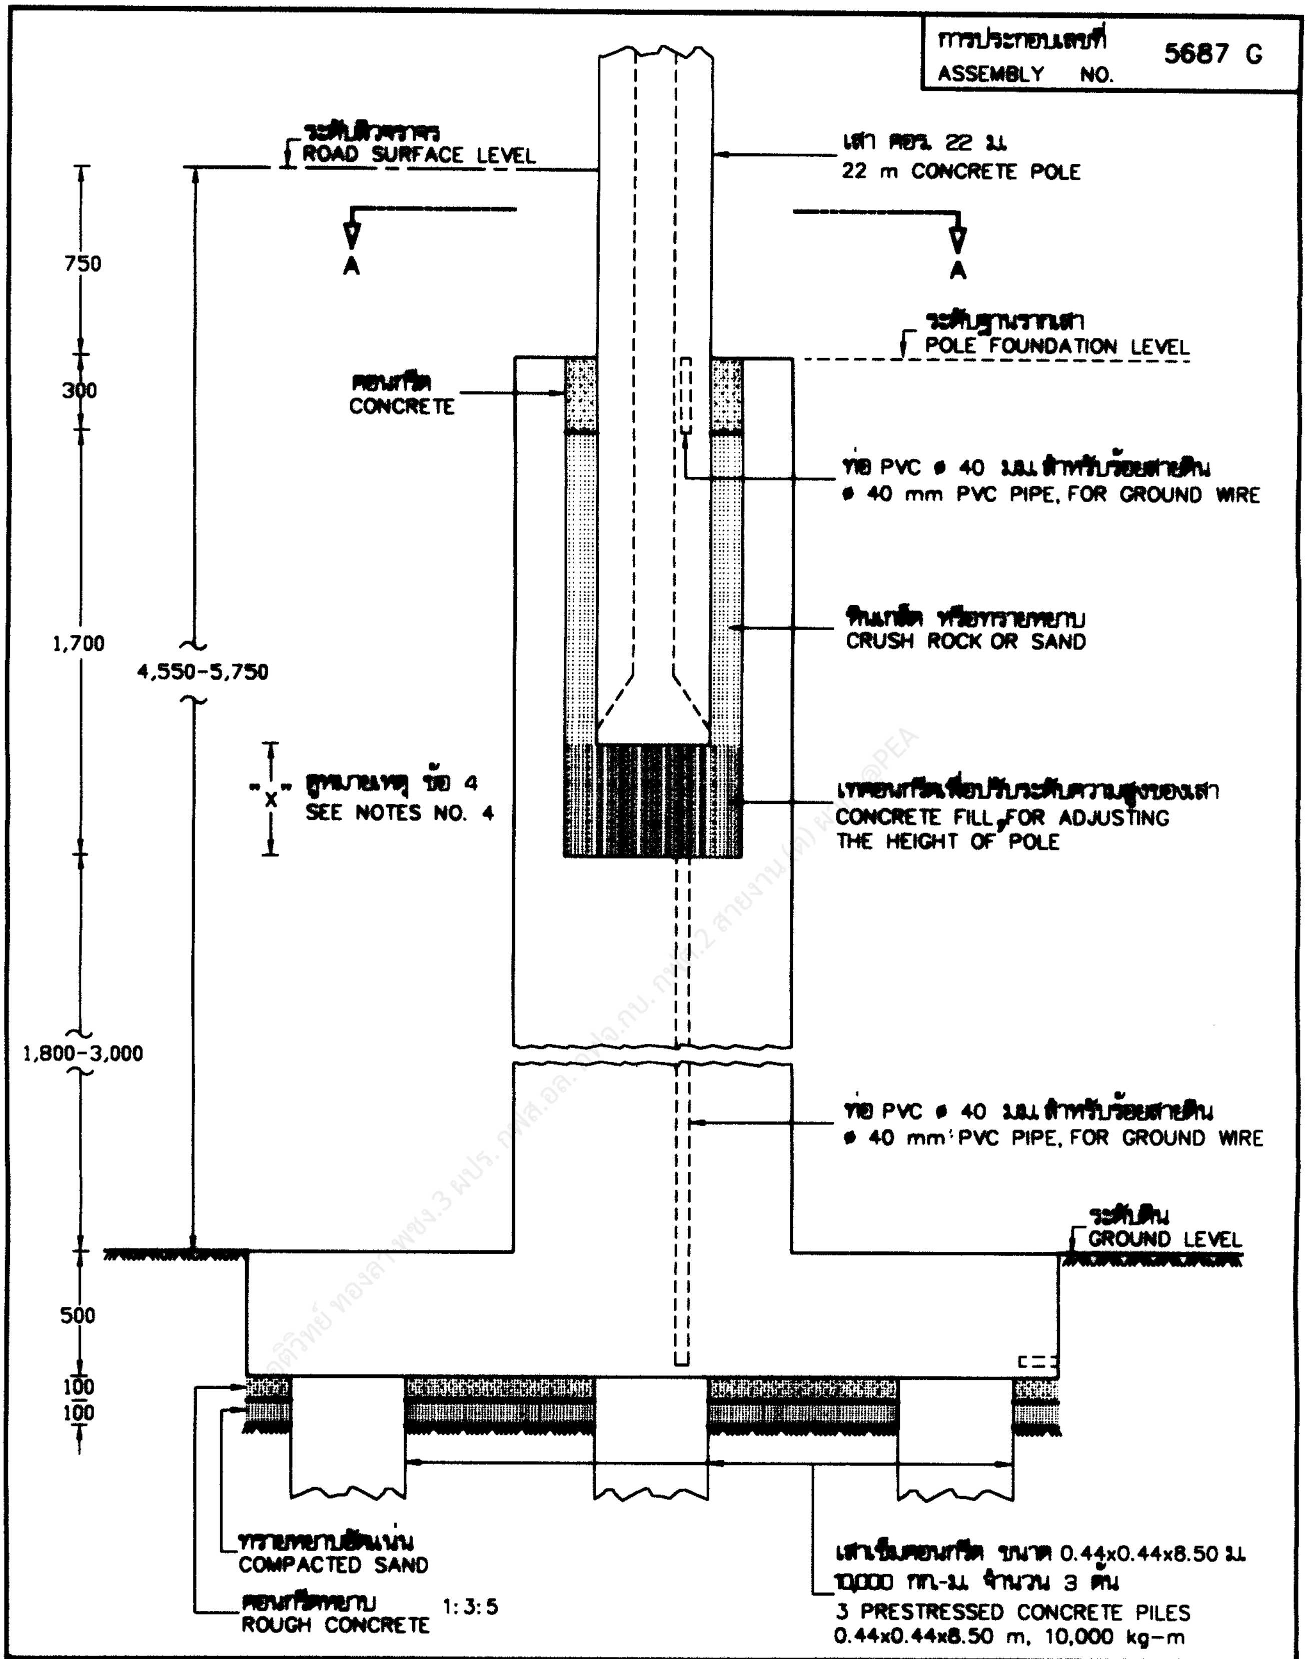
ระดับผิวจราจร
ROAD SURFACE LEVEL
เสา คอร. 22 ม.
22 m CONCRETE POLE
A
A
ระดับฐานรากเสา
POLE FOUNDATION LEVEL
คอนกรีต
CONCRETE
ท่อ PVC ⌀ 40 มม. สำหรับร้อยสายดิน
⌀ 40 mm PVC PIPE, FOR GROUND WIRE
หินเกล็ด หรือทรายหยาบ
CRUSH ROCK OR SAND
750
300
1,700
4,550-5,750
"X"
ดูหมายเหตุ ข้อ 4
SEE NOTES NO. 4
เทคอนกรีตเพื่อปรับระดับความสูงของเสา
CONCRETE FILL FOR ADJUSTING THE HEIGHT OF POLE
1,800-3,000
ท่อ PVC ⌀ 40 มม. สำหรับร้อยสายดิน
⌀ 40 mm PVC PIPE, FOR GROUND WIRE
ระดับดิน
GROUND LEVEL
500
100
100
ทรายหยาบอัดแน่น
COMPACTED SAND
คอนกรีตหยาบ 1:3:5
ROUGH CONCRETE
เสาเข็มคอนกรีต ขนาด 0.44x0.44x8.50 ม.
10,000 กก.-ม. จำนวน 3 ต้น
3 PRESTRESSED CONCRETE PILES
0.44x0.44x8.50 m, 10,000 kg-m

กองมาตรฐานระบบไฟฟ้า
ฝ่ายมาตรฐานและความปลอดภัย

ผู้เขียน ..สมชาย..
ผู้ตรวจ
วิศวกร
หัวหน้าแผนก
ผู้อำนวยการกอง
ผู้อำนวยการฝ่าย

รองผู้ว่าการวางแผนและพัฒนาระบบไฟฟ้า

การไฟฟ้าส่วนภูมิภาค

ผู้ว่าการ

รายละเอียดที่ 10 ก 23 ก.ย. 2547
ฐานรากเสา (แบบที่ 21)

DETAIL 10 A
POLE FOUNDATION (TYPE 21)

ใช้แทนแบบ SA1-015/45016
ถูกแทนโดยแบบ
เขียนเสร็จวันที่ 10 พ.ค. 2547
แก้แบบวันที่
หน่วยเป็น มิลลิเมตร
มาตราส่วน 1:30

แบบเลขที่ SA1-015/47024
แผ่นที่ 1 ของจำนวน 2 แผ่น

23 ก.ย. 2547

การประกอบเลขที่
ASSEMBLY NO. 5687 G

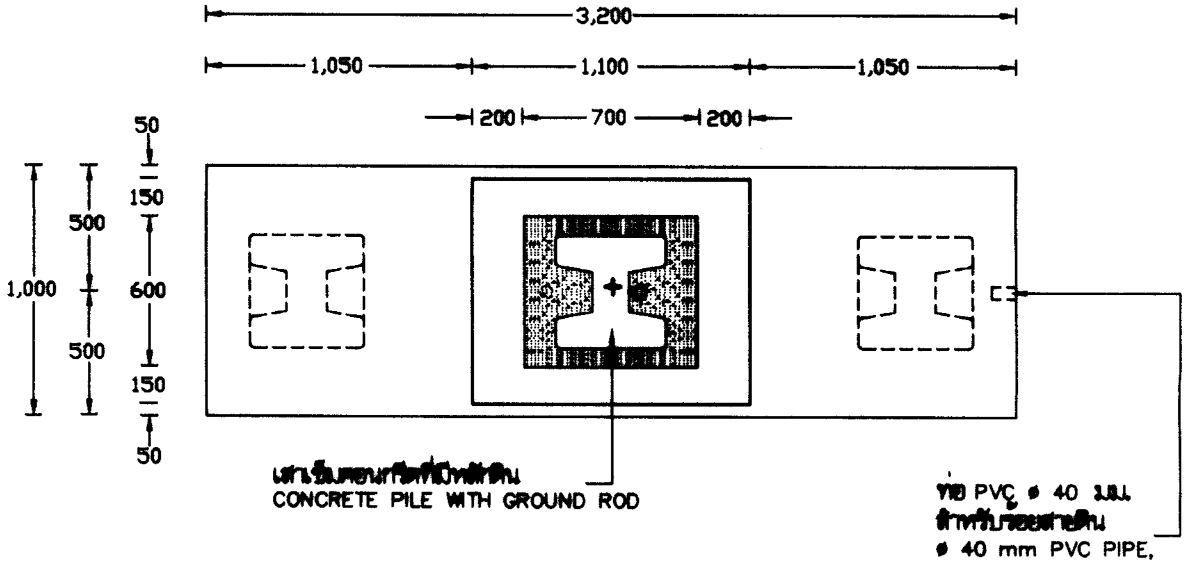

รูปตัด
SECTION A–A

หมายเหตุ

1 ใช้ในกรณีทางตรงหรือทางโค้ง ที่ไม่มีสายยึดโยง (กรณีพื้นที่ก่อสร้างฐานรากเสามีระดับต่ำกว่าระดับผิวจราจร 4.55-5.75 ม.)
2 ดูรายละเอียดเพิ่มเติมใน แบบเลขที่ IB2–011/44019
3 ดูข้อกำหนดการติดตั้งฐานรากเสาในเขตทางหลวง ตามแบบเลขที่ SA1–015/43012 (การประกอบเลขที่ 5687)

4 ระยะ "X"= 450 มม. สำหรับการก่อสร้างฐานรากเสา ในพื้นที่ทางหลวงที่ไม่มีทางเท้า ส่วนพื้นที่อื่นๆ ระยะ "X"= 0 มม.

NOTES

1 USE FOR STRAIGHT OR ANGLE LINE WITHOUT GUY (IN CASE OF GROUND SURFACE LEVEL IS BETWEEN 4.55–5.75 m LOWER THAN ROAD SURFACE LEVEL) .
2 SEE ADDITIONAL DETAIL, DWG. NO. IB2–011/44019 .
3 SEE RECOMMENDATION, FOR POLE FOUNDATION INSTALLATION IN HIGHWAY AREA, DWG. NO. SA1–015/43012 (ASSEMBLY NO. 5687) .
4 THE "X" IS 450 mm HEIGHT FOR FOUNDATION CONSTRUCTION IN HIGHWAY AREA WHICH HAVE NO PAVEMENT, OTHER AREA THE "X" IS ZERO .

อติวิทย์ ทอง... กฟจ.กน. กฟต.2 สายงาน (ต) ผวก. @PEA

กองมาตรฐานระบบไฟฟ้า
ฝ่ายมาตรฐานและความปลอดภัย

ผู้เขียน ..สมชาย..........
ผู้สำรวจ ....
วิศวกร ....
หัวหน้าแผนก ....
ผู้อำนวยการกอง ....
ผู้อำนวยการฝ่าย ....

รองผู้ว่าการวางแผนและพัฒนาระบบไฟฟ้า

การไฟฟ้าส่วนภูมิภาค

ผู้ว่าการ ....

23 ก.ย. 2547

รายละเอียดที่ 10 A
ฐานรากเสา (แบบที่ 21)

DETAIL 10 A
POLE FOUNDATION (TYPE 21)

ใช้แทนแบบ SA1–015/45016
ถูกแทนโดยแบบ ....
เขียนเสร็จวันที่ .10. ส.ค. .2547.
แก้แบบวันที่ ....
มิติเป็น ..มิลลิเมตร..
มาตราส่วน ...1:30...

แบบเลขที่ SA1–015/47024
แผ่นที่ .2. ของจำนวน .2. แผ่น

23 ก.ย. 2547