การประกอบเลขที่ 0211
ASSEMBLY NO. 0211

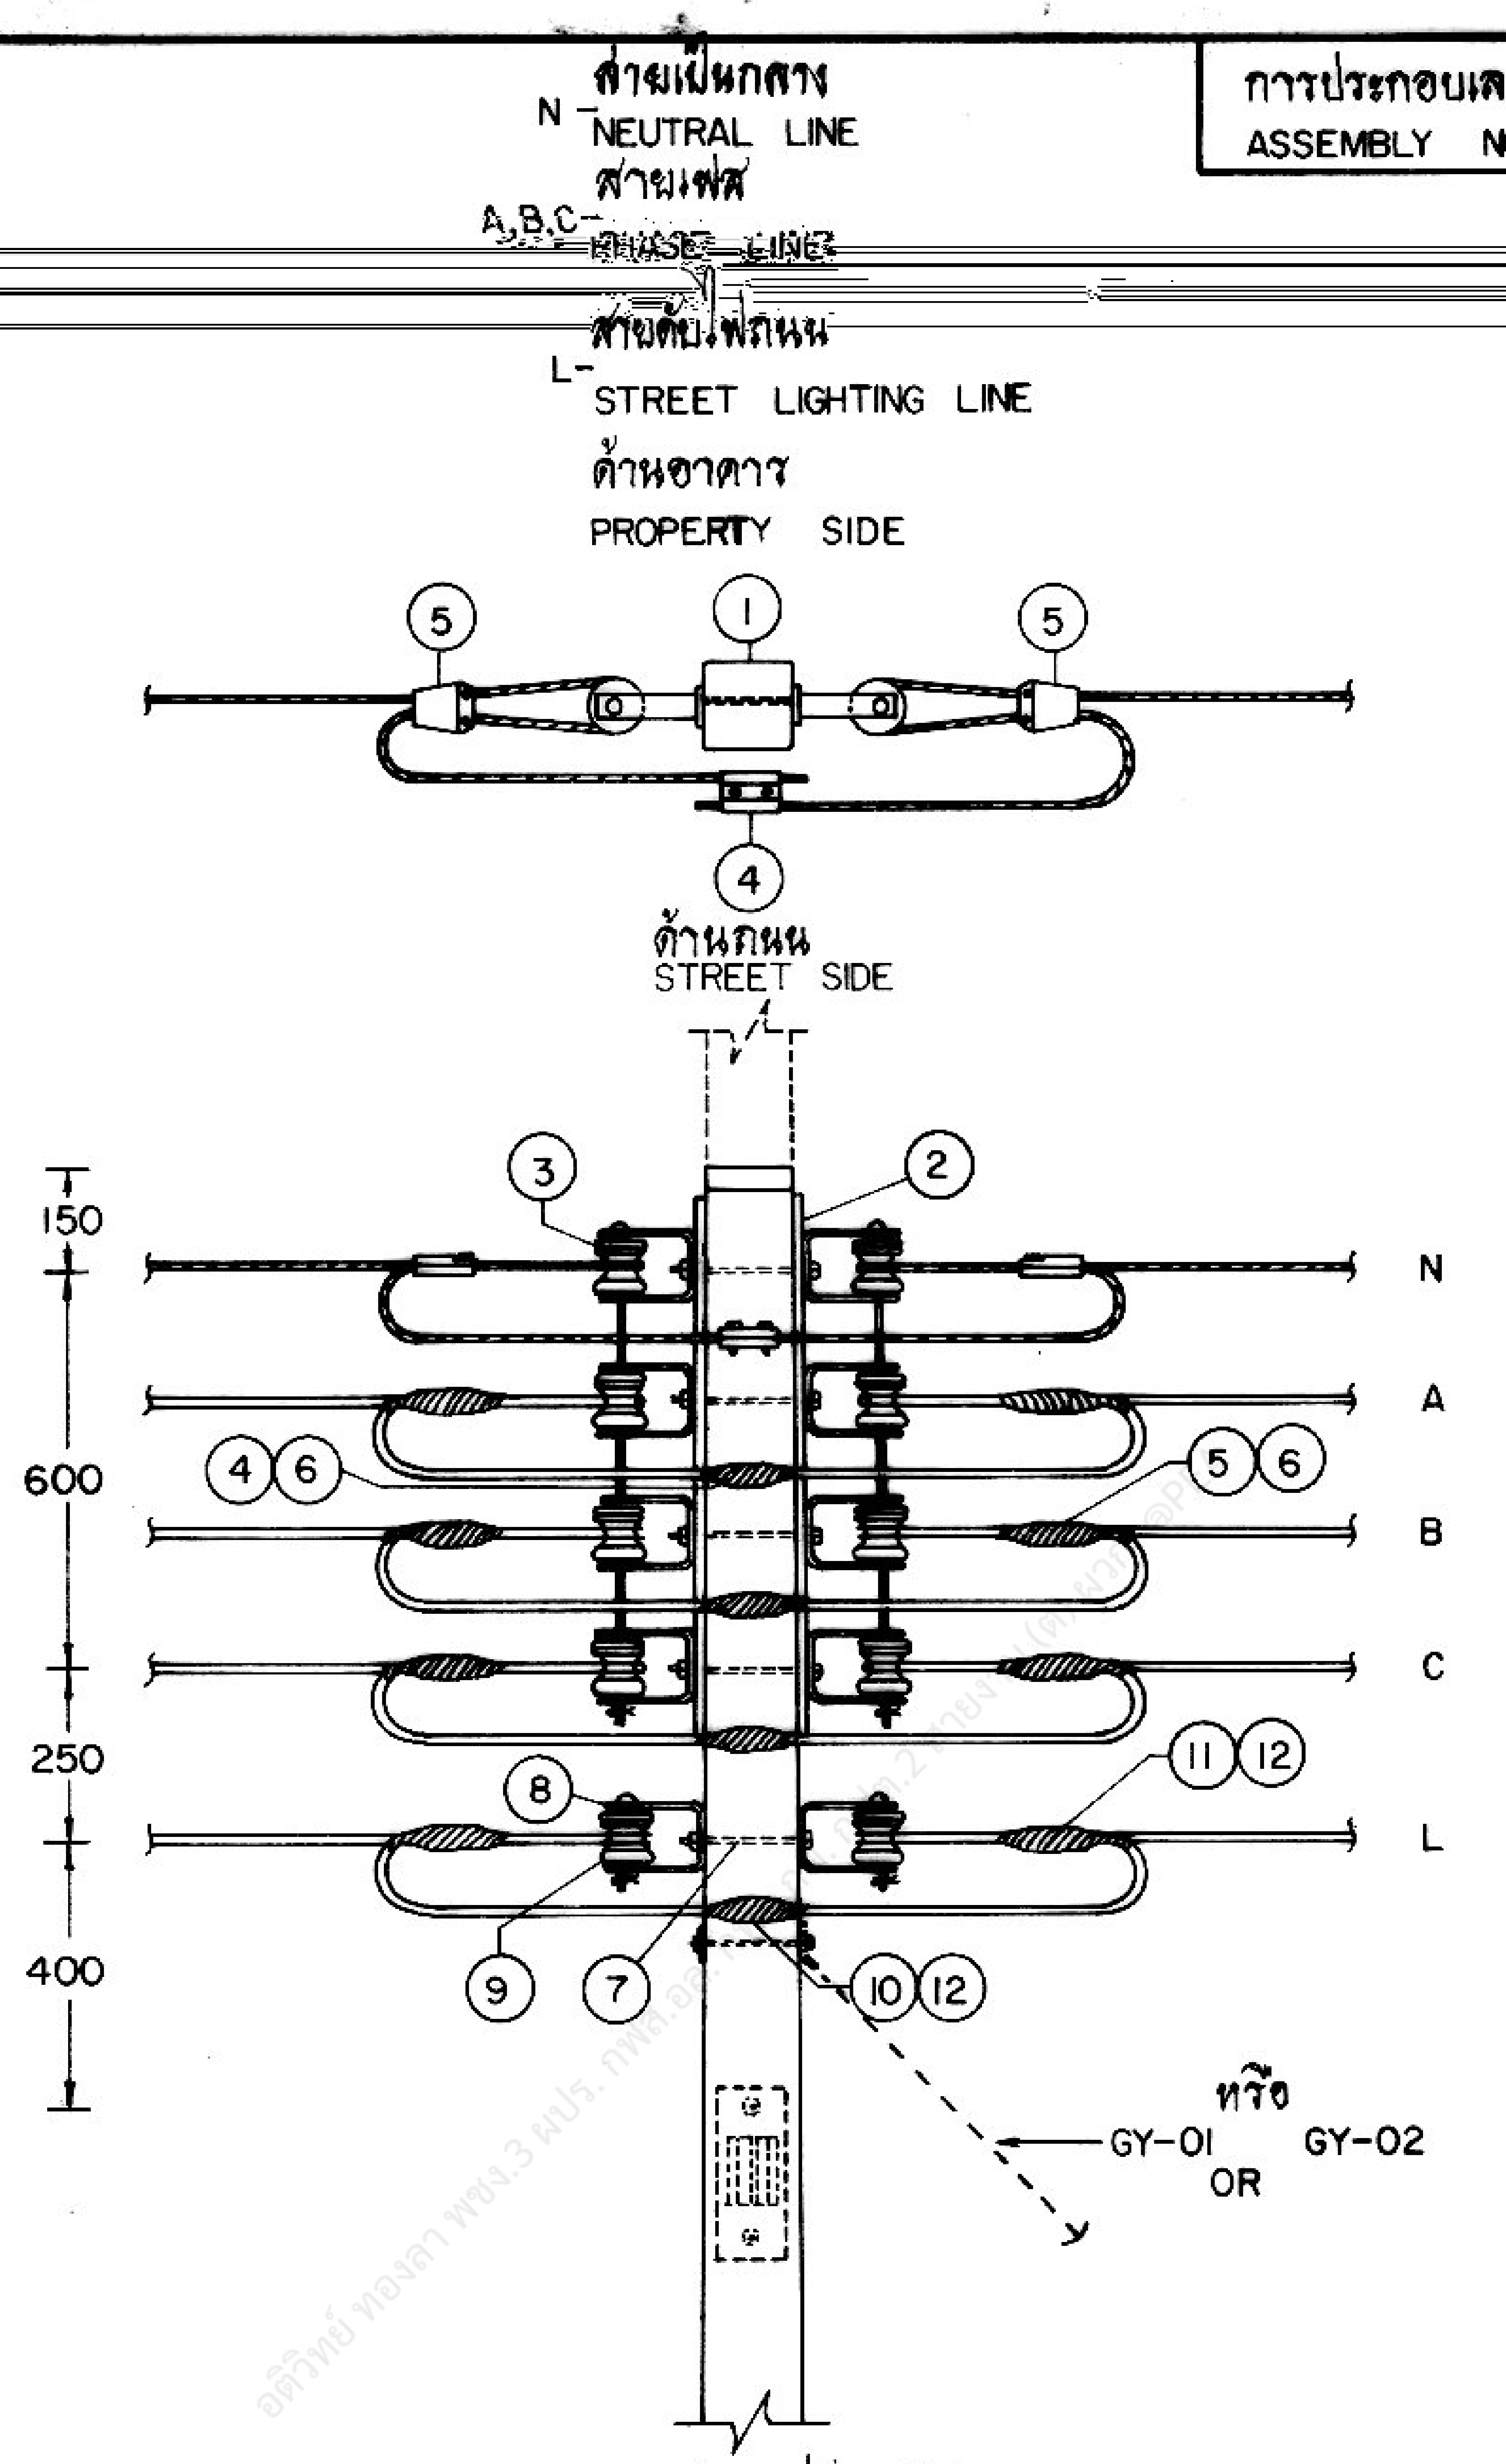

แบบ 3 เฟส 4 สาย
3-PHASE 4-WIRE

หมายเหตุ ให้พันหุ้ม พีจี. คอนเนคเตอร์และ คอนเนคเตอร์เข้าปลายสายสำหรับสายหุ้มฉนวนด้วย PVC เทป

NOTE PG. CONNECTOR AND DEADEND CONNECTOR FOR INSULATED CONDUCTOR SHALL BE INSULATED WITH PVC TAPE.

กองวิศวกรรมไฟฟ้าและเครื่องกล
ฝ่ายวิศวกรรม

ผู้เขียน
ผู้ตรวจ
วิศวกร
หัวหน้าแผนก
หัวหน้ากอง
ผู้อำนวยการฝ่าย
รองผู้ว่าการฝ่ายเทคนิค

การไฟฟ้าส่วนภูมิภาค

ผู้ว่าการ

การติดตั้งแร็คแรงต่ำกับเสาคอนกรีต 9 ม.
สำหรับเข้าปลายสาย 2 ข้าง

SECONDARY RACK INSTALLATION ON 9m CONCRETE POLE
FOR DOUBLE DEADEND STRUCTURE

ใช้แทนแบบ
ถูกแทนโดยแบบ
เขียนเสร็จวันที่ 15 สค. 21
แก้แบบวันที่
มิติเป็น มม.
มาตราส่วน 1:20
แบบเลขที่ SA1-015/21047
แผ่นที่ 1 ของจำนวน 2 แผ่น

การประกอบเลขที่
ASSEMBLY NO. 0211

บัญชีวัสดุ
BILL OF MATERIAL

ลำดับที่ ITEM	รายละเอียด DESCRIPTION	จำนวน REQ'D	วัสดุเลขที่ MAT. NO.
1	สลักเกลียว M 16 X 200 มม. BOLT, MACHINE, M 16 X 200 mm	4 *	01110202
1a	สลักเกลียว M 16 X 250 มม. สำหรับเสาคอนกรีต 12 ม. BOLT, MACHINE, M 16 X 250 mm FOR 12 m CONCRETE POLE	4 *	01110203
2	แร็ค 4 X200 มม. แบบหลังยื่น RACK, SECONDARY, MEDIUM PRESSED STEEL 4 X 200 mm EXTENSION BACK	2	03130002
3	ลูกรอกแรงต่ำ มอก. 227 แบบ ข (แบบ 53-2) INSULATOR, SPOOL TYPE, L.T. TIS 227 TYPE B (CLASS 53-2)	4	03030000
4	พี.จี. คอนเนคเตอร์ สำหรับสายอะลูมิเนียม ขนาดตามต้องการ CONNECTOR, PARALLEL GROOVE, Al SIZE AS REQUIRED	4	02300102-3
5	คอนเนคเตอร์เข้าปลายสายอะลูมิเนียม ขนาดตามต้องการ CONNECTOR, DEADEND, Al SIZE AS REQUIRED	8	02310000-2
6	PVC เทป กว้าง 19 มม. (ใช้ความยาว 2 ม. ต่อ จุด) มอก. 386 PVC TAPE 19 mm WIDE (2 m LONG PER POINT) TIS 386		02180001 or 02180002
	สำหรับการติดตั้งสายดับไฟถนน FOR STREET LIGHTING INSTALLATION		
7	สลักเกลียว M 16 X 200 มม. BOLT, MACHINE, M 16 X 200 mm	1	01110201
7a	สลักเกลียว M 16X250 มม. สำหรับเสาคอนกรีต 12 ม. BOLT, MACHINE, M 16X250 mm FOR 12 m CONCRETE POLE	1	01110203
8	ที่จับลูกรอก สำหรับลูกรอก มอก.227 (แบบ 53-2) CLEVIS, FLAT STEEL, FOR INSULATOR TIS 227 (CLASS 53-2)	2	03130100
9	ลูกรอกแรงต่ำ มอก. 227 แบบ ข (แบบ 53-2) INSULATOR, SPOOL TYPE, L.T. TIS 227 TYPE B (CLASS 53-2)	3	03030000
10	พี.จี. คอนเนคเตอร์ สลักคู่สำหรับสายอะลูมิเนียม 25–95 ต.มม. CONNECTOR, PARALLEL GROOVE, DOUBLE BOLT, Al. 25 – 95 mm^2	1	02300102
11	คอนเนคเตอร์เข้าปลายสายอะลูมิเนียม 25 – 35 ต.มม. CONNECTOR, DEADEND, Al 25 – 35 mm^2	2	02310000
12	PVC เทป กว้าง 19 มม. (ใช้ความยาว 2 ม. ต่อจุด) มอก. 386 PVC TAPE 19 mm WIDE (2 m LONG PER POINT) TIS 386		02180001 or 02180002

หมายเหตุ *กรณีติดตั้งสายยึดโยง ให้เพิ่มสลักเกลียว M 16X200 มม. หรือ M 16X250 มม. จำนวน 1 ตัว และแหวนสี่เหลี่ยมแบน 52X52X4.5 มม. จำนวน 1 ตัว

NOTE * FOR GUY ASSEMBLY, ADD ONE M 16 X 200 mm OR M 16 X 250 mm MACHINE BOLT AND ONE 50 X 50 X 5 mm SQUARE WASHER.

กองวิศวกรรมไฟฟ้าและเครื่องกล ฝ่ายวิศวกรรม	การไฟฟ้าส่วนภูมิภาค	ใช้แทนแบบ ถูกแทนโดยแบบ
ผู้เขียน ผู้สำรวจ วิศวกร หัวหน้าแผนก หัวหน้ากอง ผู้อำนวยการฝ่าย	ผู้ว่าการ	เขียนเสร็จวันที่ 15 สค. 21 แก้แบบวันที่ คิดเป็น มาตราส่วน
	การติดตั้งแร็คแรงต่ำกับเสาคอนกรีต 9 ม. สำหรับเข้าปลายสาย 2 ข้าง	
รองผู้ว่าการฝ่ายเทคนิค	SECONDARY RACK INSTALLATION ON 9 m CONCRETE POLE FOR DOUBLE DEADEND STRUCTURE	แบบเลขที่ SAI-015/21047 แผ่นที่ 2 ของจำนวน 2 แผ่น