การประกอบเลขที่
ASSEMBLY NO. 0514

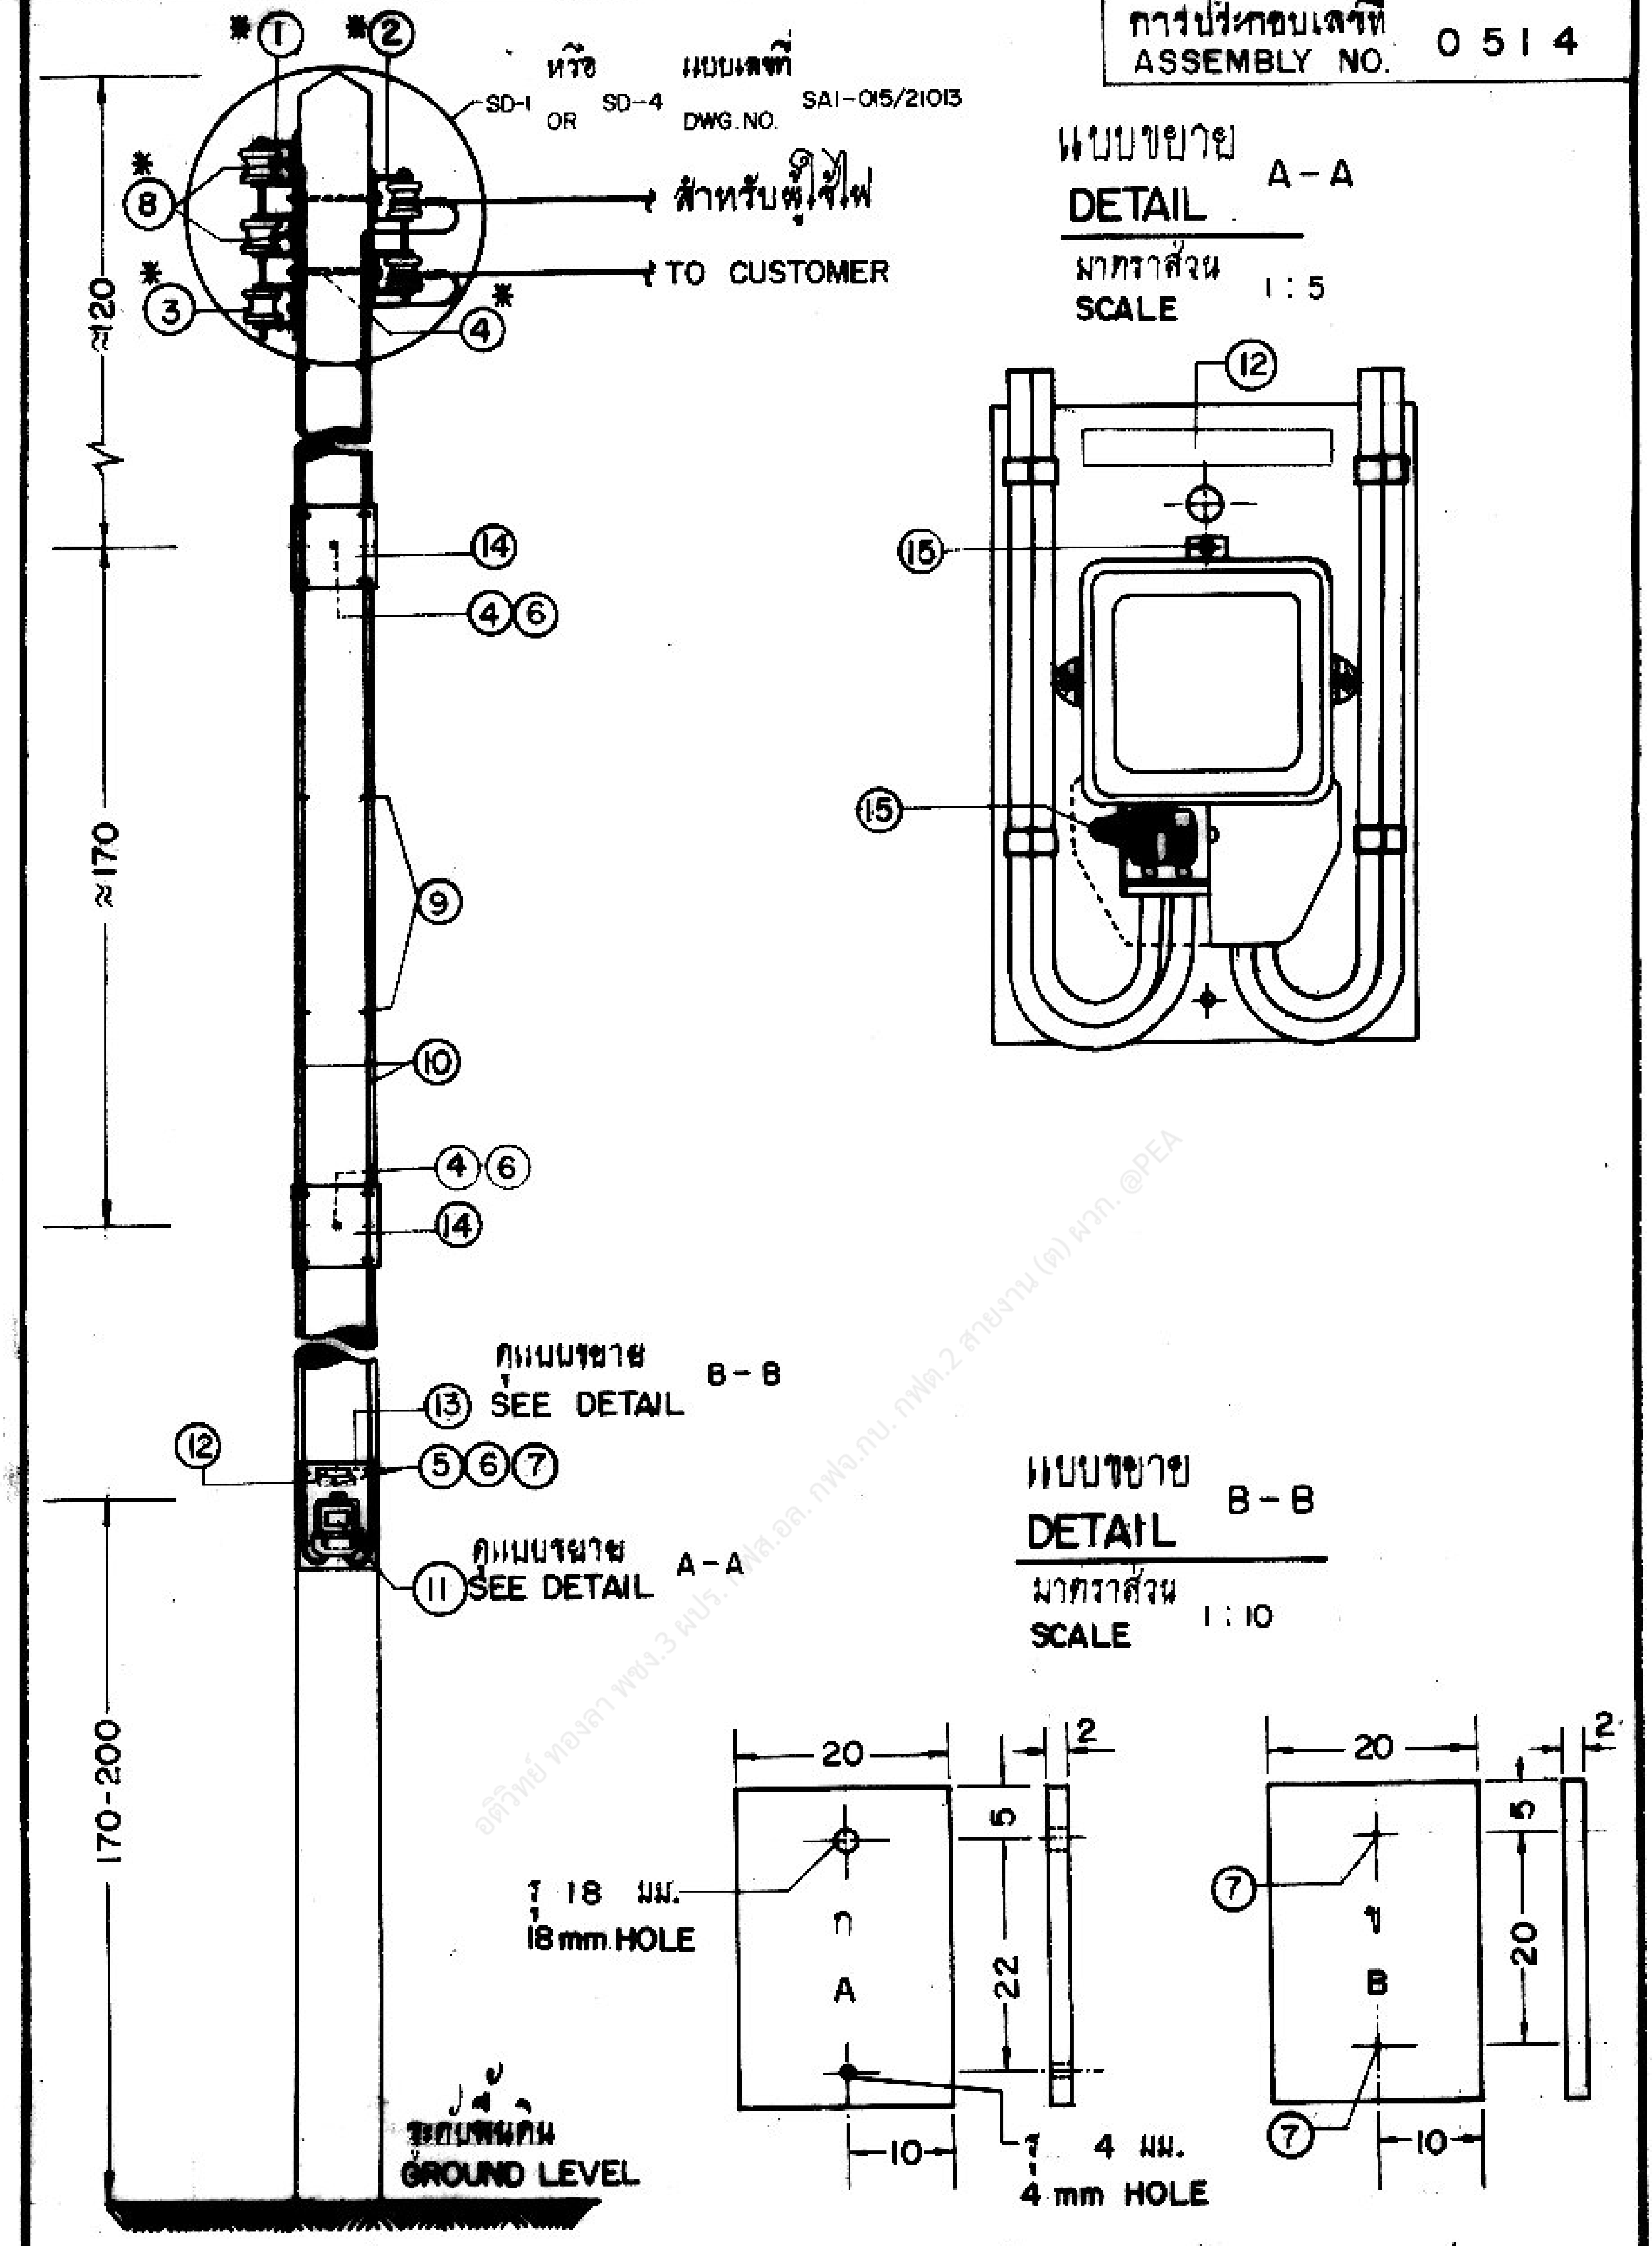

* จำนวนอุปกรณ์ให้ดูแบบการประกอบอุปกรณ์ที่หัวเสาแบบเลขที่ SAI-015/21013 (การประกอบเลขที่ 0519)
NUMBER OF MATERIALS, SEE DWG. FOR POLE TOP ASSEMBLY, DWG. NO. SAI-015/21013, (ASSEMBLY NO. 0519)

กองวิศวกรรมและวางแผน	การไฟฟ้าส่วนภูมิภาค	ใช้แทนแบบ I51-1001/1OF2
ผู้เขียน ระพี สถาปนิก วิศวกร หัวหน้าแผนก ผู้อำนวยการกอง	ผู้ว่าการ การติดตั้งมิเตอร์ 1 เฟส สำหรับมิเตอร์ 1 ตัว ขนาด 3-10 แอมแปร์	ถูกแทนโดยแบบ เขียนเสร็จวันที่ 11 ม.ค. 15 แก้แบบวันที่ 17 ก.ค. 21 คิดเป็น จน. มาตราส่วน
รองผู้ว่าการฝ่ายเทคนิค	1-Ø METER INSTALLATION FOR 1 METER RATING 3-10 AMPERES	แบบเลขที่ I50-015/150001 แผ่นที่ 1 ของจำนวน 2 แผ่น

25

การประกอบเลขที่
ASSEMBLY NO. 0514

บัญชีวัสดุ
BILL OF MATERIAL

ลำดับที่ ITEM	รายละเอียด DESCRIPTION	จำนวน REQ'D		วัสดุเลขที่ MAT. NO.
		ก/A	ข/B	
1	แร็คตามต้องการ RACK, SECONDARY, AS REQUIRED	-	-	03130000-2
2	แร็กสำหรับต่อเข้าบ้านผู้ใช้ไฟตามต้องการ RACK, SECONDARY, TO CUSTOMER AS REQUIRED	-	-	03130000-2
3	ลูกรอกแรงต่ำ มอก. 227 แบบ ข (แบบ 53-2) INSULATOR, SPOOL TYPE, L.T. TIS 227 TYPE B (CLASS 53-2)	-	-	03030000
4	สลักเกลียวหัวเหลี่ยม M 16X200 มม.พร้อมน็อทเหลี่ยม BOLT, MACHINE, M 16 X200 mm COMPLETE WITH SQUARE NUT	2	-	01110202
5	สลักเกลียวหัวเหลี่ยม M 16X250 มม. พร้อมน็อทเหลี่ยม BOLT, MACHINE, M16 X 250 mm COMPLETE WITH SQUARE NUT	1	-	01110203
6	แหวนเหลี่ยมแบนขนาด 52 X 52 X 4.5 มม. รู Ø 18 มม. มอก. 258 WASHER, SQUARE FLAT, 52 X 52 X 4.5 mm, HOLE Ø 18 mm, TIS 258	6	-	01180100
7	ตะปูเหล็กหัวกลมแบน ยาว 60 มม. Ø 2.80 มม. มอก. 113 NAIL, ROUND MILD STEEL WIRE 60mm LONG Ø 2.80mm TIS 113	-	2	
8	คอนเน็คเตอร์สำหรับสายอะลูมิเนียมกับสายอะลูมิเนียมพันด้วย PVC เทปแล้วหุ้มด้วยคอมเปาด์ CONNEC Al TO Al WRAPPED WITH PVC TAPE & COATED WITH INSUL. COM.	-	-	02300100-1 and 02180001
9	เข็มขัดรัดสายไฟ ช่วงระยะ 50 ซม. STRAP, CABLE AT 50 cm INTERVALS			
10	สายอะลูมิเนียมหุ้มฉนวนเข้ามิเตอร์แรงต่ำ 0.6/1 kV CONDUCTOR, NAYY OR NAY 0.6/1 kV, Al	ม. m	ม. m	02070100-1
11	วัตต์อาวร์มิเตอร์ 1 เฟส METER, WATTHOUR 1-Ø WITH EXTENDED TERMINAL COVER	1	1	06000000-1
12	หมายเลขผู้ใช้ไฟ NUMBER OF CUSTOMER	1	1	
13	แป้นไม้รองรับมิเตอร์ไสแล้ว ขนาด 30 X 20X2 ซม. METER PLATE(HARD WOOD)SURFACE FINISHED SIZE 30X20X2 cm	1	1	
14	แป้นไม้สำหรับยึดสายเข้าและออกจากมิเตอร์ไสแล้วขนาด 20 X 20 X 2 ซม. CABLE PLATE(HARD WOOD)SURFACE FINISHED SIZE 20X20X2 cm	2	-	
15	ตะปูเกลียว ขนาด 25 มม. SCREW, WOOD, SIZE 25 mm	3	3	

หมายเหตุ
1. ก สำหรับเสาคอนกรีตแรงต่ำ และ ข สำหรับเสาไม้แรงต่ำ
2. บัญชีวัสดุใช้เฉพาะการติดตั้งมิเตอร์แรงต่ำเท่านั้น ส่วนการประกอบอุปกรณ์ที่หัวเสาให้ดูแบบเลขที่ SAI-015/21013
3. สำหรับการติดตั้งบนเสาคอนกรีตแรงสูง 12 ม. ให้ใช้บัญชีวัสดุของเสาคอนกรีตแรงต่ำ แต่ให้เพิ่มความยาวของสลักเกลียวอีก 50 มม.

NOTES
1. A FOR L.T. CONCRETE POLE & B FOR L.T. WOOD POLE.
2. BILL OF MATERIALS USE ONLY FOR L.T. METER INSTALLATION, SEE DWG. FOR POLE TOP ASSEMBLY, DWG. NO. SAI-015/21013. (ASSEMBLY NO. 0519)
3. FOR INSTALLATION ON 12 m H.T. CONCRETE POLE, USE BILL OF MATERIAL FOR L.T. CONCRETE POLE BUT ADD 50 mm TO THE LENGTH OF MACHINE BOLT.

กองวิศวกรรมและวางแผน
ผู้เขียน
สถาปนิก
วิศวกร
หัวหน้าแผนก
ผู้อำนวยการกอง
รองผู้ว่าการฝ่ายเทคนิค

การไฟฟ้าส่วนภูมิภาค
ผู้ว่าการ

การติดตั้งมิเตอร์ 1 เฟส สำหรับมิเตอร์ 1 ตัว
ขนาด 3 - 10 แอมแปร์

1Ø METER INSTALLATION FOR 1 METER
RATING 3 - 10 AMPERES

ใช้แทนแบบ I51-1001/2 OF 2
ถูกแทนโดยแบบ
เขียนเสร็จวันที่ 18 ม.ค. 15
แก้แบบวันที่ 17 กค. 21
มิติเป็น
มาตราส่วน
แบบเลขที่ I50-015/15001
แผ่นที่ 2 ของจำนวน 2 แผ่น