การประกอบเลขที่ 0307
ASSEMBLY NO.

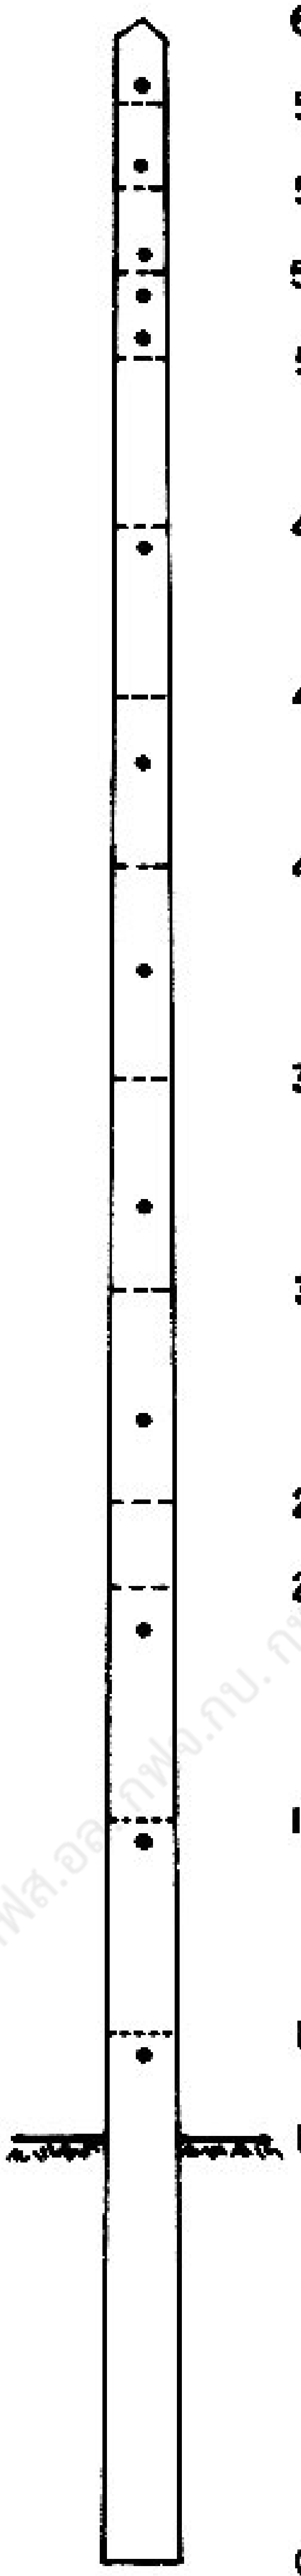

การใช้งาน APPLICATION	ความยาวรู มม. HOLE LENGTH mm	ตำแหน่งรู ม. HOLE POSITION m	ตำแหน่งรู ม. HOLE POSITION m	ความยาวรู มม. HOLE LENGTH mm	การใช้งาน APPLICATION
	120	6.000	6.000	120	
	122	5.850	5.800	122	
แร็คพาดสายแรงต่ำ และไม้คอนพาดสายแรงต่ำ SECONDARY RACK & L.T. CROSSARM	124	5.650	5.600	124	แร็คพาดสายแรงต่ำ SECONDARY RACK
	126	5.450	5.400	126	
	127	5.350			
	128	5.250	5.200	128	
แป้นไม้ยึดสายเข้าออกมิเตอร์ และยึดสายดิน CABLE PLATE & EARTHING FIXTURE	133	4.750	4.800	132	แป้นไม้ยึดสายเข้าออกมิเตอร์ และยึดสายดิน CABLE PLATE & EARTHING FIXTURE
			4.400	136	
ยึดสายดิน EARTHING FIXTURE	138	4.250			ยึดสายดิน EARTHING FIXTURE
			4.000	140	
	143	3.750			
			3.500	145	
แป้นไม้รองรับมิเตอร์ และตู้มิเตอร์ METER PLATE & METER CABINET	148	3.200			แป้นไม้รองรับมิเตอร์ และตู้มิเตอร์ METER PLATE & METER CABINET
			3.000	150	
	153	2.700			
			2.500	155	
			2.300	157	
	158	2.200			
ยึดสายดิน EARTHING FIXTURE	163	1.700	1.750	163	ยึดสายดิน EARTHING FIXTURE
	168	1.200	1.250	168	
	ระดับดิน GROUND LEVEL	1.000	1.000	ระดับดิน GROUND LEVEL	
	180	0.000	0.000	180	

หมายเหตุ

1 ความต้านทานโมเมนต์ใช้งานของเสาที่ระดับดิน ไม่น้อยกว่า 550 กก.- ม.
2 ขนาดรูเสา ø 19 มม. (3/4")
3 น้ำหนักเสาประมาณ 320 กก.

NOTES

1 MINIMUM RESISTING OF BENDING MOMENT AT GROUND LEVEL SHALL BE 550 kg-m .
2 HOLE SIZE ø 19 mm (3/4") .
3 WEIGHT OF POLE APPROXIMATE 320 kg .

กองวิศวกรรมไฟฟ้าและเครื่องกล
ฝ่ายวิศวกรรม
ผู้เขียน
ผู้ตรวจ
วิศวกร
หัวหน้าแผนก
หัวหน้ากอง
ผู้อำนวยการฝ่าย
รองผู้ว่าการฝ่ายเทคนิค

การไฟฟ้าส่วนภูมิภาค
ผู้ว่าการ

เสาคอนกรีตอัดแรง ขนาด 6.00 ม.
(เสาบริการ)

6.00 m CONCRETE POLE
(SERVICE POLE)

ใช้แทนแบบ
ถูกแทนโดยแบบ
เขียนเสร็จวันที่ 26 มี.ค. 23
แก้แบบวันที่
ผิดเป็น
มาตราส่วน 1 : 40
แบบเลขที่ SAI-015/23049
แผ่นที่ 1 ของจำนวน 1 แผ่น

7 มิ.ย. 2523