การประกอบเลขที่ ASSEMBLY NO.	5687 L

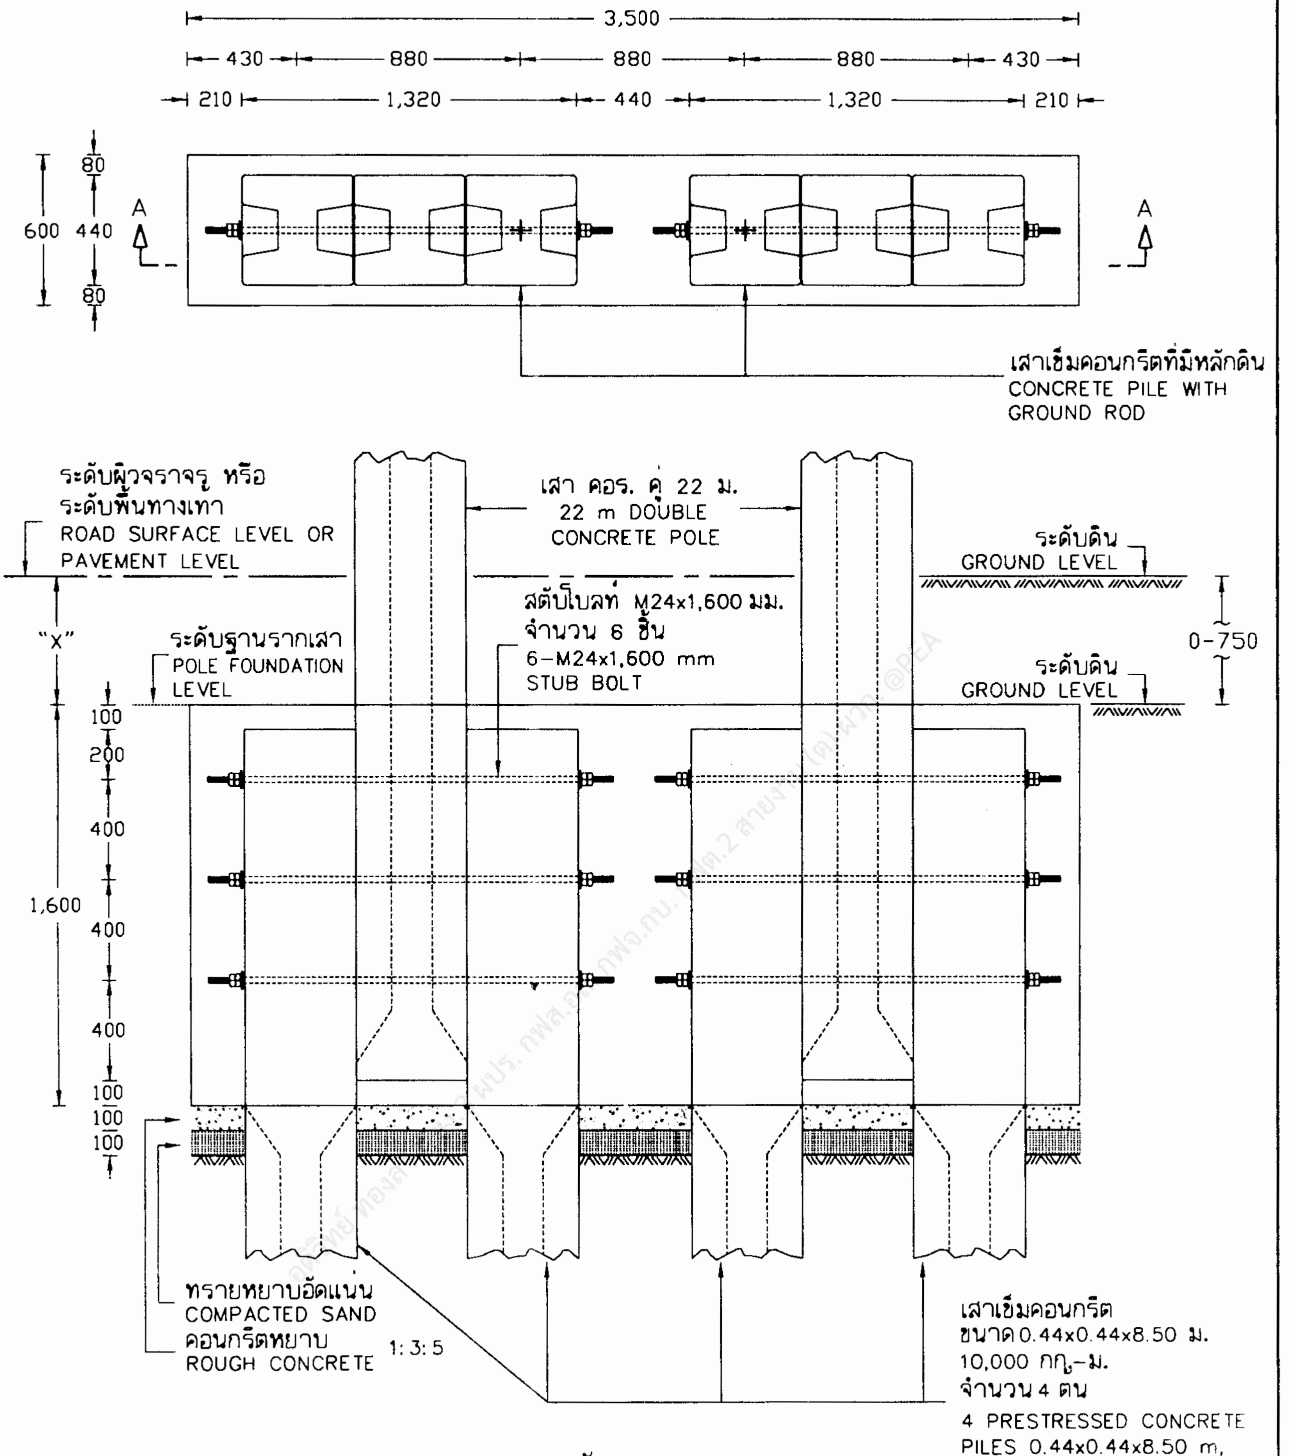

รูปตัด A–A
SECTION

กองมาตรฐานระบบไฟฟ้า ฝ่ายมาตรฐานและความปลอดภัย	การไฟฟ้าส่วนภูมิภาค	ใช้แทนแบบ .... ถูกแทนโดยแบบ ....
ผู้เขียน สมชาย ผู้สำรวจ วิศวกร หัวหน้าแผนก ผู้อำนวยการกอง ผู้อำนวยการฝ่าย	ผู้ว่าการ .... รายละเอียดที่ 10 B ฐานรากเสา (แบบที่ 13)	เขียนเสร็จวันที่ 1 มิ.ย. 2552 แก้แบบวันที่ .... มิติเป็น มิลลิเมตร มาตราส่วน 1:30
รองผู้ว่าการวางแผนและพัฒนาระบบไฟฟ้า	DETAIL 10 B POLE FOUNDATION (TYPE 13)	แบบเลขที่ SA1–015/52007 แผ่นที่ 1 ของจำนวน 2 แผ่น

การประกอบเลขที่ 5687 L
ASSEMBLY NO. 5687 L

หมายเหตุ

1 ให้ใช้ใน พื้นที่จำกัดซึ่งหมายถึง พื้นที่ที่ถูกจำกัดด้วยสาธารณูปโภค และพื้นที่ที่ไม่สามารถก่อสร้างฐานรากเสาคู่ คอร. แบบปกติได้

2 ใช้ในกรณีทางตรงหรือทางโค้ง ที่ไม่มีสายยึดโยง (กรณีพื้นที่ก่อสร้างฐานรากเสามีระดับต่ำกว่าระดับผิวจราจร หรือระดับพื้นทางเท้า 0.00-0.75 ม.)

3 ดูรายละเอียดเพิ่มเติมใน แบบเลขที่ IB4-A3/52001

4 ระยะ "X" สำหรับใช้กำหนดระดับฐานรากเสา มีดังนี้-.
  4.1 พื้นที่ทั่วไป
    กรณีมีทางเท้า และไม่มีทางเท้า
      ระยะ "X" = 300 มม.
  4.2 พื้นที่ทางหลวง
    กรณีมีทางเท้า
      ระยะ "X" = 300 มม.
    กรณีไม่มีทางเท้า
      ระยะ "X" = 750 มม.
  * กรณีไม่มีทางเท้า ให้เทียบระยะจากระดับผิวจราจร

NOTES

1 USE FOR LIMITED AREAS WHICH ARE THE LIMITED AREA WITH PUBLIC UTILITY AND AREAS THAT GENERAL DOUBLE POLE FOUNDATIONS CAN NOT BE CONSTRUCTED .

2 USE FOR STRAIGHT OR ANGLE LINE WITHOUT GUY (IN CASE OF GROUND SURFACE LEVEL IS BETWEEN 0.00–0.75 m LOWER THAN ROAD SURFACE LEVEL OR PAVEMENT LEVEL) .

3 SEE ADDITIONAL DETAIL, DWG. NO. IB4–A3/52001 .

4 THE SPACE FOR POLE FOUNDATION LEVEL SETTING,"X" .–
  4.1 GENERAL AREA
    IN CASE OF HAVING AND NO PAVEMENT,
      THE "X" IS 300 mm .
  4.2 HIGHWAY AREA
    IN CASE OF HAVING PAVEMENT,
      THE "X" IS 300 mm .
    IN CASE OF NO PAVEMENT,
      THE "X" IS 750 mm .
  * IN CASE OF NO PAVEMENT, THE SPACE IS COMPARED WITH ROAD SURFACE LEVEL

อดิวิทย์ ทองลา พชง.3 ผปร. กฟส.อล. กฟจ.กบ. กฟต.2 สาย

กองมาตรฐานระบบไฟฟ้า ฝ่ายมาตรฐานและความปลอดภัย	การไฟฟ้าส่วนภูมิภาค	ใช้แทนแบบ .... ถูกแทนโดยแบบ ....
ผู้เขียน ..สมชาย.......... ผู้สำรวจ .... วิศวกร .... หัวหน้าแผนก .... ผู้อำนวยการกอง .... ผู้อำนวยการฝ่าย	ผู้ว่าการ .... รายละเอียดที่ 10 B ฐานรากเสา (แบบที่ 13)	เขียนเสร็จวันที่ 1 มิ.ย. 2552 แก้แบบวันที่ .... มิติเป็น .... มาตราส่วน ....
รองผู้ว่าการวางแผนและพัฒนาระบบไฟฟ้า	DETAIL 10 B POLE FOUNDATION (TYPE 13)	แบบเลขที่ SA1-015/52007 แผ่นที่ 2 ของจำนวน 2 แผ่น