
การประกอบเลขที่ ASSEMBLY NO. 5209

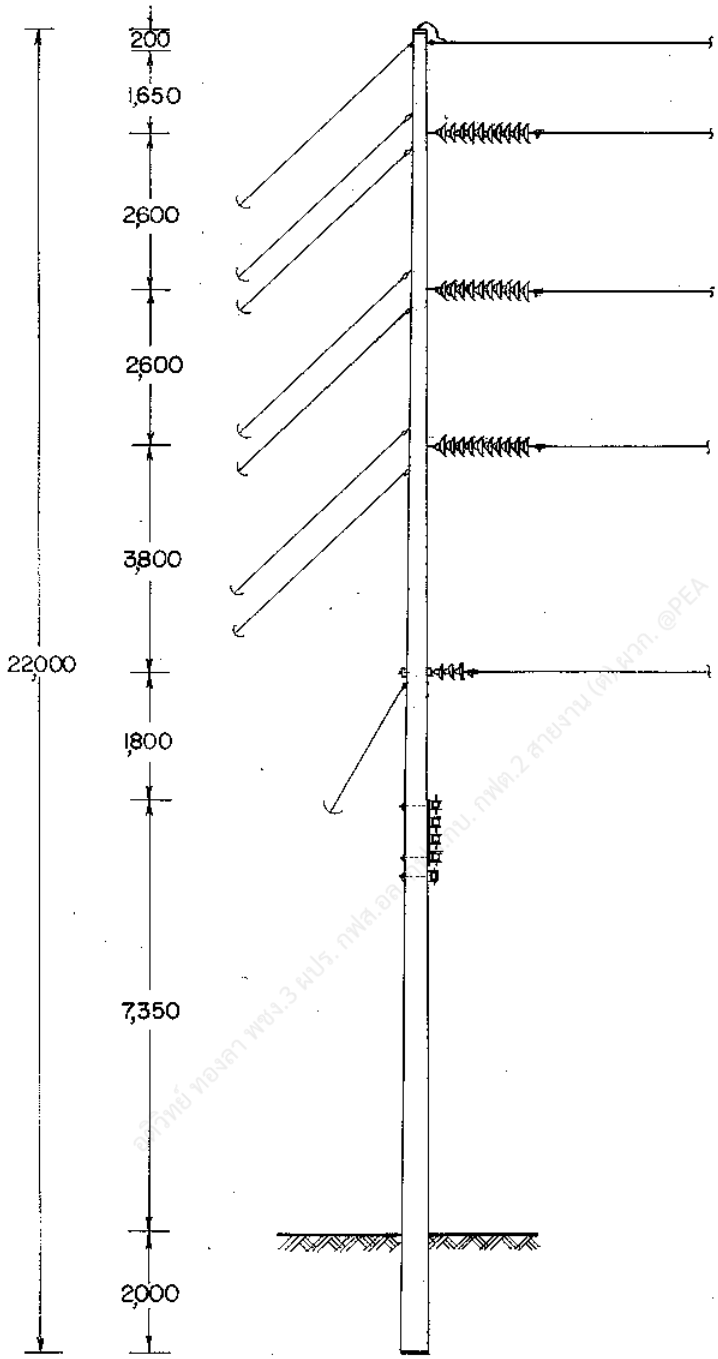


แบบ TYPE SS-DE-1

JAPANESE EXPERT TO PEA

กองวิศวกรรม	การไฟฟ้าส่วนภูมิภาค
ผู้เขียน / สถาปนิก / วิศวกร / หัวหน้าแผนก / ผู้อำนวยการกอง / รองผู้ว่าการฝ่ายเทคนิค	ผู้ว่าการ 26 มิ.ย. 19
	แผนโครงสร้างเสาสูงระนาบ 115 kV วงจรเดี่ยว แผนเสาสำหรับเข้าฟลายสาย
	115 kV LINE STRUCTURE CONSTRUCTION SINGLE CIRCUIT DEAD END STRUCTURE

ใช้แทนแบบ.....
ถูกแทนโดยแบบ.....
เขียนเสร็จวันที่ 18 มิ.ย. 19
แก้แบบวันที่ 24 มิ.ย. 23
มิติเป็น M.M.
มาตราส่วน 1:125
แบบเลขที่ S02-015/19026
แผ่นที่ 1 ของจำนวน 3 แผ่น

การประกอบเลขที่ ASSEMBLY NO. 5209

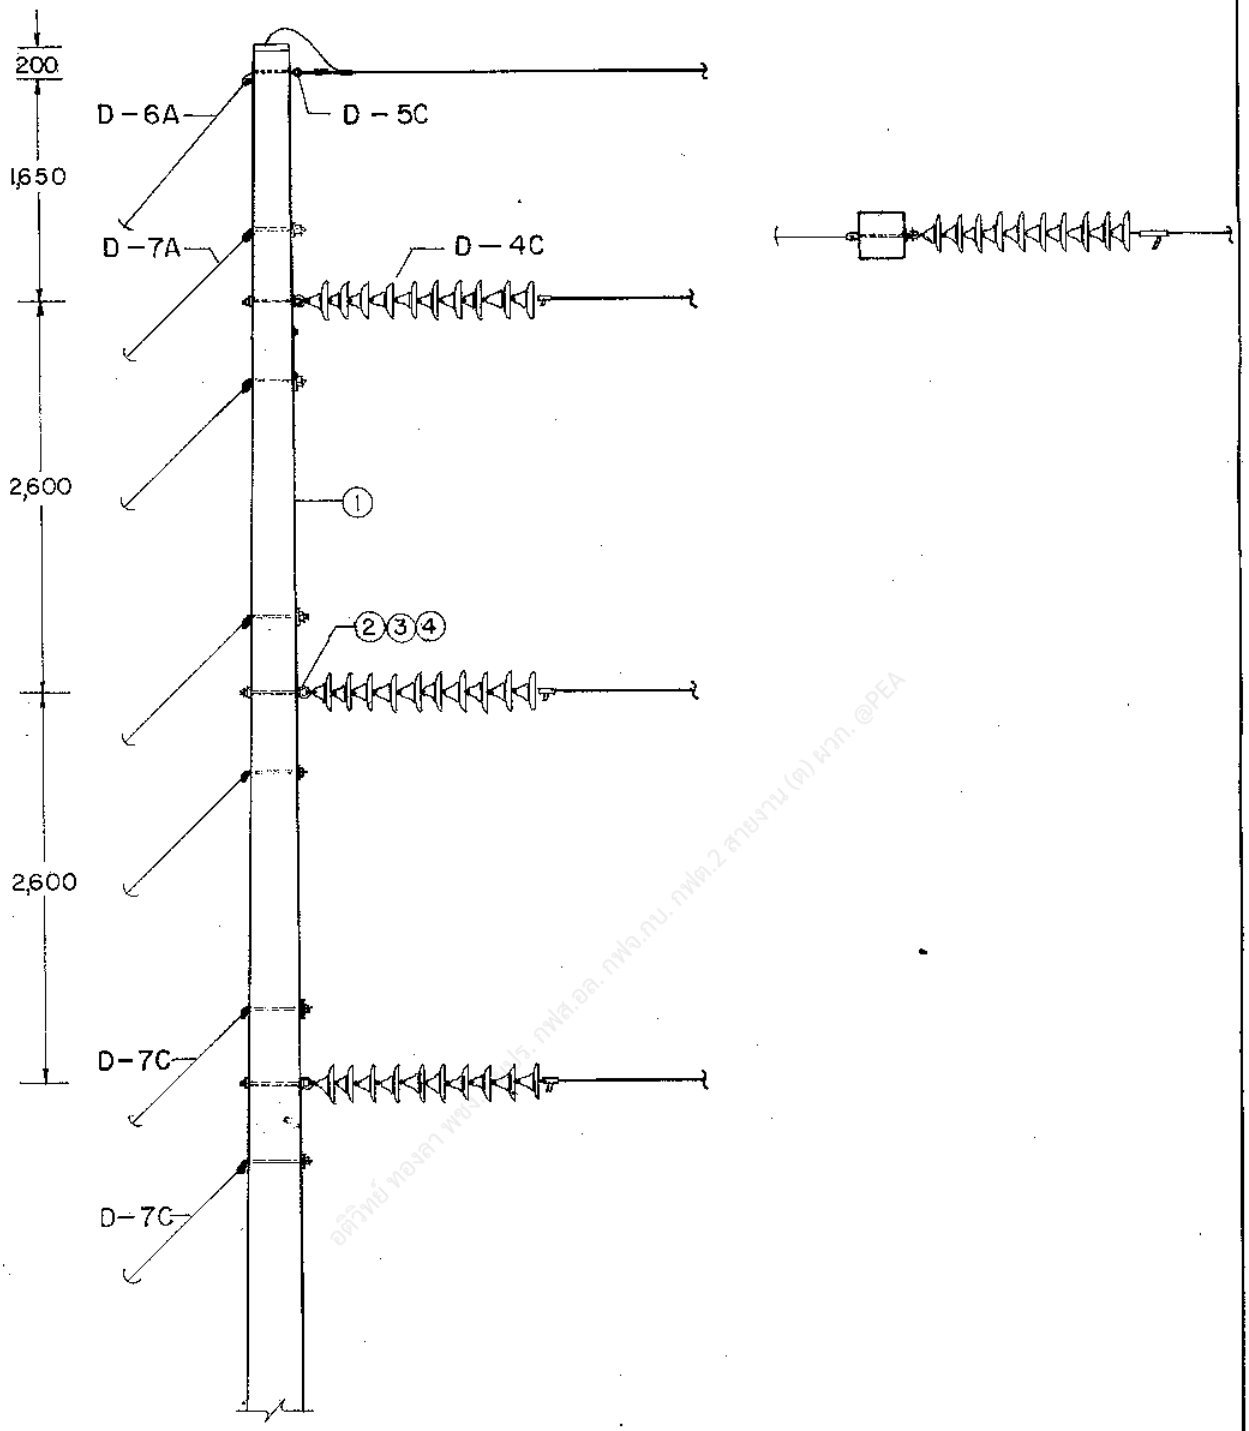

JAPANESE EXPERT TO PEA.

กองวิศวกรรม	การไฟฟ้าส่วนภูมิภาค	ใช้แทนแบบ
ผู้เขียน	ผู้ว่าการ	ถูกแทนโดยแบบ
วิศวกร	แบบโครงสร้างเสาส่งระนาบ 115 kV	เขียนเสร็จวันที่ 18 มี.ค. 19
หัวหน้าแผนก	วงจรเดี่ยว	แก้แบบวันที่ 24 มี.ค. 23, 15 ก.ย. 40
ผู้อำนวยการกอง	แผนเสาสำหรับเข้าปลายสาย	มิติเป็น ม.ม.
รองผู้ว่าการฝ่ายเทคนิค	115 kV LINE STRUCTURE CONSTRUCTION SINGLE CIRCUIT DEAD END STRUCTURE	มาตราส่วน 1:50
		แบบเลขที่ SO2-015/19026
		แผ่นที่ 2 ของจำนวน 3 แผ่น

การประกอบเลขที่ ASSEMBLY NO. 5209

บัญชีวัสดุ
BILL OF MATERIAL

ลำดับที่ ITEM	รายละเอียด DESCRIPTION	จำนวน REQ'D	วัสดุเลขที่ MAT. NO.
1	เสาคอนกรีต 22 ม. POLE, CONCRETE 22 m. LONG	1	00010011 (0041)
2	สลักห่วงโอเวล M 20 x 350 มม. BOLT, OVAL EYE M 20 x 350 mm.	3	01150100 (0260)
3	แหวนสี่เหลี่ยมโค้ง 62X62X6 มม.รู Ø 22 มม. มอก. 258 WASHER, SQUARE, FLAT 62X62X6 mmHOLE Ø 22mm TIS 258	6	01180101 (0356)
4	แหวนสปริง M 20 มอก. 259 WASHER, LOCK, M 20, TIS 259	3	01180302 (0366)
	รายละเอียด DETAIL		
D-4C	การประกอบลูกถ้วยแขวน SUSPENSION INSULATOR ASSEMBLY	3	
D-5C	การต่อสายล่อฟ้า OVERHEAD GROUND WIRE CONNECTION	1	
D-6A	การประกอบสายยึดโยงลวดเหล็กตีเกลียว 50 ต.มม. STEEL STRANDED WIRE 50 mm^2 GUY ASSEMBLY	1	
D-7A	การประกอบสายยึดโยงลวดเหล็กตีเกลียว 95 ต.มม. STEEL STRANDED WIRE 95 mm^2 GUY ASSEMBLY	4	
D-7C	การประกอบสายยึดโยงลวดเหล็กตีเกลียว 95 ต.มม. STEEL STRANDED WIRE 95 mm^2 GUY ASSEMBLY	2	
D-9A	สมอบกคอนกรีต CONCRETE ANCHOR	1	
D-10A	ฐานรากเสา POLE FOUNDATION	1	

JAPANESE EXPERT TO PEA.

วิศวกรรม

ผู้เขียน

สถาปนิก

วิศวกร

หัวหน้าแผนก

ผู้อำนวยการกอง

รองผู้ว่าการฝ่ายเทคนิค

การไฟฟ้าส่วนภูมิภาค

ผู้ว่าการ

แบบโครงสร้างเสาส่งระบบ 115 kV
วงจรเดี่ยว
แบบเสาสำหรับเข้าปลายสาย

115 kV LINE STRUCTURE CONSTRUCTION
SINGLE CIRCUIT
DEAD END STRUCTURE

ใช้แทนแบบ

ถูกแทนโดยแบบ

เขียนเสร็จวันที่ 18 มีค. 19

แก้แบบครั้งที่ 24 มีค. 23
15 กันย 40

มิติเป็น

มาตราส่วน

แบบเลขที่ S02-015/19026

แผ่นที่ 3 ของจำนวน 3 แผ่น