การประกอบเลขที่
ASSEMBLY NO 3408

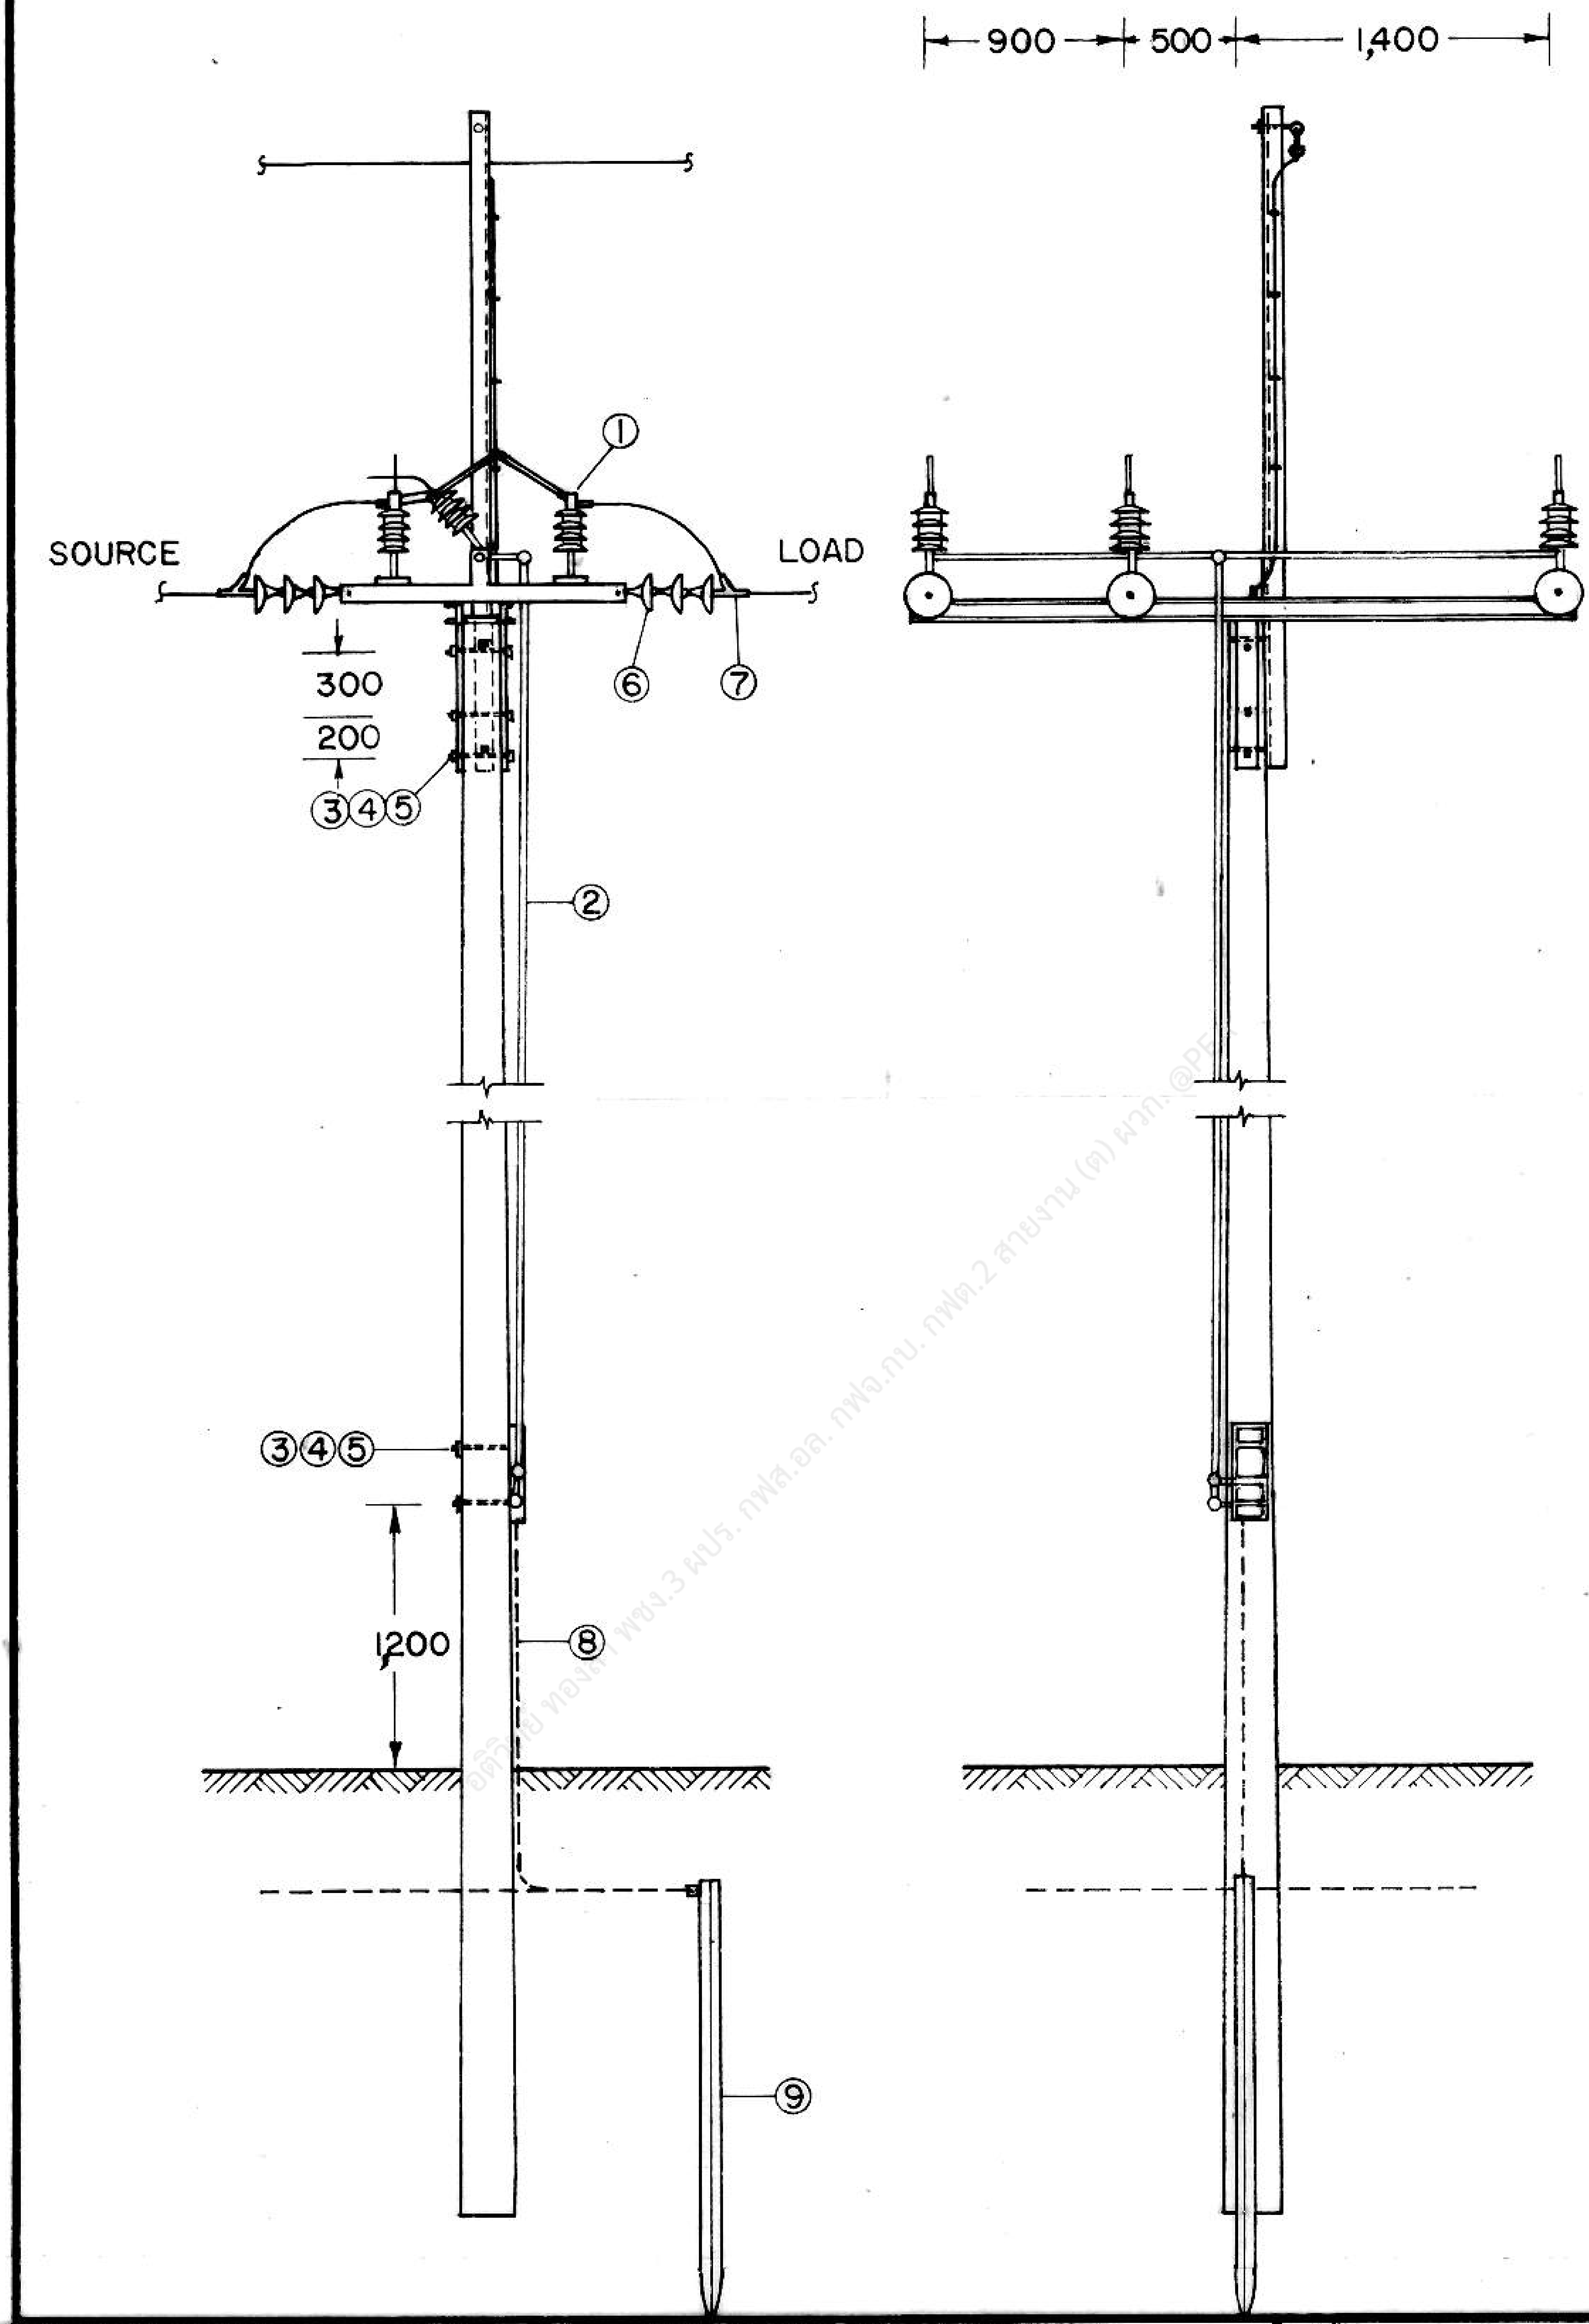

กองวิศวกรรม	การไฟฟ้าส่วนภูมิภาค	ใช้แทนแบบ ถูกแทนโดยแบบ
ผู้เขียน สถาปนิก วิศวกร หัวหน้าแผนก ผู้อำนวยการกอง	ผู้ว่าการ 7 มิ.ย. 2517 การติดตั้งสวิตช์ตัดตอนแรงสูง 3 ขา 33 kV	เขียนเสร็จวันที่ 3 มิ.ย. 17 แก้แบบวันที่ มิติเป็น มม. มาตราส่วน 1:50
รองผู้ว่าการฝ่ายเทคนิค	INSTALLATION OF ISOLATING SWITCH TRIPLE POLE 33 kV	แบบเลขที่ S02-015/17033 แผ่นที่ 1 ของจำนวน 2 แผ่น

7 มิ.ย. 2517

การประกอบ เลขที่
ASSEMBLY NO. 3408

บัญชีวัสดุ
BILL OF MATERIAL

ลำดับที่ ITEM	รายละเอียด DESCRIPTION	จำนวน REQ'D	วัสดุเลขที่ MAT. NO.
1	สวิตช์ตัดตอนแรงสูง 3 ขา 33 kV, 400 แอมป์ SWITCH, ISOLATING, TRIPLE POLE, 33 kV, 400 A	1	04060100
2	กลไกบังคับด้วยมือ สำหรับสวิตช์แยก 33 kV MANUAL OPERATING MECHANISM FOR SWITCH ISOLATING 33 kV	1	04069902
3	สลักเกลียว M 16 X 300 มม. BOLT, MACHINE M 16 X 300 mm	5	01110204
4	แหวนสี่เหลี่ยมแบน 52 X 52 X 4.5 มม. รู Ø 18 มม. มอก. 258 WASHER, SQUARE, FLAT 52 X 52 X 4.5 mm HOLE Ø 18 mm TIS 258	5	01180100
5	แหวนสปริง M 16 มอก. 259 WASHER, LOCK M 16 TIS 259	5	01180301
6	ลูกถ้วยแขวน มอก. 354 แบบ ง (แบบ 52-4) INSULATOR, SUSPENSION TYPE, TIS 354 TYPE D (CLASS 52-4)	18	03020002
7	สเตรนแคล้มป์ แบบตรง สำหรับสายอะลูมิเนียม 35 - 120 ต.มม. CLAMP, STRAIN, STRAIGHT TYPE FOR Al 35 - 120 mm^2	6	03110000 03110002
8	สายดินแบนแผ่นเหล็ก 30 X 3.5 มม. ชุบสังกะสี พร้อมอุปกรณ์ยึด CONDUCTOR, GROUND, FLAT IRON 30 X 3.5 mm GALV., COMP. WITH FIXING ACCESS.	11 ม. m.	01220010
9	หลักดิน 60 X 60 X 5 มม. ยาว 2 ม. ROD, GROUND 60 X 60 X 5 mm, 2 m LONG	1	01220002

กองวิศวกรรม

ผู้เขียน
สถาปนิก
วิศวกร
หัวหน้าแผนก
ผู้อำนวยการกอง
รองผู้ว่าการฝ่ายเทคนิค

การไฟฟ้าส่วนภูมิภาค

ผู้ว่าการ

7 มิ.ย. 2517

การติดตั้งสวิตช์ตัดตอนแรงสูง 3 ขา 33 kV

INSTALLATION OF ISOLATING SWITCH
TRIPLE POLE 33 kV

ใช้แทนแบบ
ถูกแทนโดยแบบ
เขียนเสร็จวันที่ 3 มิ.ย. 17
แก้แบบวันที่
มิติเป็น มม.
มาตราส่วน 1 : 50
แบบเลขที่ S02-015/17033
แผ่นที่ 2 ของจำนวน 2 แผ่น

7 มิ.ย. 2517