การประกอบเลขที่
ASSEMBLY NO. 3216

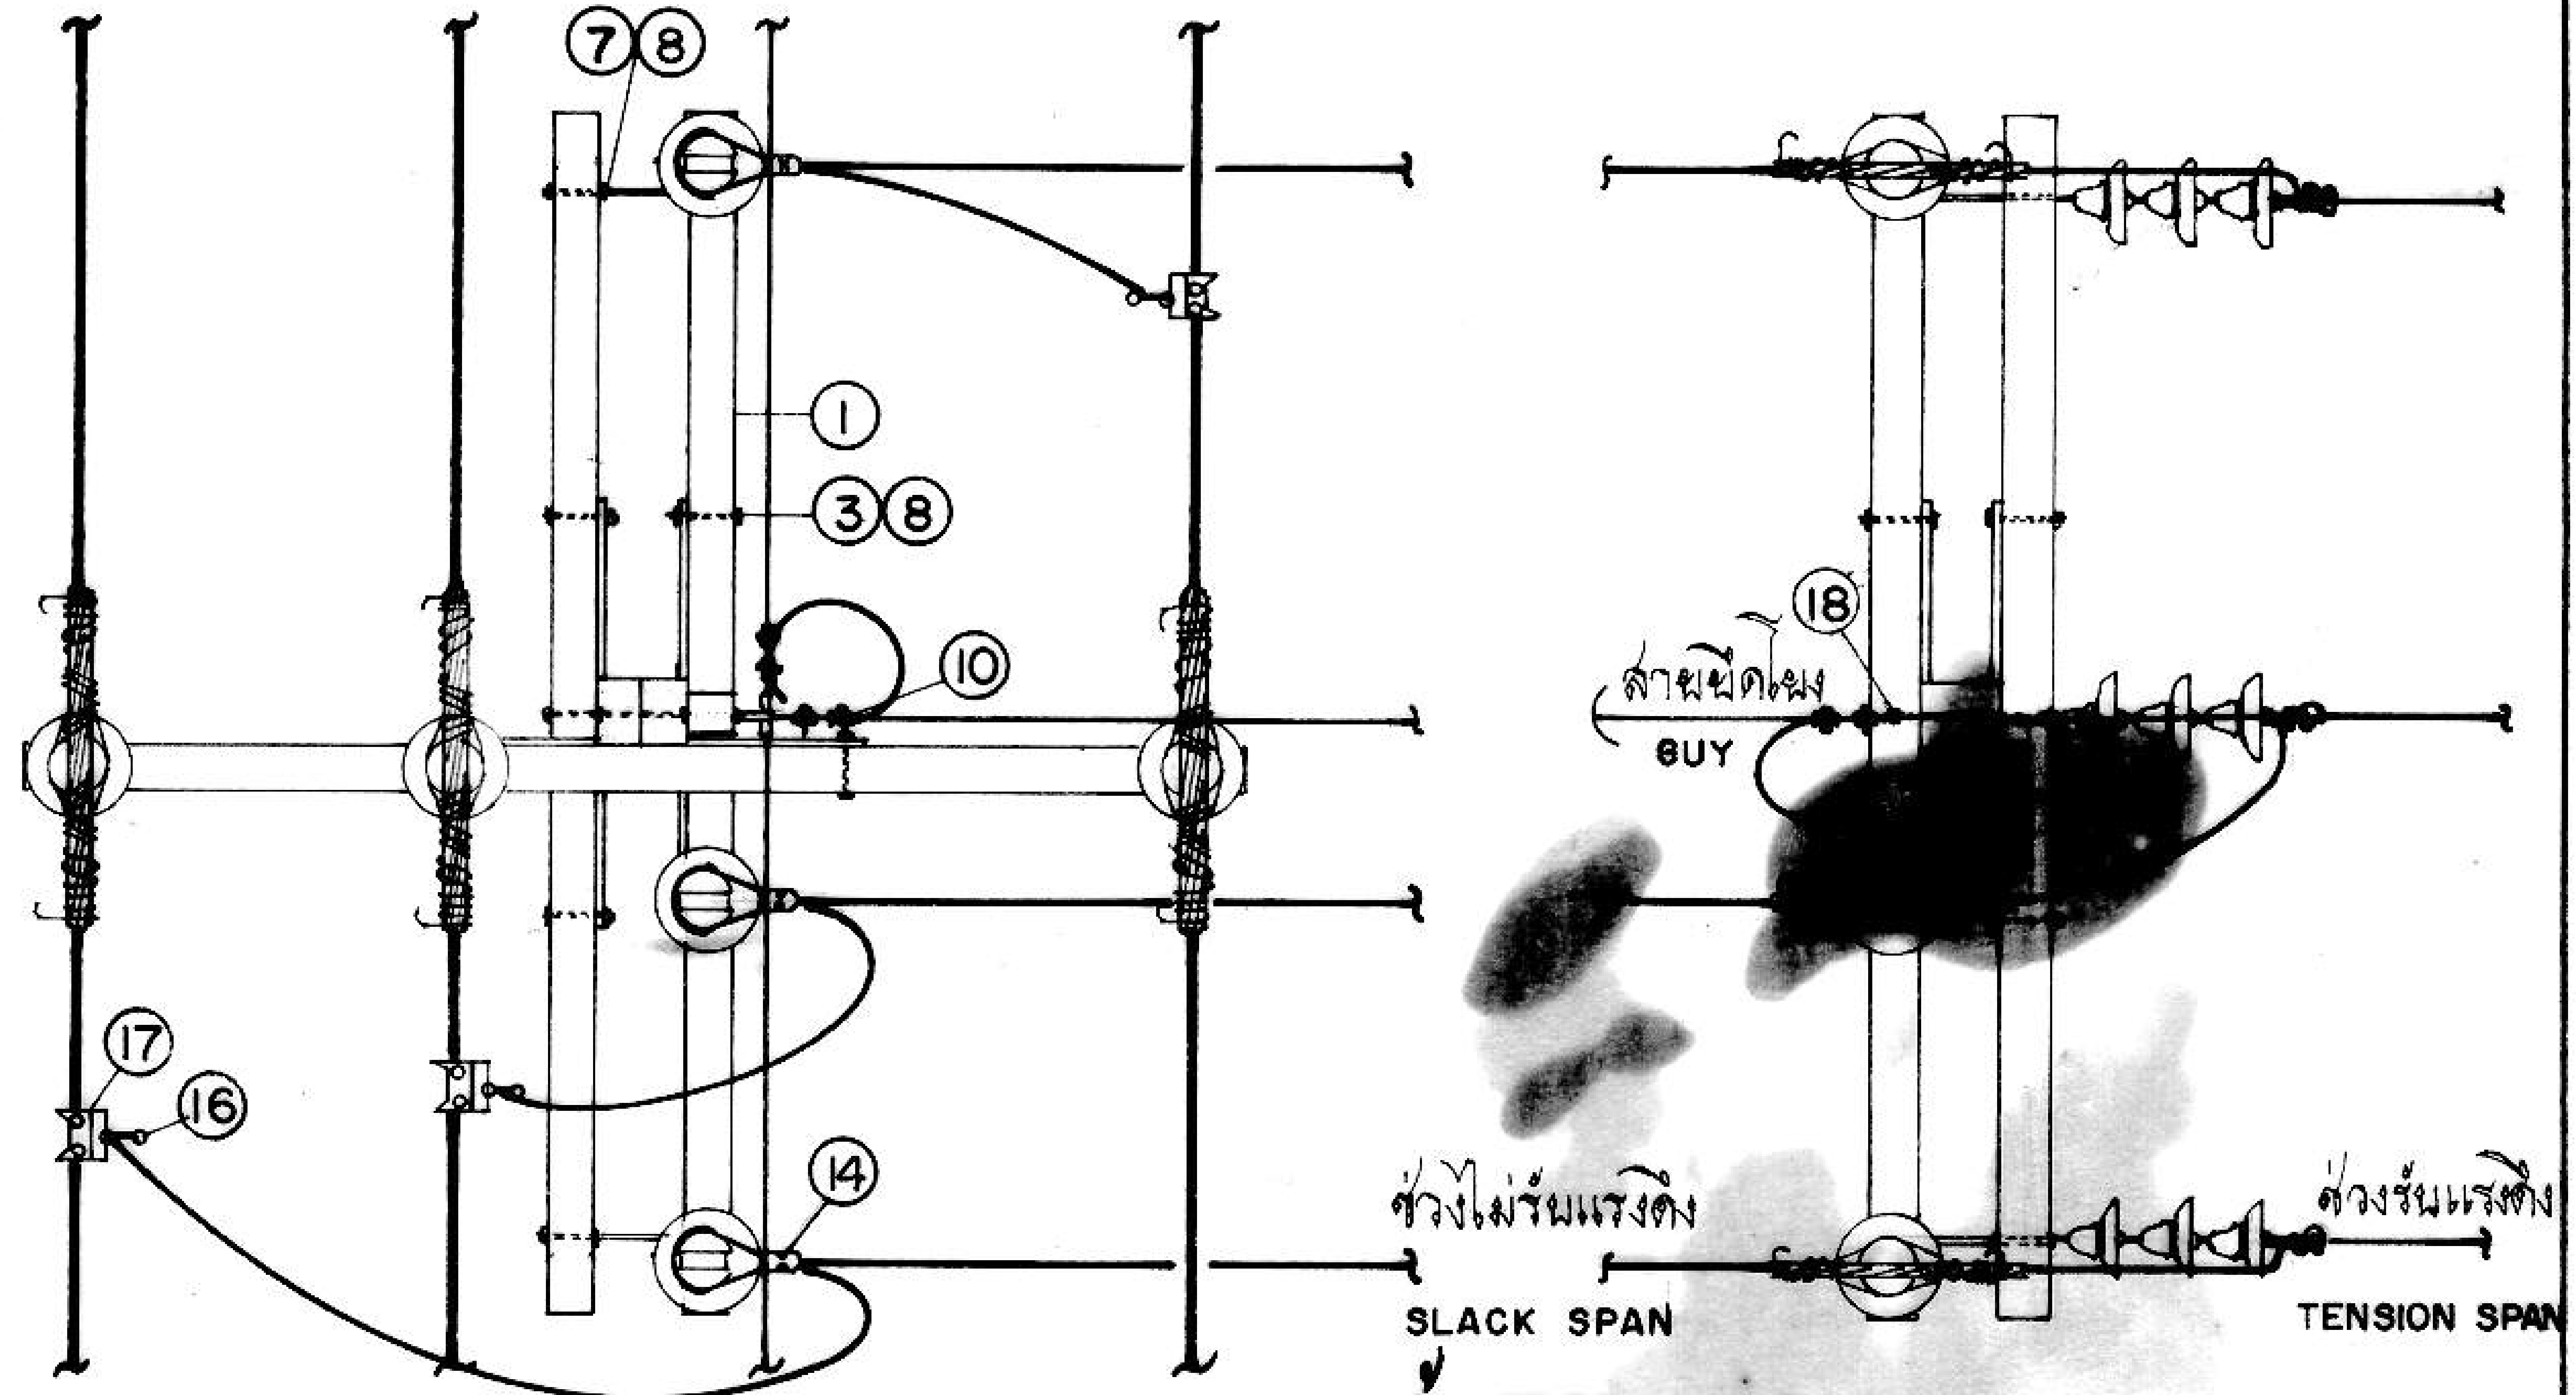

ด้านบน
TOP VIEW

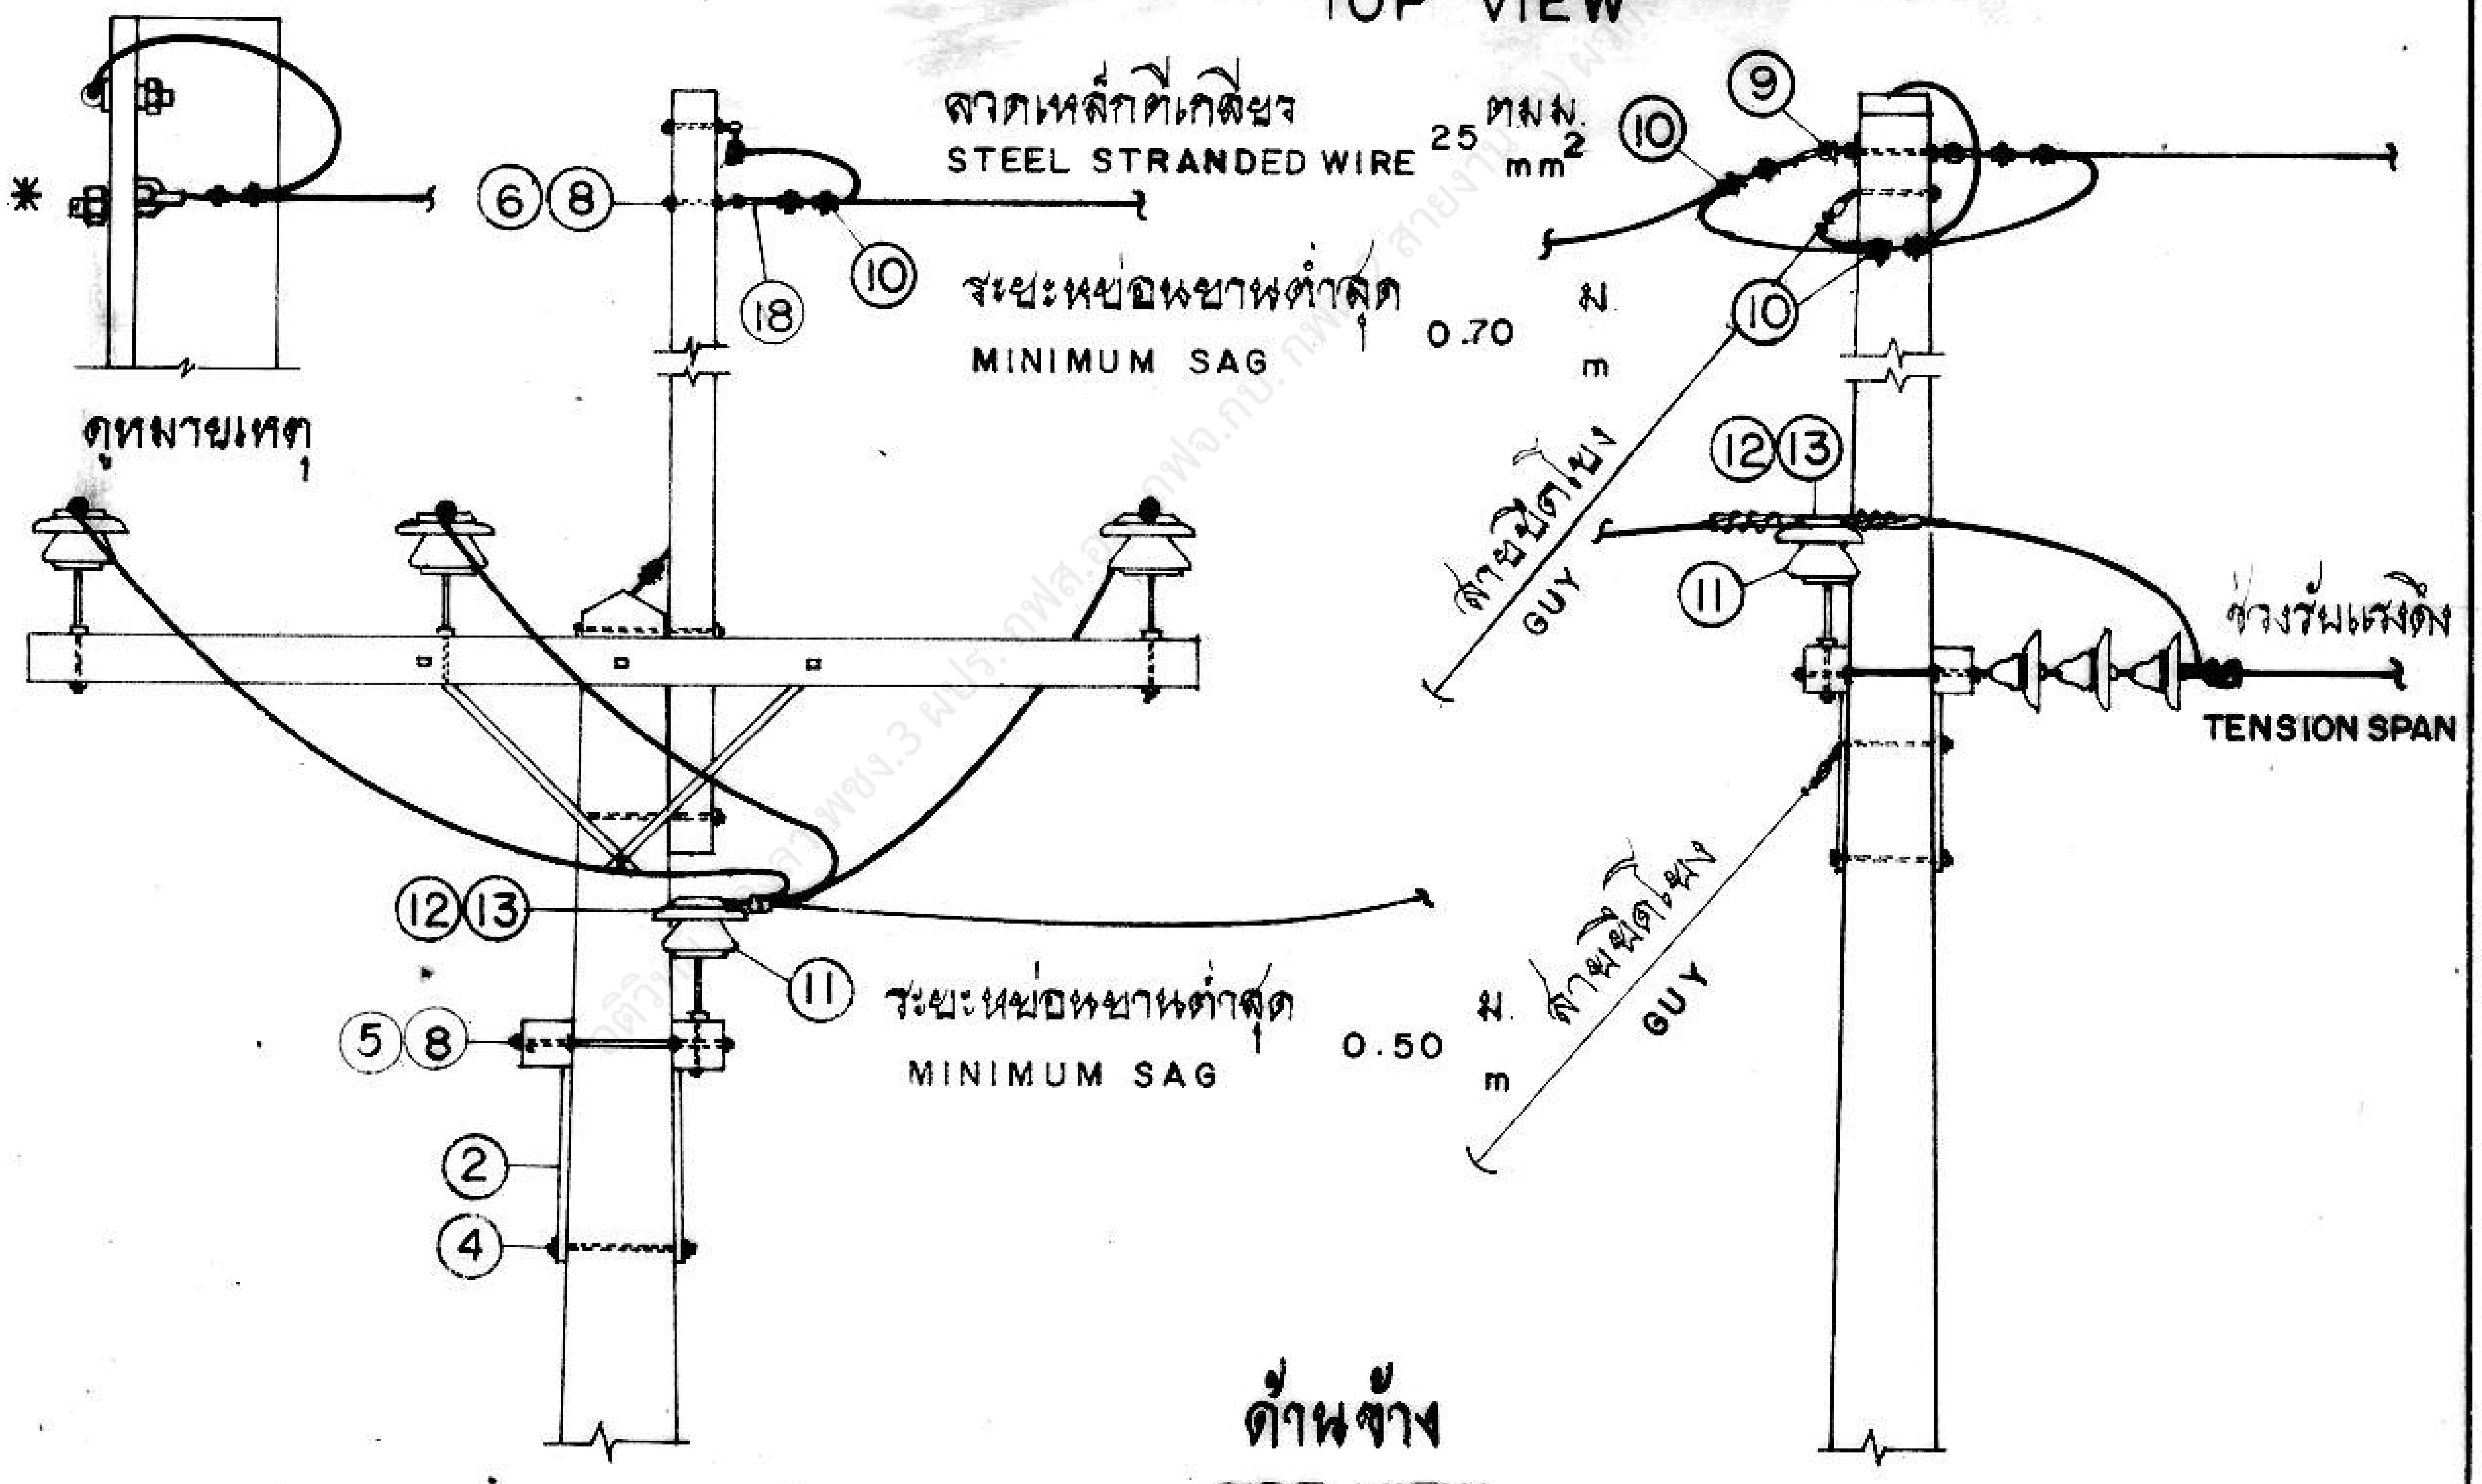

ด้านข้าง
SIDE VIEW

วงจรประธาน
MAIN CIRCUIT

วงจรย่อย
LATERAL CIRCUIT

กองวิศวกรรม

ผู้เขียน ...ชัย ...
ตรวจ.........
วิศวกร.........
หัวหน้าแผนก.........
ผู้อำนวยการกอง.........
รองผู้ว่าการฝ่ายเทคนิค.........

การไฟฟ้าส่วนภูมิภาค

ผู้ว่าการ .... 17 มิ.ย. 2519

การติดตั้งลูกถ้วยก้านตรงระบบ 33 kV
กรณีพาดสายช่วงสั้นไม่รับแรงดึง
ก ที่เสาต้นแยกสายแบบต่อสายตรง

PIN INSULATOR INSTALLATION 33 kV SYSTEM
SLACK SPAN LATERAL
A AT TAP LINE POLE WITH DIRECT CONNECTION

ใช้แทนแบบ.........
ถูกแทนโดยแบบ.........
เขียนเสร็จวันที่ 20 กพ. 19
แก้แบบวันที่.........
มิติเป็น มม.
มาตราส่วน 1 : 40
แบบเลขที่ S02-015/19011
แผ่นที่ 1 ของจำนวน 4 แผ่น

การประกอบเลขที่
ASSEMBLY NO. 3216

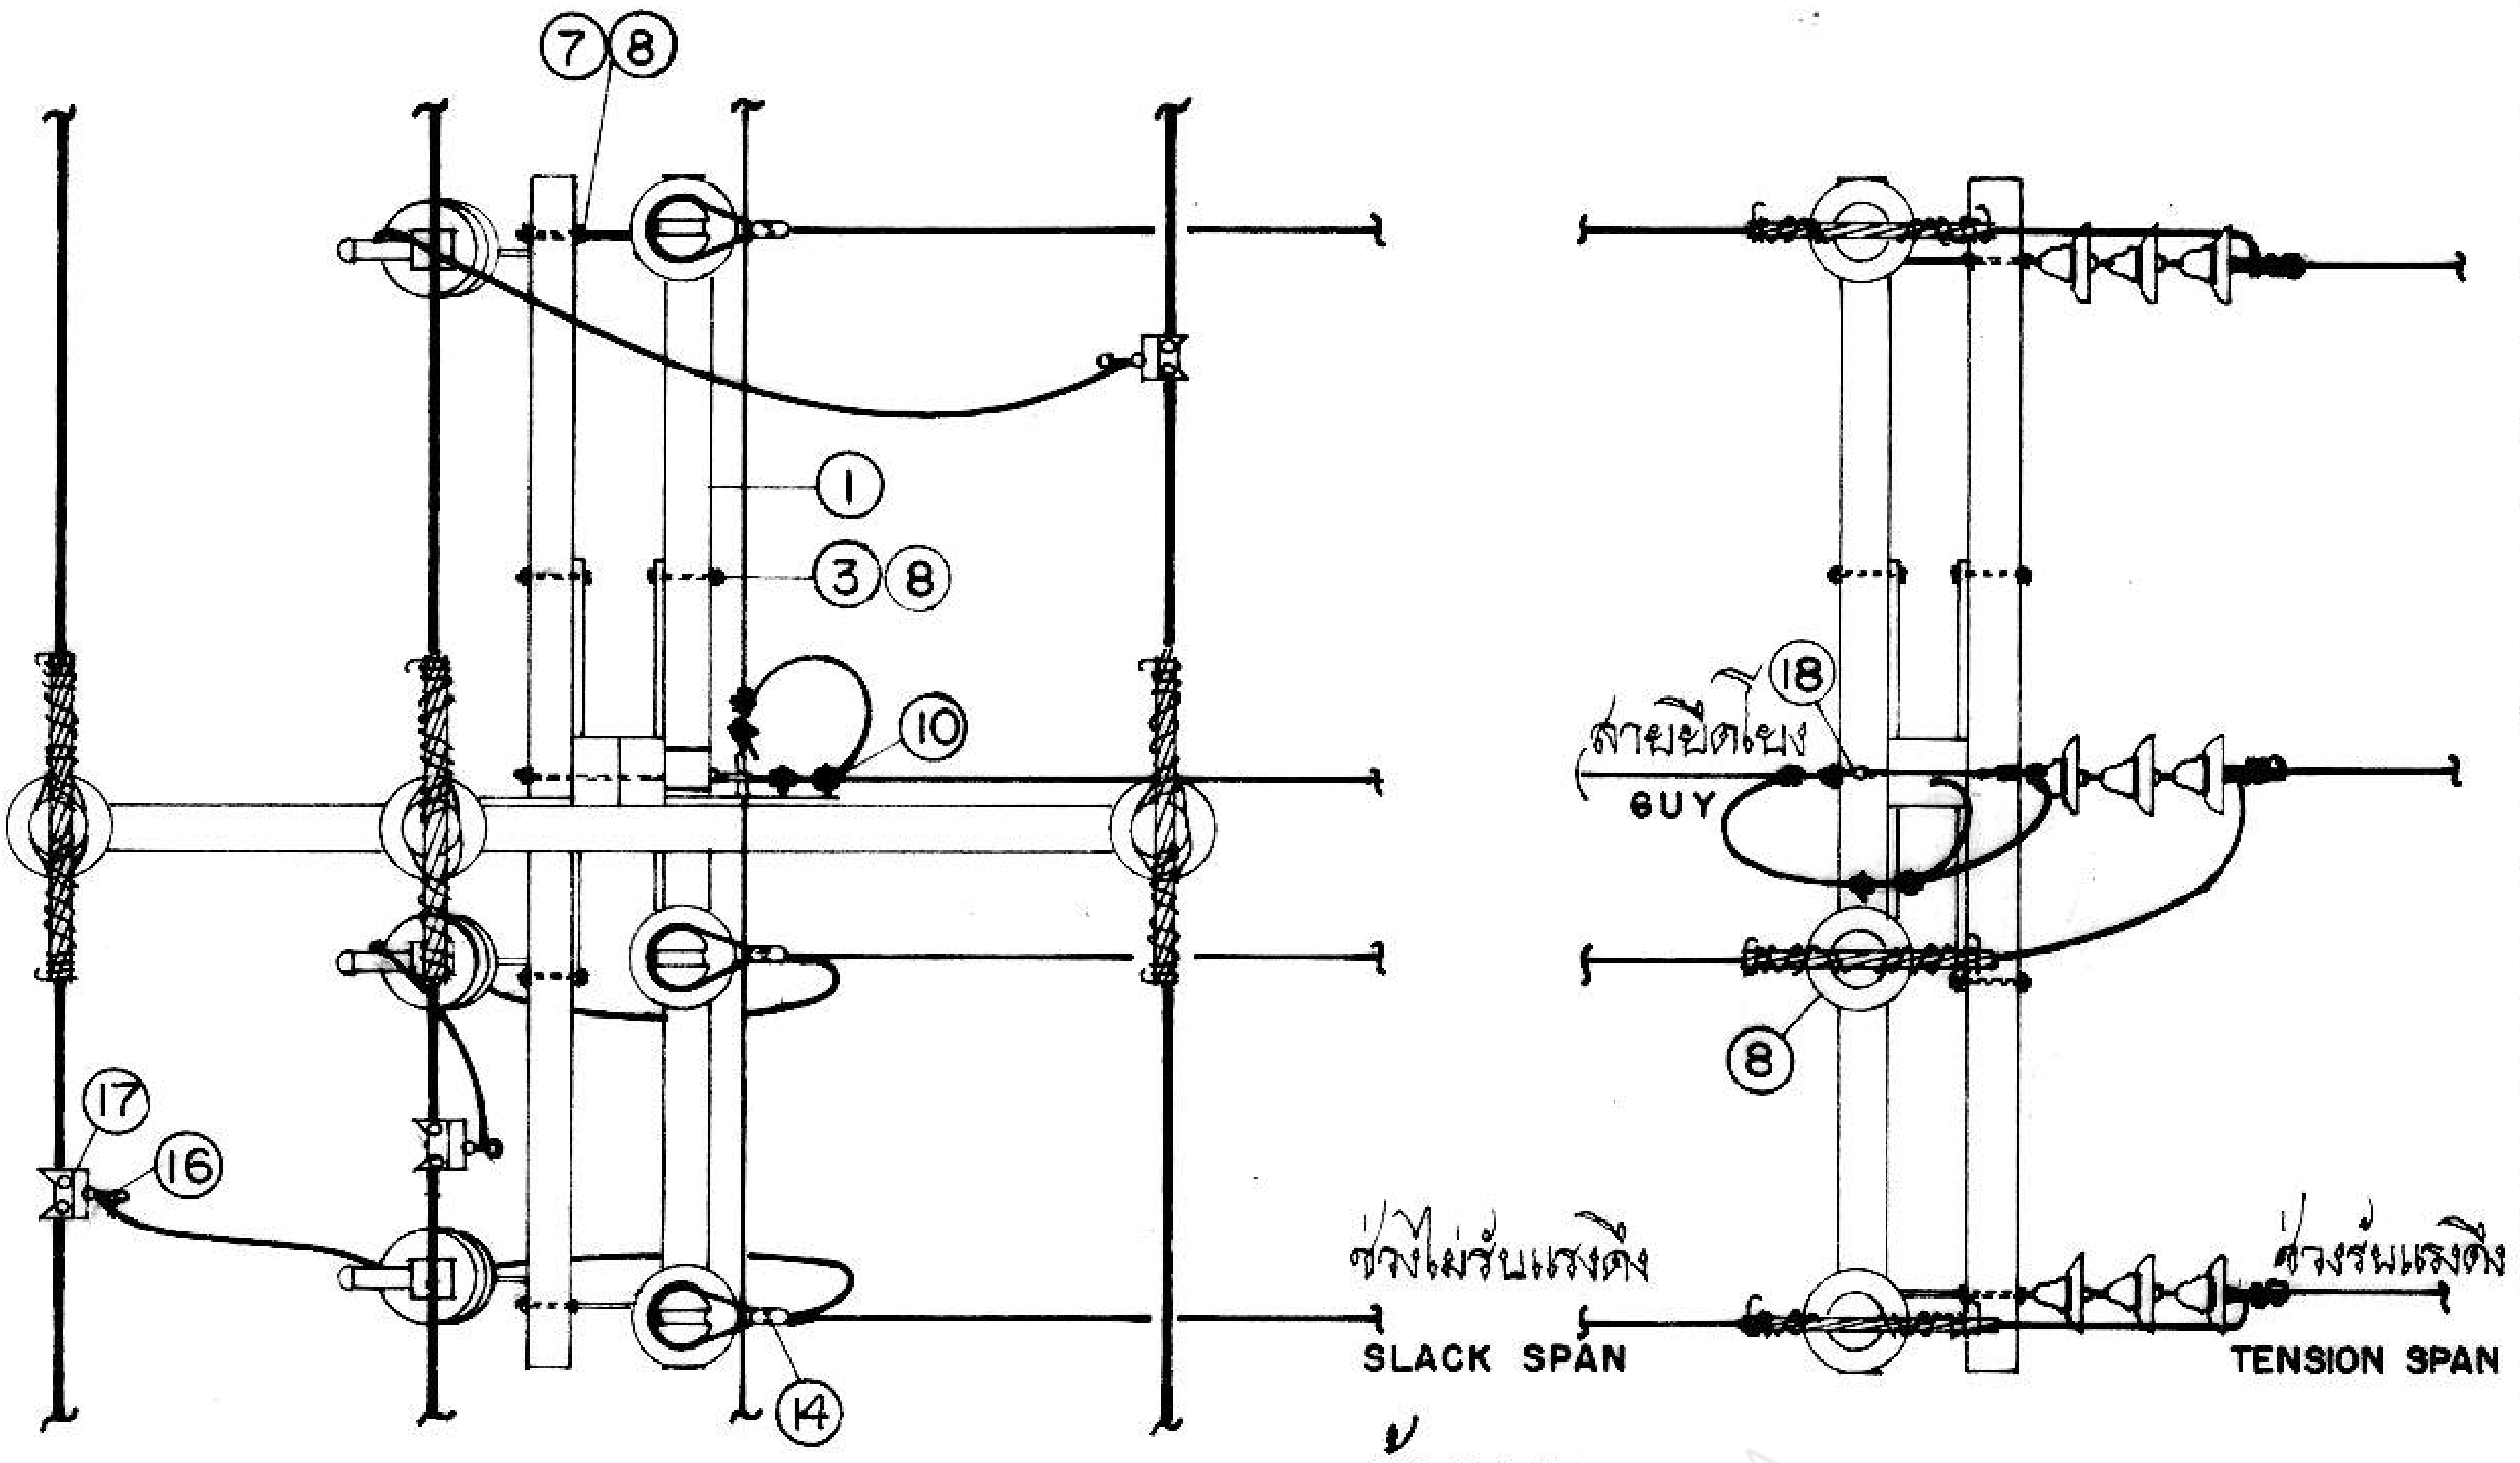

ด้านบน
TOP VIEW

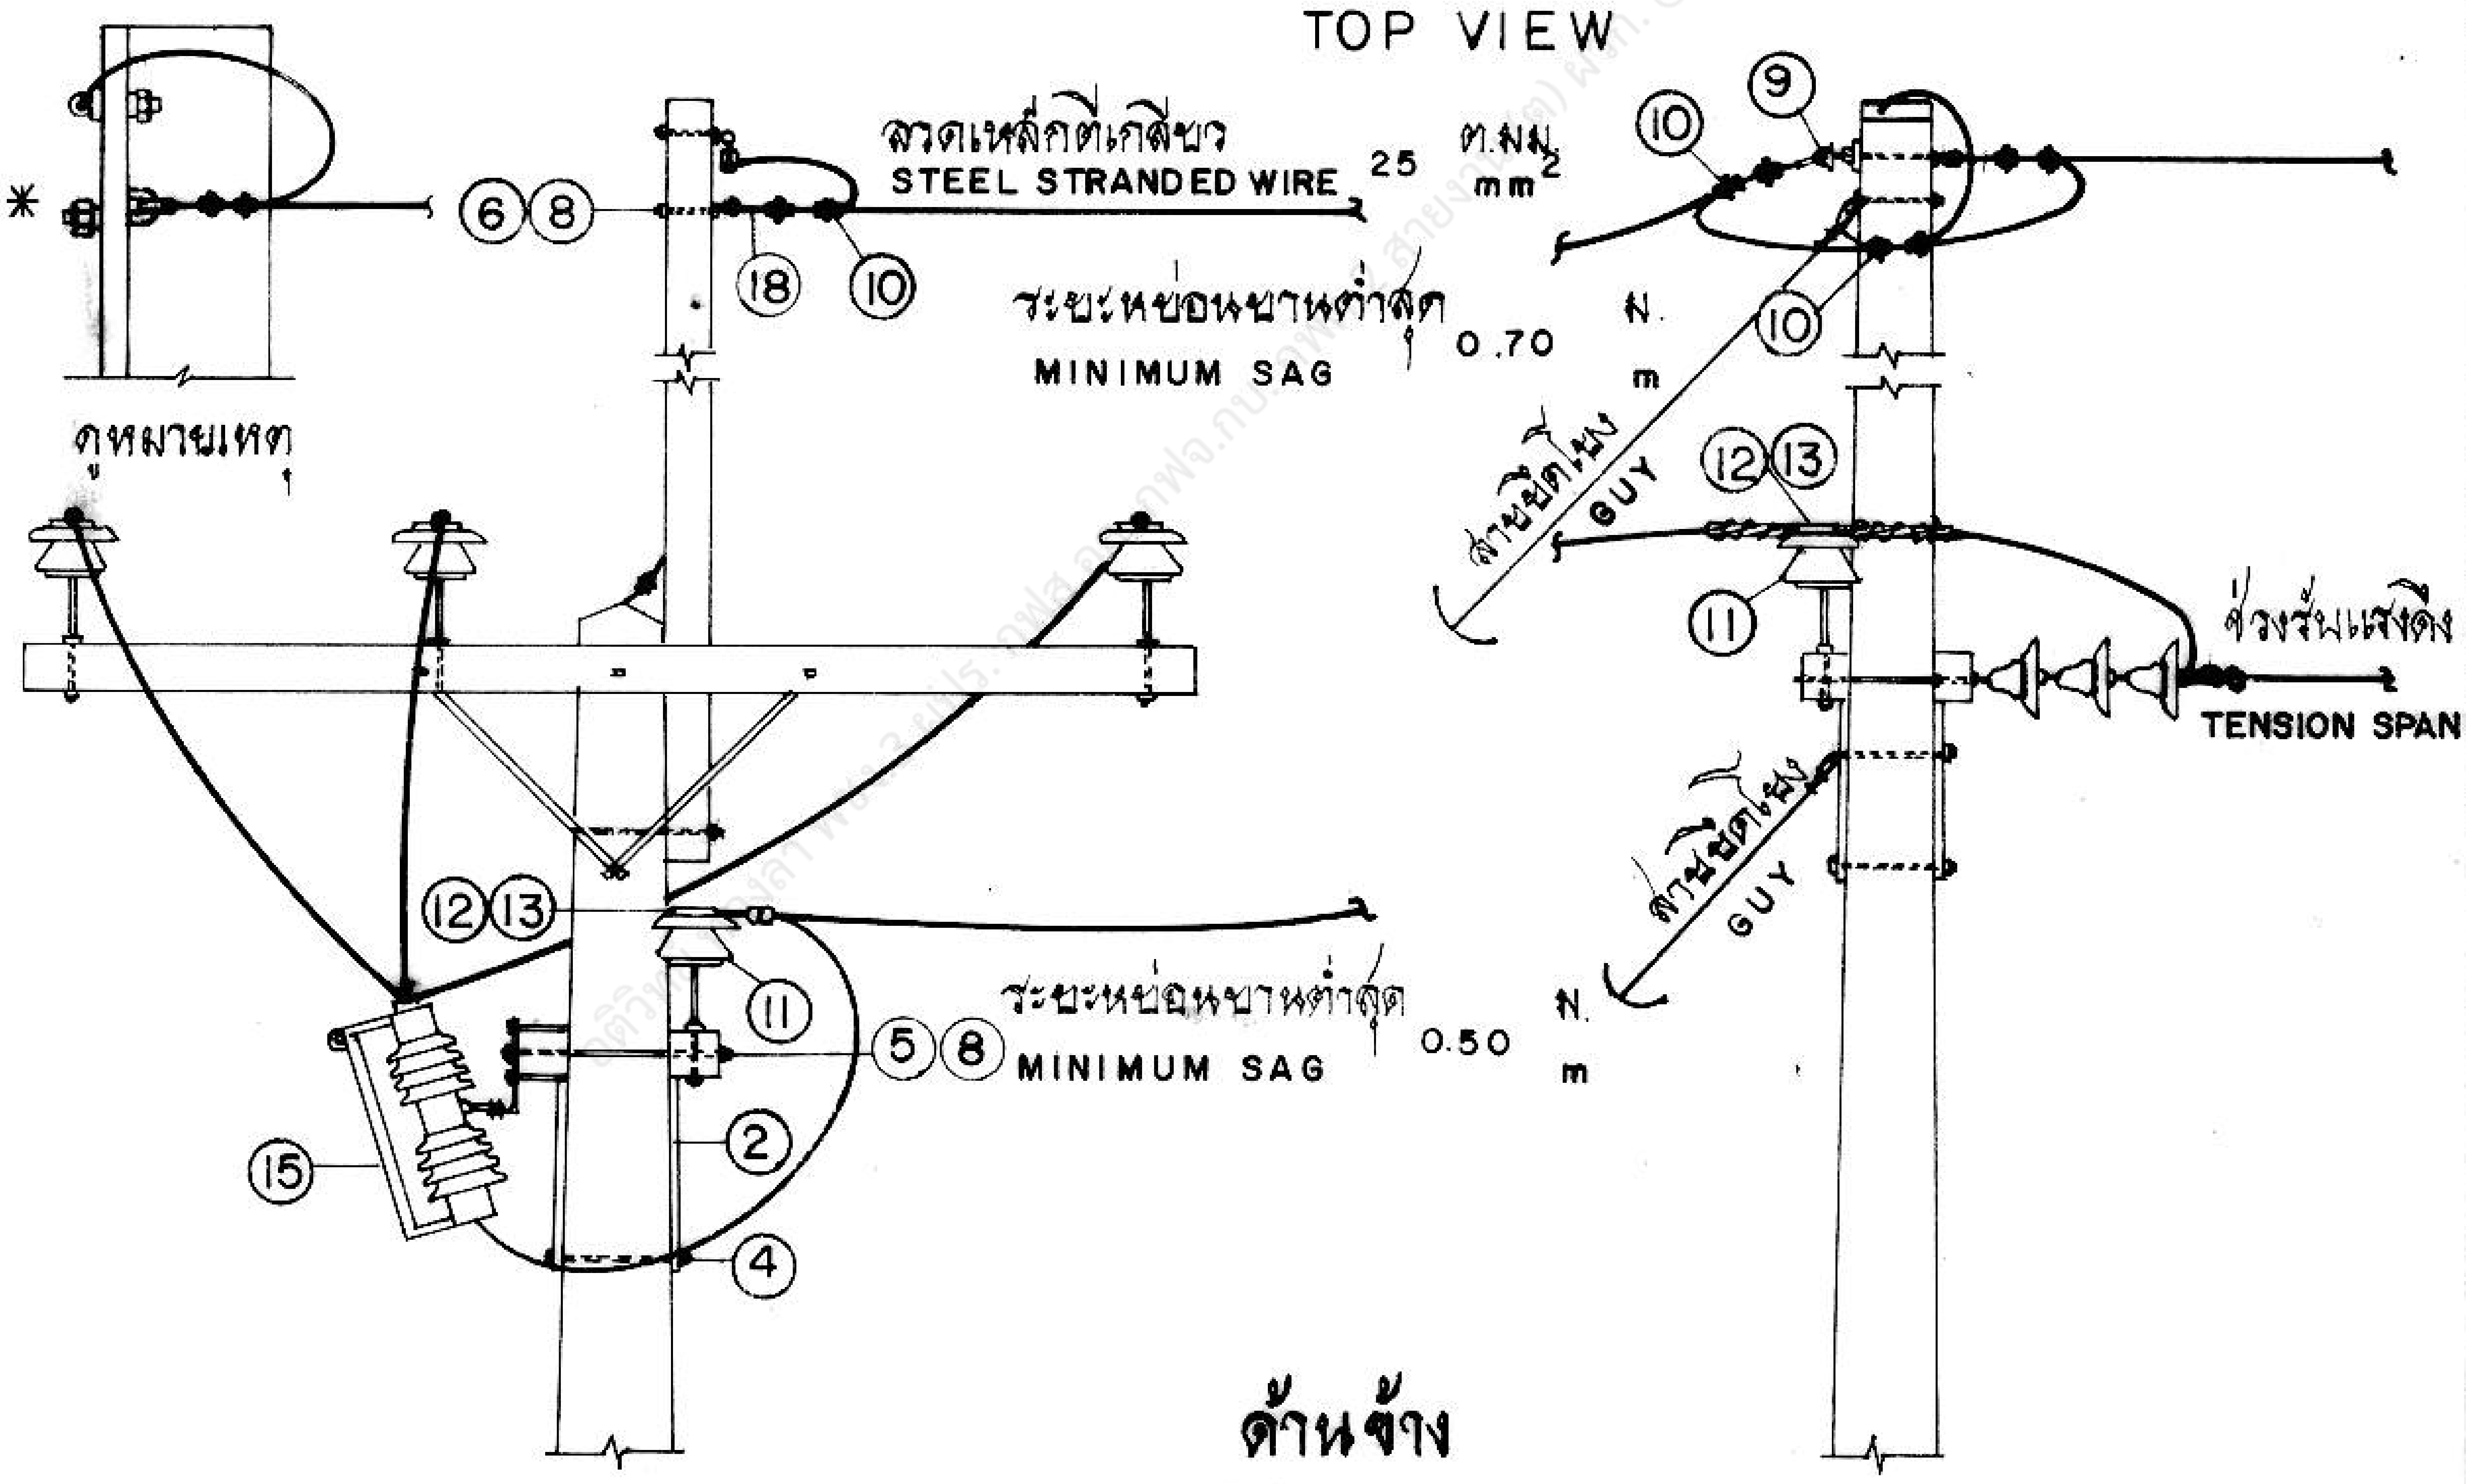

ด้านข้าง
SIDE VIEW

วงจรประธาน
MAIN CIRCUIT

วงจรย่อย
LATERAL CIRCUIT

กองวิศวกรรม

ผู้เขียน ....
สถาปนิก ....
วิศวกร ....
หัวหน้าแผนก ....
ผู้อำนวยการกอง ....
รองผู้ว่าการฝ่ายเทคนิค ....

การไฟฟ้าส่วนภูมิภาค

ผู้ว่าการ ~~12 ส.ค. 2519~~

การติดตั้งลูกถ้วยก้านตรงระบบ 33 kV
กรณีพาดสายช่วงสั้นไม่รับแรงดึง
ข ที่เสาต้นแยกสายแบบต่อผ่านคัทเอาท์

PIN INSULATOR INSTALLATION 33kV SYSTEM
SLACK SPAN LATERAL
B AT TAP LINE POLE WITH CUT-OUT CONNECTION

ใช้แทนแบบ ....
ถูกแทนโดยแบบ ....
เขียนเสร็จวันที่ 20 ก.พ. 19
แก้แบบวันที่ ....
มิติเป็น ม.ม.
มาตราส่วน 1 : 40
แบบเลขที่ S02-015/1901L
แผ่นที่ 2 ของจำนวน 4 แผ่น

การประกอบเลขที่
ASSEMBLY NO. 3216

บัญชีวัสดุ
BILL OF MATERIAL

ลำดับที่ ITEM	รายละเอียด DESCRIPTION	จำนวน REQ'D ก/A	ข/B	วัสดุเลขที่ MAT. NO.
1	ไม้คอนสายแรงสูง 100 x 120 x 3000 มม. CROSSARM, WOOD, H.T. 100 x 120 x 3000 mm.	2	2	00100003 (0101)
2	เหล็กประกับไม้คอน 40 x 6 x 1000 มม. BRACE, FLAT, FOR CROSSARM 40 x 6 x 1000 mm	4	4	01200002 (0121)
3	สลักเกลียว M 16 x 130 มม. BOLT, MACHINE, M 16 x 130 mm	4	4	01110200 (0220)
4	สลักเกลียว M 16 x 250 มม. BOLT, MACHINE, M 16 x 250 mm	1	1	01110203 (0223)
5	สลักเกลียว M 16 x 450 มม. BOLT, MACHINE, M 16 x 450 mm	1	1	01110207 (0227)
6	สลักห่วงกลม M 16 x 200 มม. BOLT, MACHINE, M 16 x 200 mm	1	1	01140001 (0253)
7	สลักเกลียวตลอด M 16 x 450 มม. BOLT, DOUBLE ARMING M 16 x 450 mm	2	2	01120001 (0244)
8	แหวนสี่เหลี่ยมแบน 52 X 52 X 4.5 มม. รู Ø 18 มม. มอก. 258 WASHER, SQUARE, FLAT 52 X 52 X 4.5 mm HOLE Ø 18 mm TIS 258	16	16	01180100 (0355)
9	นัทรูปห่วง M 16 DIN 582 NUT, EYE M 16 DIN 582	1	1	01180001 (0345)
10	ยูแคล้มสลัก 1 ตัว M 8 CLAMP, SINGLE U-BOLT, M 8	8	8	01230000 (0165)
11	ลูกถ้วยก้านตรง 33 kV มอก. 279 แบบ ค (แบบ 56-3) พร้อมก้าน INSULATOR, PIN TYPE, 33 kV, TIS 279 TYPE C (CLASS 56-3) COMP. WITH PIN	6	6	03000002 03100001
12	ลวดอะลูมิเนียมแบน 1 x 10 มม. ความยาวตามต้องการ TAPE, ARMOR, Al 1 x 10 mm LENGTH AS REQ'D			02200000 (0700)
13	ลวดอะลูมิเนียมกลม 4 มม. ความยาวตามต้องการ TIE WIRE, Al 4 mm LENGTH AS REQ'D			02200002 (0704)
14	คอนเนคเตอร์เข้าปลายสายอะลูมิเนียม ขนาดตามต้องการ CONNECTOR, DEADEND, Al SIZE AS REQ'D	3	3	02310000 or 02310001
15	ดรอพเอาท์ ฟิวส์คัทเอาท์หนึ่งอินซูเลเตอร์ 33 kV 100 แอมป์ CUTOUT, FUSE, OPEN TYPE, SINGLE INSULATOR DROP-OUT 33kV 100 A	–	3	04010100 (1426)
16	ฮอทไลน์แคล้มป์สำหรับสายอะลูมิเนียมขนาดตามต้องการ CLAMP, HOTLINE, MAIN LINE, SIZE AS REQ'D	3	3	02330100 or 02330101
17	สเตอร์รัพแคล้มป์ หรือเบลแคล้มป์ฮอทไลน์ ขนาดตามต้องการ CLAMP, STIRRUP OR BAIL, HOT LINE, MAIN LINE, Al SIZE AS REQ'D	3	3	02330000 or 02330001
18	กายทิมเบิ้ลสำหรับสายยึดโยงขนาด 50 - 95 ต.มม. THIMBLE, GUY, FOR STEEL WIRE 50 - 95 mm^2	2	2	01210304 (0150)

หมายเหตุ * ในกรณีเป็นเหล็กฉากรับสายล่อฟ้าต้องเพิ่มยูแคล้มป์สลักเดียว (วัสดุเลขที่ 01230000) 2 ตัว และกราวด์วายแคล้มป์ (วัสดุเลขที่ 01230205) 1 ตัว

กองวิศวกรรม	การไฟฟ้าส่วนภูมิภาค	ใช้แทนแบบ.......... ถูกแทนโดยแบบ.......... เขียนเสร็จวันที่ 20 ก.พ. 19
ผู้เขียน.......... สถาปนิก.......... วิศวกร.......... หัวหน้าแผนก.......... ผู้อำนวยการกอง..........	ผู้ว่าการ.......... การติดตั้งลูกถ้วยก้านตรงระบบ 33 kV กรณีพาดสายช่วงสั้นไม่รับแรงดึง ค บัญชีวัสดุ	แก้แบบวันที่.......... มิติเป็น มม. มาตราส่วน.......... แบบเลขที่ S02-015/19011
รองผู้ว่าการฝ่ายเทคนิค..........	PIN INSULATOR INSTALLATION 33 kV SYSTEM SLACK SPAN LATERAL C BILL OF MATERIAL	แผ่นที่ 3 ของจำนวน 4 แผ่น

การประกอบเลขที่
ASSEMBLY NO. 3216

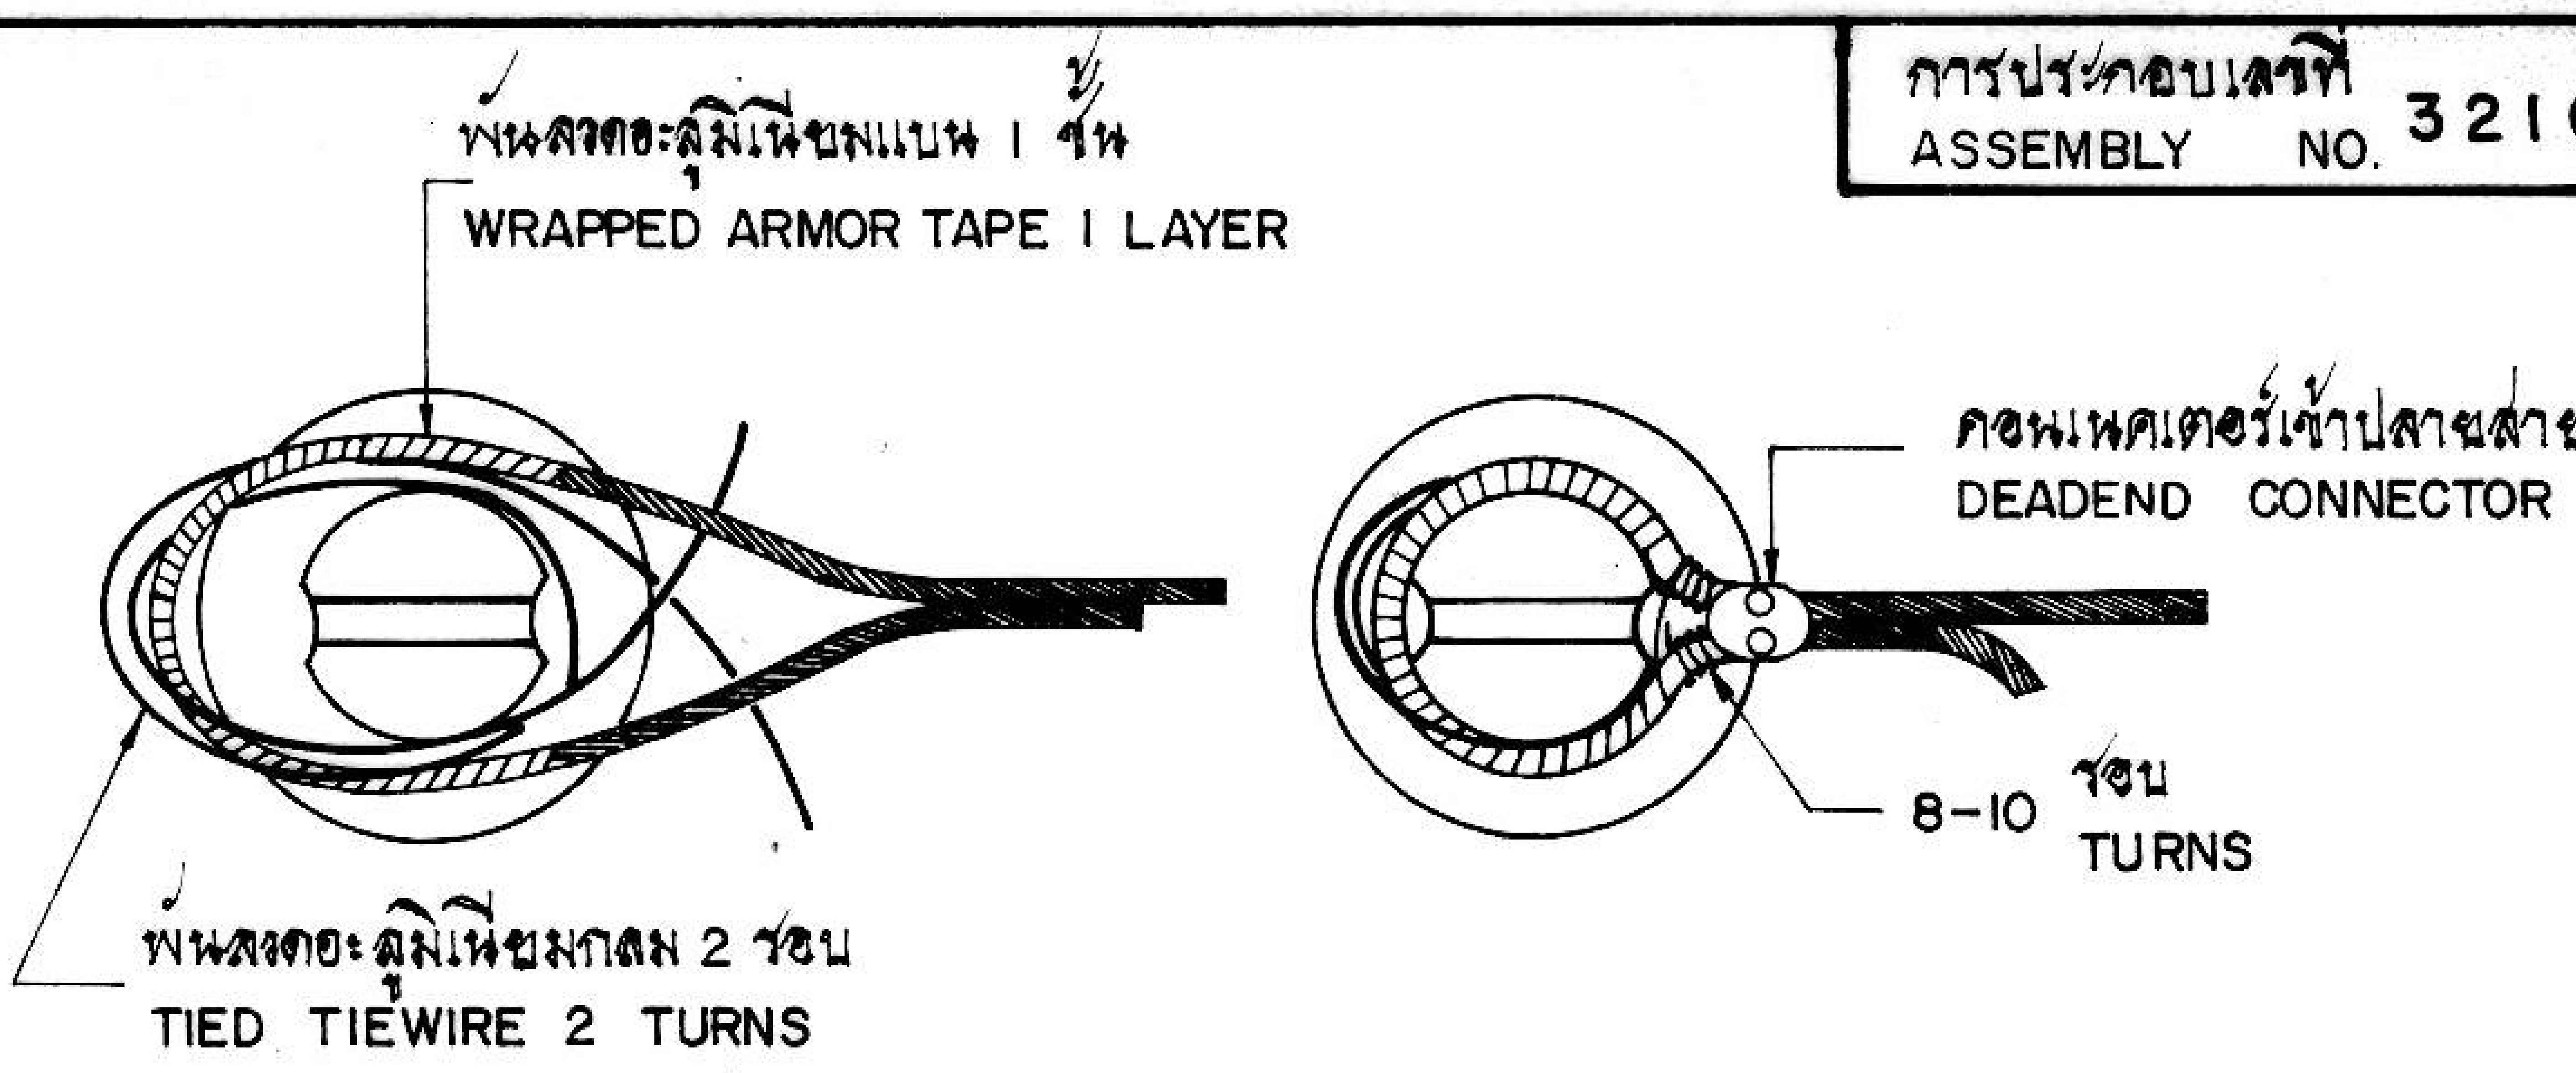
พันลวดอะลูมิเนียมแบน 1 ชั้น
WRAPPED ARMOR TAPE I LAYER
คอนเนคเตอร์เข้าปลายสาย
DEADEND CONNECTOR
8-10 รอบ
TURNS
พันลวดอะลูมิเนียมกลม 2 รอบ
TIED TIEWIRE 2 TURNS

ขั้นที่ 1
I STAGE

ขั้นสุดท้าย
FINAL STAGE

วิธีผูกลูกถ้วย
TYING METHOD

ข้อแนะนำในการติดตั้ง

1. ขนาดสายสูงสุด สายอะลูมิเนียม หรืออะลูมิเนียมอัลลอย 50 ต.มม.
   สายอะลูมิเนียมแกนเหล็ก 35/6 ต.มม.
2. ระยะระหว่างเสาช่วงไม่รับแรงดึงไม่เกิน 20 ม.
3. ให้พันลวดอะลูมิเนียมแบนรอบสายไฟหนึ่งชั้น แล้วใช้ลวดอะลูมิเนียมกลมพันรอบลูกถ้วยและสายไฟ พร้อมกับใช้คอนเนคเตอร์เข้าปลายสาย 1 ชุด จับสายไฟให้ใกล้ลูกถ้วยมากที่สุด

INSTALLATION SUGGESTION

1. CONDUCTOR, MAXIMUM SIZE ; Al OR Al-ALLOY 50 mm^2
   ACSR 35/6 mm^2
2. MAXIMUM SLACK SPAN LATERAL 20 m.
3. CONDUCTOR SHOULD BE WRAPPED WITH ALUMINIUM ARMOR TAPE ONE LAYER AND TIED WITH TIE WIRE. THE CONDUCTOR SHOULD BE CLAMPED WITH DEADEND CONNECTOR CLOSE TO INSULATOR.

กองวิศวกรรม	การไฟฟ้าส่วนภูมิภาค	ใช้แทนแบบ ถูกแทนโดยแบบ เขียนเสร็จวันที่ 20 กพ. 19 แก้แบบวันที่ ผลิตเป็น มาตราส่วน
ผู้เขียน สถาปนิก วิศวกร หัวหน้าแผนก ผู้อำนวยการกอง	ผู้ว่าการ 12 มิ.ย. 2519	
	การติดตั้งลูกถ้วยก้านตรงระบบ 33 kV กรณีพาดสายช่วงสั้นไม่รับแรงดึง ง ข้อแนะนำในการติดตั้ง	
รองผู้ว่าการฝ่ายเทคนิค	PIN INSULATOR INSTALLATION 33 kV SYSTEM SLACK SPAN LATERAL D INSTALLATION SUGGESTION	แบบเลขที่ S02-015/19011 แผ่นที่ 4 ของจำนวน 4 แผ่น

12 มิ.ย. 2519