การประกอบเลขที่ **5358**
ASSEMBLY NO.

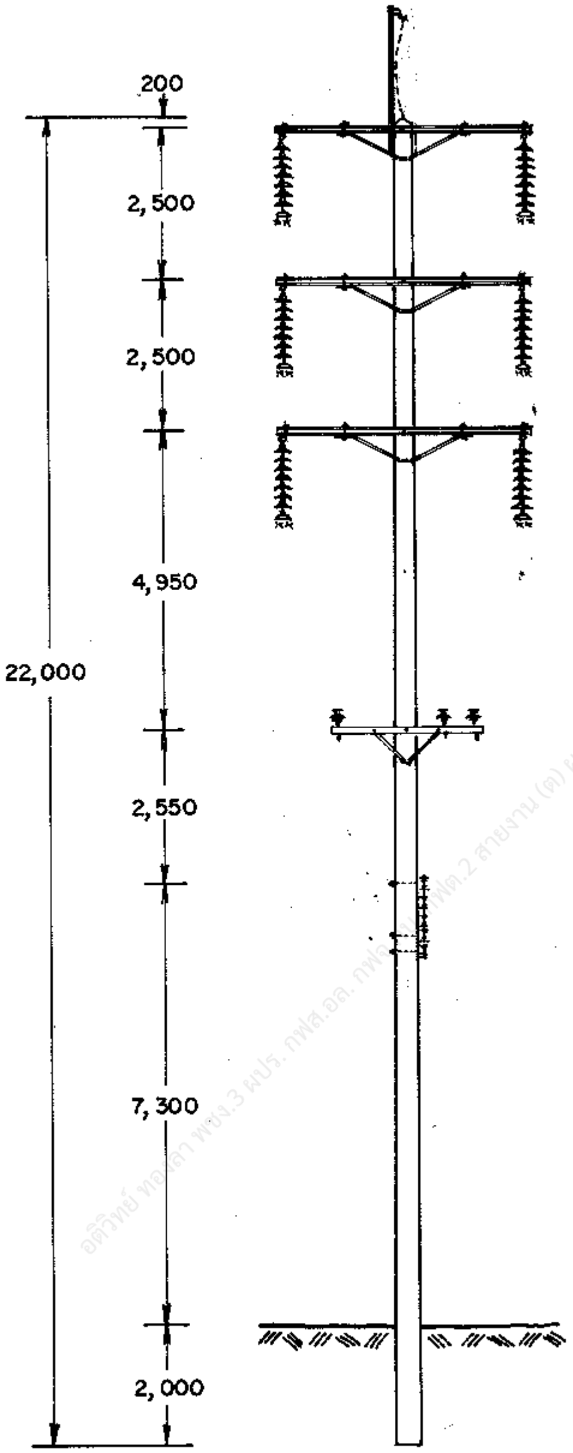

อดิวิทย์ ทองลา พชง.3 ผปร. กฟส.อล. กฟ[illegible] กฟต.2 สายงาน (ต) ผวก. @PEA

กองวิศวกรรมไฟฟ้าและเครื่องกล ฝ่ายวิศวกรรม	**การไฟฟ้าส่วนภูมิภาค**	ใช้แทนแบบ ________ ถูกแทนโดยแบบ ________
ผู้เขียน __ อัพฯถ. __ ผู้ตรวจ ________ วิศวกร ________ หัวหน้าแผนก ________ ผู้อำนวยการกอง ________ ผู้อำนวยการฝ่าย ________	ผู้ว่าการ ________ 5 ส.ค. 2537 115 kV วงจรคู่ สายไฟฟ้าคู่ เสาสำหรับทางตรง แบบ DD-TG-3	เขียนเสร็จวันที่ 15 ธค. 2536 แก้แบบวันที่ ________ มิติเป็น มิลลิเมตร มาตราส่วน 1 : 125
รองผู้ว่าการฝ่ายเทคนิค ผู้ เรื่องแทน	115kV DOUBLE CIRCUIT DOUBLE CONDUCTOR TANGENT STRUCTURE TYPE DD-TG-3	แบบเลขที่ SAI-015/36004 แผ่นที่ 1 ของจำนวน 3 แผ่น

การประกอบเลขที่
ASSEMBLY NO. **5358**

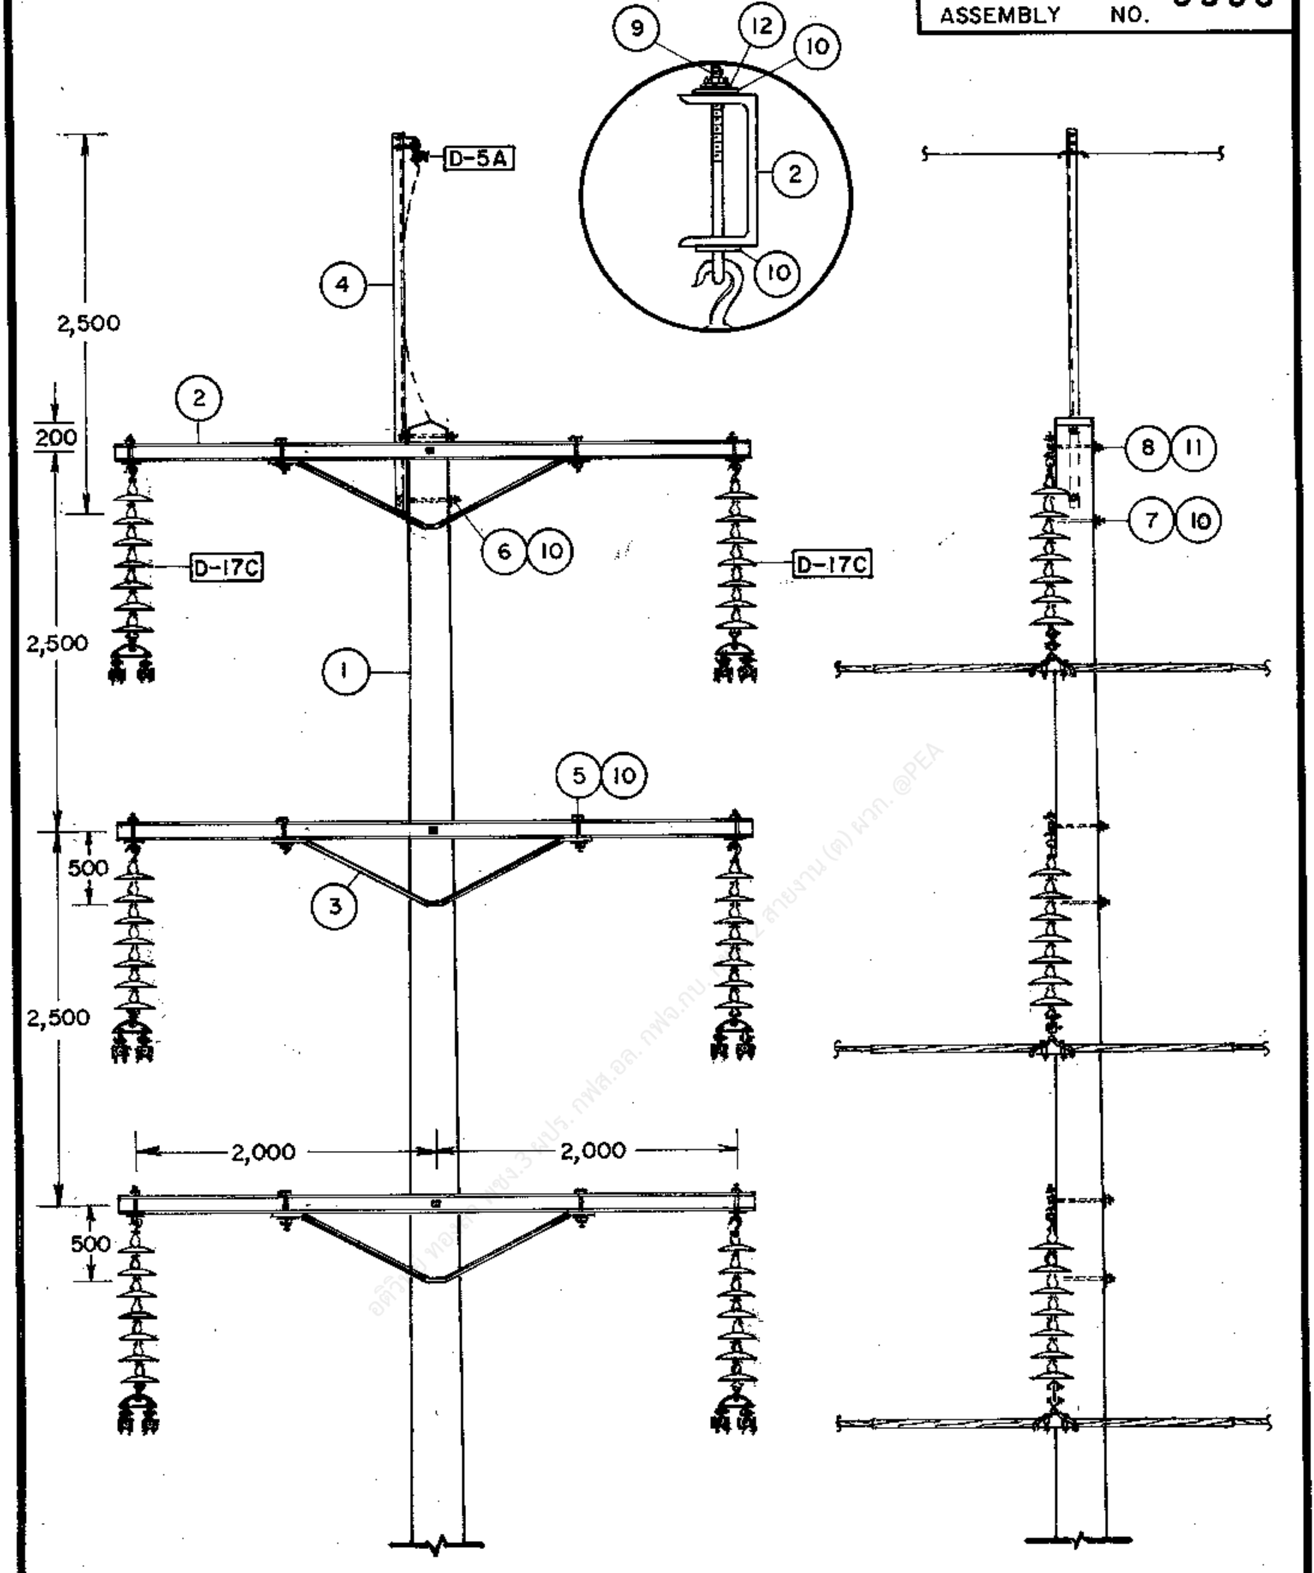

กองวิศวกรรมไฟฟ้าและเครื่องกล
ฝ่ายวิศวกรรม

ผู้เขียน ________
ผู้สำรวจ ________
วิศวกร ________
หัวหน้าแผนก ________
ผู้อำนวยการกอง ________
ผู้อำนวยการฝ่าย ________

รองผู้ว่าการฝ่ายเทคนิค

การไฟฟ้าส่วนภูมิภาค

5 ม.ค. 2537

ผู้ว่าการ ________

115 kV วงจรคู่ สายไฟฟ้าคู่
เสาสำหรับทางตรง
แบบ DD-TG-3

115 kV DOUBLE CIRCUIT DOUBLE CONDUCTOR
TANGENT STRUCTURE
TYPE DD-TG-3

ใช้แทนแบบ ________
ถูกแทนโดยแบบ ________
เขียนเสร็จวันที่ 15 ธค. 2536
แก้แบบวันที่ ________
มิติเป็น มิลลิเมตร
มาตราส่วน 1 : 50

แบบเลขที่ SAI-015/36004
แผ่นที่ 2 ของจำนวน 3 แผ่น

การประกอบเลขที่ ASSEMBLY NO. **5358**

บัญชีวัสดุ
BILL OF MATERIAL

ลำดับที่ ITEM	รายละเอียด DESCRIPTION	จำนวน REQ'D	วัสดุเลขที่ MAT. NO.
1	เสาคอนกรีต 22 ม. POLE, CONCRETE 22 m LONG	1	00010011 (0041)
2	คอนสายแบบเหล็กรูปรางน้ำ ขนาด 100X50X5 มม. ยาว 4.20 ม. มอก. 116 CROSSARM, STEEL, CHANNEL 100X50X5 mm, 4.20 m LONG, TIS 116	3	
3	เหล็กฉากรับคอนสาย ขนาด 50X50X6 มม. ช่วงกว้าง 1,800 มม. ดรอพ 450 มม. BRACE, ANGLE STEEL, 50X50X6 mm, 1,800 mm WIDE, 450 mm DROP	3	01200007 (0119)
4	เหล็กฉากรับสายล่อฟ้าทางตรง ยาว 2.50 ม. OVERHEAD GROUND WIRE BAYONET, 2.50 m LONG	1	01010004 (0135)
5	สลักเกลียว M 16X130 มม. BOLT, MACHINE, M 16X130 mm	6	01110200 (0220)
6	สลักเกลียว M 16X300 มม. BOLT, MACHINE, M 16X300 mm	2	01110204 (0224)
7	สลักเกลียว M 16X350 มม. BOLT, MACHINE, M 16X350 mm	3	01110205 (0225)
8	สลักเกลียว M 20X350 มม. BOLT, MACHINE, M 20X350 mm	3	01110300
9	สลักห่วงโอแวล M 16X150 มม. BOLT, OVAL EYE, M 16X150 mm	6	01150000 (0257)
10	แหวนสี่เหลี่ยมแบน 52X52X4.5 มม. รู Ø 18 มม. มอก. 258 WASHER, SQUARE, FLAT 52X52X4.5 mm, HOLE Ø 18 mm, TIS 258	23	01180100 (0355)
11	แหวนสี่เหลี่ยมแบน 62X62X6 มม. รู Ø 22 มม. มอก. 258 WASHER, SQUARE, FLAT 62X62X6 mm, HOLE Ø 22 mm, TIS 258	6	01180101 (0356)
12	แหวนสปริง M 16 มอก. 259 WASHER, LOCK, M 16, TIS 259	6	01180301 (0365)
D-17C	การประกอบลูกถ้วยแขวน SUSPENSION INSULATOR ASSEMBLY	6	
D-5A	การต่อสายล่อฟ้า OVERHEAD GROUND WIRE CONNECTION	1	
D-10A	ฐานรากเสา POLE FOUNDATION	1	

กองวิศวกรรมไฟฟ้าและเครื่องกล
ฝ่ายวิศวกรรม

ผู้เขียน
ผู้สำรวจ
วิศวกร
หัวหน้าแผนก
ผู้อำนวยการกอง
ผู้อำนวยการฝ่าย

รองผู้ว่าการฝ่ายเทคนิค

การไฟฟ้าส่วนภูมิภาค

5 มค. 2537

ผู้ว่าการ

115 kV วงจรคู่ สายไฟฟ้าคู่
เสาสำหรับทางตรง
แบบ DD-TG-3

115 kV DOUBLE CIRCUIT DOUBLE CONDUCTOR
TANGENT STRUCTURE
TYPE DD-TG-3

ใช้แทนแบบ
ถูกแทนโดยแบบ
เขียนเสร็จวันที่ 15 ธค. 2536
แก้แบบวันที่
มิติเป็น
มาตราส่วน

แบบเลขที่ SAI-015/36004
แผ่นที่ 3 ของจำนวน 3 แผ่น