

การประกอบเลขที่ ASSEMBLY NO. 3234

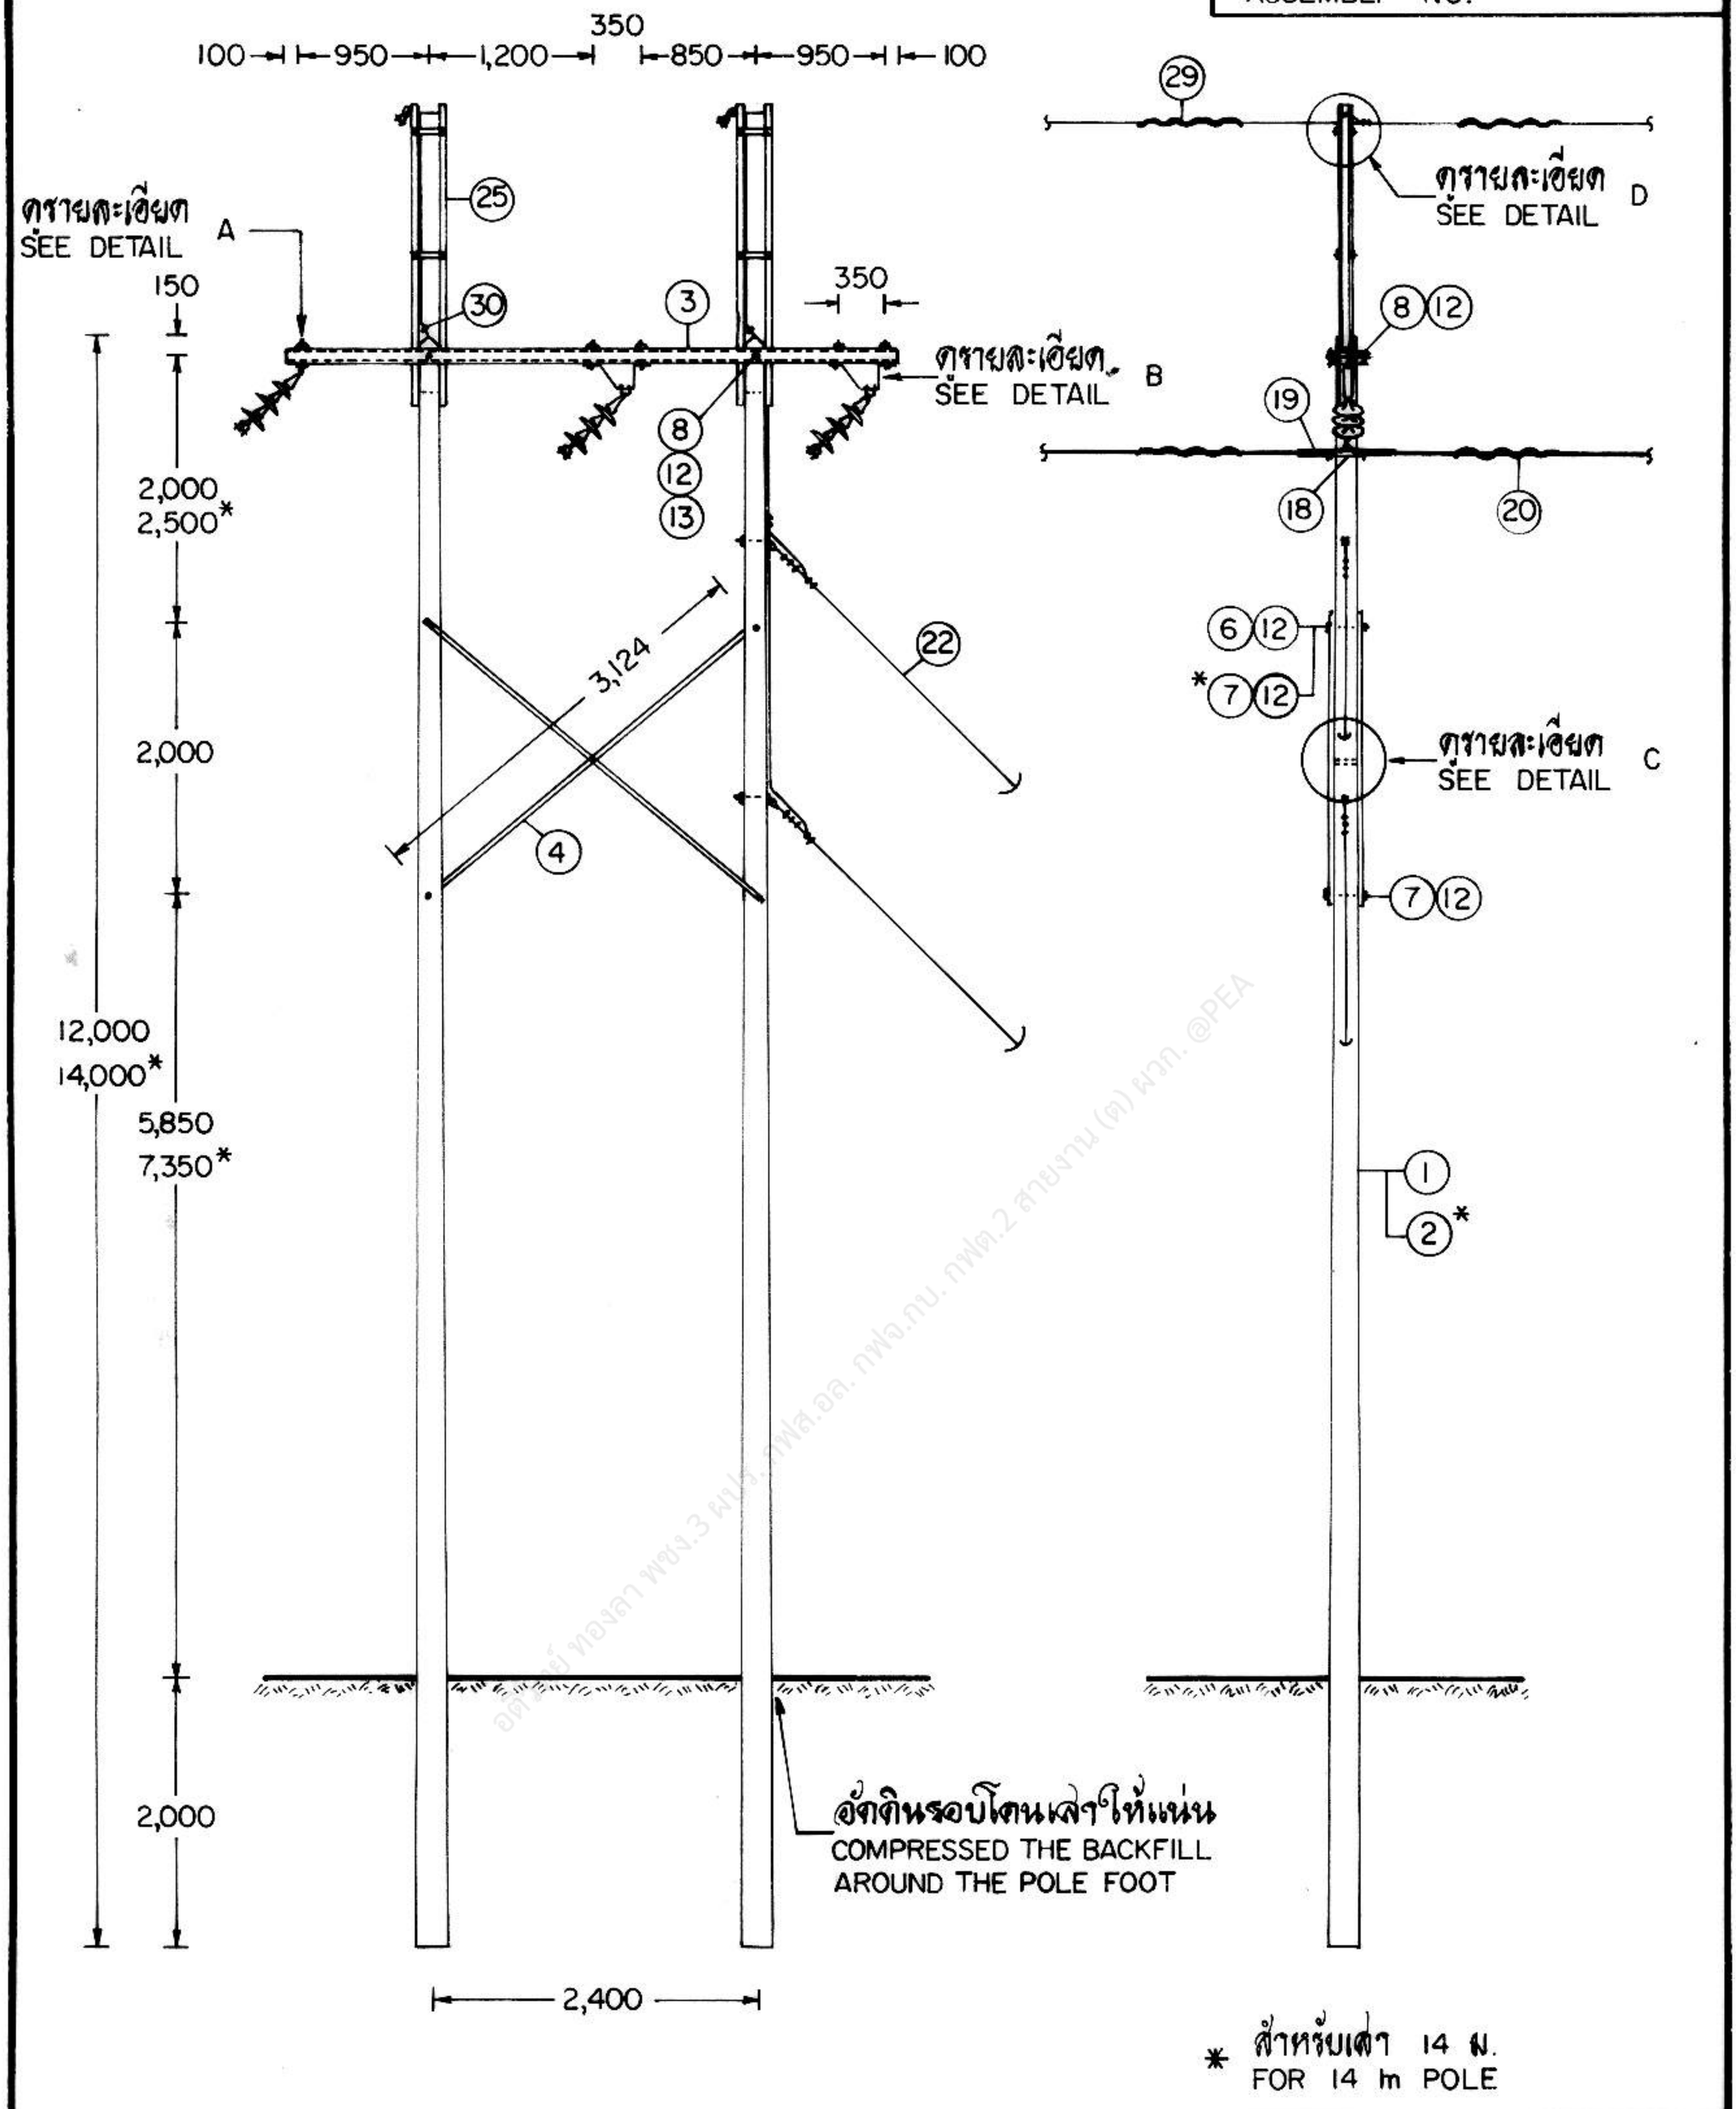


กองวิศวกรรมไฟฟ้าและเครื่องกล ฝ่ายวิศวกรรม	**การไฟฟ้าส่วนภูมิภาค**	ใช้แทนแบบ ถูกแทนโดยแบบ เขียนเสร็จวันที่ 20 ส.ค. 34 แก้แบบวันที่ มิติเป็น มิลลิเมตร มาตราส่วน 1:75
ผู้เขียน ผู้สำรวจ วิศวกร หัวหน้าแผนก ผู้อำนวยการกอง ผู้อำนวยการฝ่าย	ผู้ว่าการ 16 ก.ย 34	
	โครงสร้างเสาคู่ สำหรับแรงสายไฟฟ้า ระบบ 33 kV ช่วงเสา 120 – 200 ม. มุม > 5°- 30°	
ของผู้ว่าการฝ่ายเทคนิค	33 kV, H-FRAME SUSPENSION STRUCTURE SPAN 120 – 200 m LINE ANGLE > 5°- 30°	แบบเลขที่ SAI-015/34020 แผ่นที่ 1 ของจำนวน 5 แผ่น

12 ก.ย. 2534


การประกอบเลขที่ 3234
ASSEMBLY NO.

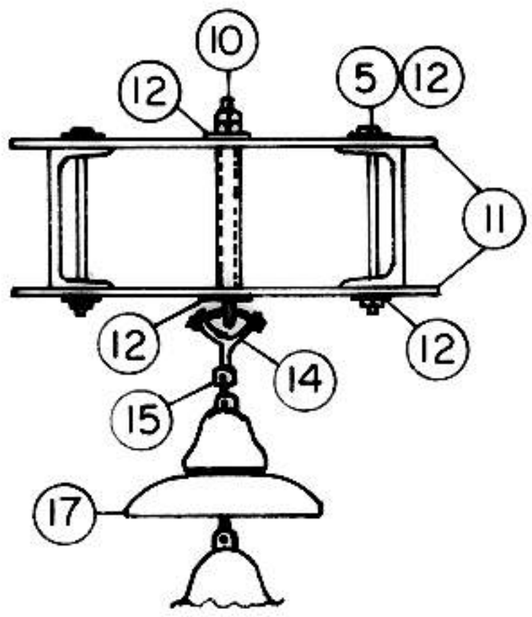


รายละเอียด A
DETAIL

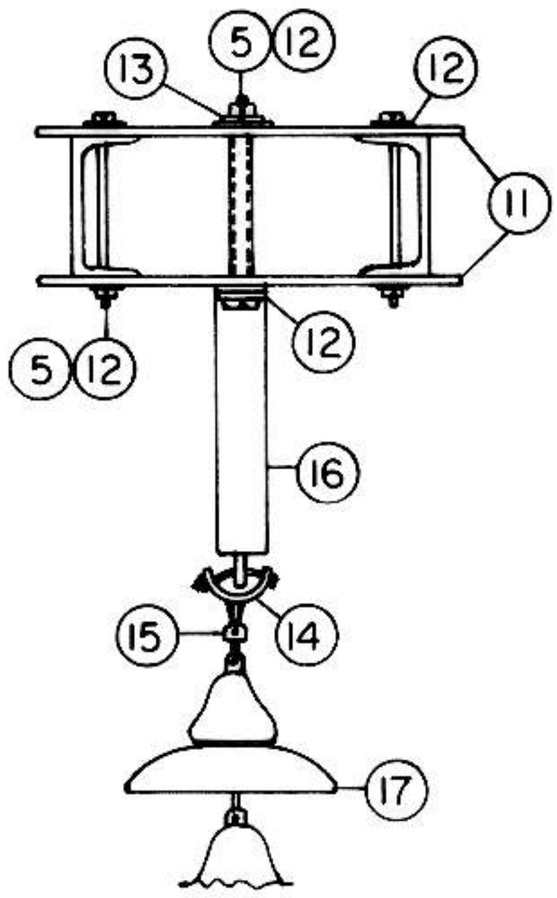


รายละเอียด B
DETAIL

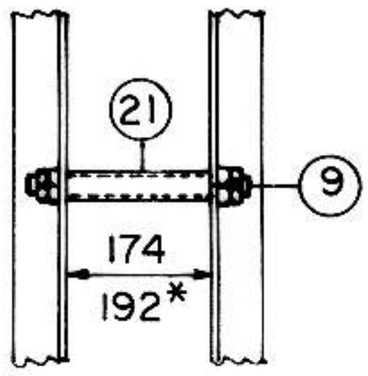


รายละเอียด C
DETAIL

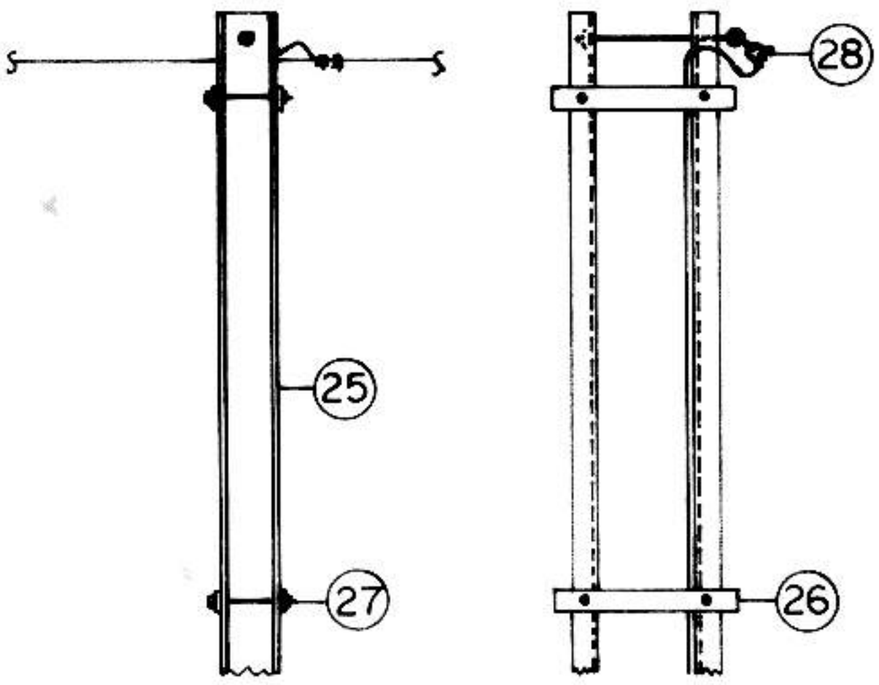


รายละเอียด D
DETAIL

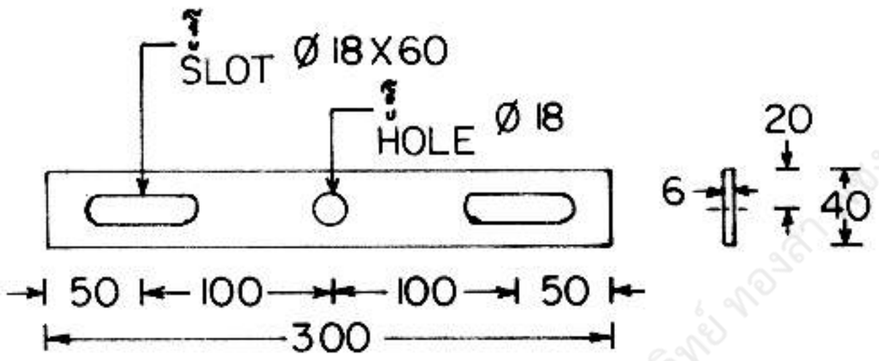

(11) เหล็กแผ่น 40 X 6 มม. ยาว 300 มม.
(สามารถทำจากวัสดุเลขที่ 01200002 ได้)
STEEL, PLATE, 40 X 6 mm, 300 mm LONG
(MAY BE MADE FROM MAT. NO. 01200002)

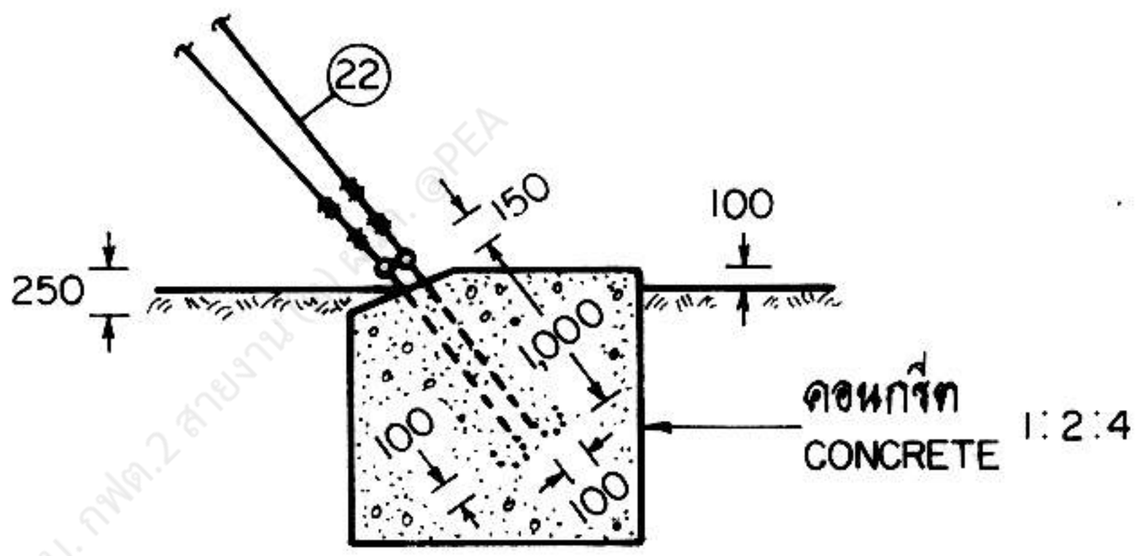

(23) สมอยึดคอนกรีต
CONCRETE ANCHOR

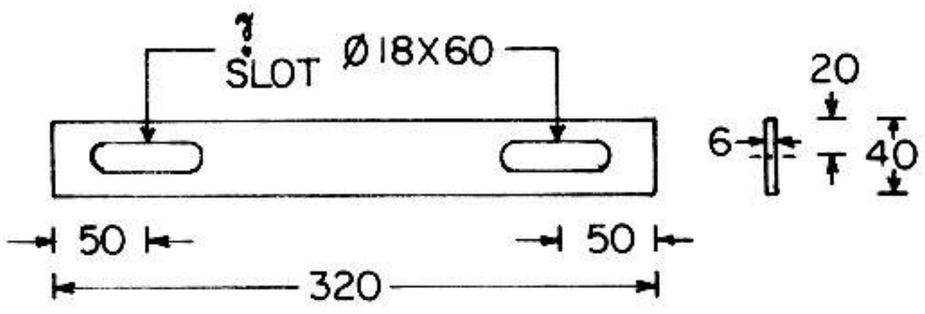

(26) เหล็กแผ่น 40 X 6 มม. ยาว 320 มม.
(สามารถทำจากวัสดุเลขที่ 01200002 ได้)
STEEL, PLATE, 40 X 6 mm, 320 mm LONG
(MAY BE MADE FROM MAT. NO. 01200002)

กองวิศวกรรมไฟฟ้าและเครื่องกล
ฝ่ายวิศวกรรม

ผู้เขียน ...
ผู้สำรวจ ...
วิศวกร สัมพันธ์
หัวหน้าแผนก ...
ผู้อำนวยการกอง ...
ผู้อำนวยการฝ่าย ...

ของผู้ว่าการฝ่ายเทคนิค ...

การไฟฟ้าส่วนภูมิภาค

ผู้ว่าการ ... 16 ก.ย. 34

โครงสร้างเสาคู่ สำหรับแขวนสายไฟฟ้า ระบบ 33 kV
ช่วงเสา 120 - 200 ม.
มุม > 5°-30°


33 kV, H-FRAME SUSPENSION STRUCTURE
SPAN 120 - 200 m
LINE ANGLE > 5°-30°

ใช้แทนแบบ ...
ถูกแทนโดยแบบ ...
เขียนเสร็จวันที่ 20 ส.ค. 34
แก้แบบวันที่ ...
มิติเป็น มิลลิเมตร
มาตราส่วน ...

แบบเลขที่ SAI-015/34020
แผ่นที่ 2 ของจำนวน 5 แผ่น

12 ก.ย. 2536

การประกอบเลขที่ ASSEMBLY NO. **3234**

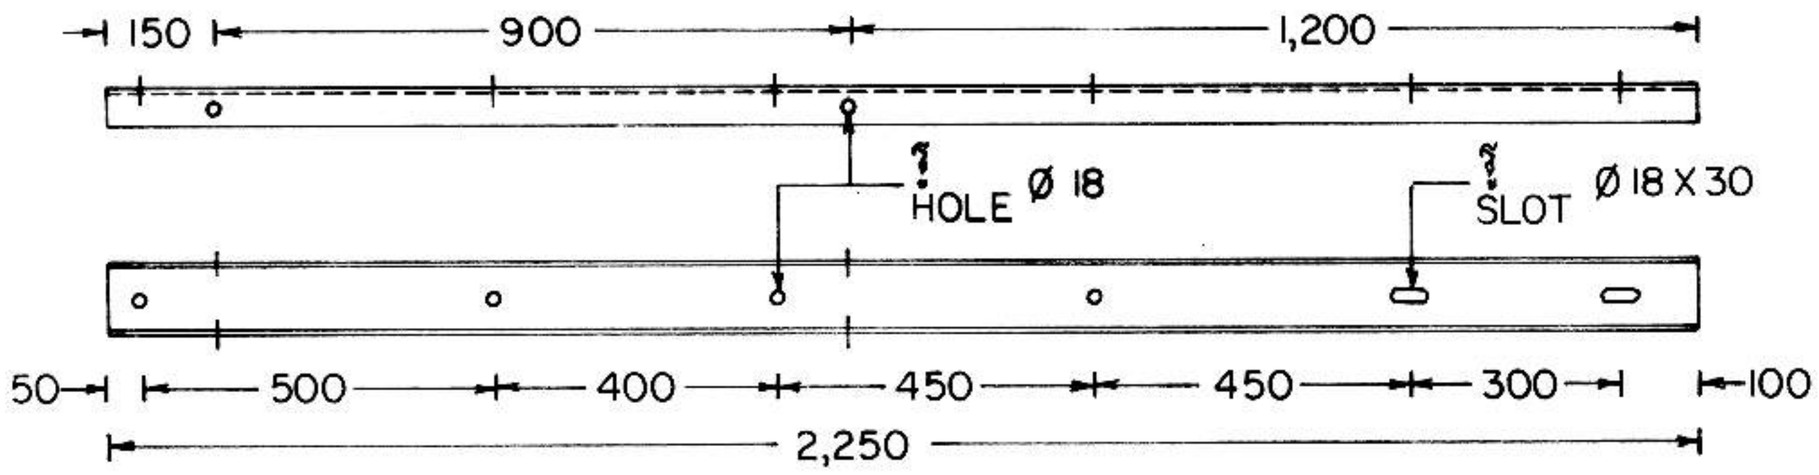

(25) เหล็กรูปรางน้ำ ขนาด 100 X 50 X 5 มม. ยาว 2.25 ม. มอก. 116 (สามารถทำจากวัสดุเลขที่ 01000100 ได้)
STEEL, CHANNEL, 100 X 50 X 5 mm, 2.25 m LONG, TIS 116 (MAY BE MADE FROM MAT. NO. 01000100)

บัญชีวัสดุ
BILL OF MATERIAL

ลำดับที่ ITEM	รายละเอียด DESCRIPTION	จำนวน REQ'D I	จำนวน REQ'D II	วัสดุเลขที่ MAT. NO.
1	เสาคอนกรีต 12 ม. POLE, CONCRETE, 12 m LONG	2	–	00010003 (0033)
2	เสาคอนกรีต 14 ม. POLE, CONCRETE, 14 m LONG	–	2	00010005 (0035)
3	เหล็กรูปรางน้ำ ขนาด 100 X 50 X 5 มม. ยาว 4.50 ม. (มอก. 116) STEEL CHANNEL, 100 X 50 X 5 mm, 4.50 m LONG (TIS 116)	2	2	(0198)
4	เหล็กฉาก ขนาด 75 X 75 X 6 มม. ยาว 3.50 ม. (มอก. 116) STEEL ANGLE, 75 X 75 X 6 mm, 3.50 m LONG (TIS 116)	2	2	01010100 (0123)
5	สลักเกลียว M 16 X 170 มม. BOLT, MACHINE, M 16 X 170 mm	14	14	01110201 (0221)
6	สลักเกลียว M 16 X 200 มม. BOLT, MACHINE, M 16 X 200 mm	2	–	01110202 (0222)
7	สลักเกลียว M 16 X 250 มม. BOLT, MACHINE, M 16 X 250 mm	6	8	01110203 (0223)
8	สลักเกลียว M 16 X 300 มม. BOLT, MACHINE, M 16 X 300 mm	2	2	01110204 (0224)
9	สลักเกลียวตลอด M 16 X 400 มม. BOLT. DOUBLE ARMING, M 16 X 400 mm	1	1	01120000 (0243)
10	สลักห่วงโอแวล M 16 X 150 มม. BOLT, OVAL EYE, M 16 X 150 mm	1	1	01150000 (0257)
11	แผ่นเหล็ก ขนาด 6 X 100 มม. ยาว 300 มม. เจาะรูตามแบบ แผ่นที่ 2 STEEL, PLATE, 6 X 100 mm, 300 mm LONG; PUNCH HOLE AS DWG. ON SHEET NO. 2	10	10	—
12	แหวนสี่เหลี่ยมแบน 52 X 52 X 4.5 มม. รู Ø 18 มม. มอก. 258 WASHER, SQUARE, FLAT, 52 X 52 X 4.5 mm, HOLE Ø 18 mm, TIS 258	38	38	01180100 (0355)
13	แหวนสปริง M 16 มอก. 259 WASHER LOCK, M 16, TIS 259	6	6	01180301 (0365)
14	ข้อต่อแบบ วาย - เคลวิส - บอล ANSI แบบ B Y-CLEVIS-BALL, ANSI, TYPE B	3	3	03140004 (0485)

กองวิศวกรรมไฟฟ้าและเครื่องกล
ฝ่ายวิศวกรรม

ผู้เสนอ ...
ผู้สำรวจ ...
วิศวกร ...
หัวหน้าแผนก ...
ผู้อำนวยการกอง ...
ผู้อำนวยการฝ่าย ...

ของผู้ว่าการฝ่ายเทคนิค ...

การไฟฟ้าส่วนภูมิภาค

ผู้ว่าการ ... 16 ก.ย. 34

โครงสร้างเสาคู่ สำหรับแขวนสายไฟฟ้า ระบบ 33 kV
ช่วงเสา 120 – 200 ม.
มุม > 5° – 30°

33 kV, H-FRAME SUSPENSION STRUCTURE
SPAN 120 – 200 m
LINE ANGLE > 5° – 30°

ใช้แทนแบบ ...
ถูกแทนโดยแบบ ...
เสนอเสร็จวันที่ 20 ส.ค. 34
แก้แบบวันที่ ...
มิติเป็น มิลลิเมตร
มาตราส่วน 1 : 20

แบบเลขที่ SAI-015/34020
แผ่นที่ 3 จากจำนวน 5 แผ่น

12 ก.ย. 2534

การประกอบเลขที่ ASSEMBLY NO. 3234

บัญชีวัสดุ
BILL OF MATERIAL

ลำดับที่ ITEM	รายละเอียด DESCRIPTION	จำนวน REQ'D I	จำนวน REQ'D II	วัสดุเลขที่ MAT. NO.
15	ข้อต่อแบบ ซ็อคเก็ต-อาย ANSI แบบ B SOCKET-EYE, ANSI, TYPE B	3	3	03140003 (0484)
16	ที่แขวนลูกถ้วยทางโค้ง BRACKET, CORNER SUSPENSION	2	2	03140012 (0489)
17	ลูกถ้วยแขวน มอก.354 แบบ ง (แบบ 52-4) INSULATOR, SUSPENSION TYPE, TIS 354, TYPE D (CLASS 52-4)	9	9	03020002 (0415)
18	ขั้วเพนซันแคล้มป์ แบบเคลวิส์ ขนาดตามต้องการ CLAMP, SUSPENSION, CLEVIS TYPE; SIZE AS REQUIRED	3	3	03120101 03120001
19	ปรีฟอร์มอาร์เมอร์ร็อด ARMOR ROD, PREFORMED	3	3	02220104 - 02220107
20	ไวเบรชั่นแดมเปอร์ แบบสไปแรล สำหรับสายอะลูมิเนียมเปลือย, สายอะลูมิเนียมแกนเหล็ก และ สายอะลูมิเนียมเรือ VIBRATION DAMPER, SPIRAL, FOR Al, ACSR, AND Al-ALLOY CONDUCTOR	6	6	02200101 - 02200103
21	ท่อเหล็ก ขื่อขนาด 20 มม. หนา 2.65 มม. ความยาวตามต้องการ PIPE, IRON, DIA. 20 mm I.D., 2.65 mm THICKNESS; LENGTH AS REQUIRED	1	1	—
22	การยึดโยง GY-32 (ลวดเหล็กตีเกลียว 95 ต.มม. ไม่รวมสมอบก) GUY GY-32 (STEEL STRANDED WIRE 95 mm^2, ANCHOR NOT INCLUDED)	2	2	—
23	สมอบกคอนกรีต 1,500 X 1,500 X 1,500 มม. (คอนกรีต 1:2:4) ANCHOR, CONCRETE, 1,500 X 1,500 X 1,500 mm (CONCRETE 1:2:4)	1	1	—
24	คอนกรีต 1:3:5 CONCRETE 1:3:5	2.5 ม.^{3} 2.5 m^3	2.5 ม.^{3} 2.5 m^3	—
25	เหล็กรูปรางน้ำ ขนาด 100 X 50 X 5 มม. ยาว 2.25 ม. มอก. 116 เจาะรูตามแบบแผ่นที่ 3 STEEL, CHANNEL, 100 X 50 X 5 mm, 2.25 m LONG; PUNCH HOLE AS DWG. ON SHEET NO. 3	4	4	—
26	เหล็กแผ่น ขนาด 40 X 6 มม. ยาว 320 มม. เจาะรูตามแบบแผ่นที่ 2 STEEL, PLATE, 40 X 6 mm, 320 mm LONG; PUNCH HOLE AS DWG. ON SHEET NO. 2	8	8	—
27	สลักเกลียว M 16 X 130 มม. BOLT, MACHINE, M 16 X 130 mm	8	8	01110200 (0220)
28	กราวด์วายร์แคล้มป์ สำหรับเสาคอนกรีต GROUND WIRE SUPPORT AND CLAMP, FOR CONCRETE POLE	2	2	01230202 (0299)
29	ไวเบรชั่นแดมเปอร์ แบบสไปแรล สำหรับลวดเหล็กตีเกลียว 25 ต.มม. VIBRATION DAMPER, SPIRAL, FOR 25 mm^2 STEEL STRANDED WIRE	4	4	02200100 (0903)
30	ยูแคล้มป์ สลัก 1 ตัว M 8 CLAMP, SINGLE U-BOLT, M 8	8	8	01230000 (0165)

กองวิศวกรรมไฟฟ้าและเครื่องกล
ฝ่ายวิศวกรรม

ผู้เขียน ...
ผู้สำรวจ ...
วิศวกร สมชาย
หัวหน้าแผนก ...
ผู้อำนวยการกอง ...
ผู้อำนวยการฝ่าย ...

ของผู้ว่าการฝ่ายเทคนิค
12 ก.ย. 2534

การไฟฟ้าส่วนภูมิภาค

ผู้ว่าการ ... 16 ก.ย. 34

โครงสร้างเสาคู่ สำหรับแขวนสายไฟฟ้า ระบบ 33 kV
ช่วงเสา 120 – 200 ม.
มุม > 5°–30°

33 kV, H-FRAME SUSPENSION STRUCTURE
SPAN 120 – 200 m
LINE ANGLE > 5°–30°

ใช้แทนแบบ ...
ถูกแทนโดยแบบ ...
เขียนแล้วเสร็จวันที่ 20 ส.ค. 34
แก้แบบวันที่ ...
มิติเป็น ...
มาตราส่วน ...

แบบเลขที่ SAI-015/34020
แผ่นที่ 4 ของจำนวน 5 แผ่น

ข้อกำหนด

การประกอบเลขที่ ASSEMBLY NO. 3234

REGULATIONS

ชนิดและขนาดของสายไฟฟ้า ตร.มม. TYPE AND SIZE OF CONDUCTOR mm^2	ระยะระหว่างเสาสูงสุด ม. MAXIMUM SPAN LENGTH m	ระยะหย่อนยานต่ำสุดของสายไฟฟ้าทุกเส้น ม. MINIMUM SAG OF ALL CONDUCTORS m
ACSR 95/15	200	3.00
ACSR 120/20		4.00
ACSR 185/30		6.00
AA 95		3.00
AA 120		3.00
AA 185		4.00

หมายเหตุ

1. จำนวนในบัญชีวัสดุ :
   สดมภ์ I สำหรับเสาคอนกรีต 12 ม.
   สดมภ์ II สำหรับเสาคอนกรีต 14 ม.
2. ACSR หมายถึงสายอะลูมิเนียมแกนเหล็ก

   AA หมายถึงสายอะลูมิเนียมเจือ
3. เสาต้นที่ปักอยู่ในบริเวณที่เป็นดินอ่อน (ดินเหนียว, ดินเลน) หรือดินแข็งปานกลาง (ดินปนทราย) ให้เทคอนกรีตหุ้มโคนเสา ลึก 2.00 ม. จากระดับผิวดิน ขนาดหน้าตัด 0.80 X 0.80 ม.

NOTES

1. REQ'D IN BILL OF MATERIAL :
   COLUMN I, FOR 12 m CONCRETE POLE.
   COLUMN II, FOR 14 m CONCRETE POLE.
2. ACSR IS ALUMINIUM CONDUCTOR, STEEL REINFORCED.
   AA IS ALL ALUMINIUM ALLOY CONDUCTOR.
3. THE POLE FOOT SHALL BE COVERED WITH CONCRETE 2.00 m DEPTH, CROSS-SECTION 0.80 X 0.80 m, IF IT IS SET IN POOR SOIL (MARCHY SOIL, OR CLAY) OR NORMAL SOIL (SANDY CLAY).

อติวิทย์ ทองสา พขง.3 ผปร. กพฟ.2 สำนักงานใหญ่ กพฟ.

กองวิศวกรรมไฟฟ้าและเครื่องกล ฝ่ายวิศวกรรม	การไฟฟ้าส่วนภูมิภาค	ใช้แทนแบบ ..... ถูกแทนโดยแบบ ..... เขียนเสร็จวันที่ 20 ส.ค. 34 แก้แบบวันที่ ..... มิติเป็น ..... มาตราส่วน .....
ผู้เขียน ..... ผู้สำรวจ ..... วิศวกร ..... หัวหน้าแผนก ..... ผู้อำนวยการกอง ..... ผู้อำนวยการฝ่าย	ผู้ว่าการ ..... 16 ส.ค. 34	
	โครงสร้างเสาคู่ สำหรับแขวนสายไฟฟ้า ระบบ 33 kV ช่วงเสา 120-200 ม. มุม >5°-30°	
ของผู้ว่าการฝ่ายเทคนิค ..... 22 ก.ย 2534	33 kV, H-FRAME SUSPENSION STRUCTURE SPAN 120-200 m LINE ANGLE >5°-30°	แบบเลขที่ SAI-015/34020 แผ่นที่ 5 ของจำนวน 5 แผ่น