การประกอบเลขที่ ASSEMBLY NO. **5 2 6 6**

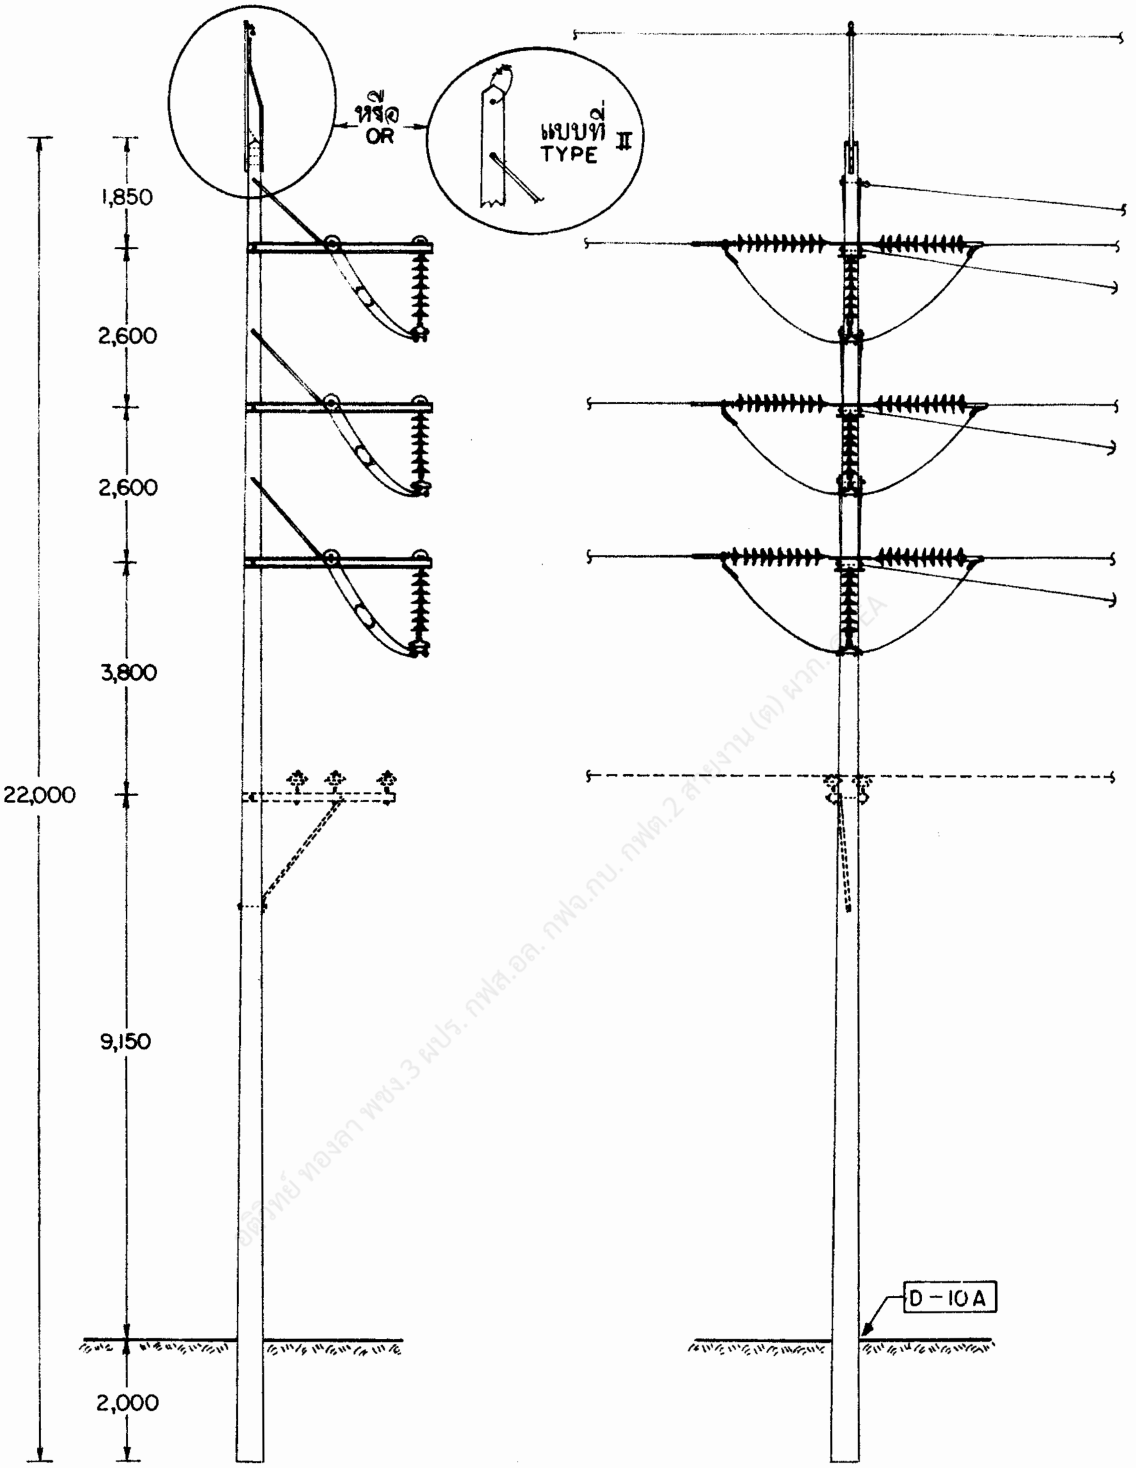

แบบที่ TYPE I

อธิวัฒน์ ทองลา พชง.3 ผปร. กฟส.อล. กฟจ.กบ. กฟต.2 สำเนางาน (ต) ผวก. EA

กองวิศวกรรมไฟฟ้าและเครื่องกล
ฝ่ายวิศวกรรม

การไฟฟ้าส่วนภูมิภาค

ผู้เขียน
ผู้สำรวจ
วิศวกร
หัวหน้าแผนก
ผู้อำนวยการกอง
ผู้อำนวยการฝ่าย
รองผู้ว่าการฝ่ายเทคนิค

ผู้ว่าการ 27 ก.พ. 35

115 kV วงจรเดี่ยว สายไฟฟ้าคู่
โครงสร้างเสาเจ้าปลายสายสองข้าง ก่อนเสาช่วงทางโค้ง
แบบ SD-AS-3

115 kV SINGLE-CIRCUIT DOUBLE-CONDUCTOR
DOUBLE DEADEND STRUCTURE, ADJACENT POLE TO ANGLE
TYPE SD-AS-3

ใช้แทนแบบ
ถูกแทนโดยแบบ
เขียนเสร็จวันที่ 30 ม.ค. 35
แก้แบบวันที่ 27 ก.ค. 38
มิติเป็น มิลลิเมตร
มาตราส่วน 1 : 125
แบบเลขที่ SAI-015/35003
แผ่นที่ 1 ของจำนวน 5 แผ่น

การประกอบเลขที่ ASSEMBLY NO. **5266**

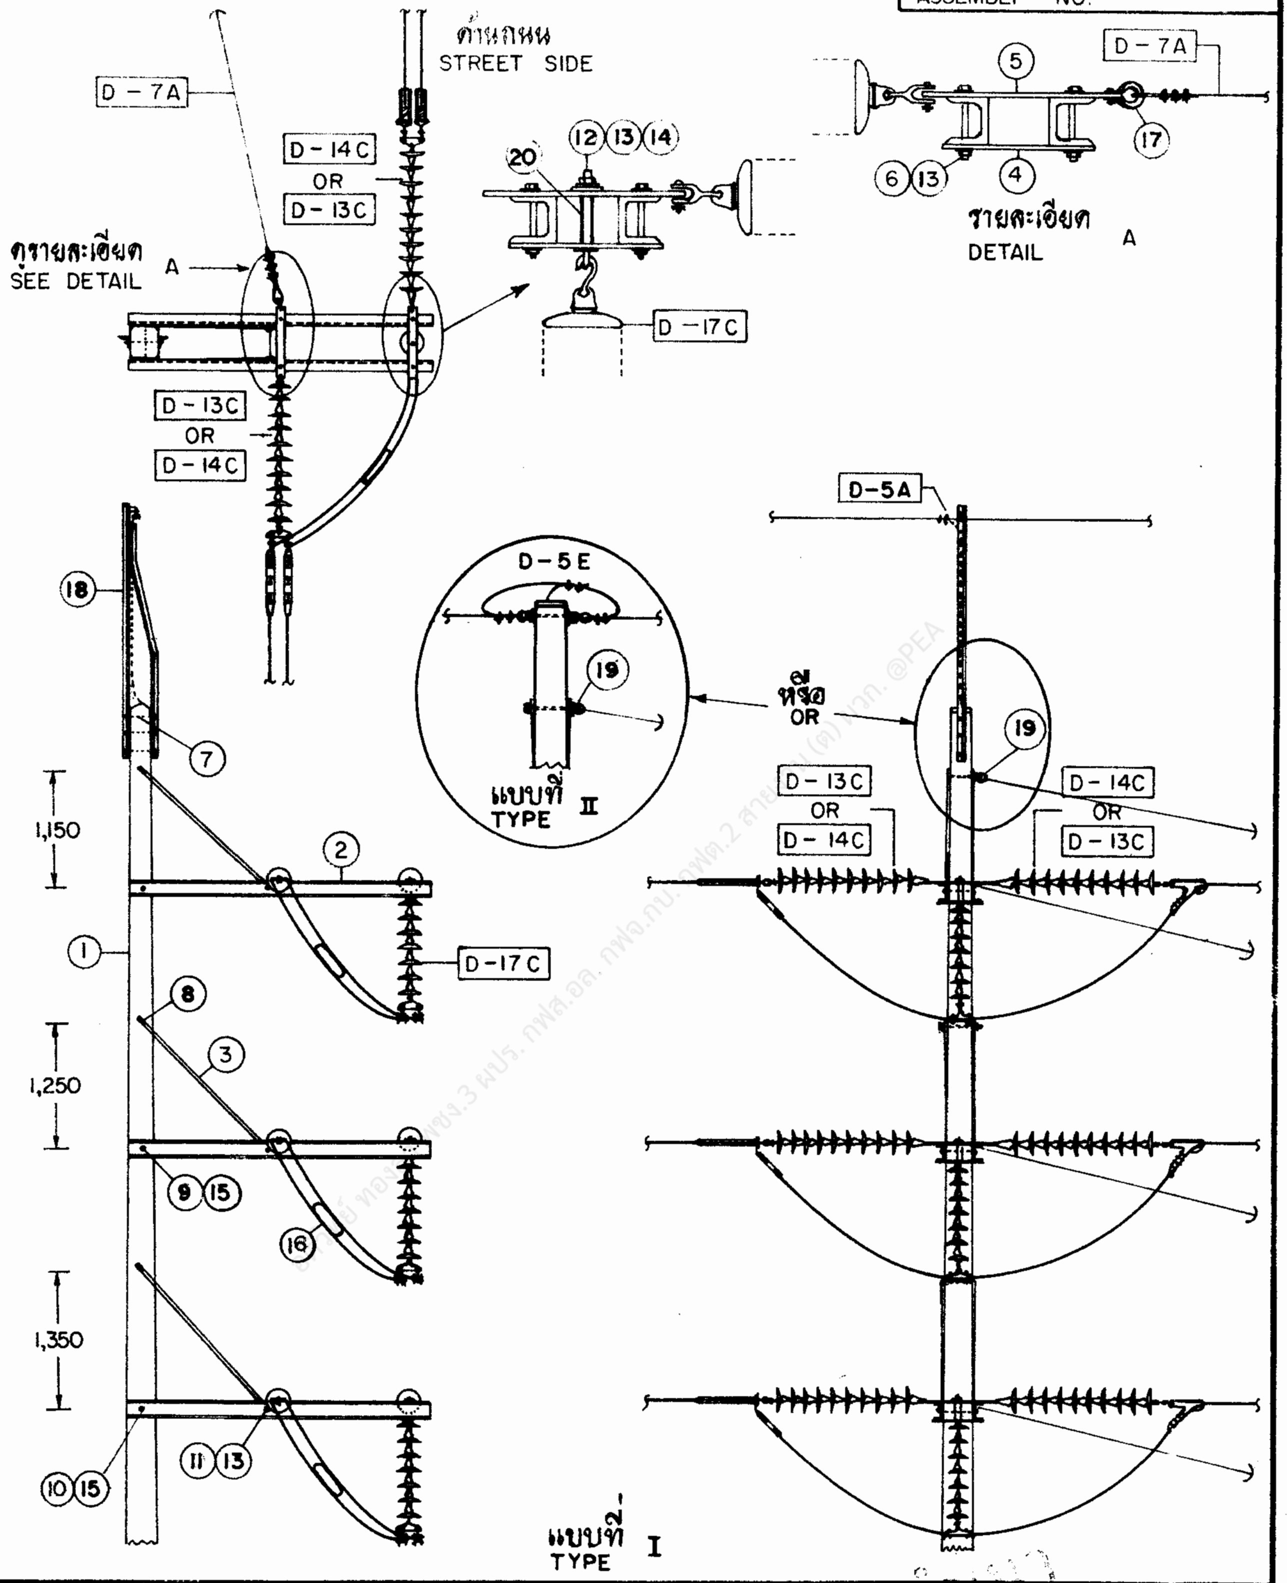

กองวิศวกรรมไฟฟ้าและเครื่องกล ฝ่ายวิศวกรรม	**การไฟฟ้าส่วนภูมิภาค**	ใช้แทนแบบ.......... ถูกแทนโดยแบบ..........
ผู้เขียน.......... ผู้สำรวจ.......... วิศวกร.......... หัวหน้าแผนก.......... ผู้อำนวยการกอง.......... ผู้อำนวยการฝ่าย..........	ผู้ว่าการ.......... 27 ก.พ.35	เขียนเสร็จวันที่ 30 ม.ค.35 แก้แบบวันที่ 27 ก.ค.38 มิติเป็น มิลลิเมตร มาตราส่วน 1 : 75
	115 kV วงจรเดี่ยว สายไฟฟ้าคู่ โครงสร้างเสาเข้าปลายสายสองข้าง ก่อนเสาช่วงทางโค้ง แบบ SD - AS - 3	
รองผู้ว่าการฝ่ายเทคนิค..........	115 kV SINGLE-CIRCUIT DOUBLE-CONDUCTOR DOUBLE DEADEND STRUCTURE, ADJACENT POLE TO ANGLE TYPE SD - AS - 3	แบบเลขที่ SAI-015/35003 แผ่นที่ 2 ของจำนวน 5 แผ่น

การประกอบเลขที่
ASSEMBLY NO. **5266**

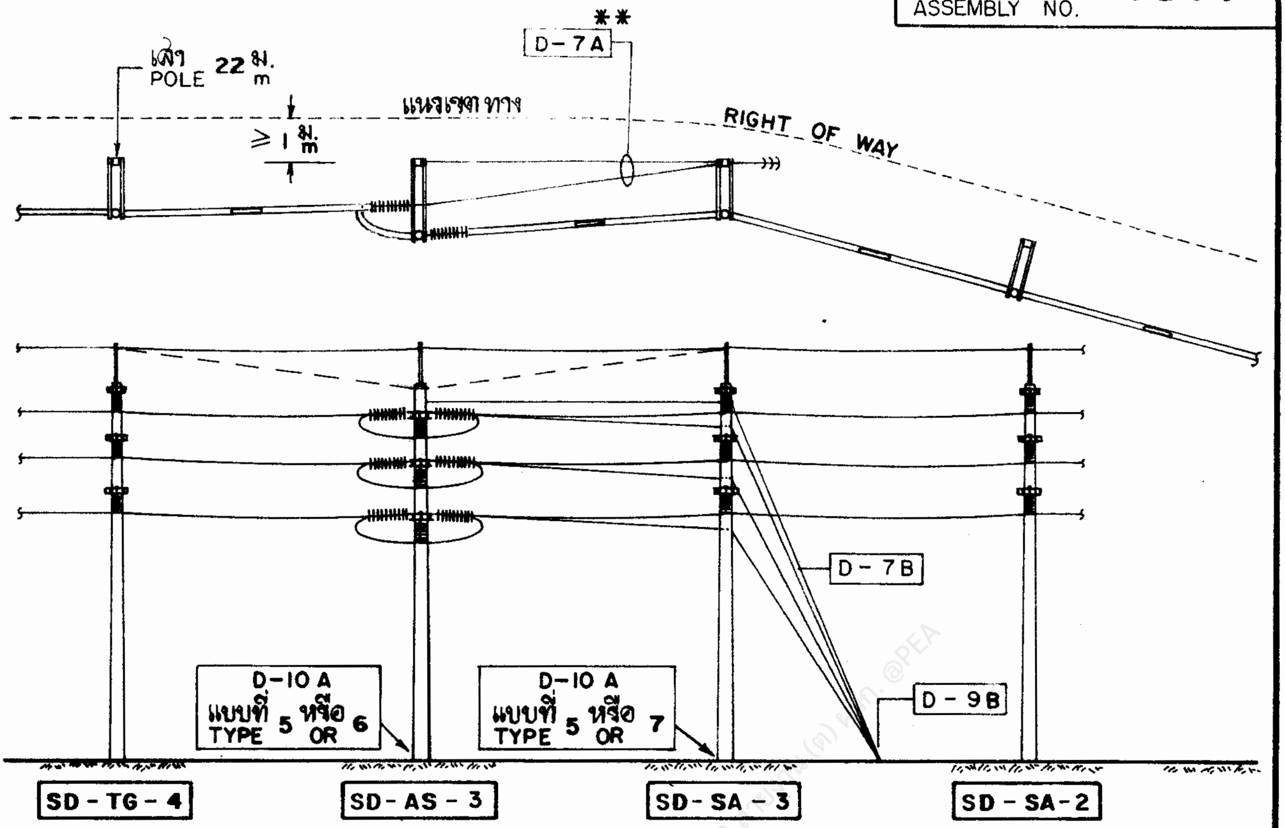

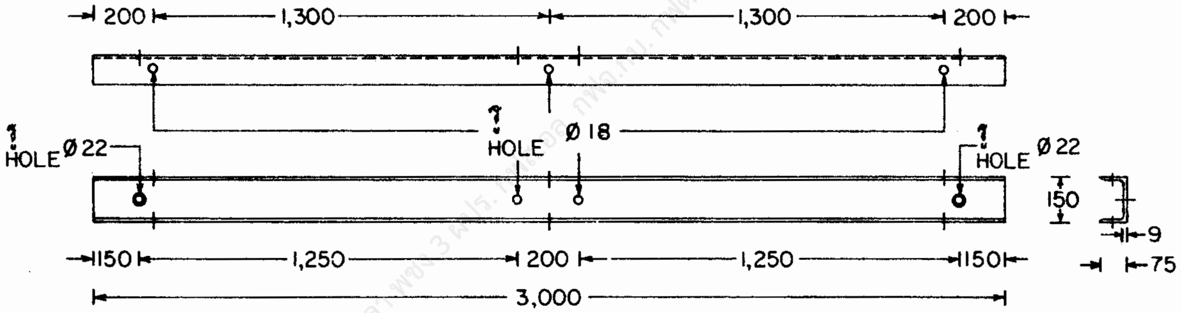

วัสดุลำดับที่
MATERIAL ITEM ②

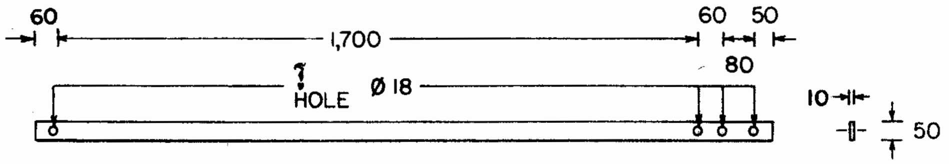

วัสดุลำดับที่
MATERIAL ITEM ③

กองวิศวกรรมไฟฟ้าและเครื่องกล ฝ่ายวิศวกรรม	**การไฟฟ้าส่วนภูมิภาค**	ใช้แทนแบบ ถูกแทนโดยแบบ
ผู้เขียน ผู้สำรวจ วิศวกร หัวหน้าแผนก ผู้อำนวยการกอง ผู้อำนวยการฝ่าย	ผู้ว่าการ 27 ก.พ. 35 115 kV วงจรเดี่ยว สายไฟฟ้าคู่ โครงสร้างเสาเข้าปลายสายสองข้าง ก่อนเสาช่วงทางโค้ง แบบ SD - AS - 3	เขียนเสร็จวันที่ 30 ม.ค. 35 แก้แบบวันที่ 27 ก.ค. 38 มิติเป็น มิลลิเมตร มาตราส่วน 1:20, 1:25
รองผู้ว่าการฝ่ายเทคนิค	115 kV SINGLE-CIRCUIT DOUBLE-CONDUCTOR DOUBLE DEADEND STRUCTURE, ADJACENT POLE TO ANGLE TYPE SD - AS - 3	แบบเลขที่ SAI-015/35003 แผ่นที่ 3 ของจำนวน 5 แผ่น

การประกอบเลขที่ ASSEMBLY NO. **5266**

บัญชีวัสดุ
BILL OF MATERIAL

ลำดับที่ ITEM	รายละเอียด DESCRIPTION	จำนวน REQ'D		วัสดุเลขที่ MAT. NO.
		I	II	
1	เสาคอนกรีต 22 ม. POLE, CONCRETE 22 m LONG	1	1	00010011 (0041)
2	คอนสายแบบเหล็กรูปรางน้ำ ขนาด 150 X 75 X 9 มม. ยาว 3.00 ม. มอก. 116 CROSSARM, STEEL CHANNEL, 150 X 75 X 9 mm, 3.00 m LONG TIS 116	6	6	—
3	เหล็กประกับคอนสาย ขนาด 50 X 10 X 1,950 มม. มอก. 55 BRACE, FLAT, FOR CROSSARM, 50 X 10 X 1,950 mm TIS 55	6	6	—
4	เหล็กแผ่น ขนาด 6 X 100 X 450 มม. PLATE, STEEL, 6 X 100 X 450 mm	6	6	01030002 (0143)
5	แผ่นเหล็กยึดสองปลาย ขนาด 12 X 100 X 760 มม. PLATE, STEEL, DOUBLE ARMING, 12 X 100 X 760 mm	6	6	01030102 (6006)
6	สลักเกลียว M 16 X 250 มม. BOLT, MACHINE, M 16 X 250 mm	12	12	01110203 (0223)
7	สลักเกลียว M 16 X 300 มม. BOLT, MACHINE, M 16 X 300 mm	4	1	01110204 (0224)
8	สลักเกลียว M 16 X 350 มม. BOLT, MACHINE, M 16 X 350 mm	2	2	01110205 (0225)
9	สลักเกลียว M 20 X 350 มม. BOLT, MACHINE, M 20 X 350 mm	2	2	01110300
10	สลักเกลียว M 20 X 400 มม. BOLT, MACHINE, M 20 X 400 mm	1	1	01110301 (0233)
11	สลักเกลียวตลอด M 16 X 400 มม. BOLT, DOUBLE ARMING, M 16 X 400 mm	3	3	01120000 (0243)
12	สลักห่วงโอแวล M 16 X 200 มม. BOLT, OVAL EYE, M 16 X 200 mm	3	3	01150001 (0258)
13	แหวนสี่เหลี่ยมแบน 52 X 52 X 4.5 มม. รู Ø 18 มม. มอก. 258 WASHER SQUARE, FLAT 52 X 52 X 4.5 mm, HOLE Ø 18 mm, TIS 258	42	42	01180100 (0355)
14	แหวนสปริง M 16 มอก. 259 WASHER, LOCK, M 16, TIS 259	3	3	01180301 (0365)
15	แหวนสี่เหลี่ยมแบน 62 X 62 X 6 มม. รู Ø 22 มม. มอก. 258 WASHER SQUARE, FLAT 62 X 62 X 6 mm, HOLE Ø 22 mm, TIS 258	6	6	01180101 (0356)
16	ปรีฟอร์มแยกสาย SPACER, HELICAL ROD, PREFORMED	6	6	02240000 (0918)
17	ทิมเบิลเคลวิส สำหรับปรีฟอร์มเข้าปลายสาย CLEVIS, THIMBLE, FOR PREFORMED DEADEND	3	3	03140011 (0482)
18	เหล็กฉากรับสายล่อฟ้าทางโค้ง ขนาด 65 X 65 X 6 มม. ยาว 2,500 มม. มอก. 116 OVERHEAD GROUND WIRE CORNER BAYONET, 65 X 65 X 6 mm, 2,500 mm LONG, TIS 116	1	—	01010005 (0136)
19	อายนัท M 16 DIN 582 พร้อมกายทิมเบิล NUT, EYE, M 16 DIN 582, WITH THIMBLE GUY	1	1	
20	ท่อเหล็ก รูขนาด 20 มม. หนา 2.65 มม. ยาว 150 มม. PIPE, IRON DIA. 20 mm I.D., 2.65 mm THICKNESS, 150 mm LONG	3	3	— 0150002

กองวิศวกรรมไฟฟ้าและเครื่องกล ฝ่ายวิศวกรรม	**การไฟฟ้าส่วนภูมิภาค**	ใช้แทนแบบ ถูกแทนโดยแบบ
ผู้เขียน ผู้สำรวจ วิศวกร หัวหน้าแผนก ผู้อำนวยการกอง ผู้อำนวยการฝ่าย	ผู้ว่าการ 27 ก.พ. 35 115 kV วงจรเดี่ยว สายไฟฟ้าคู่ โครงสร้างเสาเข้าปลายสายสองข้าง ก่อนเสาช่วงทางโค้ง แบบ SD-AS-3	เขียนเสร็จวันที่ 30 ม.ค. 35 แก้แบบวันที่ 27 ก.ค. 38 มิติเป็น มาตราส่วน
รองผู้ว่าการฝ่ายเทคนิค	115 kV SINGLE-CIRCUIT DOUBLE-CONDUCTOR DOUBLE DEADEND STRUCTURE, ADJACENT POLE TO ANGLE TYPE SD-AS-3	แบบเลขที่ SAI-015/35003 แผ่นที่ 4 ของจำนวน 5 แผ่น

การประกอบเลขที่
ASSEMBLY NO. **5266**

รายละเอียด
DETAIL

D-13C	การประกอบลูกถ้วยแขวน SUSPENSION INSULATOR ASSEMBLY	3	3	
D-14C	การประกอบลูกถ้วยแขวน SUSPENSION INSULATOR ASSEMBLY	3	3	
D-17C	การประกอบลูกถ้วยแขวน SUSPENSION INSULATOR ASSEMBLY	3	3	
D-5A	การต่อสายล่อฟ้า	1	—	
D-5E	OVERHEAD GROUND WIRE CONNECTION	—	1	
** D-7A	การประกอบสายยึดโยงลวดเหล็กตีเกลียว 95 ต.มม. STEEL STRANDED WIRE 95 mm^2 GUY ASSEMBLY	4	4	
* D-10A	ฐานรากเสา ตามแบบเลขที่ IBI-015/240024 (การประกอบเลขที่ 5667) POLE FOUNDATION ACCD. TO DWG. NO. IBI-015/240024 (ASSEMBLY NO. 5667)	1	1	

* อาจเปลี่ยนแปลงเป็นแบบอื่น โดยขึ้นอยู่กับสภาพของดิน
IT MAY BE CHANGED TO THE OTHER TYPE WHICH DEPEND ON SOIL CONDITION .

** ตัดรายการ สลักห่วงแบบธรรมดา (วัสดุเลขที่ 0163) และแหวนสี่เหลี่ยมแบน (วัสดุเลขที่ 0355)
OMITTED, STRAND EYE BOLT (MAT. NO. 0163) AND SQUARE FLAT WASHER (MAT. NO. 0355) .

อดิวิทย์ ทองลา พชง.3 ผปร. กฟส.อล. กฟ[illegible] (ต) ผวก. @PEA

กองวิศวกรรมไฟฟ้าและเครื่องกล
ฝ่ายวิศวกรรม

ผู้เขียน
ผู้สำรวจ
วิศวกร
หัวหน้าแผนก
ผู้อำนวยการกอง
ผู้อำนวยการฝ่าย

รองผู้ว่าการฝ่ายเทคนิค

การไฟฟ้าส่วนภูมิภาค

ผู้ว่าการ .... 27 ก.พ. 35

115 kV วงจรเดี่ยว สายไฟฟ้าคู่
โครงสร้างเสาเข้าปลายสายสองข้าง ก่อนเสาช่วงทางโค้ง
แบบ SD-AS-3

115 kV SINGLE-CIRCUIT DOUBLE-CONDUCTOR
DOUBLE DEADEND STRUCTURE, ADJACENT POLE TO ANGLE
TYPE SD-AS-3

ใช้แทนแบบ ....
ถูกแทนโดยแบบ ....
เขียนเสร็จวันที่ 30 ม.ค. 35
แก้แบบวันที่ 27 ก.ค. 38
มิติเป็น ....
มาตราส่วน ....
แบบเลขที่ SAI-015/35003
แผ่นที่ 5 ของจำนวน 5 แผ่น