

การประกอบเลขที่ ASSEMBLY NO. 5223

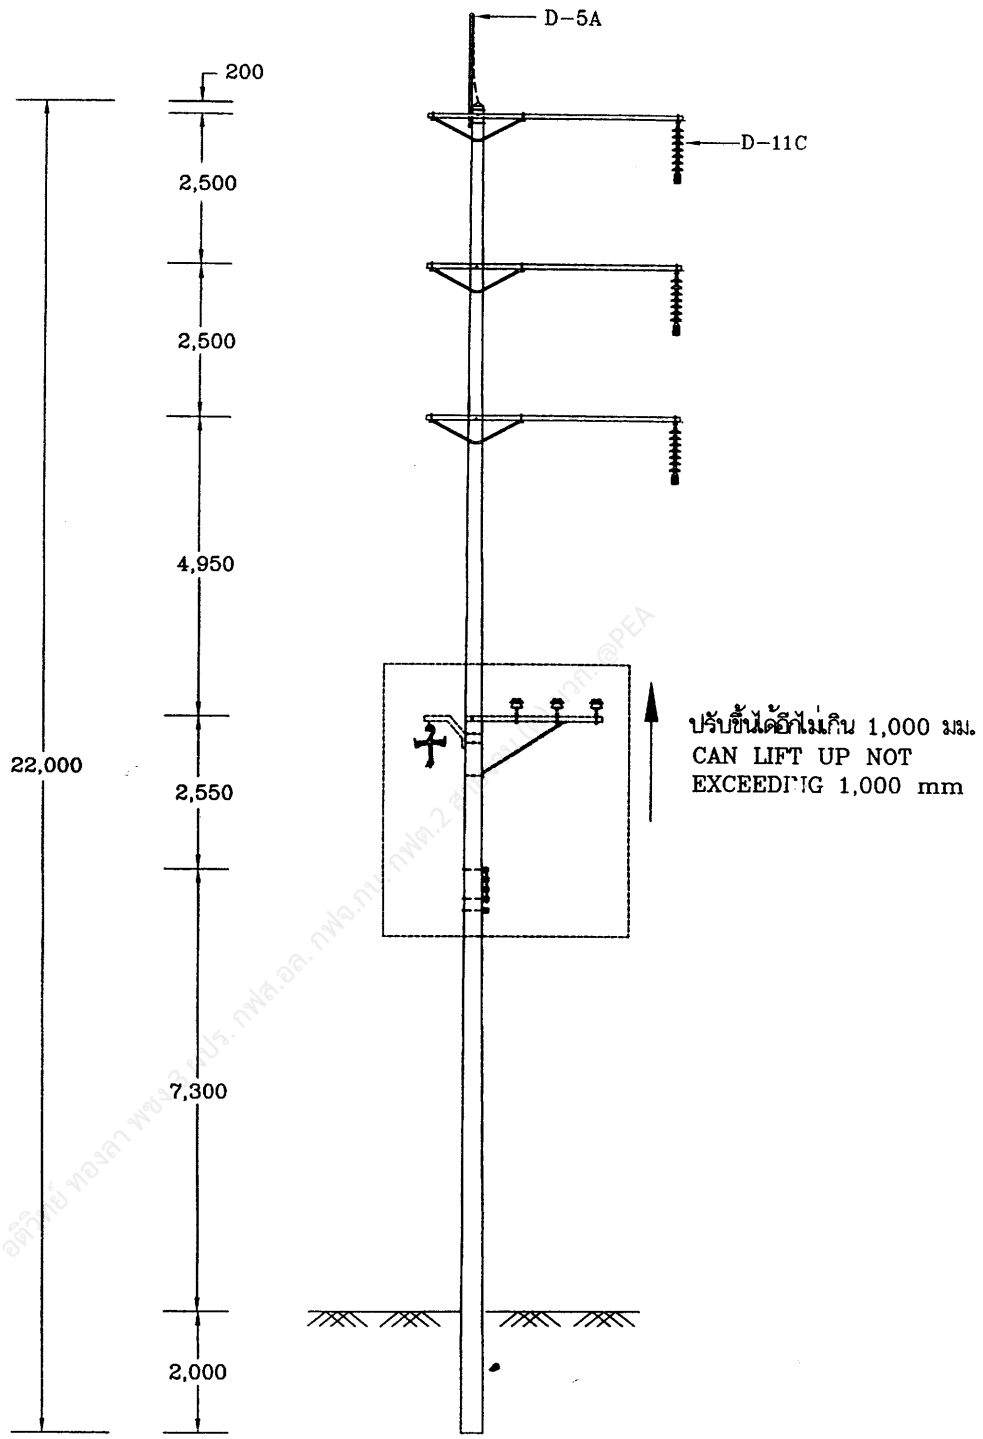


| | | |
|---|---|---|
| กองวิศวกรรมไฟฟ้าและเครื่องกล<br>ฝ่ายวิศวกรรม | การไฟฟ้าส่วนภูมิภาค | ใช้แทนแบบ .....<br>ถูกแทนโดยแบบ ..... |
| ผู้เขียน ...สมนึก สาคร.....<br>ผู้สำรวจ .....<br>วิศวกร .....<br>หัวหน้าแผนก .....<br>ผู้อำนวยการกอง .....<br>ผู้อำนวยการฝ่าย ..... | ผู้ว่าการ ..... 16 พ.ย. 254 | เขียนเสร็จวันที่ 21 ตค. 2541<br>แก้แบบวันที่ .....<br>มิติเป็น ...มิลลิเมตร.....<br>มาตราส่วน ...1..:..125..... |
| รองผู้ว่าการเทคนิคและบริการ<br>..... | 115 kV วงจรเดี่ยว สายไฟฟ้าเดี่ยว<br>เสาสำหรับทางตรง<br>แบบ SS-TG-6 | |
| | 115 kV SINGLE CIRCUIT SINGLE CONDUCTOR<br>TANGENT STRUCTURE<br>TYPE SS-TG-6 | แบบเลขที่ SA1-015/41014<br>แผ่นที่ 1 ของจำนวน 4 แผ่น |

| การประกอบเลขที่ ASSEMBLY NO. | 5223 |
|---|---|

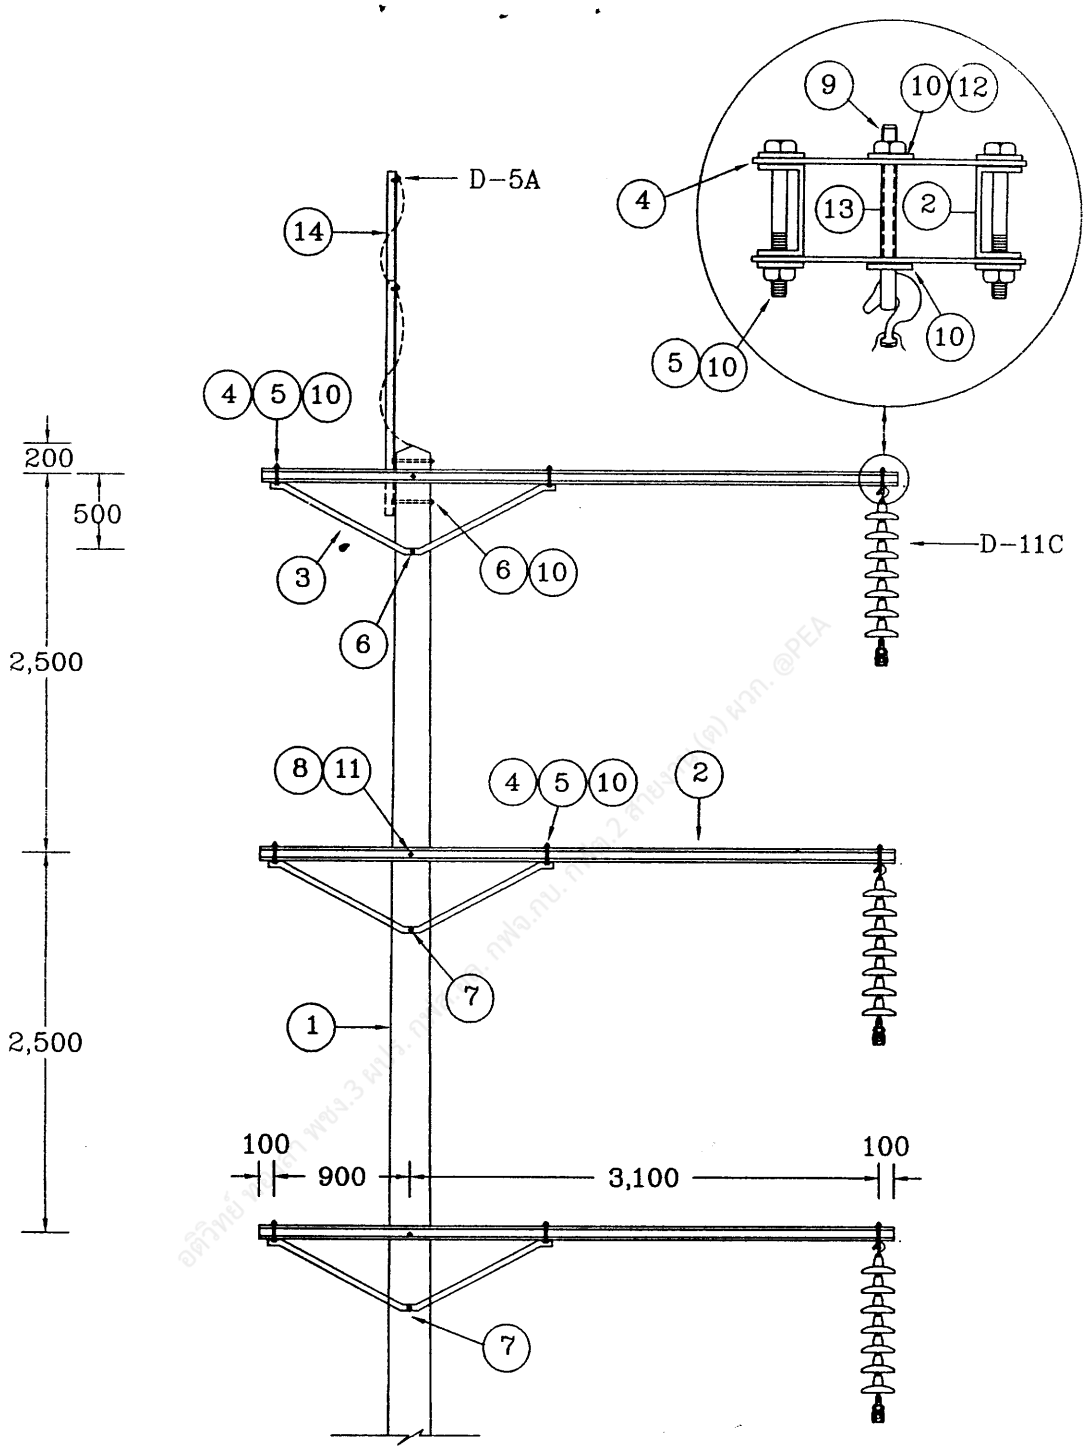


| | | |
|---|---|---|
| กองวิศวกรรมไฟฟ้าและเครื่องกล<br>ฝ่ายวิศวกรรม | การไฟฟ้าส่วนภูมิภาค | ใช้แทนแบบ.....<br>ถูกแทนโดยแบบ..... |
| ผู้เขียน สมนึก สาคร<br>ผู้สำรวจ.....<br>วิศวกร.....<br>หัวหน้าแผนก.....<br>ผู้อำนวยการกอง.....<br>ผู้อำนวยการฝ่าย..... | ผู้ว่าการ..... 16 ต.ค. 2541<br>115 kV วงจรเดี่ยว สายไฟฟ้าเดี่ยว<br>เสาสำหรับทางตรง<br>แบบ SS-TG-6 | เขียนเสร็จวันที่ 21 ตค.2541<br>แก้แบบวันที่ .....<br>มิติเป็น มิลลิเมตร<br>มาตราส่วน 1 : 50 |
| รองผู้ว่าการเทคนิคและบริการ<br>..... | 115 kV SINGLE CIRCUIT SINGLE CONDUCTOR<br>TANGENT STRUCTURE<br>TYPE SS-TG-6 | แบบเลขที่ SA1-015/41014<br>แผ่นที่ 2 ของจำนวน 4 แผ่น |


การประกอบเลขที่ ASSEMBLY NO. 5223


บัญชีวัสดุ
BILL OF MATERIAL

| ลำดับที่ ITEM | รายละเอียด DISCRIPTION | จำนวน REQ'D | วัสดุเลขที่ MAT.NO |
|---|---|---|---|
| 1 | เสาคอนกรีต 22 ม.<br>POLE, CONCRETE, 22 m LONG | 1 | 00010011 |
| 2 | คอนสายแบบเหล็กรูปรางน้ำ ขนาด 100x50x5 มม. ยาว 4.20 ม. มอก.116<br>CROSSARM,STEEL,CHANNEL, 100x50x5 mm, 4.20 m LONG, TIS 116 | 6 | 01030003 |
| 3 | เหล็กฉากรับคอนสาย ขนาด 50x50x6 มม. ช่วงกว้าง 1,800 มม. ดรอพ 450 มม.<br>BRACE,ANGLE STEEL, 50x50x6 mm, 1,800 mm WIDE, 450 mm, DROP | 6 | 00120007 |
| 4 | แผ่นเหล็ก ขนาด 6x100x450 มม.<br>PLATE,STEEL,6x100x450 mm | 12 | 01030002 |
| 5 | สลักเกลียว M 16x170 มม.<br>BOLT, MACHINE, M 16x170 mm | 18 | 01110201 |
| 6 | สลักเกลียว M 16x300 มม.<br>BOLT, MACHINE, M 16x300 mm | 3 | 01110204 |
| 7 | สลักเกลียว M 16x350 มม.<br>BOLT, MACHINE, M 16x350 mm | 2 | 01110205 |
| 8 | สลักเกลียว M 20x350 มม.<br>BOLT, MACHINE, M 20x350 mm | 3 | 01110300 |
| 9 | สลักห่วงโอแวล M 16x150 มม.<br>BOLT, OVAL EYE, M 16x150 mm | 3 | 01150000 |
| 10 | แหวนสี่เหลี่ยมแบน 52x52x4.5 มม. รู ø 18 มม. มอก. 258<br>WASHER, SQUARE, FLAT, 52x52x4.5 mm, HOLE ø 18 mm, TIS 258 | 44 | 01180100 |
| 11 | แหวนสี่เหลี่ยมแบน 62x62x6 มม. รู ø 22 มม. มอก. 258<br>WASHER, SQUARE, FLAT, 62x62x6 mm, HOLE ø 22 mm, TIS 258 | 6 | 01180101 |
| 12 | แหวนสปริง M 16 มอก. 259<br>WASHER, LOCK, M 16, TIS 259 | 3 | 01180301 |
| 13 | ท่อเหล็กขนาดระบุ 20 ประเภทที่ 2 ยาว 100 มม. มอก.277 แต่ไม่มีเกลียวที่ปลาย<br>PIPE,STEEL,SIZE 20,TYPE 2,100 mm. LONG ,TIS.277; BUT WITHOUT THREADED END | 3 | 01050000 |
| 14 | เหล็กฉาก รับสายล่อฟ้า 65x65x6 มม. ยาว 2,500 มม.<br>STEEL,ANGLE, OVERHEAD GROUND WIRE BAYONET,65x65x6 mm 2,500 mm LONG | 1 | 01010004 |
| | | | |
| D-11C | การประกอบลูกถ้วยแขวน<br>SUSPENSION INSULATOR ASSEMBLY | 3 | |
| D-5A | การต่อสายล่อฟ้า<br>OVERHEAD GROUND WIRE CONNECTION | 1 | |

| | | |
|---|---|---|
| กองวิศวกรรมไฟฟ้าและเครื่องกล<br>ฝ่ายวิศวกรรม | การไฟฟ้าส่วนภูมิภาค | ใช้แทนแบบ.....<br>ถูกแทนโดยแบบ..... |
| ผู้เขียน....สมนึก...สาคร...<br>ผู้สำรวจ.....<br>วิศวกร.....<br>หัวหน้าแผนก.....<br>ผู้อำนวยการกอง.....<br>ผู้อำนวยการฝ่าย..... | ผู้ว่าการ..... 16 พ.ย. 2541<br>115 kV วงจรเดี่ยว สายไฟฟ้าเดี่ยว<br>เสาสำหรับทางตรง<br>แบบ SS-TG-6 | เขียนเสร็จวันที่ 21 ต.ค. 2541<br>แก้แบบวันที่ .....<br>มิติเป็น.....<br>มาตราส่วน..... |
| รองผู้ว่าการเทคนิคและบริการ<br>..... | 115 kV SINGLE CIRCUIT SINGLE CONDUCTOR<br>TANGENT STRUCTURE<br>TYPE SS-TG-6 | แบบเลขที่ SA1-015/41014<br>แผ่นที่ 3 ของจำนวน 4 แผ่น |

| การประกอบเลขที่ ASSEMBLY NO. | 5223 |
|---|---|

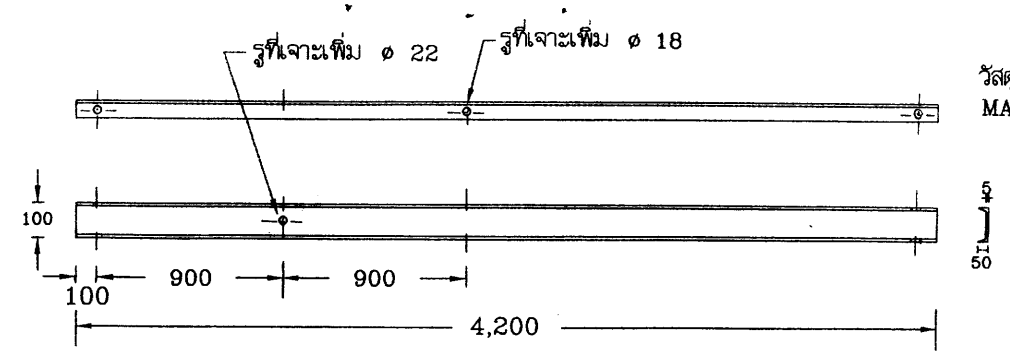

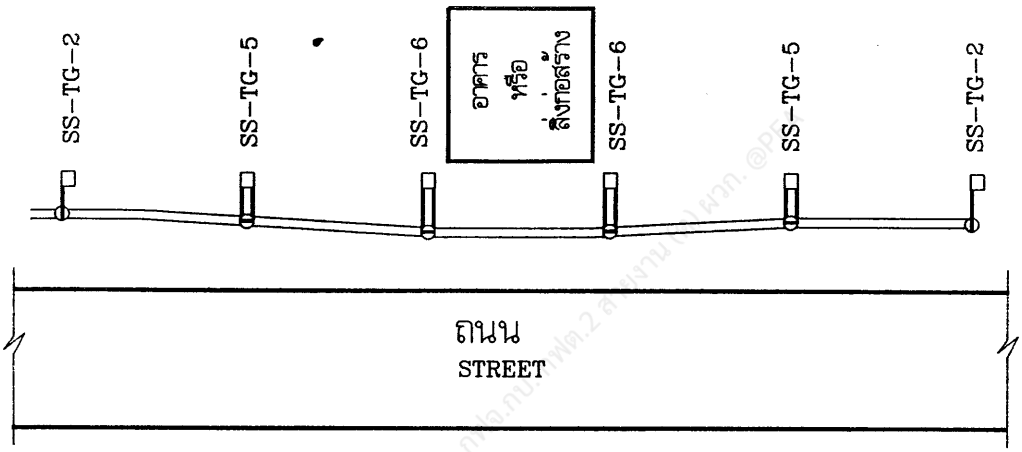
## การนำไปใช้งาน
## APPLICATION

หมายเหตุ

แบบนี้นำมาใช้กรณีที่ต้องการเพิ่มระยะห่างระหว่างสายไฟฟ้ากับอาคาร ป้าย และสิ่งก่อสร้างอื่น ๆ

NOTES

THIS DWG. USE FOR ADDITIONAL CLEARANCES BETWEEN CONDUCTOR AND BUILDING, OR SIGN OR OTHER STRUCTURE.

| | | |
|---|---|---|
| กองวิศวกรรมไฟฟ้าและเครื่องกล<br>ฝ่ายวิศวกรรม | การไฟฟ้าส่วนภูมิภาค | ใช้แทนแบบ.....<br>ถูกแทนโดยแบบ..... |
| ผู้เขียน สมนึก สาคร<br>ผู้สำรวจ.....<br>วิศวกร.....<br>หัวหน้าแผนก.....<br>ผู้อำนวยการกอง.....<br>ผู้อำนวยการฝ่าย..... | ผู้ว่าการ..... 15 พ.ย. 2541 | เขียนเสร็จวันที่ 21 ตค. 2541<br>แก้แบบวันที่ .....<br>มิติเป็น มิลลิเมตร<br>มาตราส่วน..... |
| | 115 kV วงจรเดี่ยว สายไฟฟ้าเดี่ยว<br>เสาสำหรับทางตรง<br>แบบ SS-TG-6 | |
| รองผู้ว่าการเทคนิคและบริการ<br>..... | 115 kV SINGLE CIRCUIT SINGLE CONDUCTOR<br>TANGENT STRUCTURE<br>TYPE SS-TG-6 | แบบเลขที่ SA1-015/41014<br>แผ่นที่ 4 ของจำนวน 4 แผ่น |