
การประกอบเลขที่
ASSEMBLY NO. 5206

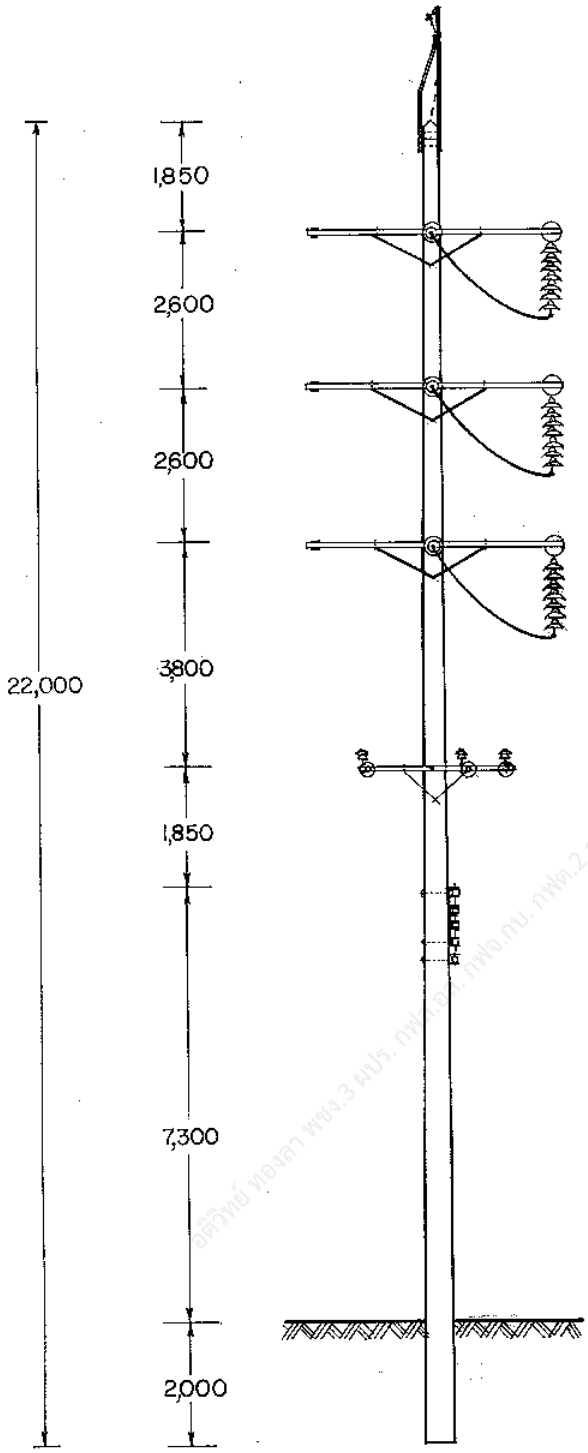

แบบ
TYPE SS-AS-1

JAPANESE EXPERT TO PEA. Y. Yamada

กองวิศวกรรม

ผู้เขียน
ตรวจทาน
วิศวกร
หัวหน้าแผนก
ผู้อำนวยการกอง
รองผู้ว่าการฝ่ายเทคนิค

การไฟฟ้าส่วนภูมิภาค


ผู้ว่าการ


แผนโครงสร้างเสาสังระนม 115 kV
วงจรเดี่ยว
แผนเสาสำหรับทางโค้ง (ช่วงไม่รับแรงดึง)


115 kV LINE STRUCTURE CONSTRUCTION
SINGLE CIRCUIT
ANGLE STRUCTURE (SLACK SPAN)

ใช้แทนแบบ
ถูกแทนโดยแบบ
เขียนเสร็จวันที่ 17 มีค. 19
แก้แบบครั้งที่ 24 มีค. 23
มิติเป็น มม.
มาตราส่วน 1 : 125
แบบเลขที่ S02-015/19024
แผ่นที่ 1 ของจำนวน 4 แผ่น

การประกอบเลขที่ ASSEMBLY NO. 5206

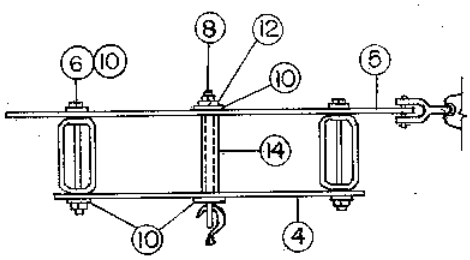

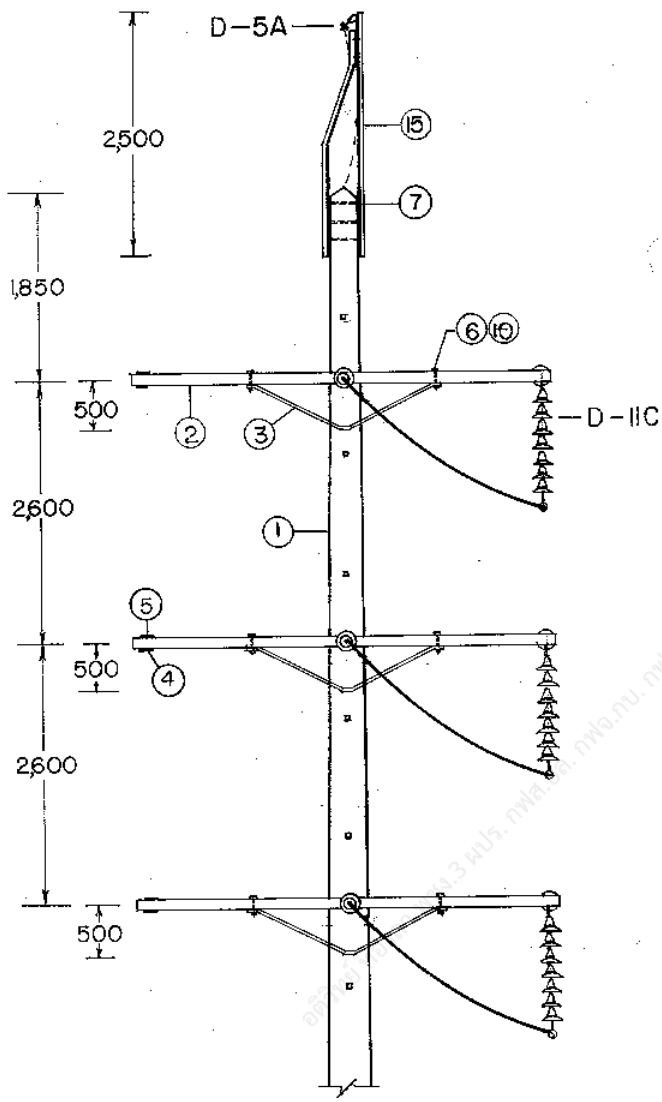

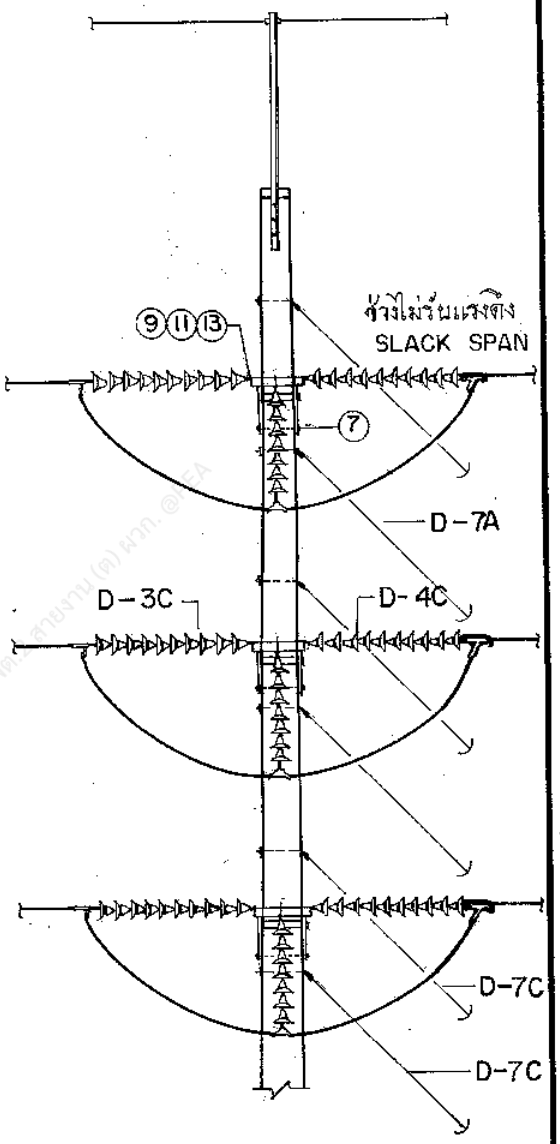

JAPANESE EXPERT TO PEA.

กองวิศวกรรม	การไฟฟ้าส่วนภูมิภาค	ใช้แทนแบบ.....
ผู้เขียน.....	ผู้ว่าการ.....	ถูกแทนโดยแบบ.....
ตรวจทาน.....	แผนโครงสร้างเสาสายระบบ 115 kV	เขียนเสร็จวันที่ 17 มิถุนายน 19
วิศวกร.....	วงจรเดียว	แก้แบบวันที่ 24 มีนาคม 23
หัวหน้าแผนก.....	แผนเสาสำหรับทางโค้ง (ช่วงไม่รับแรงดึง)	15 กันยายน 40
ผู้อำนวยการกอง.....	115 kV LINE STRUCTURE CONSTRUCTION	มิติเป็น มม.
รองผู้ว่าการฝ่ายเทคนิค.....	SINGLE CIRCUIT	มาตราส่วน 1 : 75
	ANGLE STRUCTURE (SLACK SPAN)	แบบเลขที่ S02-015/19024
		แผ่นที่ 2 รวมจำนวน 4 แผ่น

การประกอบเลขที่ ASSEMBLY NO. 5206

บัญชีวัสดุ
BILL OF MATERIAL

ลำดับที่ ITEM	รายละเอียด DESCRIPTION	จำนวน REQ'D	รหัสวัสดุที่ MAT'L NO.
1	เสาคอนกรีต 22 ม. POLE, CONCRETE 22 m LONG	1	00010011 (0041)
2	คอนสำเร็จแผ่นเหล็ก 100 x 50x3.2 มม. ยาว 4.20 ม. CROSSARM, STEEL 100 x 50x3.2 mm 4.20 m LONG	6	00120001 (0116)
3	เหล็กฉากรั้นคอนสำเร็จขนาด 50 x 50 x 6 มม. ช่างกว้าง 1800 มม.ความลึก 450 มม. BRACE, ANGLE STEEL, 50 x 50 x 6 mm. 1800 mm. WIDE 450 mm. DROP	6	00120007 (1119)
4	แผ่นเหล็กขนาด 6 x 100 x 450 มม. PLATE, STEEL 6 x 100 x 450 mm.	6	01030002 (0143)
5	แผ่นเหล็กรั้นสอง สำหรับ ขนาด 12 x 100 x 650 มม. PLATE, STEEL, DOUBLE ARMING 12 x 100 x 650 mm.	6	01030100 (0145)
6	สลักเกลียว M 16 x 170 มม. BOLT, MACHINE M 16 x 170 mm.	24	01110201 (0221)
7	สลักเกลียว M 16 x 350 มม. BOLT, MACHINE M 16 x 350 mm.	6	01110205 (0225)
8	สลักห่วงโอเวล M 16 x 150 มม. BOLT, OVAL EYE M 16 x 150 mm.	3	01150000 (0257)
9	สลักห่วงโอเวล M 20 x 450 มม. BOLT, OVAL EYE M 20 x 450 mm.	3	01150101 (0261)
10	แหวนสี่เหลี่ยมจัตุรัส 52 X 52 X 4.5 มม.รู Ø 18 มม. มอก. 258 WASHER, SQUARE, FLAT 52X52X4.5 mm. HOLE Ø 18 mm. TIS. 258	42	01180100 (0355)
11	แหวนสี่เหลี่ยมแบน 62 X 62 X 6 มม.รู Ø 22 มม. มอก. 258 WASHER, SQUARE, FLAT 62 X 62 X 6 mm. HOLE Ø 22 mm TIS 258	6	01180101 (0356)
12	แหวนสปริง M 16 มอก. 259 WASHER, LOCK, M 16, TIS 259	3	01180301 (0365)
13	แหวนสปริง M 20 มอก. 259 WASHER, LOCK, M 20, TIS 259	3	01180302 (0366)
14	ท่อเหล็กขนาด 20 มม. หนา 2.65 มม. ยาว 100 มม. มอก. 277 ประเภท 2 PIPE, IRON DIA. 20 mm ID. 2.65 THICKNESS 100 mm LONG, TIS 277, TYPE 2	3	01050000 (0905)
15	เหล็กฉากรั้นสายล่อฟ้าทางโค้ง OVERHEAD GROUND WIRE CORNER BAYONET	1	01010005 (0136)

JAPANESE EXPERT TO PEA.

กองวิศวกรรม

ผู้เขียน
สัตาปนิก
วิศวกร
หัวหน้าแผนก
ผู้อำนวยการกอง
รองผู้ว่าการฝ่ายเทคนิค

การไฟฟ้าส่วนภูมิภาค

ผู้ว่าการ

แบบโครงสร้างเสาส่งระบบ 115 kV
วงจรเดี่ยว
แบบเสาสำหรับทางโค้ง (ช่วงไม่รับแรงดึง)

115 kV LINE STRUCTURE CONSTRUCTION
SINGLE CIRCUIT
ANGLE STRUCTURE (SLACK SPAN)

ใช้แทนแบบ
ถูกแทนโดยแบบ
เขียนเสร็จวันที่ 17 มี.ค. 19
แก้แบบวันที่ 24 มี.ค. 23
ผู้เขียน
มาตราส่วน
แบบเลขที่ S02-015/19024
แผ่นที่ 3 จากจำนวน 4 แผ่น

การประกอบเลขที่ ASSEMBLY NO. 5206

บัญชีวัสดุ
BILL OF MATERIAL

ลำดับที่ ITEM	รายละเอียด DETAIL	จำนวน REQ'D	หมายเลขที่ PART NO.
D-3C	การประกอบลูกถ้วยแขวน SUSPENSION INSULATOR ASSEMBLY	3	
D-4C	การประกอบลูกถ้วยแขวน SUSPENSION INSULATOR ASSEMBLY	3	
D-5A	การต่อสายล่อฟ้า OVERHEAD GROUND WIRE CONNECTION	1	
D-7A	การประกอบสายยึดโยงลวดเหล็กตีเกลียว 95 ตร.มม. STEEL STRANDED WIRE 95 mm^2 GUY ASSEMBLY	4	
D-7C	การประกอบสายยึดโยงลวดเหล็กตีเกลียว 95 ตร.มม. STEEL STRANDED WIRE 95 mm^2 GUY ASSEMBLY	2	
D-9B	สมอฝังคอนกรีต CONCRETE ANCHOR	1	
D-10A	ฐานรากเสา POLE FOUNDATION	1	
D-11C	การประกอบลูกถ้วยแขวน SUSPENSION INSULATOR ASSEMBLY	3	

JAPANESE EXPERT TO PEA.

กองวิศวกรรม	การไฟฟ้าส่วนภูมิภาค	ใช้แทนแบบ.....
ผู้เขียน.....	ผู้ว่าการ.....	ลอกแทนโดยแบบ.....
ผู้ตรวจ.....	แบบโครงสร้างเสาสิ้นสุดระบบ 115 kV วงจรเดี่ยว แบบเสาสำหรับทางโค้ง (ช่วงไม่รับแรงดึง)	เขียนเสร็จวันที่ 17 มี.ค. 19 แก้แบบวันที่ 24 มี.ค. 23 15 พ.ย. 40
หัวหน้าแผนก.....	115 kV LINE STRUCTURE CONSTRUCTION SINGLE CIRCUIT ANGLE STRUCTURE (SLACK SPAN)	ผู้เขียน.....
ผู้อำนวยการกอง.....		ตรวจสอบ.....
รองผู้ว่าการฝ่ายเทคนิค.....		แบบเลขที่ S02-015/19024
		แผ่นที่ 4 จากทั้งหมด 4 แผ่น