
การประกอบเลขที่ ASSEMBLY NO. 3206

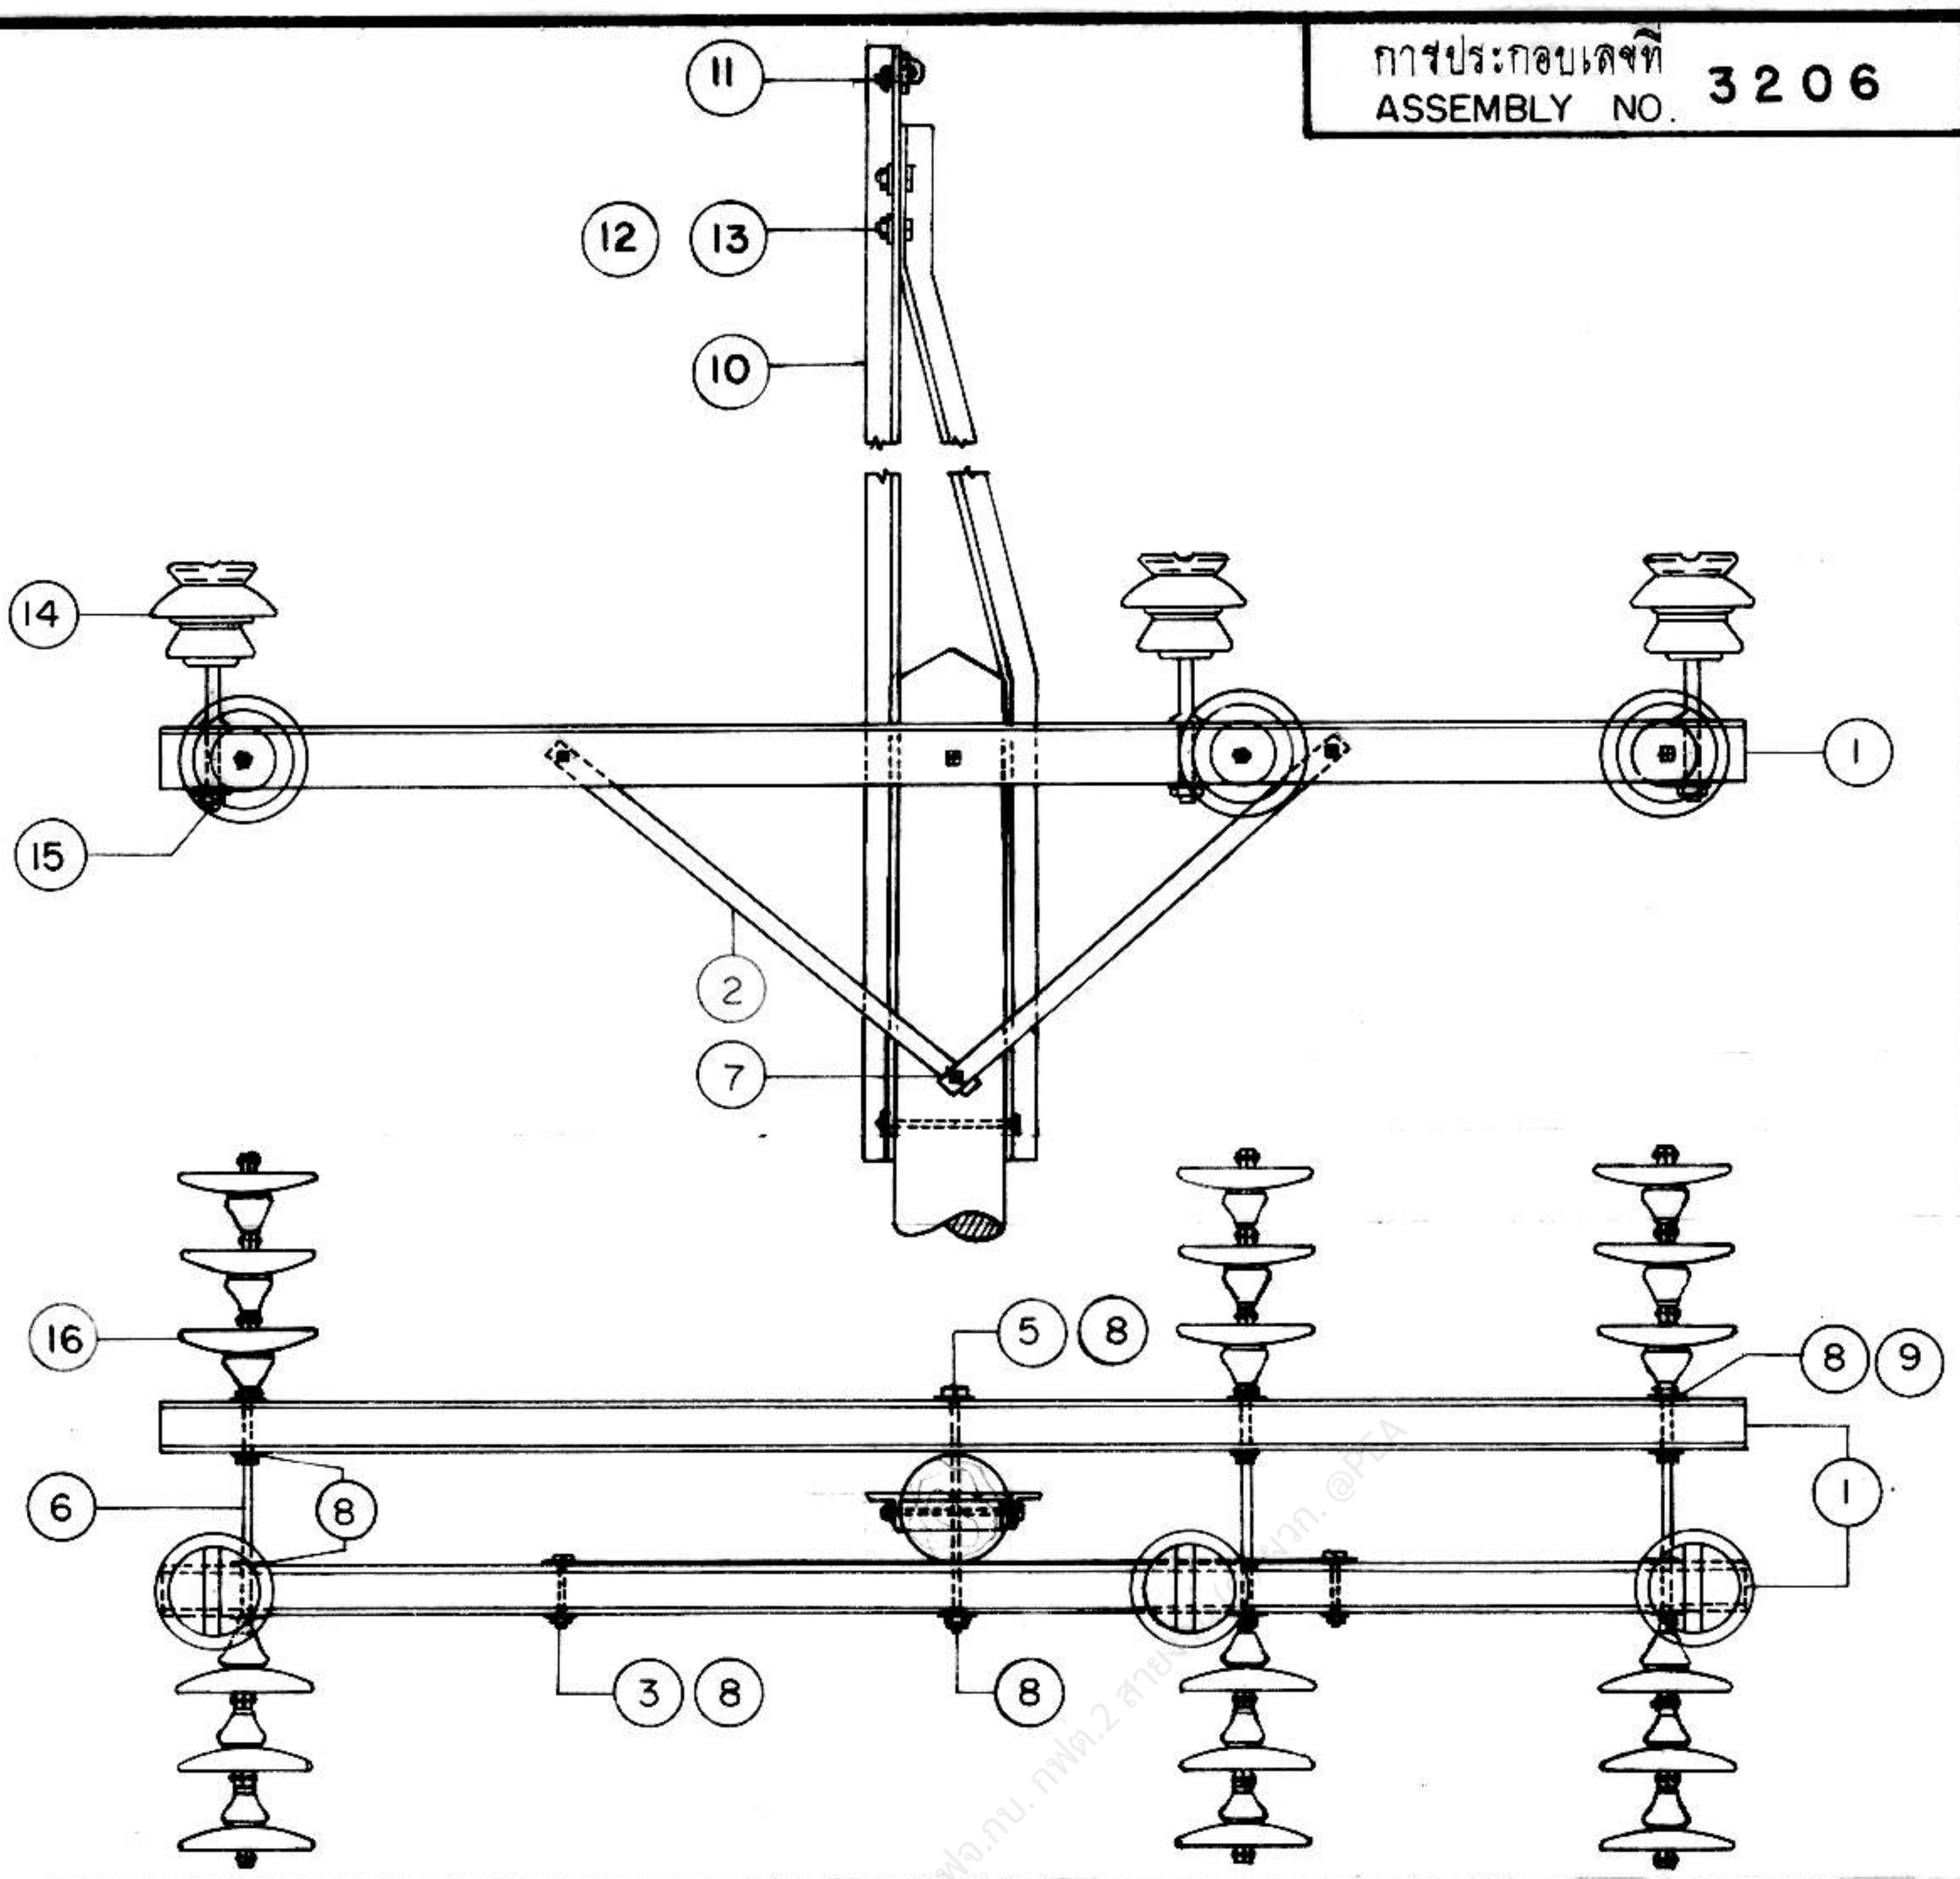

BILL OF MATERIAL

ITEM	DESCRIPTION	REQ'D	MAT. NO.
1	ไม้คอนสายขนาด 100 X 120 X 3,000 มม. CROSSARM (HT.) WOOD, 100 X 120 X 3,000 mm	2	00100003 (0101)
2	เหล็กปะกันไม้คอน 40 X 6 X 1,000 มม. BRACE, FLAT, FOR CROSSARM , 40 X 6 X 1,000 mm	2	01200002 (0121)
3	สลักเกลียว M 16 X 130 มม. BOLT, MACHINE , M 16 X 130 mm	2	01110200 (0220)
4	สลักเกลียว M 16 X 300 มม. BOLT, MACHINE , M 16 X 300 mm	2	01110204 (0224)
5	สลักเกลียว M 16 X 450 มม. BOLT, MACHINE, M 16 X 450 mm	1	01110207 (0227)
6	สลักเกลียว ห่วงกลม M 16X450 มม. BOLT , DOUBLE ARMING, ROUND EYE , M 16X450 mm	3	01120004 (0247)
7	สลักเกลียวปลอยขนาด 16 X 130 มม. SCREW , LAG , 16 X 130 mm	1	01170001 (0325)
8	แหวนสี่เหลี่ยมแบน ขนาด 52 X 52 X 4.5 มม. รู Ø 18 มม. มอก. 258 WASHER, SQUARE, FLAT, 52 X 52 X 4.5 mm HOLE Ø 18 mm TIS 258	16	01180100 (0355)

กองวิศวกรรมและวางแผน	การไฟฟ้าส่วนภูมิภาค	ใช้แทนแบบ .....
ผู้เขียน	ผู้ว่าการ	ถูกแทนโดยแบบ .....
สถาปนิก		เขียนเสร็จวันที่ 24 ตค. 12
วิศวกร	การประกอบไม้คอนค่ากับเสาไม้	แก้แบบจันที่ .....
หัวหน้าแผนก	ระบบ 33 kV , 3 เฟส, มุม 30°-60°	มิติเป็น มม.
ผู้อำนวยการกอง		มาตราส่วน 1:25
ร่องผู้ว่าการฝ่ายเทคนิค	33 kV, DOUBLE CROSSARM ASSEMBLY ON WOOD POLE, 3-PHASE, 30°-60°	แบบเลขที่ I50-015/120309
		แผ่นที่ 1 ของจำนวน 2 แผ่น

การประกอบเลขที่ ASSEMBLY NO. 3206

BILL OF MATERIAL

ITEM	DESCRIPTION	REQ'D	MAT. NO.
9	นัทรูปห่วง M 16 DIN 582 NUT, EYE M16, DIN 582	3	01180001 (0345)
10	เหล็กฉากรับสายล่อฟ้า 60X60X6X3000 มม. OVERHEAD GROUND WIRE CORNER BAYONET	1	01010007 (0129)
11	กราวด์ไวร์แคล็มป์แบบ J 1152 GROUND WIRE CLAM J 1152	1	01230205 (0296)
12	สลักเกลียว M 12X35 มม. BOLT, MACHINE , M 12 X 35 mm	2	01110100 (0212)
13	แหวนสปริง M 12 มอก. 259 WASHER, LOCK , M 12 , TIS 259	2	01180300 (0364)
14	ลูกถ้วยก้านตรง 33 kV มอก. 279 แผน ค (แผน 56-3) INSULATOR, PIN TYPE, 33 kV TIS 279 TYPE C (CLASS 56-3)	3	03000002 (0409)
15	ก้านลูกถ้วยแรงสูง 33 kV PIN, INSULATOR	3	03100001 (0422)
16	ลูกถ้วยแขวน มอก. 354 แผน ง (แผน 52-4) INSULATOR, SUSPENSION TYPE, TIS 354 TYPE D (CLASS 52-4)	18	03020002 (0415)

อดิวิทย์ ทองลา พชง.3 ผปร. กฟส.อด. กฟจ.กบ. กฟต.2 สายงาน (ค) ผวก.

กองวิศวกรรมและจางแผน	การไฟฟ้าส่วนภูมิภาค	ใช้แทนแบบ
ผู้เขียน	ผู้จ่าการ	ถูกแทนโดยแบบ
สถาปนิก		เขียนเสร็จวันที่ 24 ตค. 12
วิศวกร	การประกอบไม้ดอนคู่กับเสาไม้	แก้แบบวันที่
หัวหน้าแผนก	ระบบ 33 kV , 3 เฟส, มุม 30°-60°	มิติเป็น
ผู้อำนวยการกอง		มาตราส่วน
รองผู้จ่าการฝ่ายเทคนิค	33 kV, DOUBLE CROSSARM ASSEMBLY ON WOOD POLE, 3-PHASE, 30°-60°	แบบเลขที่ I50-015/120309
		แผ่นที่ 2 ของจำนวน 2 แผ่น