| | |
|---|---|
| การประกอบเลขที่<br>ASSEMBLY NO. | 3244 |

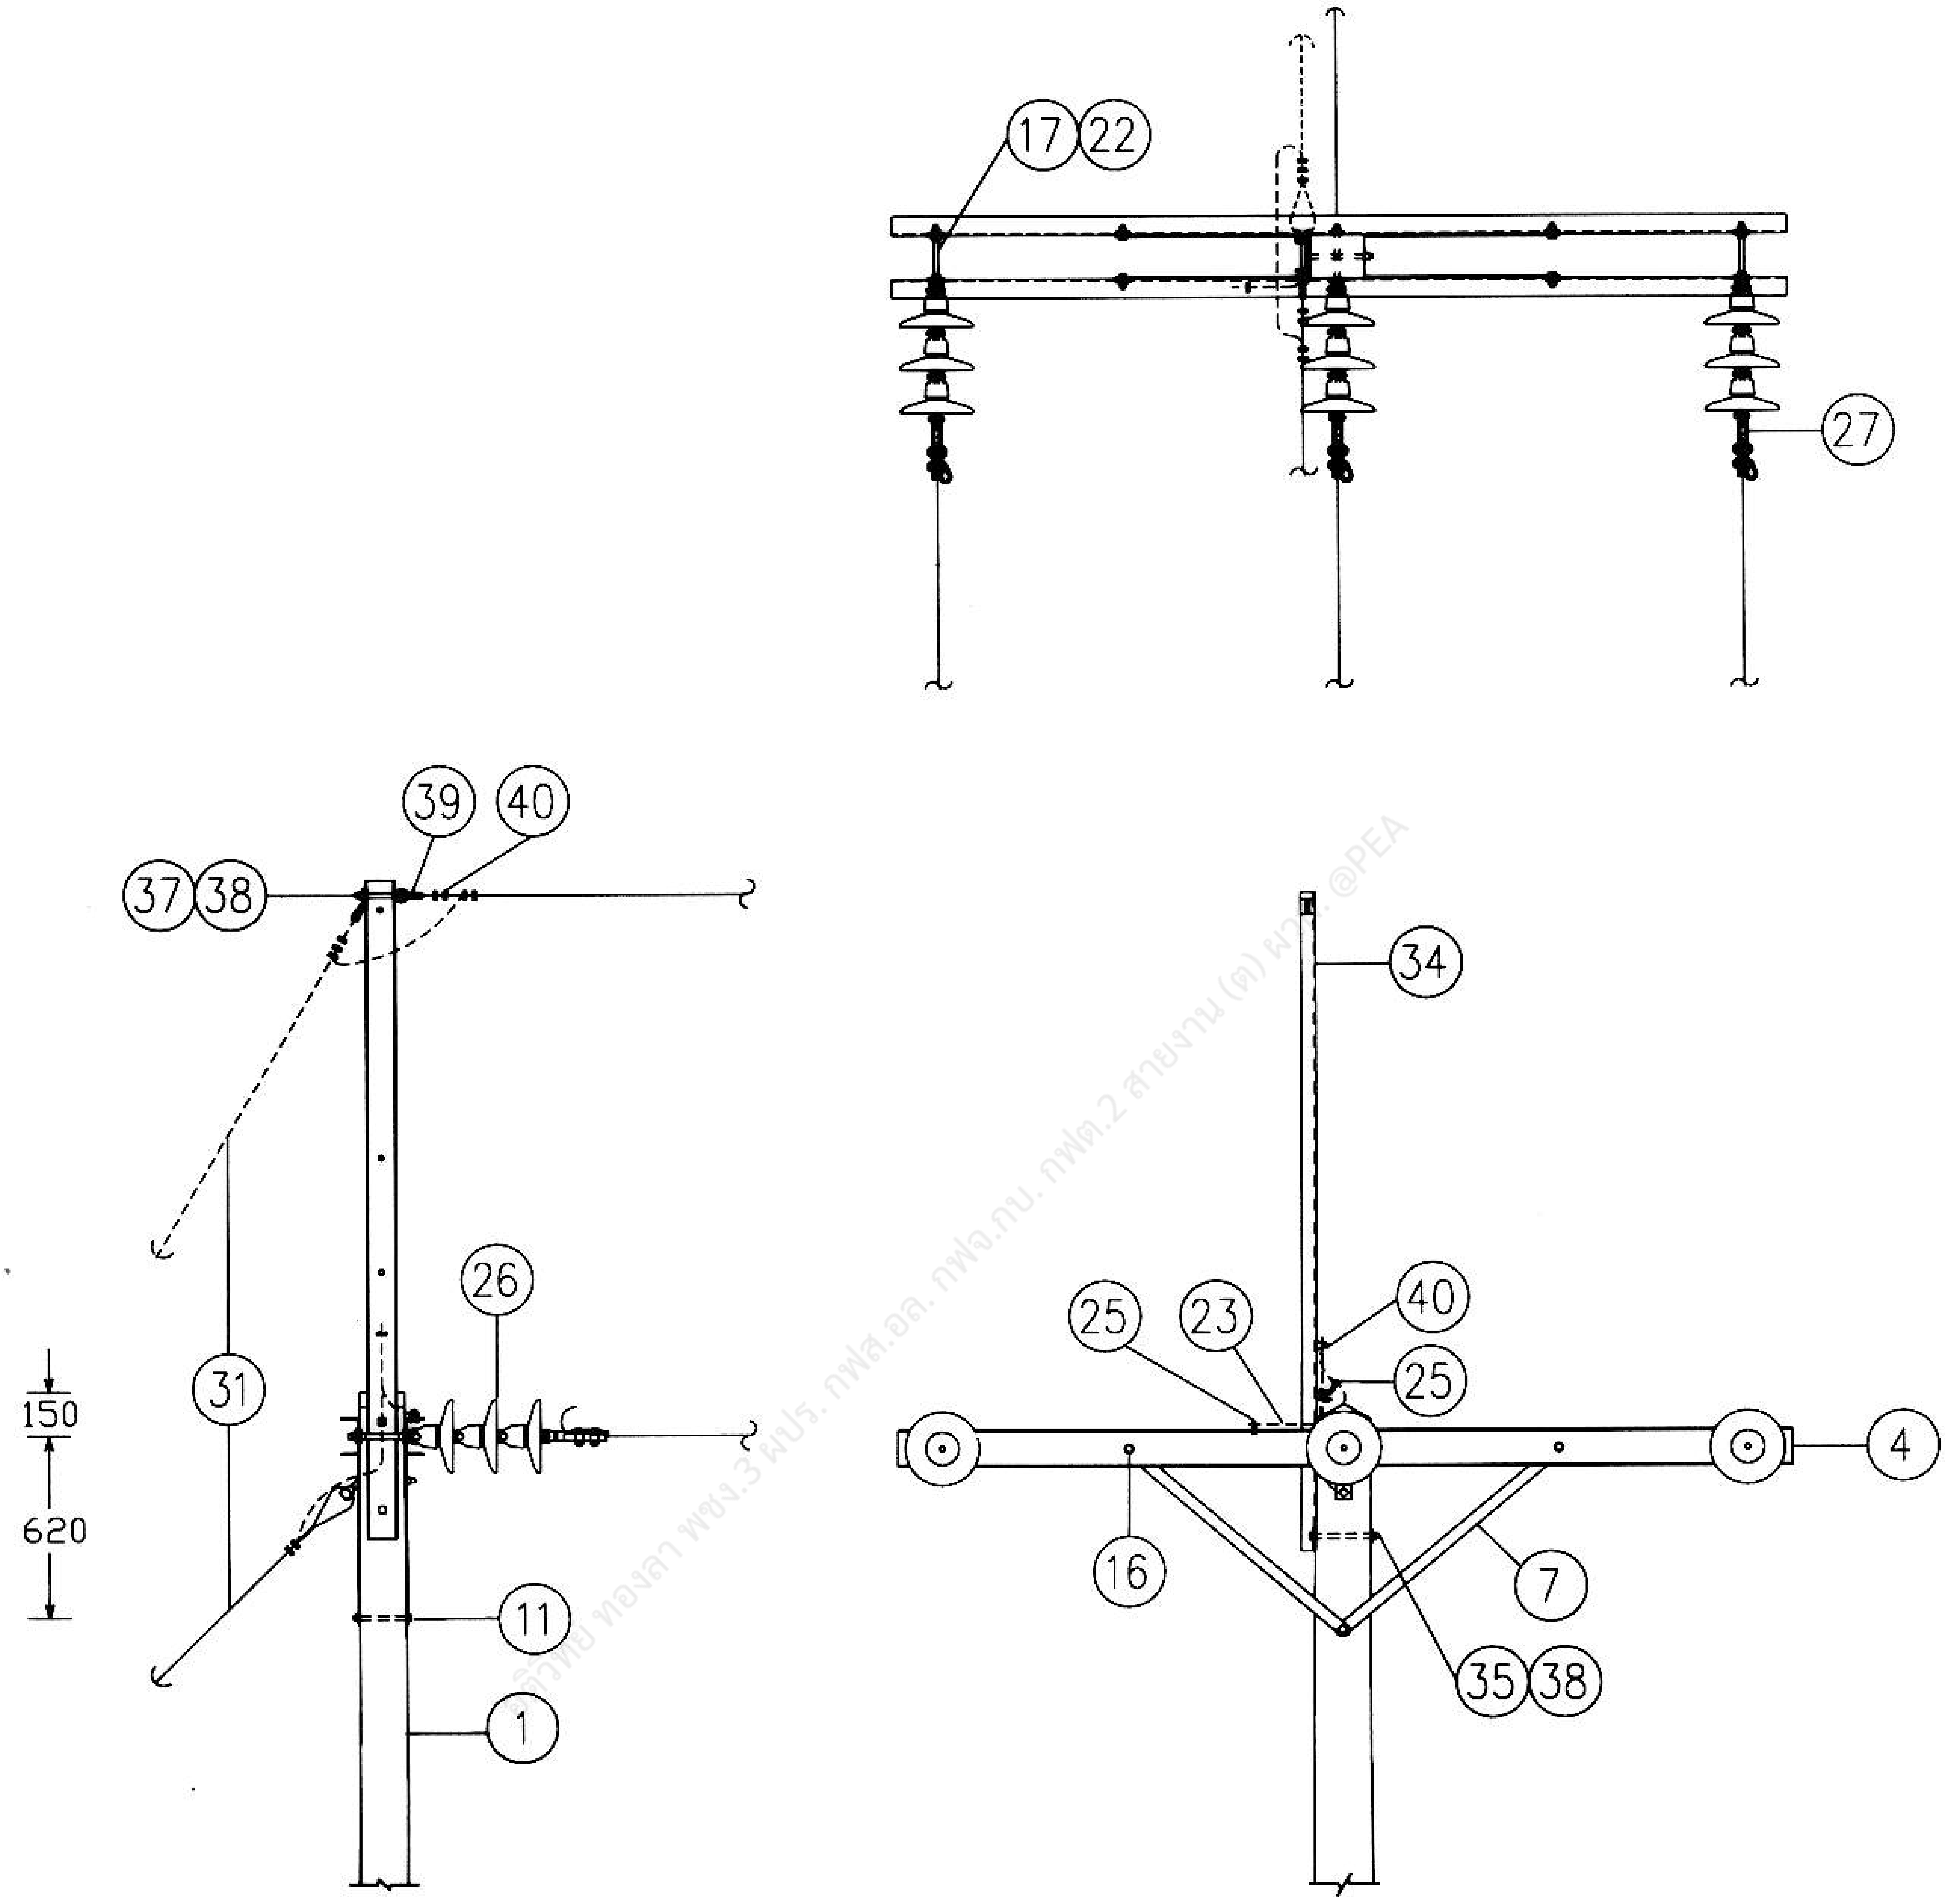

**การประกอบคอนแบบธรรมดา 1 วงจร ( กรณีพาดสายเปลือย )**

1 CIRCUIT CROSSARM ASSEMBLY ( BARE CONDUCTOR STRINGING )

ทองลา พชง.3 ผปร. กฟส.อล. กฟจ.กบ. กฟต.2 สายงาน (ต) ผวก. @PEA

กองวิศวกรรมไฟฟ้าและเครื่องกล
ฝ่ายวิศวกรรม

# การไฟฟ้าส่วนภูมิภาค

ผู้เขียน .......................
ผู้สำรวจ .......................
วิศวกร .......................
หัวหน้าแผนก .......................
ผู้อำนวยการกอง .......................
ผู้อำนวยการฝ่าย .......................

ผู้ว่าการ .......................
22 เม.ย. 2540

**การประกอบคอนเหล็กรูปรางน้ำกับเสาคอนกรีต**
**33 kV**
**สำหรับเข้าปลายสาย**

CHANNEL STEEL CROSSARM ASSEMBLY ON CONCRETE POLE
33 kV
FOR DEADENDING

รองผู้ว่าการ
.......................
22 เม.ย. 2540

ใช้แทนแบบ .......................
ถูกแทนโดยแบบ .......................
เขียนเสร็จวันที่ 25 มี.ค. 2540
แก้แบบวันที่ .......................
มิติเป็น มิลลิเมตร
มาตราส่วน 1 : 40
แบบเลขที่ SA4-015/40006
แผ่นที่ 1 ของจำนวน 9 แผ่น

การประกอบเลขที่ 
ASSEMBLY NO. **3244**

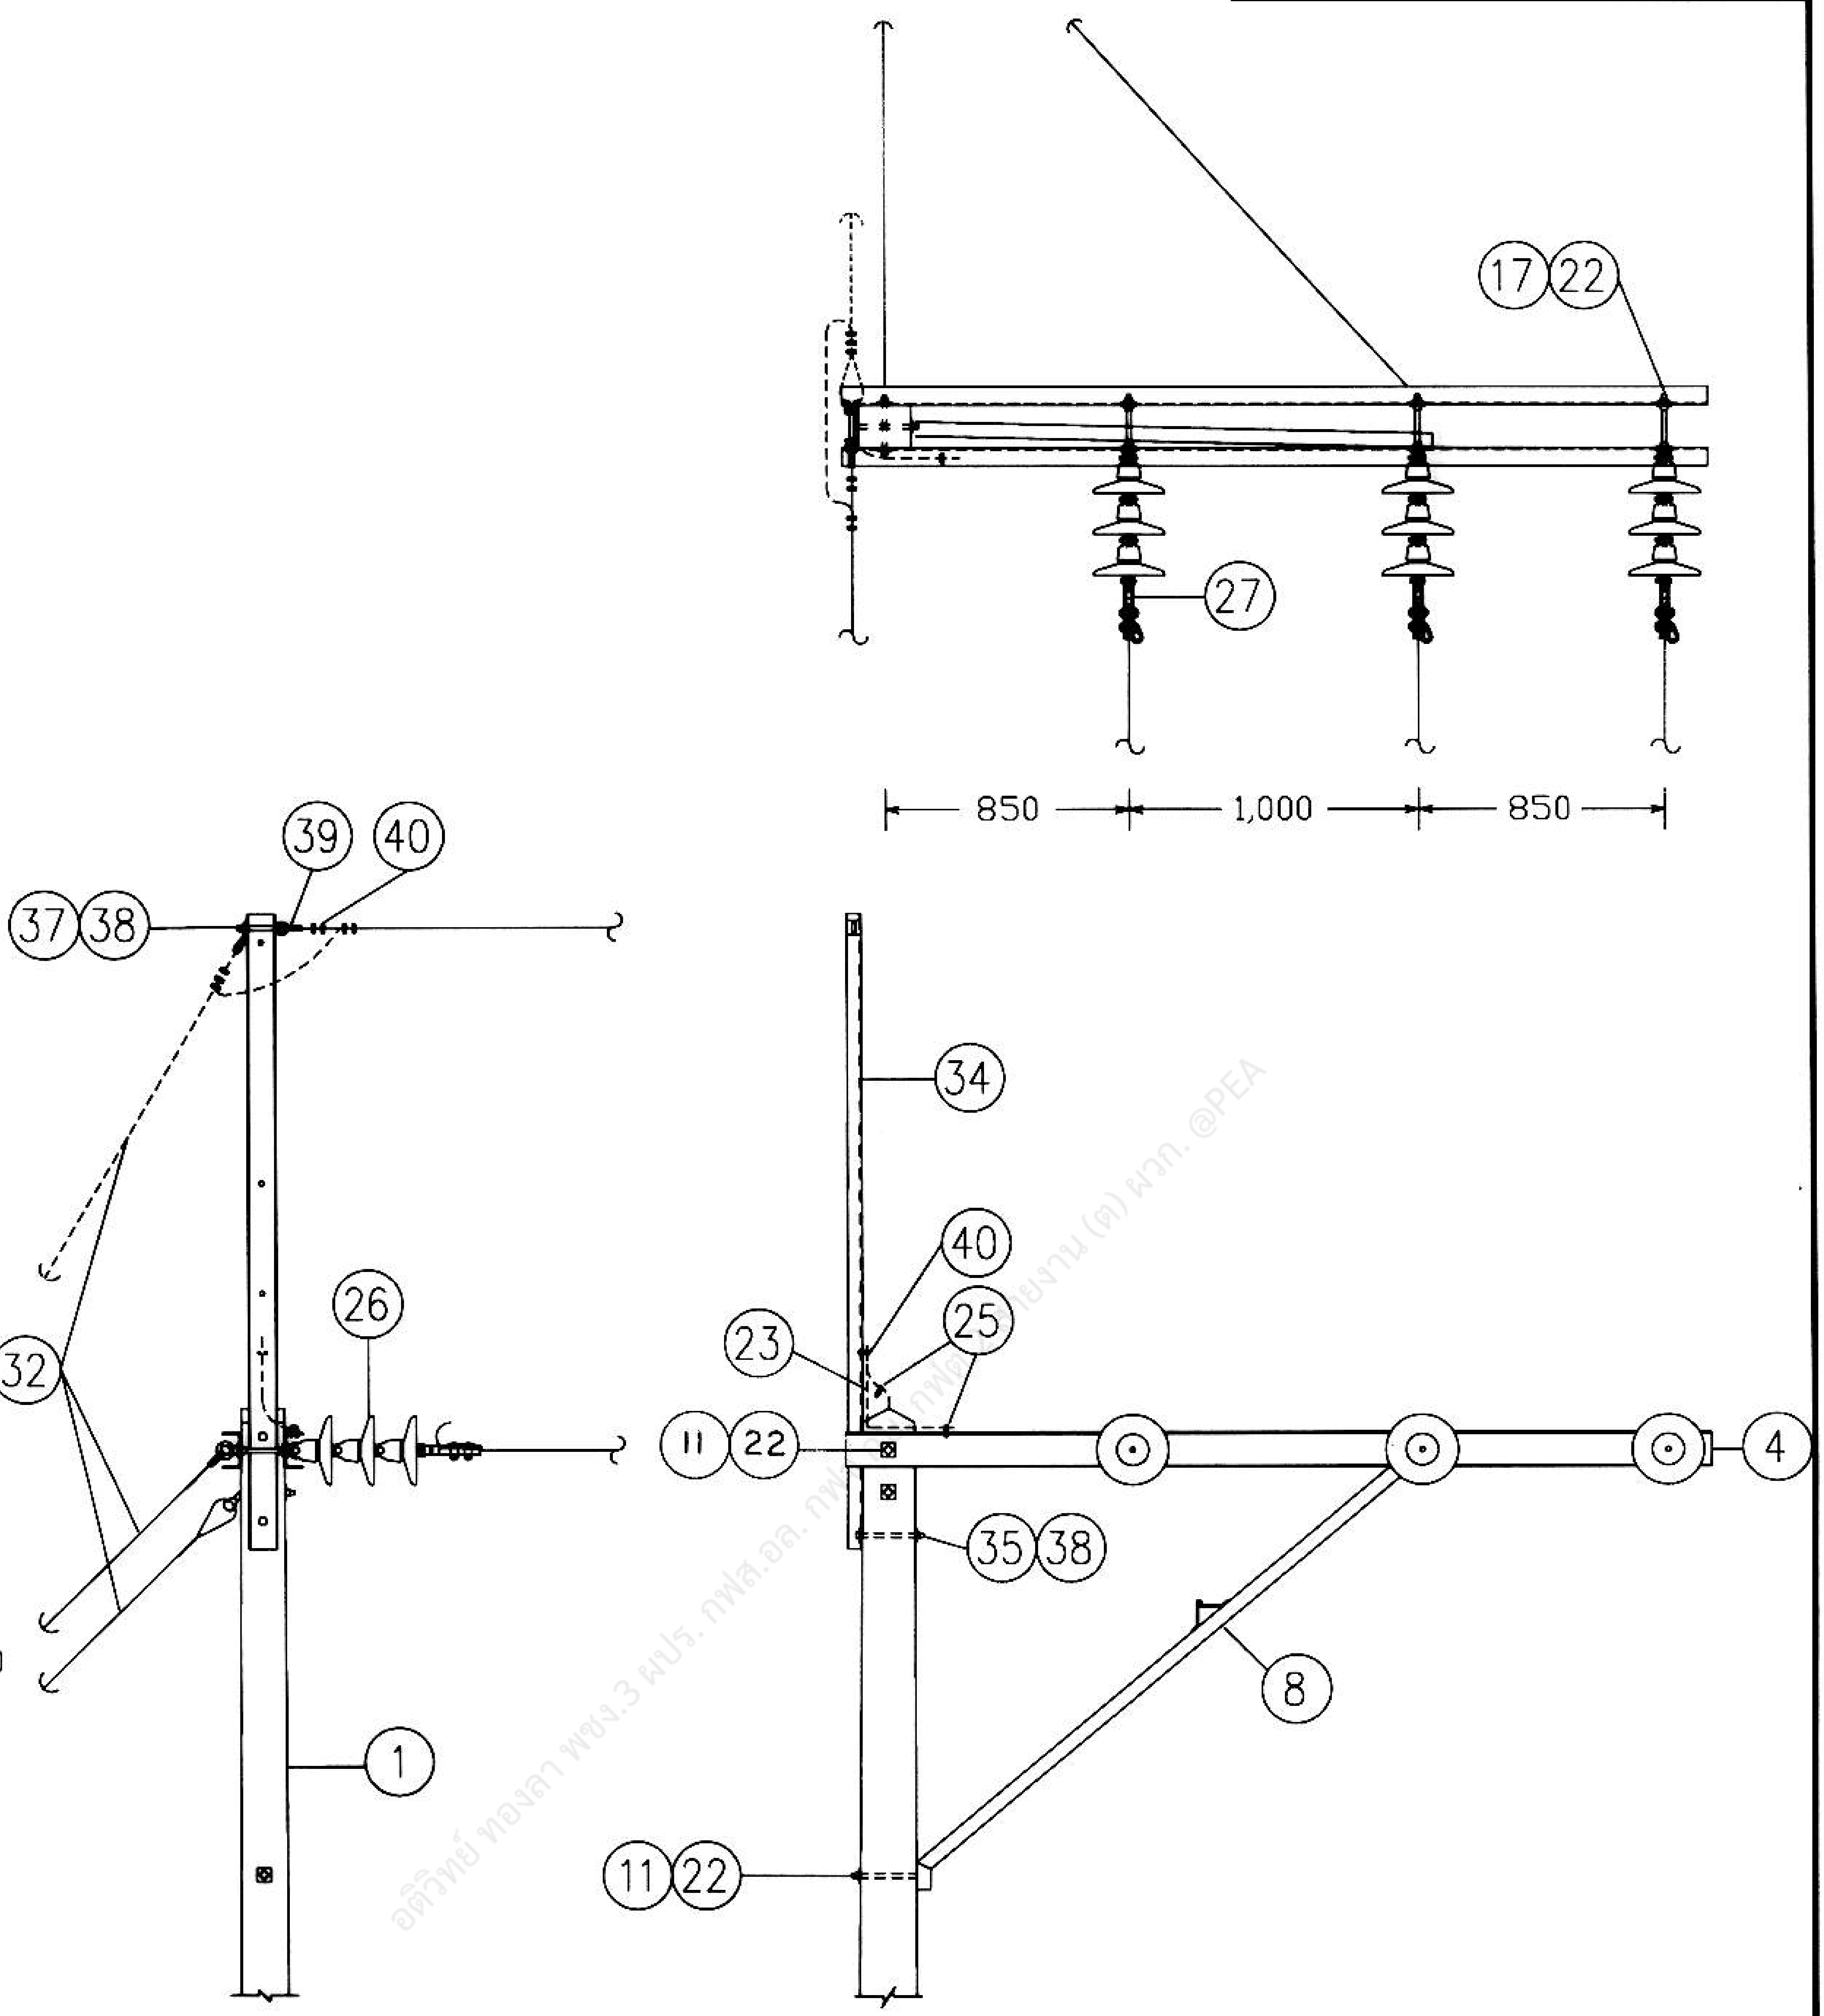

อดิวิทย์ ทองลา พชง.3 ผปร. กฟส.อล. กฟ[illegible] ...ยงาน (ต) ผวก. @PEA

II **การประกอบคอนแบบท้าวแขน 1 วงจร ( กรณีพาดสายเปลือย )**
1 CIRCUIT ALLEY ARM ASSEMBLY ( BARE CONDUCTOR STRINGING )

กองวิศวกรรมไฟฟ้าและเครื่องกล
ฝ่ายวิศวกรรม

# การไฟฟ้าส่วนภูมิภาค

ผู้เขียน B. Supphalit
ผู้สำรวจ
วิศวกร
หัวหน้าแผนก
ผู้อำนวยการกอง
ผู้อำนวยการฝ่าย

ผู้ว่าการ
22 เม.ย. 2540

**การประกอบคอนเหล็กรูปรางน้ำกับเสาคอนกรีต**
**33 kV**
**สำหรับเข้าปลายสาย**

CHANNEL STEEL CROSSARM ASSEMBLY ON CONCRETE POLE
33 kV
FOR DEADENDING

รองผู้ว่าการ
22 เม.ย. 2540

ใช้แทนแบบ ..............
ถูกแทนโดยแบบ ..............
เขียนเสร็จวันที่ 25 มี.ค. 2540
แก้แบบวันที่ ..............
มิติเป็น มิลลิเมตร
มาตราส่วน 1 : 40
แบบเลขที่ SA4-015/40006
แผ่นที่ 2 ของจำนวน 9 แผ่น

การประกอบเลขที่
ASSEMBLY NO. **3244**

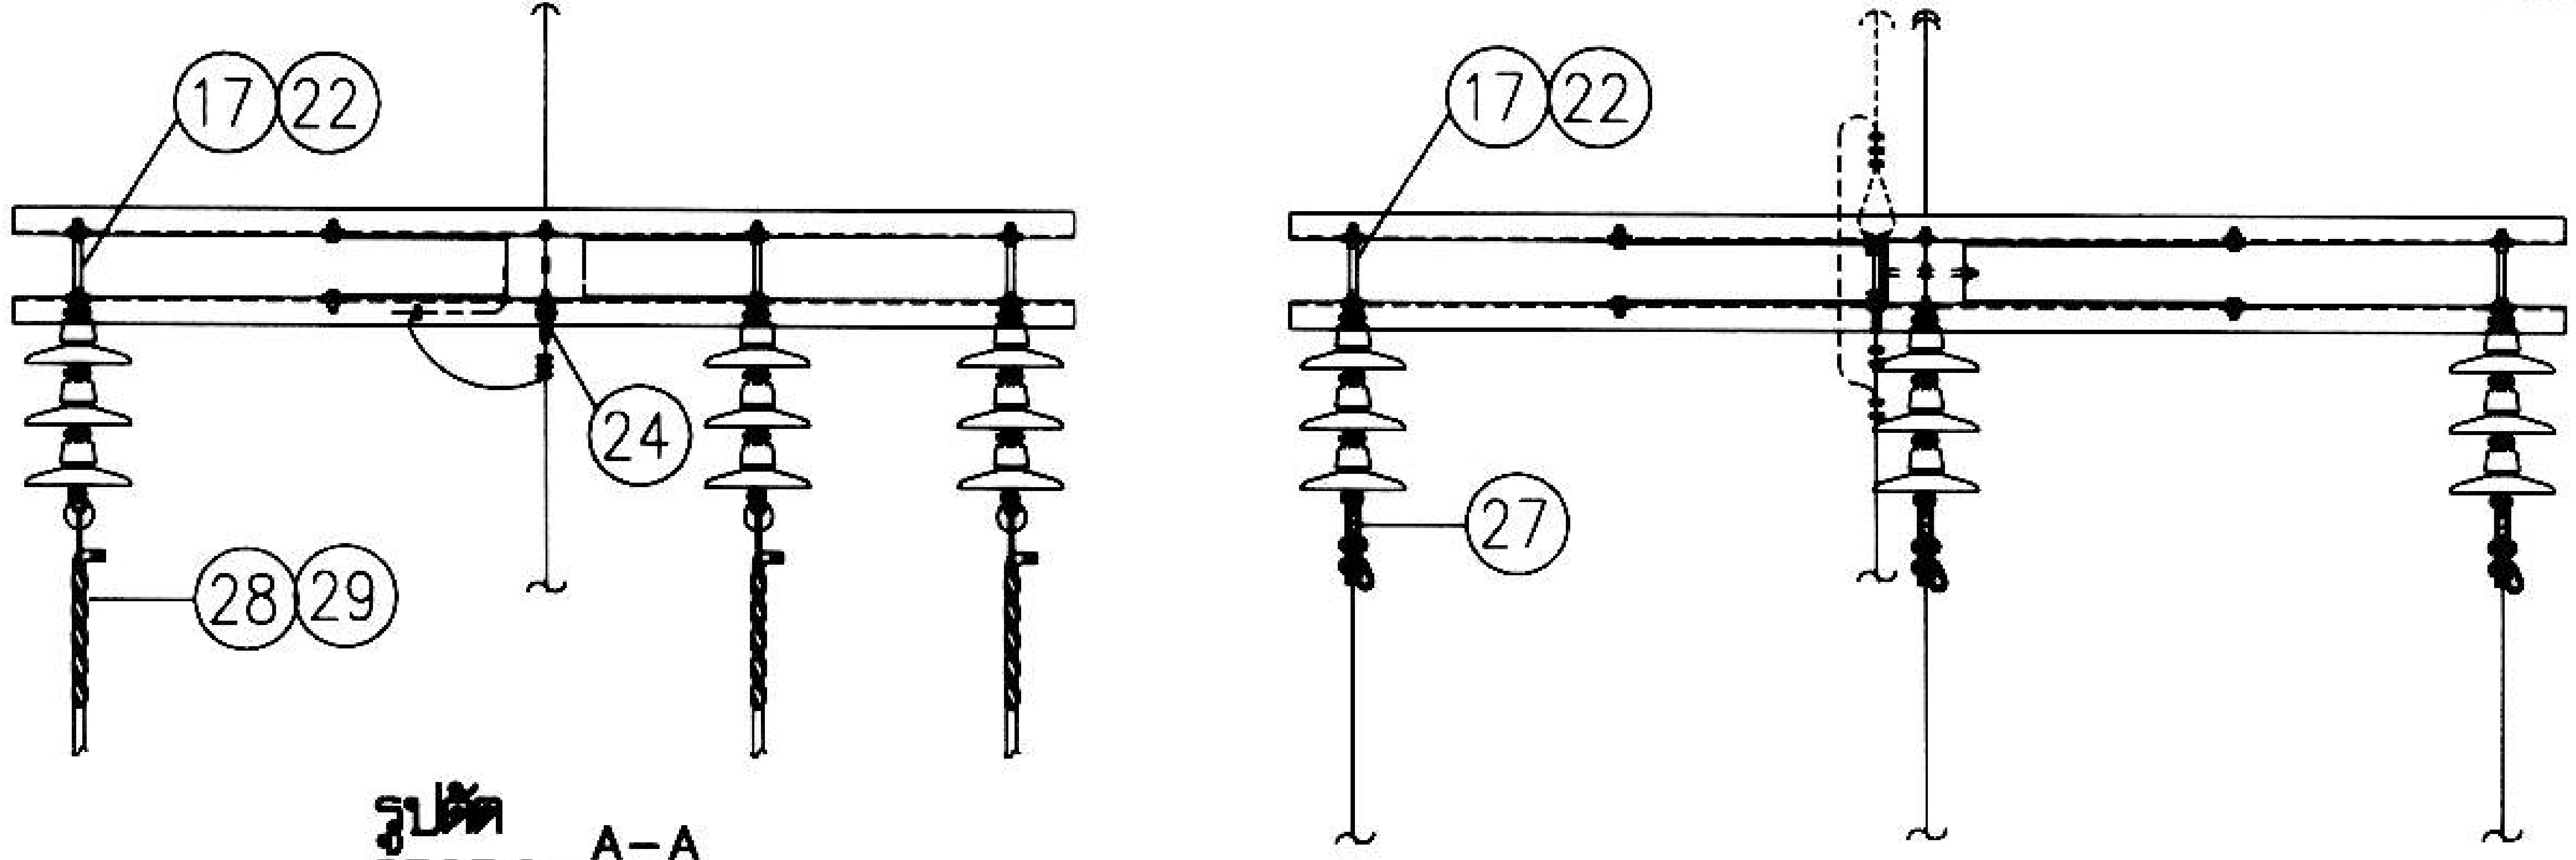

รูปตัด
SECTION A–A

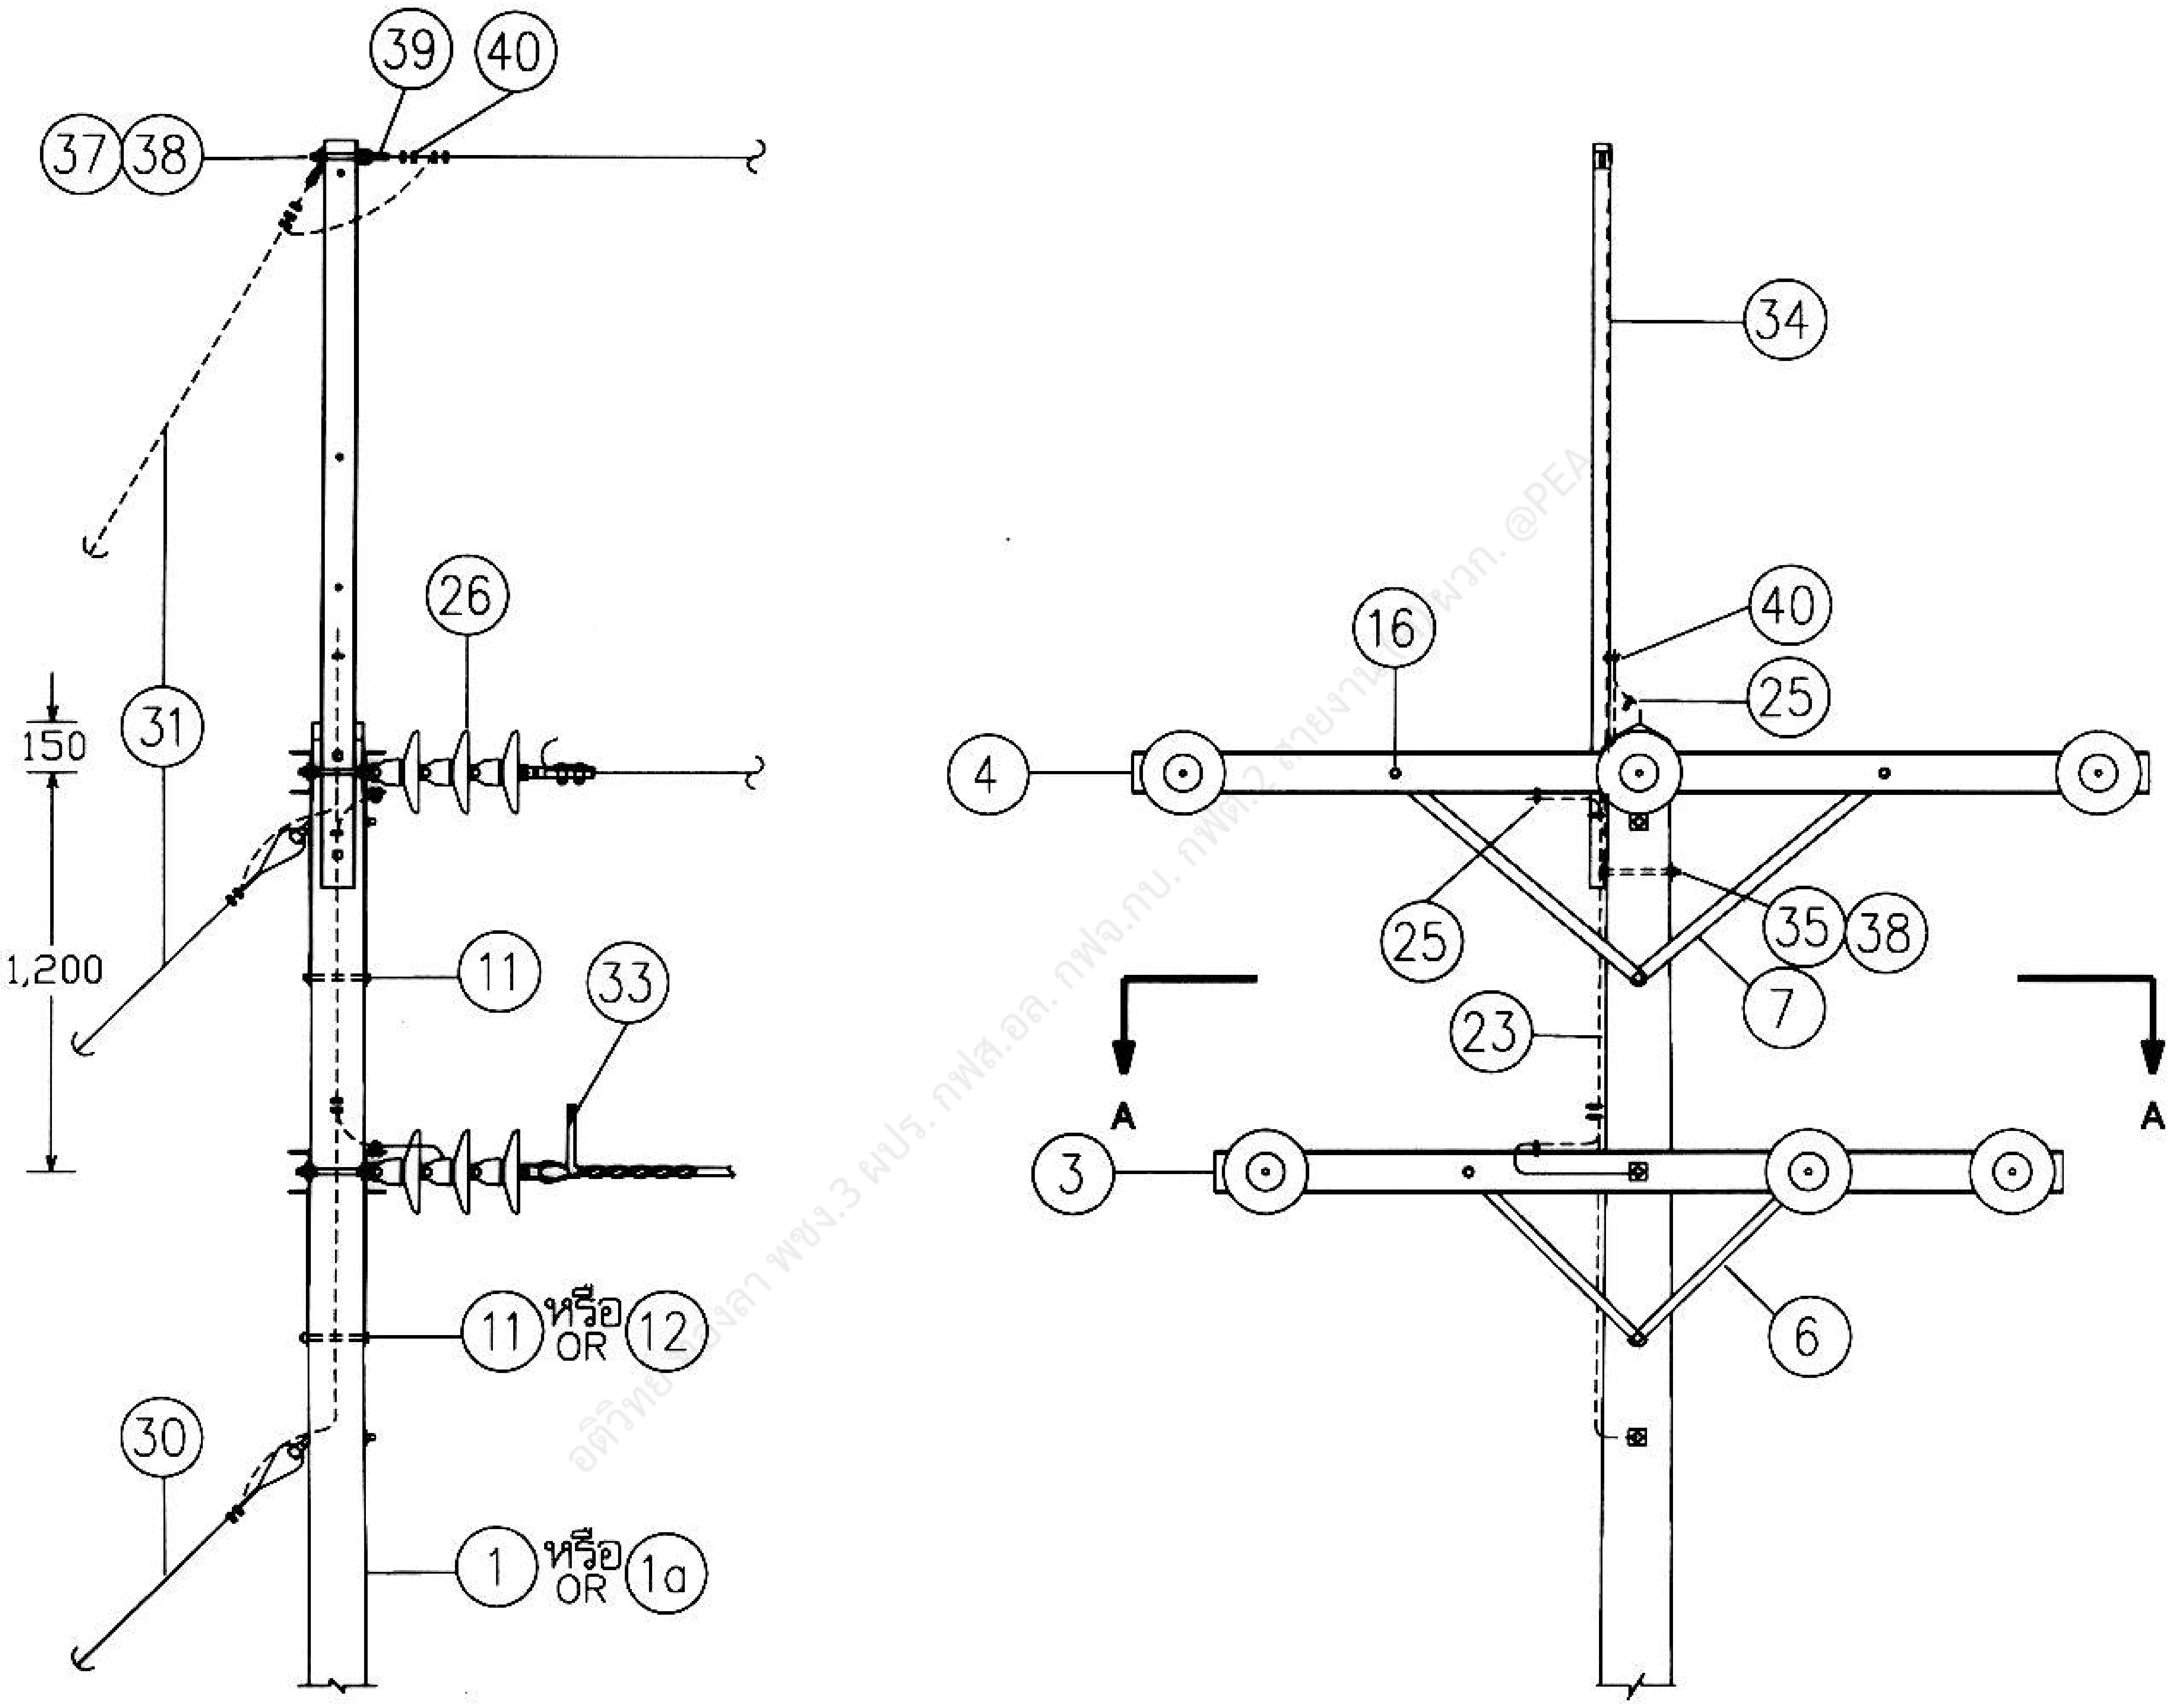

III **การประกอบคอนแบบธรรมดา 2 วงจร ( กรณีพาดสายเปลือย 1 วงจร และเคเบิลอากาศ 1 วงจร )**
2 CIRCUIT CROSSARM ASSEMBLY ( 1 CIRCUIT BARE CONDUCTOR AND 1 CIRCUIT AERIAL CABLE )

กองวิศวกรรมไฟฟ้าและเครื่องกล
ฝ่ายวิศวกรรม

ผู้เขียน ..................
ผู้สำรวจ ..................
วิศวกร ..................
หัวหน้าแผนก ..................
ผู้อำนวยการกอง ..................
ผู้อำนวยการฝ่าย ..................

รองผู้ว่าการ
..................
22 เม.ย. 2540

# การไฟฟ้าส่วนภูมิภาค

ผู้ว่าการ ..................
22 เม.ย. 2540

การประกอบคอนเหล็กรูปรางน้ำกับเสาคอนกรีต
33 kV
สำหรับเข้าปลายสาย

CHANNEL STEEL CROSSARM ASSEMBLY ON CONCRETE POLE
33 kV
FOR DEADENDING

ใช้แทนแบบ ..................
ถูกแทนโดยแบบ ..................
เขียนเสร็จวันที่ 25 มีค. 2540
แก้แบบวันที่ ..................
มิติเป็น มิลลิเมตร
มาตราส่วน ..................
แบบเลขที่ SA4–015/40006
แผ่นที่ 3 ของจำนวน 9 แผ่น

การประกอบเลขที่ ASSEMBLY NO. **3244**

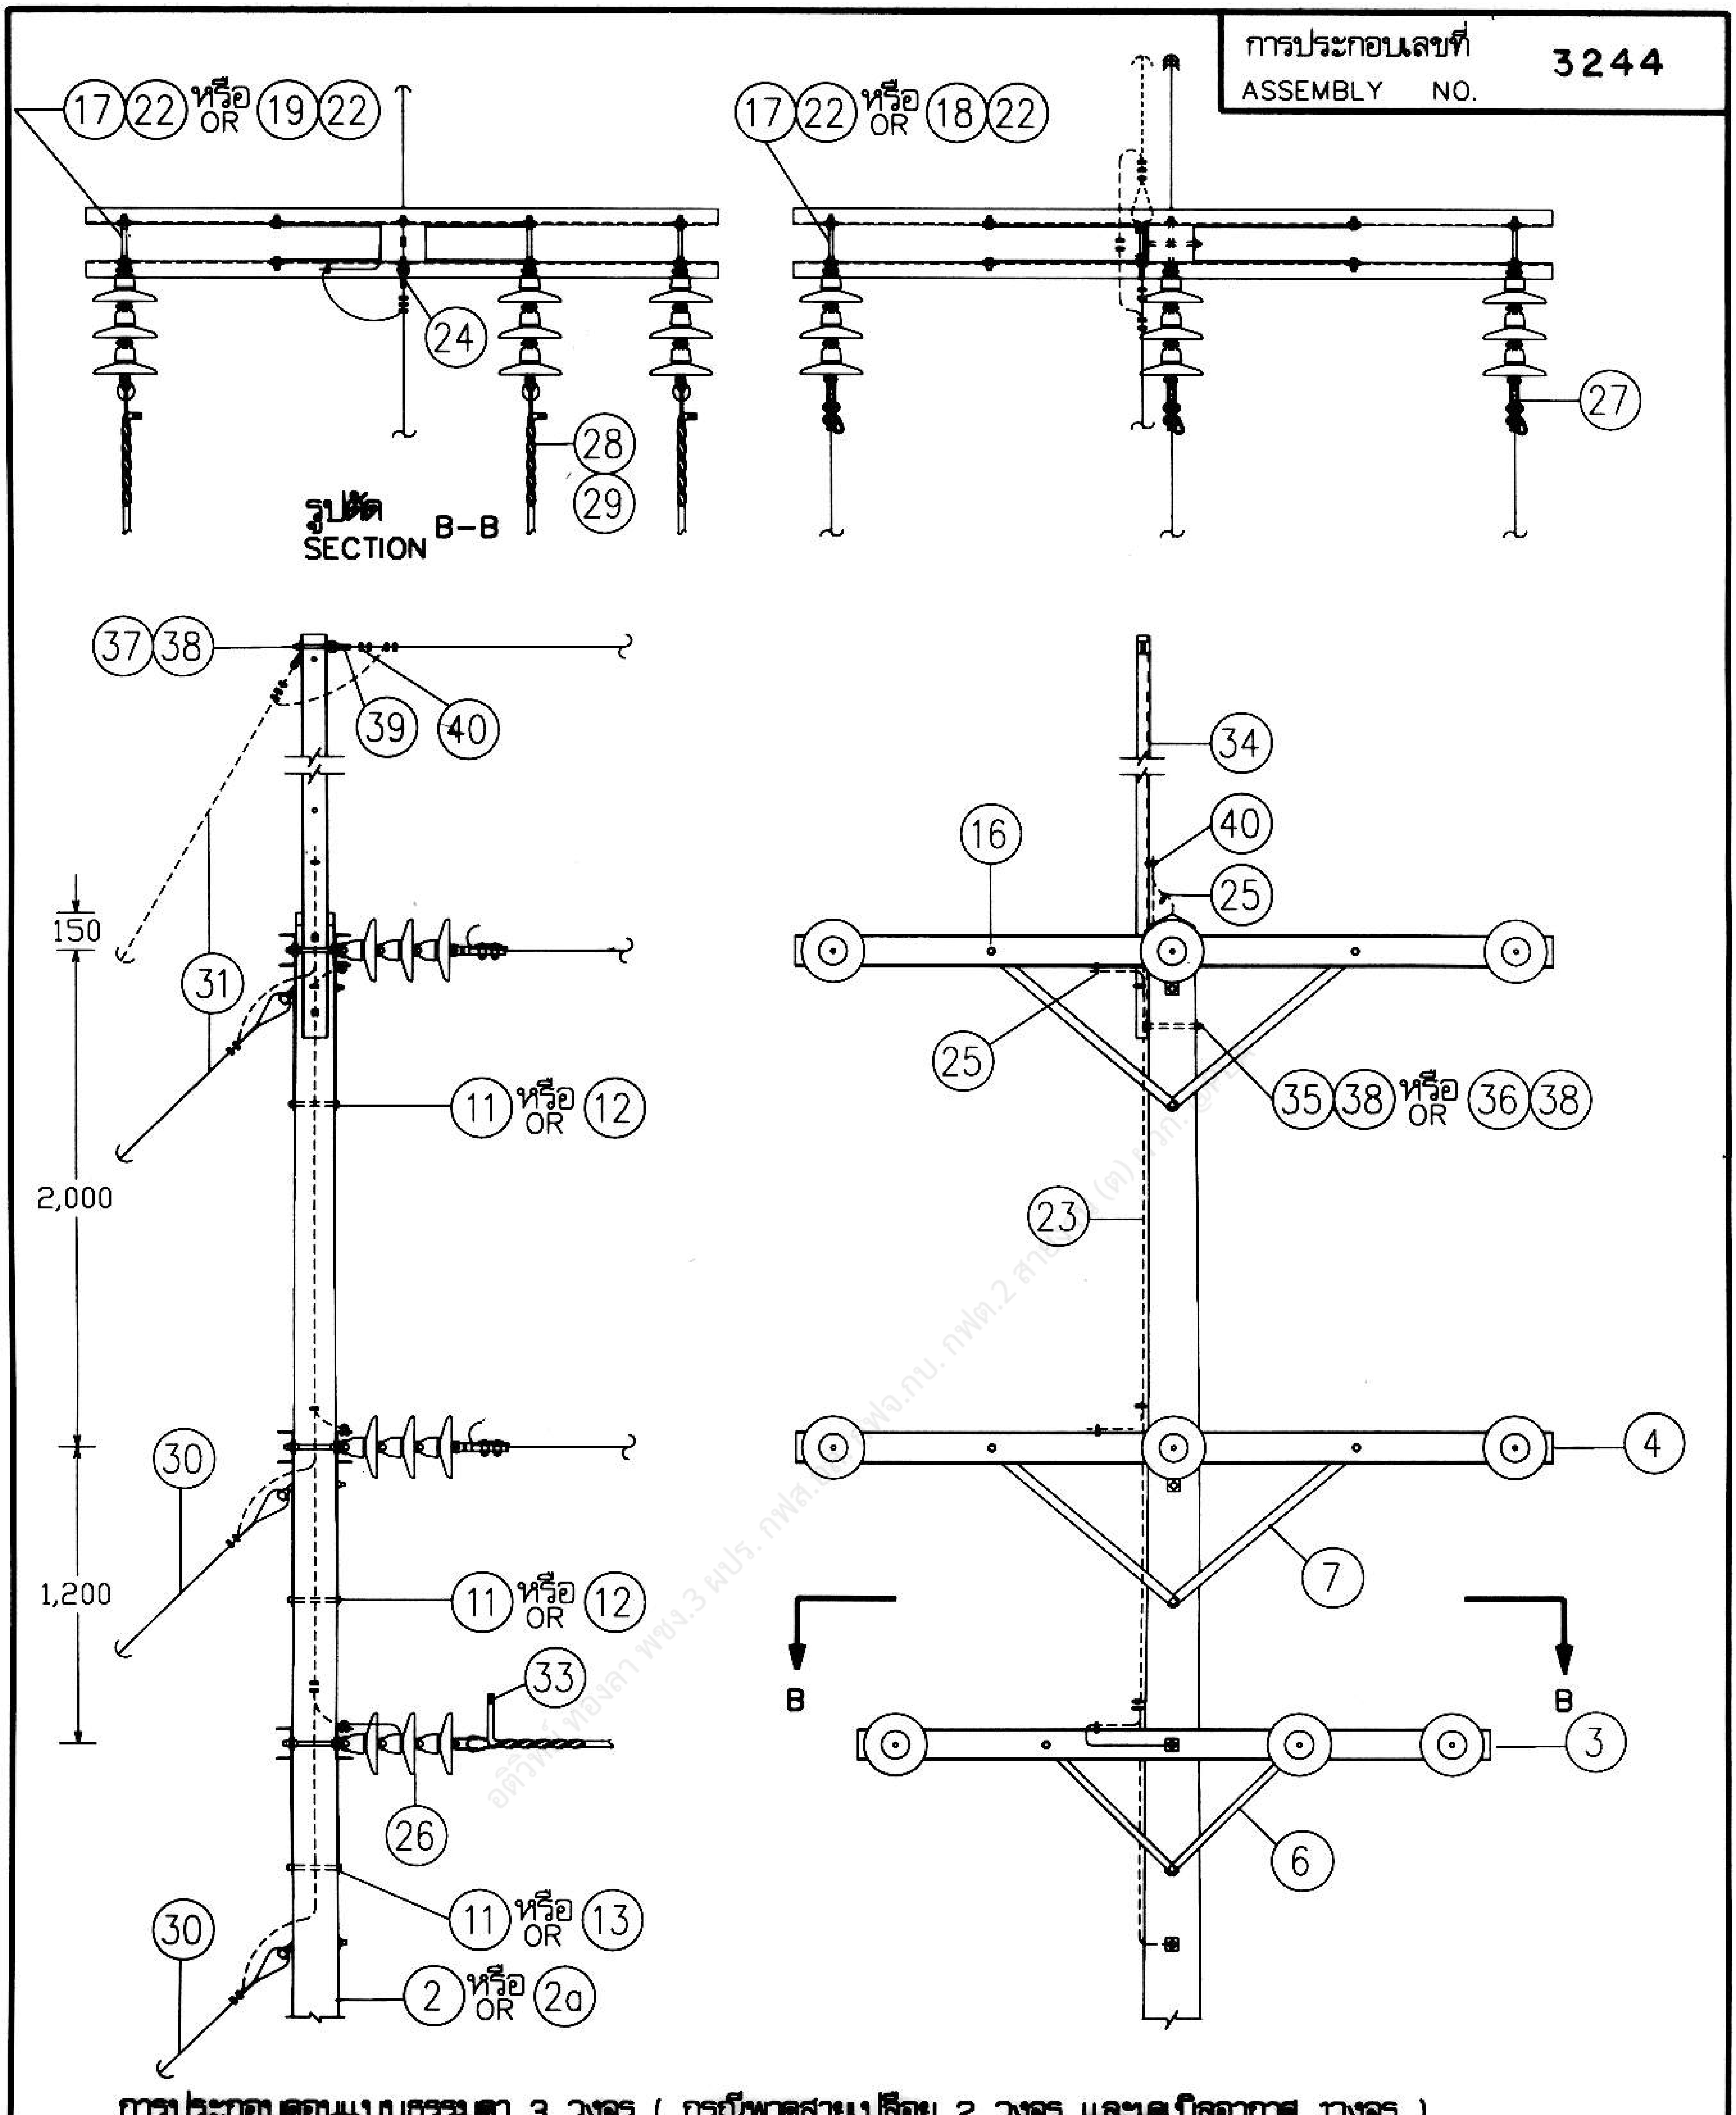

IV **การประกอบคอนแบบธรรมดา 3 วงจร ( กรณีพาดสายเปลือย 2 วงจร และเคเบิลอากาศ 1วงจร )**

3 CIRCUIT CROSSARM ASSEMBLY ( 2 CIRCUIT BARE CONDUCTOR AND 1 CIRCUIT AERIAL CABLE )

| | | |
|---|---|---|
| กองวิศวกรรมไฟฟ้าและเครื่องกล<br>ฝ่ายวิศวกรรม | การไฟฟ้าส่วนภูมิภาค | ใช้แทนแบบ ..............<br>ถูกแทนโดยแบบ .............. |
| ผู้เขียน B. Supphakit<br>ผู้สำรวจ ..............<br>วิศวกร ..............<br>หัวหน้าแผนก ..............<br>ผู้อำนวยการกอง ..............<br>ผู้อำนวยการฝ่าย .............. | ผู้ว่าการ ..............<br>22 เม.ย. 2540<br>**การประกอบคอนเหล็กรูปรางน้ำกับเสาคอนกรีต**<br>**33 kV**<br>**สำหรับเข้าปลายสาย** | เขียนเสร็จวันที่ 25 มี.ค. 2540<br>แก้แบบวันที่ ..............<br>มิติเป็น มิลลิเมตร<br>มาตราส่วน 1 : 40 |
| รองผู้ว่าการ<br>..............<br>22 เม.ย. 2540 | CHANNEL STEEL CROSSARM ASSEMBLY ON CONCRETE POLE<br>33 kV<br>**FOR DEADENDING** | แบบเลขที่ SA4-015/40006<br>แผ่นที่ 4 ของจำนวน 9 แผ่น |

การประกอบเลขที่
ASSEMBLY NO. **3244**

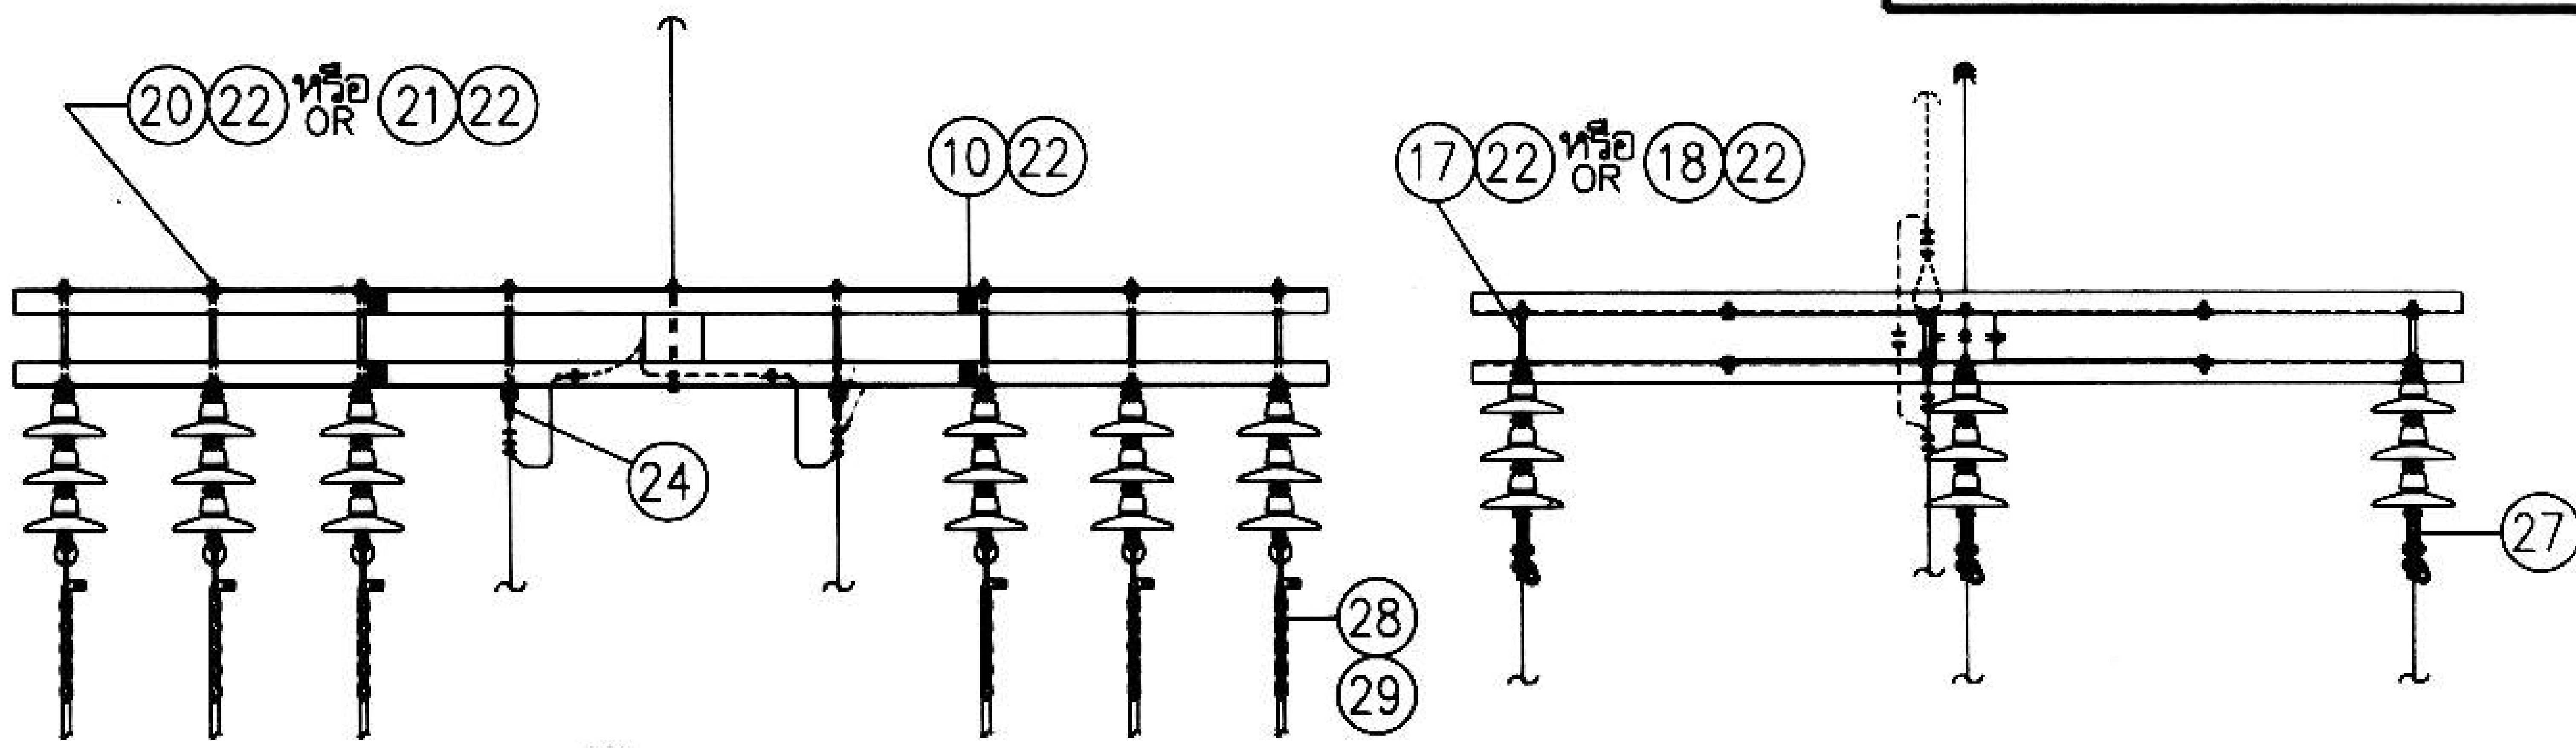

**รูปตัด**
SECTION C–C

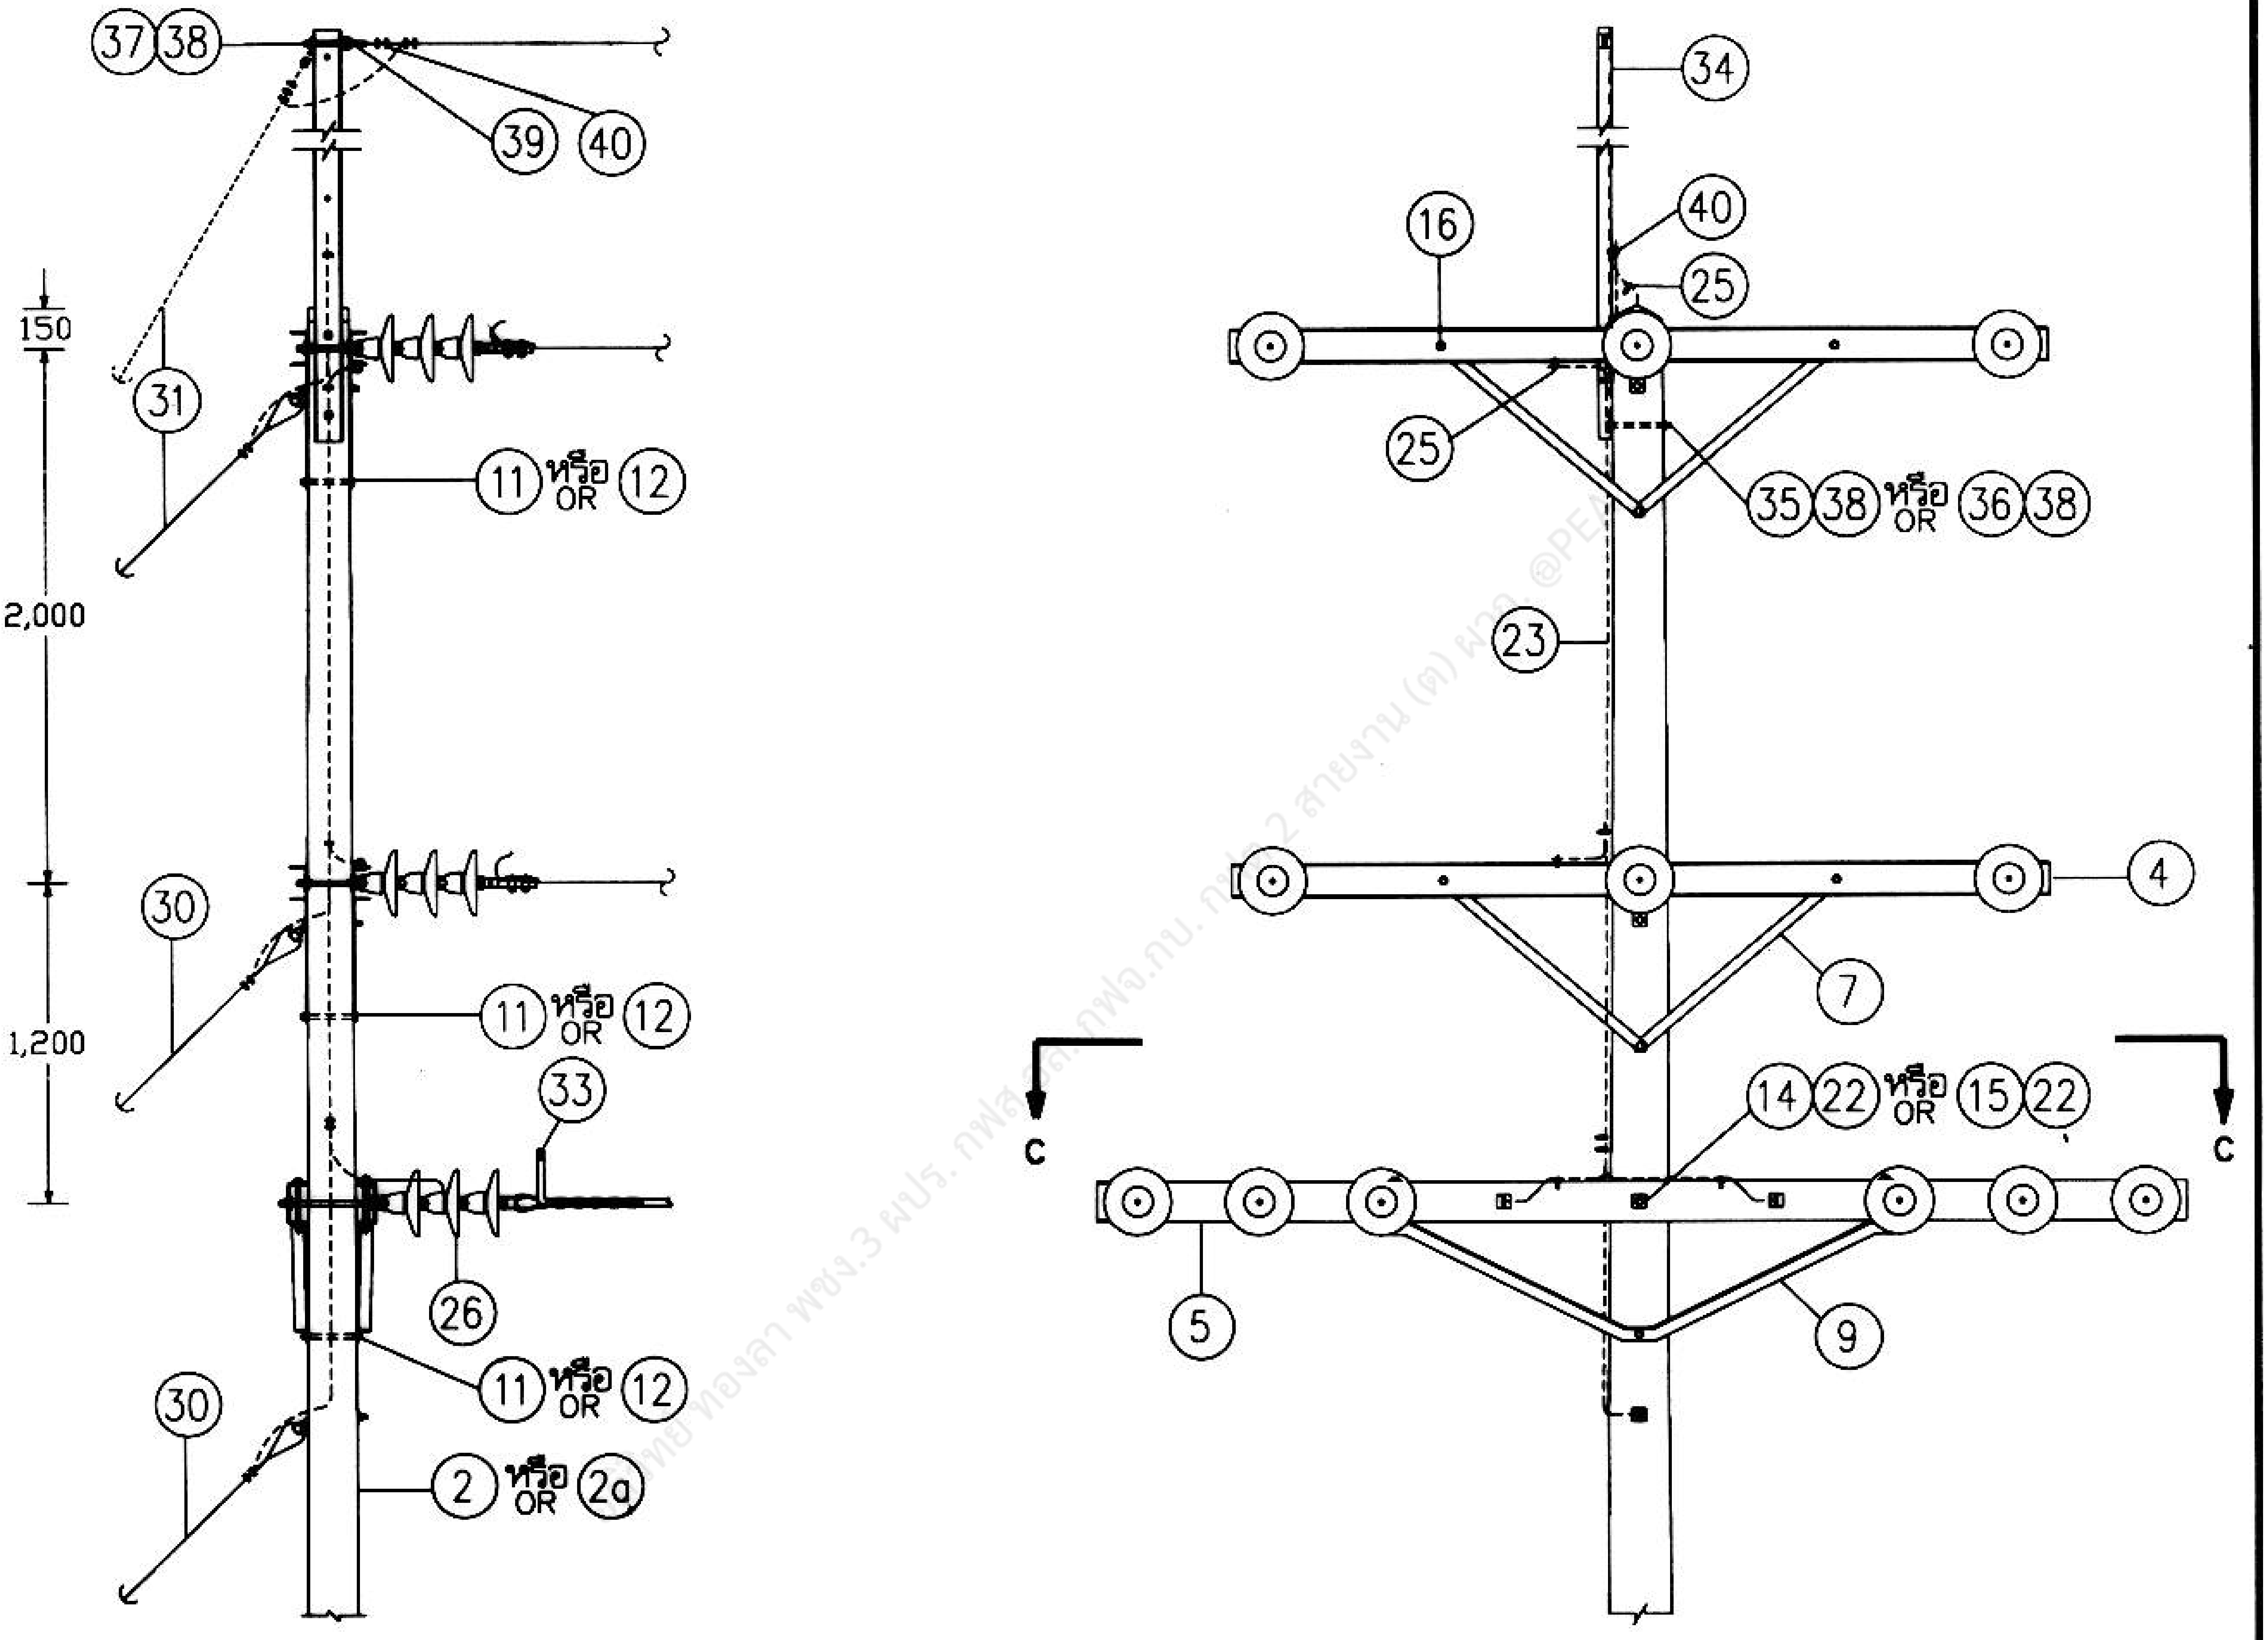

V

**การประกอบคอนแบบธรรมดา 4 วงจร ( กรณีพาดสายเปลือย 2 วงจร และเคเบิลอากาศ 2 วงจร )**

4 CIRCUIT CROSSARM ASSEMBLY ( 2 CIRCUIT BARE CONDUCTOR AND 2 CIRCUIT AERIAL CABLE STRINGING)

| | | |
|---|---|---|
| กองวิศวกรรมไฟฟ้าและเครื่องกล<br>ฝ่ายวิศวกรรม | การไฟฟ้าส่วนภูมิภาค | ใช้แทนแบบ ..............<br>ถูกแทนโดยแบบ .............. |
| ผู้เขียน B. Supphakit<br>ผู้สำรวจ ..............<br>วิศวกร ..............<br>หัวหน้าแผนก ..............<br>ผู้อำนวยการกอง ..............<br>ผู้อำนวยการฝ่าย .............. | ผู้ว่าการ ..............<br>22 เม.ย. 2540<br>การประกอบคอนเหล็กรูปรางน้ำกับเสาคอนกรีต<br>33 kV<br>สำหรับเข้าปลายสาย | เขียนเสร็จวันที่ 25 มี.ค. 2540<br>แก้แบบวันที่ ..............<br>มิติเป็น มิลลิเมตร<br>มาตราส่วน 1 : 50 |
| รองผู้ว่าการ<br>..............<br>22 เม.ย. 2540 | CHANNEL STEEL CROSSARM ASSEMBLY ON CONCRETE POLE<br>33 kV<br>FOR DEADENDING | แบบเลขที่ SA4–015/40006<br>แผ่นที่ 5 ของจำนวน 9 แผ่น |

การประกอบเลขที่ ASSEMBLY NO. **3244**

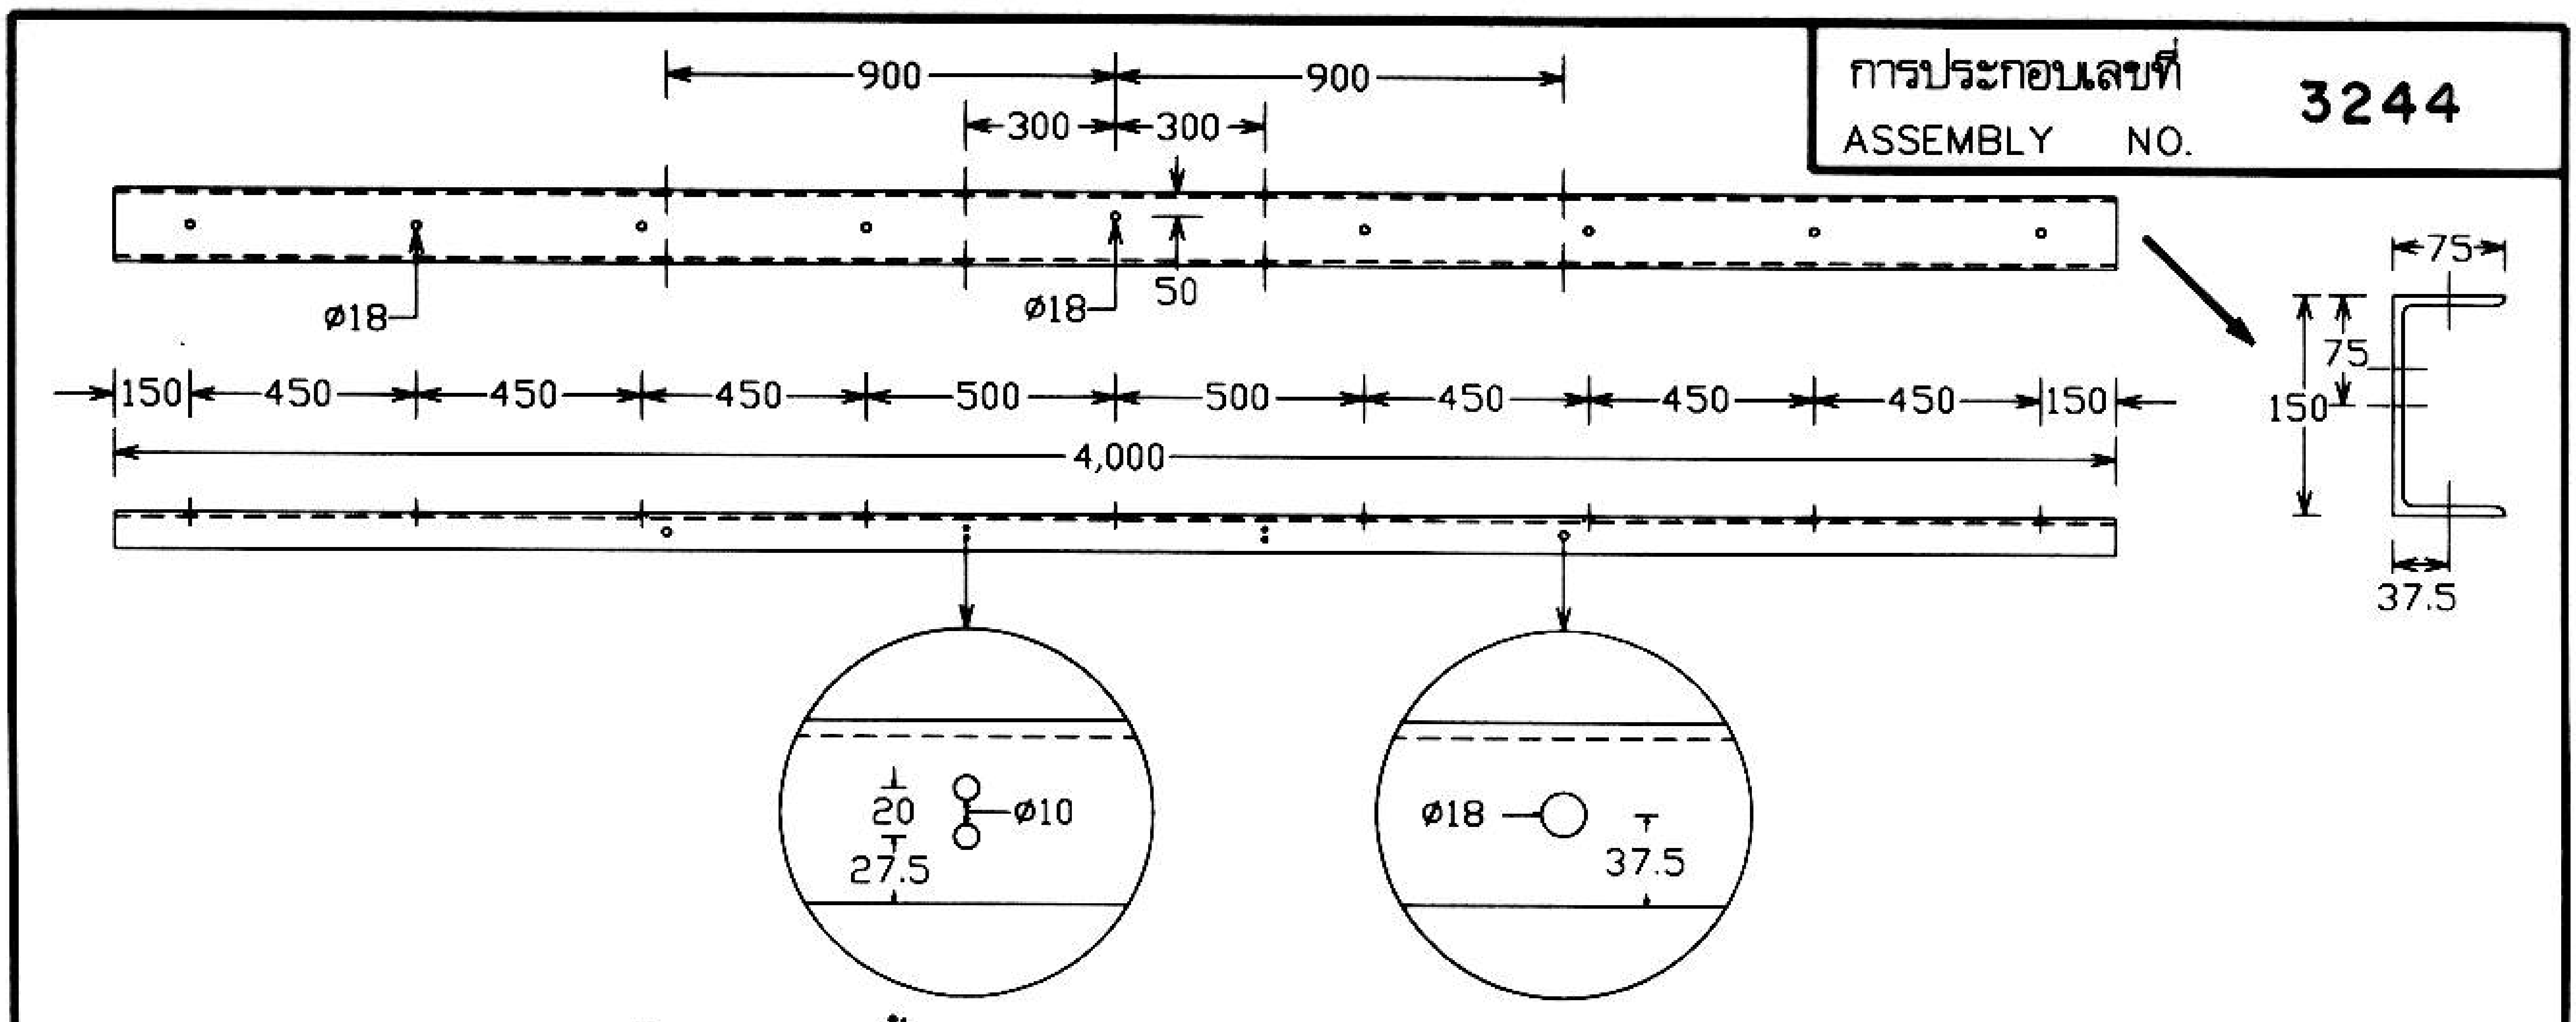

⑤ **เหล็กรูปรางน้ำ ขนาด 150 X 75 X 6.5 มม. ยาว 4 ม. มอก. 1227**
**CHANNEL STEEL, 150 X 75 X 6.5 mm, 4 m LONG, TIS 1227**

## บัญชีวัสดุ
## BILL OF MATERIAL

| ลำดับที่ ITEM | รายละเอียด DESCRIPTION | จำนวน REQ'D | | | | | | | | วัสดุเลขที่ MAT. NO. |
|---|---|---|---|---|---|---|---|---|---|---|
| | | I | II | III | III* | IV | IV* | V | V* | |
| 1 | เสาคอนกรีต 12 เมตร<br>POLE, CONCRETE, 12 m LONG | 1 | 1 | 1 | – | – | – | – | – | 00010004 |
| 1a | เสาคอนกรีต 12.20 เมตร<br>POLE, CONCRETE, 12.20 m LONG | – | – | – | 1 | – | – | – | – | 00010012 |
| 2 | เสาคอนกรีต 14 เมตร<br>POLE, CONCRETE, 14 m LONG | – | – | – | – | 1 | – | 1 | – | 00010006 |
| 2a | เสาคอนกรีต 14.30 เมตร<br>POLE, CONCRETE, 14.30 m LONG | – | – | – | – | – | 1 | – | 1 | 00010013 |
| 3 | คอนเหล็กรูปรางน้ำ ขนาด 125 X 65 X 6 มม. ยาว 2,500 มม.<br>CROSSARM, CHANNEL STEEL, 125 X 65 X 6 mm, 2,500 mm LONG | – | – | 2 | 2 | 2 | 2 | – | – | 01000202 |
| 4 | คอนเหล็กรูปรางน้ำ ขนาด 125 X 65 X 6 มม. ยาว 3,000 มม.<br>CROSSARM, CHANNEL STEEL, 125 X 65 X 6 mm, 3,000 mm LONG | 2 | 2 | 2 | 2 | 4 | 4 | 4 | 4 | 01000106 |
| 5 | เหล็กรูปรางน้ำ ขนาด 150 X 75 X 6.5 มม. ยาว 4 ม. มอก. 1227 เจาะรูตามแบบแผ่นที่ 6<br>CHANNEL STEEL, 150 X 75 X 6.5 mm, 4 m LONG, TIS 1227; PUNCH HOLE AS DWG. ON SHEET NO. 6 | – | – | – | – | – | – | 2 | 2 | – |
| 6 | เหล็กประกับคอน ขนาด 40 X 6 X 760 มม.<br>BRACE, FLAT, FOR CROSSARM, 40 X 6 X 760 mm | – | – | 4 | 4 | 4 | 4 | – | – | 01200001 |
| 7 | เหล็กประกับคอน ขนาด 30 X 6 X 1,000 มม.<br>BRACE, FLAT, FOR CROSSARM, 30 X 6 X 1,000 mm | 4 | – | 4 | 4 | 8 | 8 | 8 | 8 | 01200002 |
| 8 | เหล็กประกับคอนแบบท้าวแขน 50X50X6 มม. ยาว 2,350 มม.<br>BRACE, ALLEY ARM, 50 X 50 X 6 mm, 2,350 mm LONG | – | 1 | – | – | – | – | – | – | 01200005 |
| 9 | เหล็กฉากรับคอนสาย ขนาด 50 X 50 X 6 มม. ช่วงกว้าง 1,800 มม. ดรอพ 450 มม.<br>BRACE, ANGLE STEEL, 50 X 50 X 6 mm, 1,800 mm WIDE, 450 mm DROP | – | – | – | – | – | – | 2 | 2 | 01200007 |

กองวิศวกรรมไฟฟ้าและเครื่องกล
ฝ่ายวิศวกรรม

# การไฟฟ้าส่วนภูมิภาค

ใช้แทนแบบ ..............
ถูกแทนโดยแบบ ..............
เขียนเสร็จวันที่ 25. มี.ค. 2540
แก้แบบวันที่ ..............
มิติเป็น ..มิลลิเมตร..........
มาตราส่วน ..1 : 30..........

ผู้เขียน B. Suppalait
ผู้สำรวจ ..............
วิศวกร ..............
หัวหน้าแผนก ..............
ผู้อำนวยการกอง ..............
ผู้อำนวยการฝ่าย ..............

ผู้ว่าการ ..............
22 เม.ย. 2540

**การประกอบคอนเหล็กรูปรางน้ำกับเสาคอนกรีต**
**33 kV**
**สำหรับเข้าปลายสาย**

CHANNEL STEEL CROSSARM ASSEMBLY ON CONCRETE POLE
33 kV
**FOR DEADENDING**

รองผู้ว่าการ
22 เม.ย. 2540

แบบเลขที่ SA4-015/40006
แผ่นที่ 6 ของจำนวน 9 แผ่น

| | |
|---|---|
| การประกอบเลขที่<br>ASSEMBLY NO. | 3244 |

## บัญชีวัสดุ
## BILL OF MATERIAL

| ลำดับที่<br>ITEM | รายละเอียด<br>DESCRIPTION | จำนวน REQ'D | | | | | | | | วัสดุเลขที่<br>MAT. NO. |
|---|---|---|---|---|---|---|---|---|---|---|
| | | I | II | III | III* | IV | IV* | V | V* | |
| 10 | สลักเกลียว M16 X 200 มม.<br>BOLT, MACHINE, M16 X 200 mm | – | – | – | – | – | – | 4 | 4 | 01110202 |
| 11 | สลักเกลียว M16 X 250 มม.<br>BOLT, MACHINE, M16 X 250 mm | 1 | 2 | 2 | 1 | 3 | – | 3 | – | 01110203 |
| 12 | สลักเกลียว M16 X 300 มม.<br>BOLT, MACHINE, M16 X 300 mm | – | – | – | 1 | – | 2 | – | 3 | 01110204 |
| 13 | สลักเกลียว M16 X 350 มม.<br>BOLT, MACHINE, M16 X 350 mm | – | – | – | – | – | 1 | – | – | 01110205 |
| 14 | สลักเกลียว M16 X 400 มม.<br>BOLT, MACHINE, M16 X 400 mm | – | – | – | – | – | – | 1 | – | 01110206 |
| 15 | สลักเกลียว M16 X 450 มม.<br>BOLT, MACHINE, M16 X 450 mm | – | – | – | – | – | – | – | 1 | 01110207 |
| 16 | สลักเกลียว M16 X 50 มม. พร้อมแหวนกลม 2 อัน<br>BOLT,MACHINE,M16X50 mm, COMP. WITH 2 ROUND WASHERS | 4 | – | 6 | 6 | 10 | 10 | 8 | 8 | 01110404 |
| 17 | สลักห่วงโอแวล M16 X 250 มม.<br>BOLT, DOUBLE ARMING, OVAL EYE, M16 X 250 mm | 3 | 3 | 7 | 7 | 10 | – | 6 | – | – |
| 18 | สลักห่วงโอแวล M16 X 300 มม.<br>BOLT, DOUBLE ARMING, OVAL EYE, M16 X 300 mm | – | – | – | – | – | 6 | – | 6 | – |
| 19 | สลักห่วงโอแวล M16 X 350 มม.<br>BOLT, DOUBLE ARMING, OVAL EYE, M16 X 350 mm | – | – | – | – | – | 4 | – | – | – |
| 20 | สลักห่วงกลม M16 X 400 มม.<br>BOLT, DOUBLE ARMING, ROUND EYE, M16 X 400 mm | – | – | – | – | – | – | 8 | – | 01130000 |
| 21 | สลักห่วงกลม M16 X 450 มม.<br>BOLT, DOUBLE ARMING, ROUND EYE, M16 X 450 mm | – | – | – | – | – | – | – | 8 | 01130001 |
| 22 | แหวนสี่เหลี่ยมแบน 52X52X4.5 มม. รู ø18 มม. มอก. 258<br>WASHER,SQUARE,FLAT,52X52X4.5 mm,HOLE ø18 mm,TIS 258 | 10 | 14 | 22 | 22 | 32 | 32 | 58 | 58 | 01230000 |
| 23 | ลวดเหล็กตีเกลียว 25 ต.มม. มอก. 404<br>WIRE, STEEL STRANDED, 25 sq.mm, TIS 404 | ม<br>0.7<br>m | ม<br>0.7<br>m | ม<br>2.5<br>m | ม<br>2.5<br>m | ม<br>5<br>m | ม<br>5<br>m | ม<br>5.5<br>m | ม<br>5.5<br>m | 02200000 |
| 24 | กายทิมเบิล สำหรับสายยึดโยง 50-95 ต.มม.<br>THIMBLE, GUY, FOR 50–95 sq.mm. STEEL WIRE | – | – | 1 | 1 | 1 | 1 | 2 | 2 | 01210304 |
| 25 | ยูแคล้มป์ สลัก 1 ตัว M8<br>CLAMP, SINGLE U-BOLT, M8 | 2 | 2 | 7 | 7 | 9 | 9 | 14 | 14 | 01230000 |
| 26 | ลูกถ้วยแขวน แบบ ง (แบบ 52-4) มอก.354<br>INSULATOR, SUSPENSION, TIS 354, TYPE D(CLASS 52–4) | 9 | 9 | 18 | 18 | 27 | 27 | 36 | 36 | 03020002 |
| 27 | สเตรนแคล้มป์ สำหรับสายอะลูมิเนียม หรือ ทิมเบิลเคลวิสพร้อมปรีฟอร์มเข้าปลายสาย PIC ขนาดตามต้องการ<br>CLAMP, STRAIN, FOR AI CONDUCTOR; OR CLEVIS, THIMBLE, WITH PIC PREFORMED DEADEND: SIZE AS REQUIRED | 3 | 3 | 3 | 3 | 6 | 6 | 6 | 6 | 03110000–<br>03110101<br>or<br>03140011<br>&<br>02250101–<br>02250221 |
| 28 | ทิมเบิลเคลวิส สำหรับปรีฟอร์มเข้าปลายสาย<br>CLEVIS, THIMBLE, FOR PREFORMED DEADEND | – | – | 3 | 3 | 3 | 3 | 6 | 6 | 03140011 |

กองวิศวกรรมไฟฟ้าและเครื่องกล
ฝ่ายวิศวกรรม

# การไฟฟ้าส่วนภูมิภาค

ผู้เขียน ..........
ผู้สำรวจ ..........
วิศวกร ..........
หัวหน้าแผนก ..........
ผู้อำนวยการกอง ..........
ผู้อำนวยการฝ่าย ..........

ผู้ว่าการ ..........

22 เม.ย. 2540

รองผู้ว่าการ
..........

22 เม.ย. 2540

### การประกอบคอนเหล็กรูปรางน้ำกับเสาคอนกรีต
### 33 kV
### สำหรับเข้าปลายสาย

### CHANNEL STEEL CROSSARM ASSEMBLY ON CONCRETE POLE
### 33 kV
### FOR DEADENDING

ใช้แทนแบบ ..........
ถูกแทนโดยแบบ ..........
เขียนเสร็จวันที่ 25. มีค. 2540
แก้แบบวันที่ ..........
มิติเป็น .. - ..........
มาตราส่วน .. - ..........
แบบเลขที่ SA4-015/40006
แผ่นที่ 7 ของจำนวน 9 แผ่น

การประกอบเลขที่ 3244
ASSEMBLY NO.

## บัญชีวัสดุ
## BILL OF MATERIAL

| ลำดับที่<br>ITEM | รายละเอียด<br>DESCRIPTION | จำนวน REQ'D<br>I | II | III | III* | IV | IV* | V | V* | วัสดุเลขที่<br>MAT. NO. |
|---|---|---|---|---|---|---|---|---|---|---|
| 29 | ปรีฟอร์มเข้าปลายสาย สำหรับเคเบิลอากาศอะลูมิเนียม 33 kV ขนาดตามต้องการ<br>PREFORMED DEADEND, FOR 33 kV Al AERIAL CABLE; SIZE AS REQ'D | – | – | 3 | 3 | 3 | 3 | 6 | 6 | 02250221–<br>02260201 |
| 30 | สายยึดโยงแบบ GY-32<br>GUY ASSEMBLY, GY-32 | – | – | 1 | 1 | 2 | 2 | 2 | 2 | – |
| 31 | สายยึดโยงแบบ GY-33<br>GUY ASSEMBLY, GY-33 | 1 | – | 1 | 1 | 1 | 1 | 1 | 1 | – |
| 32 | สายยึดโยงแบบ GY-01, GY-38 และ GY-39<br>GUY ASSEMBLY, GY-01,GY-38 AND GY-39 | – | 1 | – | – | – | – | – | – | – |
| 33 | เทปพันเคเบิลอากาศแรงสูง ขนาด 3/4"X 30' สำหรับสาย PIC และเคเบิลอากาศแรงสูง<br>ELECTRICAL SPLICING TAPE, FOR HT. AERIAL CABLE SIZE 3/4"X 30'; FOR PIC AND HT. AERIAL CABLE | – | – | ม้วน<br>rolls | ม้วน<br>rolls | ม้วน<br>rolls | ม้วน<br>rolls | ม้วน<br>rolls | ม้วน<br>rolls | 02180003 |
|  |  |  |  |  |  |  |  |  |  |  |
|  |  |  |  |  |  |  |  |  |  |  |
|  |  |  |  |  |  |  |  |  |  |  |
|  |  |  |  |  |  |  |  |  |  |  |

## บัญชีวัสดุสำหรับติดตั้งสายล่อฟ้า
## BILL OF MATERIAL, FOR OHGW INSTALLATION

| ลำดับที่<br>ITEM | รายละเอียด<br>DESCRIPTION | I | II | III | III* | IV | IV* | V | V* | วัสดุเลขที่<br>MAT. NO. |
|---|---|---|---|---|---|---|---|---|---|---|
| 34 | เหล็กรูปรางน้ำรับสายล่อฟ้า ขนาด 100 X 50 X 5 มม. ยาว 2.25 ม.<br>STEEL,CHANNEL,OHGW BAYONET, 100 X 50 X 5 mm, 2.25 m LONG | 1 | 1 | 1 | 1 | 1 | 1 | 1 | 1 | 01000100 |
| 35 | สลักเกลียว M16 X 250 มม.<br>BOLT, MACHINE, M16 X 250 mm | 2 | 2 | 2 | 2 | 2 | – | 2 | – | 01110203 |
| 36 | สลักเกลียว M16 X 300 มม.<br>BOLT, MACHINE, M16 X 300 mm | – | – | – | – | – | 2 | – | 2 | 01110204 |
| 37 | สลักห่วงกลม M16 X 200มม.<br>BOLT, ROUND EYE, M16 X 200 mm | 1 | 1 | 1 | 1 | 1 | 1 | 1 | 1 | 01140001 |
| 38 | แหวนสี่เหลี่ยมแบน 52X52X4.5มม. รู ø18มม. มอก. 258<br>WASHER,SQUARE,FLAT,52X52X4.5 mm,HOLE ø18 mm,TIS 258 | 3 | 3 | 3 | 3 | 3 | 3 | 3 | 3 | 01230000 |
| 39 | กายทิมเบิ้ล สำหรับสายยึดโยง 50-95 ต.มม.<br>THIMBLE, GUY, FOR 50-95 sq.mm. STEEL WIRE | 1 | 1 | 1 | 1 | 1 | 1 | 1 | 1 | 01210304 |
| 40 | ยูแคล้มป์ สลัก 1 ตัว M8<br>CLAMP, SINGLE U-BOLT, M8 | 3 | 3 | 3 | 3 | 3 | 3 | 3 | 3 | 01230000 |
|  |  |  |  |  |  |  |  |  |  |  |

กองวิศวกรรมไฟฟ้าและเครื่องกล
ฝ่ายวิศวกรรม

ผู้เขียน ........
ผู้สำรวจ ........
วิศวกร ........
หัวหน้าแผนก ........
ผู้อำนวยการกอง ........
ผู้อำนวยการฝ่าย ........

รองผู้ว่าการ
........
22 เม.ย. 2540

# การไฟฟ้าส่วนภูมิภาค

ผู้ว่าการ ........
22 เม.ย. 2540

**การประกอบคอนเหล็กรูปรางน้ำกับเสาคอนกรีต**
**33 kV**
**สำหรับเข้าปลายสาย**

**CHANNEL STEEL CROSSARM ASSEMBLY ON CONCRETE POLE**
**33 kV**
**FOR DEADENDING**

ใช้แทนแบบ ........
ถูกแทนโดยแบบ ........
เขียนเสร็จวันที่ 25. มี.ค. 2540
แก้แบบวันที่ ........
มิติเป็น ..-..
มาตราส่วน ..-..
แบบเลขที่ SA4-015/40006
แผ่นที่ 8 ของจำนวน 9 แผ่น

| การประกอบเลขที่<br>ASSEMBLY NO. | 3244 |
|---|---|

| ลำดับที่<br>ITEM | แบบอ้างอิง<br>REFERENCE DRAWING | แบบเลขที่<br>DWG. NO. | การประกอบเลขที่<br>ASSEMBLY NO. |
|---|---|---|---|
| 1 | โครงสร้างเสา สำหรับติดตั้งระบบจำหน่าย 1-3 วงจร, 33 kV<br>POLE STRUCTURE FOR 1-3 CIRCUIT INSTALLATION, 33 kV | SA1-015/22005 | 8242 |
| 2 | โครงสร้างเสาระบบจำหน่าย 33 kV, สำหรับพาดสายหุ้ม PIC<br>33 kV DISTRIBUTION POLE STRUCTURE, FOR PIC STRINGING | IB1-015/33083 | 8244 |
| 3 | โครงสร้างเสาระบบจำหน่าย 33 kV 2 วงจร, สำหรับพาดสายหุ้ม PIC<br>33 kV DISTRIBUTION POLE STRUCTURE, 2 CIRCUIT ,FOR PIC STRINGING | IB1-015/37026<br>IB1-015/37037<br>IB1-015/34091 | 8245<br>8246<br>8276 |
| 4 | โครงสร้างเสาระบบจำหน่าย 33 kV 3-4 วงจร<br>33 kV DISTRIBUTION POLE STRUCTURE, 3-4 CIRCUIT | IB1-015/37038<br>IB1-015/34071 | 8247<br>8282 |
| 5 | คอนเหล็กรูปรางน้ำ 125 X 65 X 6 มม. ยาว 2,500 มม.<br>CHANNEL STEEL CROSSARM, 125 X 65 X 6 mm, 2,500 mm LONG | SA4-015/40001 | 2115<br>3114 |
| 6 | คอนเหล็กรูปรางน้ำ 125 X 65 X 6 มม. ยาว 3,000 มม.<br>CHANNEL STEEL CROSSARM, 125 X 65 X 6 mm, 3,000 mm LONG | SA4-015/39019 | 3113 |
| 7 | หลักของการก่อสร้างระบบจำหน่าย 33 kV,( เฉพาะแบบเหนือดิน )<br>PRINCIPLES OF 33 kV DISTRIBUTION CONSTRUCTION( OVERHEAD LINE ONLY ) | SA4-015/37017 | 9505 |

## หมายเหตุ

บัญชีวัสดุ :-

- --สดมภ์ I สำหรับการประกอบแบบคอนธรรมดา 1 วงจร บนเสาคอนกรีต 12 ม. (สำหรับสายเปลือย)
- --สดมภ์ II สำหรับการประกอบคอนแบบท้าวแขน 1 วงจร บนเสาคอนกรีต 12 ม. (สำหรับสายเปลือย)
- --สดมภ์ III สำหรับการประกอบคอนแบบธรรมดา 2 วงจร บนเสาคอนกรีต 12 ม. ( สำหรับพาดสายเปลือย 1 วงจร และสายเคเบิลอากาศ 1 วงจร )
- --สดมภ์ III* สำหรับการประกอบคอนแบบธรรมดา 2 วงจร บนเสาคอนกรีต 12.20 ม. (สำหรับพาดสายเปลือย 1 วงจร และสายเคเบิลอากาศ 1 วงจร )
- --สดมภ์ IV สำหรับการประกอบคอนแบบธรรมดา 3 วงจร บนเสาคอนกรีต 14 ม. ( สำหรับพาดสายเปลือย 2 วงจร และสายเคเบิลอากาศ 1 วงจร )
- --สดมภ์ IV* สำหรับการประกอบคอนแบบธรรมดา 3 วงจร บนเสาคอนกรีต 14.30 ม. ( สำหรับพาดสายเปลือย 2 วงจร และสายเคเบิลอากาศ 1 วงจร )
- --สดมภ์ V สำหรับการประกอบคอนแบบธรรมดา 4 วงจร บนเสาคอนกรีต 14 ม. ( สำหรับพาดสายเปลือย 2 วงจร และสายเคเบิลอากาศ 2 วงจร )
- --สดมภ์ V* สำหรับการประกอบคอนแบบธรรมดา 4 วงจร บนเสาคอนกรีต 14.30 ม. ( สำหรับพาดสายเปลือย 2 วงจร และสายเคเบิลอากาศ 2 วงจร )

## NOTES

BILL OF MATERIAL:-

- -COLUMN I, FOR 1 CIRCUIT CROSSARM ASSEMBLY ON 12 m CONCRETE POLE (BARE CONDUCTOR ) .
- -COLUMN II, FOR 1 CIRCUIT ALLEY ARM ASSEMBLY ON 12 m CONCRETE POLE (BARE CONDUCTOR ) .
- -COLUMN III, FOR 2 CIRCUIT CROSSARM ASSEMBLY ON 12 m CONCRETE POLE (1 CIRCUIT BARE CONDUCTOR AND 1 CIRCUIT AERIAL CABLE) .
- -COLUMN III*, FOR 2 CIRCUIT CROSSARM ASSEMBLY ON 12.20 m CONCRETE POLE (1 CIRCUIT BARE CONDUCTOR AND 1 CIRCUIT AERIAL CABLE) .
- -COLUMN IV, FOR 3 CIRCUIT CROSSARM ASSEMBLY ON 14 m CONCRETE POLE (2 CIRCUIT BARE CONDUCTOR AND 1 CIRCUIT AERIAL CABLE) .
- -COLUMN IV*, FOR 3 CIRCUIT CROSSARM ASSEMBLY ON 14.30 m CONCRETE POLE (2 CIRCUIT BARE CONDUCTOR AND 1 CIRCUIT AERIAL CABLE) .
- -COLUMN V, FOR 4 CIRCUIT CROSSARM ASSEMBLY ON 14 m CONCRETE POLE (2 CIRCUIT BARE CONDUCTOR AND 2 CIRCUIT AERIAL CABLE) .
- -COLUMN V*, FOR 4 CIRCUIT CROSSARM ASSEMBLY ON 14.30 m CONCRETE POLE (2 CIRCUIT BARE CONDUCTOR AND 2 CIRCUIT AERIAL CABLE) .

| | | |
|---|---|---|
| กองวิศวกรรมไฟฟ้าและเครื่องกล<br>ฝ่ายวิศวกรรม | การไฟฟ้าส่วนภูมิภาค | ใช้แทนแบบ ..........<br>ถูกแทนโดยแบบ .......... |
| ผู้เขียน ..........<br>ผู้สำรวจ ..........<br>วิศวกร ..........<br>หัวหน้าแผนก ..........<br>ผู้อำนวยการกอง ..........<br>ผู้อำนวยการฝ่าย .......... | ผู้ว่าการ ..........<br>22 เม.ย. 2540<br>การประกอบคอนเหล็กรูปรางน้ำกับเสาคอนกรีต<br>33 kV<br>สำหรับเข้าปลายสาย | เขียนเสร็จวันที่ 25. มีค. 2540<br>แก้แบบวันที่ ..........<br>มิติเป็น -<br>มาตราส่วน - |
| รองผู้ว่าการ<br>..........<br>22 เม.ย. 2540 | CHANNEL STEEL CROSSARM ASSEMBLY ON CONCRETE POLE<br>33 kV<br>FOR DEADENDING | แบบเลขที่ SA4-015/40006<br>แผ่นที่ 9 ของจำนวน 9 แผ่น |