การประกอบเลขที่ ASSEMBLY NO. **0203**

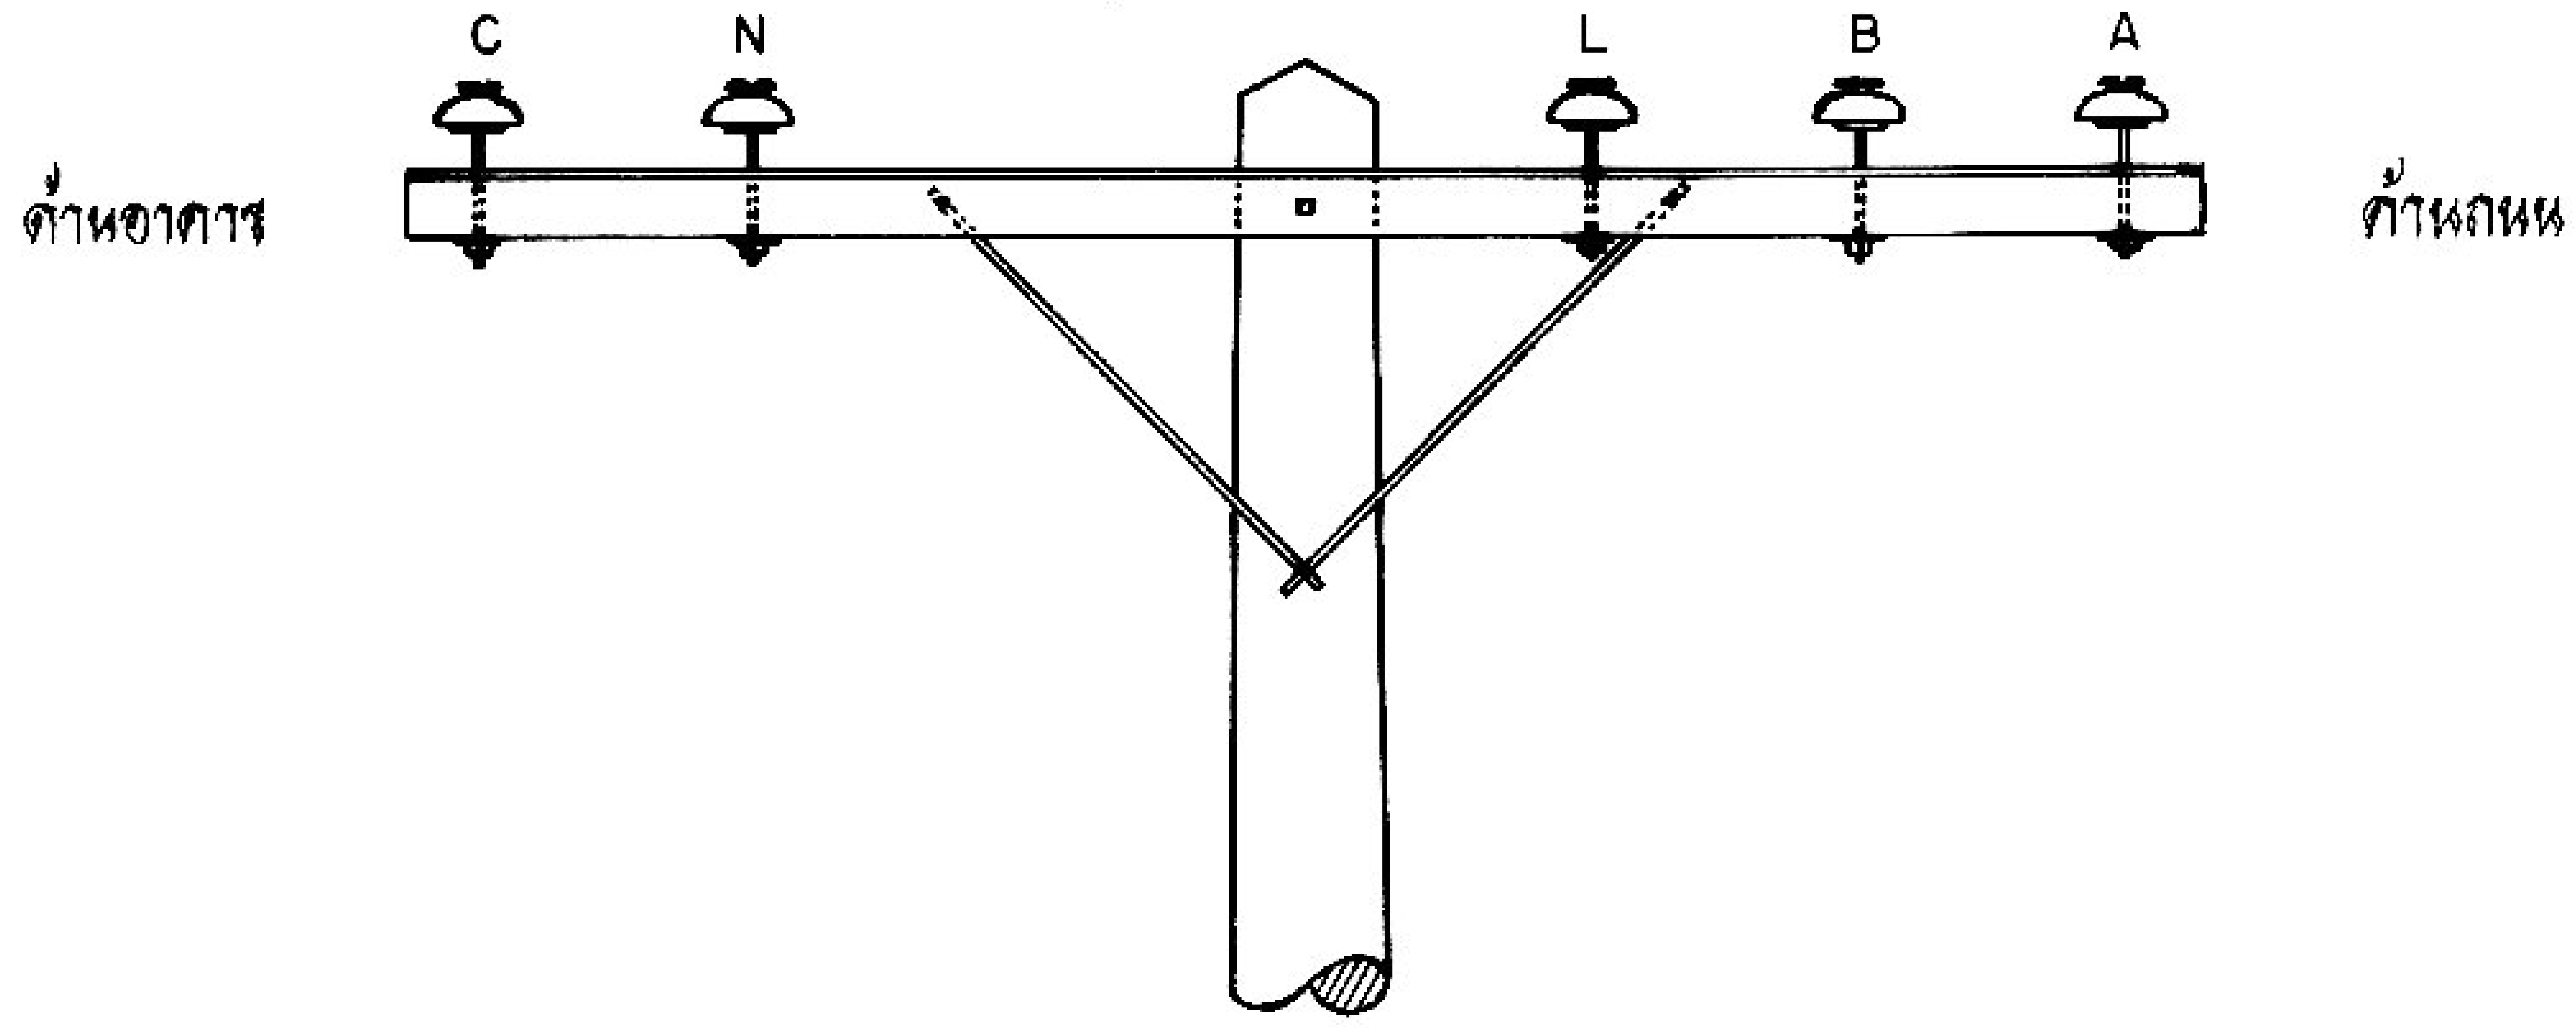

ตำแหน่งสายไฟแรงต่ำบนไม้คอน 2.50 เมตร
ระบบ 3 เฟส 4 สาย

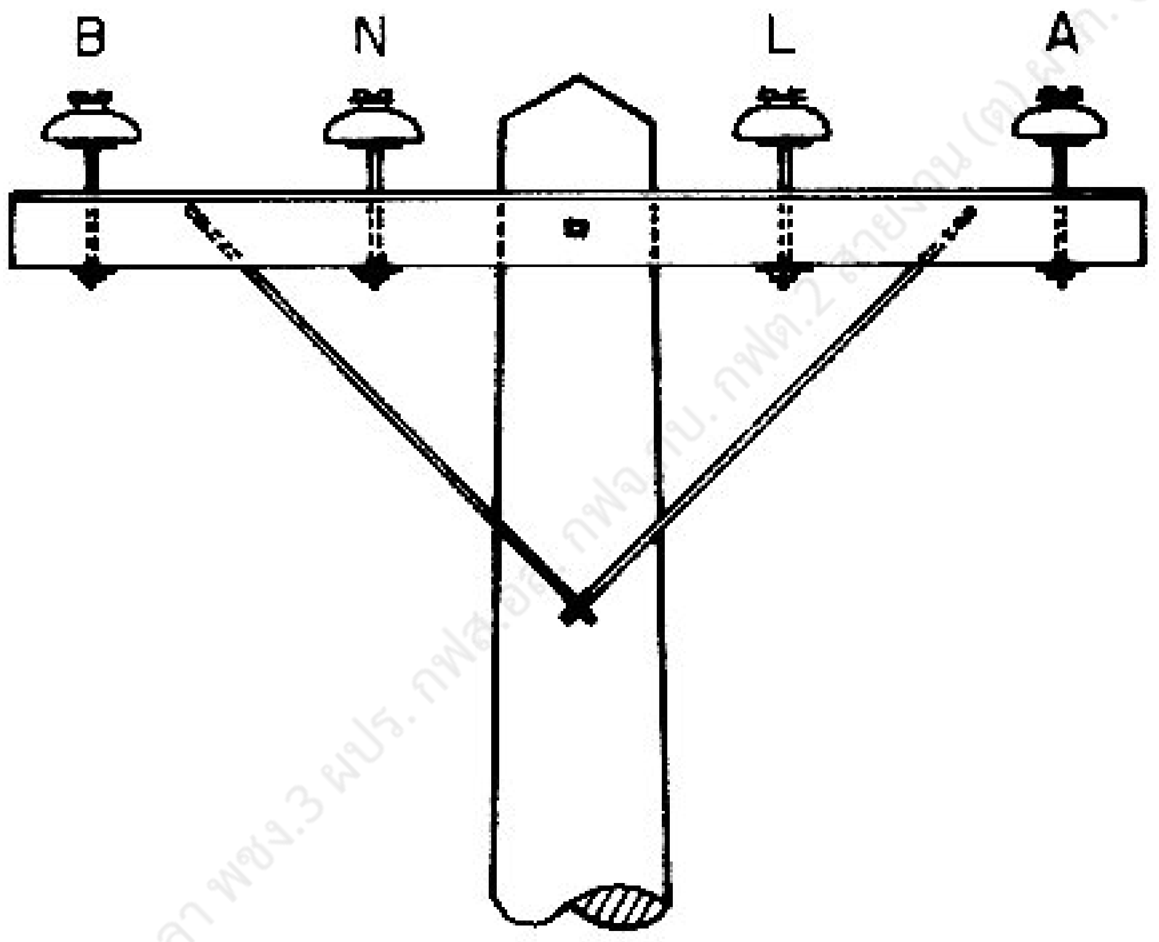

ตำแหน่งสายไฟแรงต่ำบนไม้คอน 1.50 เมตร
ระบบ 1 เฟส 3 สาย

อดิวิทย์ ทองลา พชง.3 ผปร. กฟส.[illegible] กฟจ.ธบ. กฟต.2 สายงาน (ต) [illegible] @PEA

หมายเหตุ :

A	สายเฟส
B	สายเฟส
C	สายเฟส
N	สายเป็นกลาง
L	สายไฟถนน

กองแผนการ

การไฟฟ้าส่วนภูมิภาค

ผู้เขียน ไพเราะ ทองมา
สถาปนิก
วิศวกร ประวิทย์ จิระเดชะ
หัวหน้าแผนก ประวาช (แทน)
ผู้อำนวยการกอง 2543
รองผู้ว่าการฝ่ายเทคนิค

ผู้ว่าการ

ตำแหน่งสายไฟสำหรับระบบจำหน่ายแรงต่ำ
บนไม้คอน

CIRCUIT POSITIONS FOR L.T. DISTRIBUTION
ON CROSSARM

ใช้แทนแบบ
ถูกแทนโดยแบบ
เขียนเสร็จวันที่ 31 ค.ค. 09
แก้แบบวันที่
พิมพ์เป็น ชม.
มาตราส่วน 1:25
แบบเลขที่ I50-015/090477
แผ่นที่ 1 ของจำนวน 1 แผ่น