
การประกอบเลขที่ ASSEMBLY NO. 0306

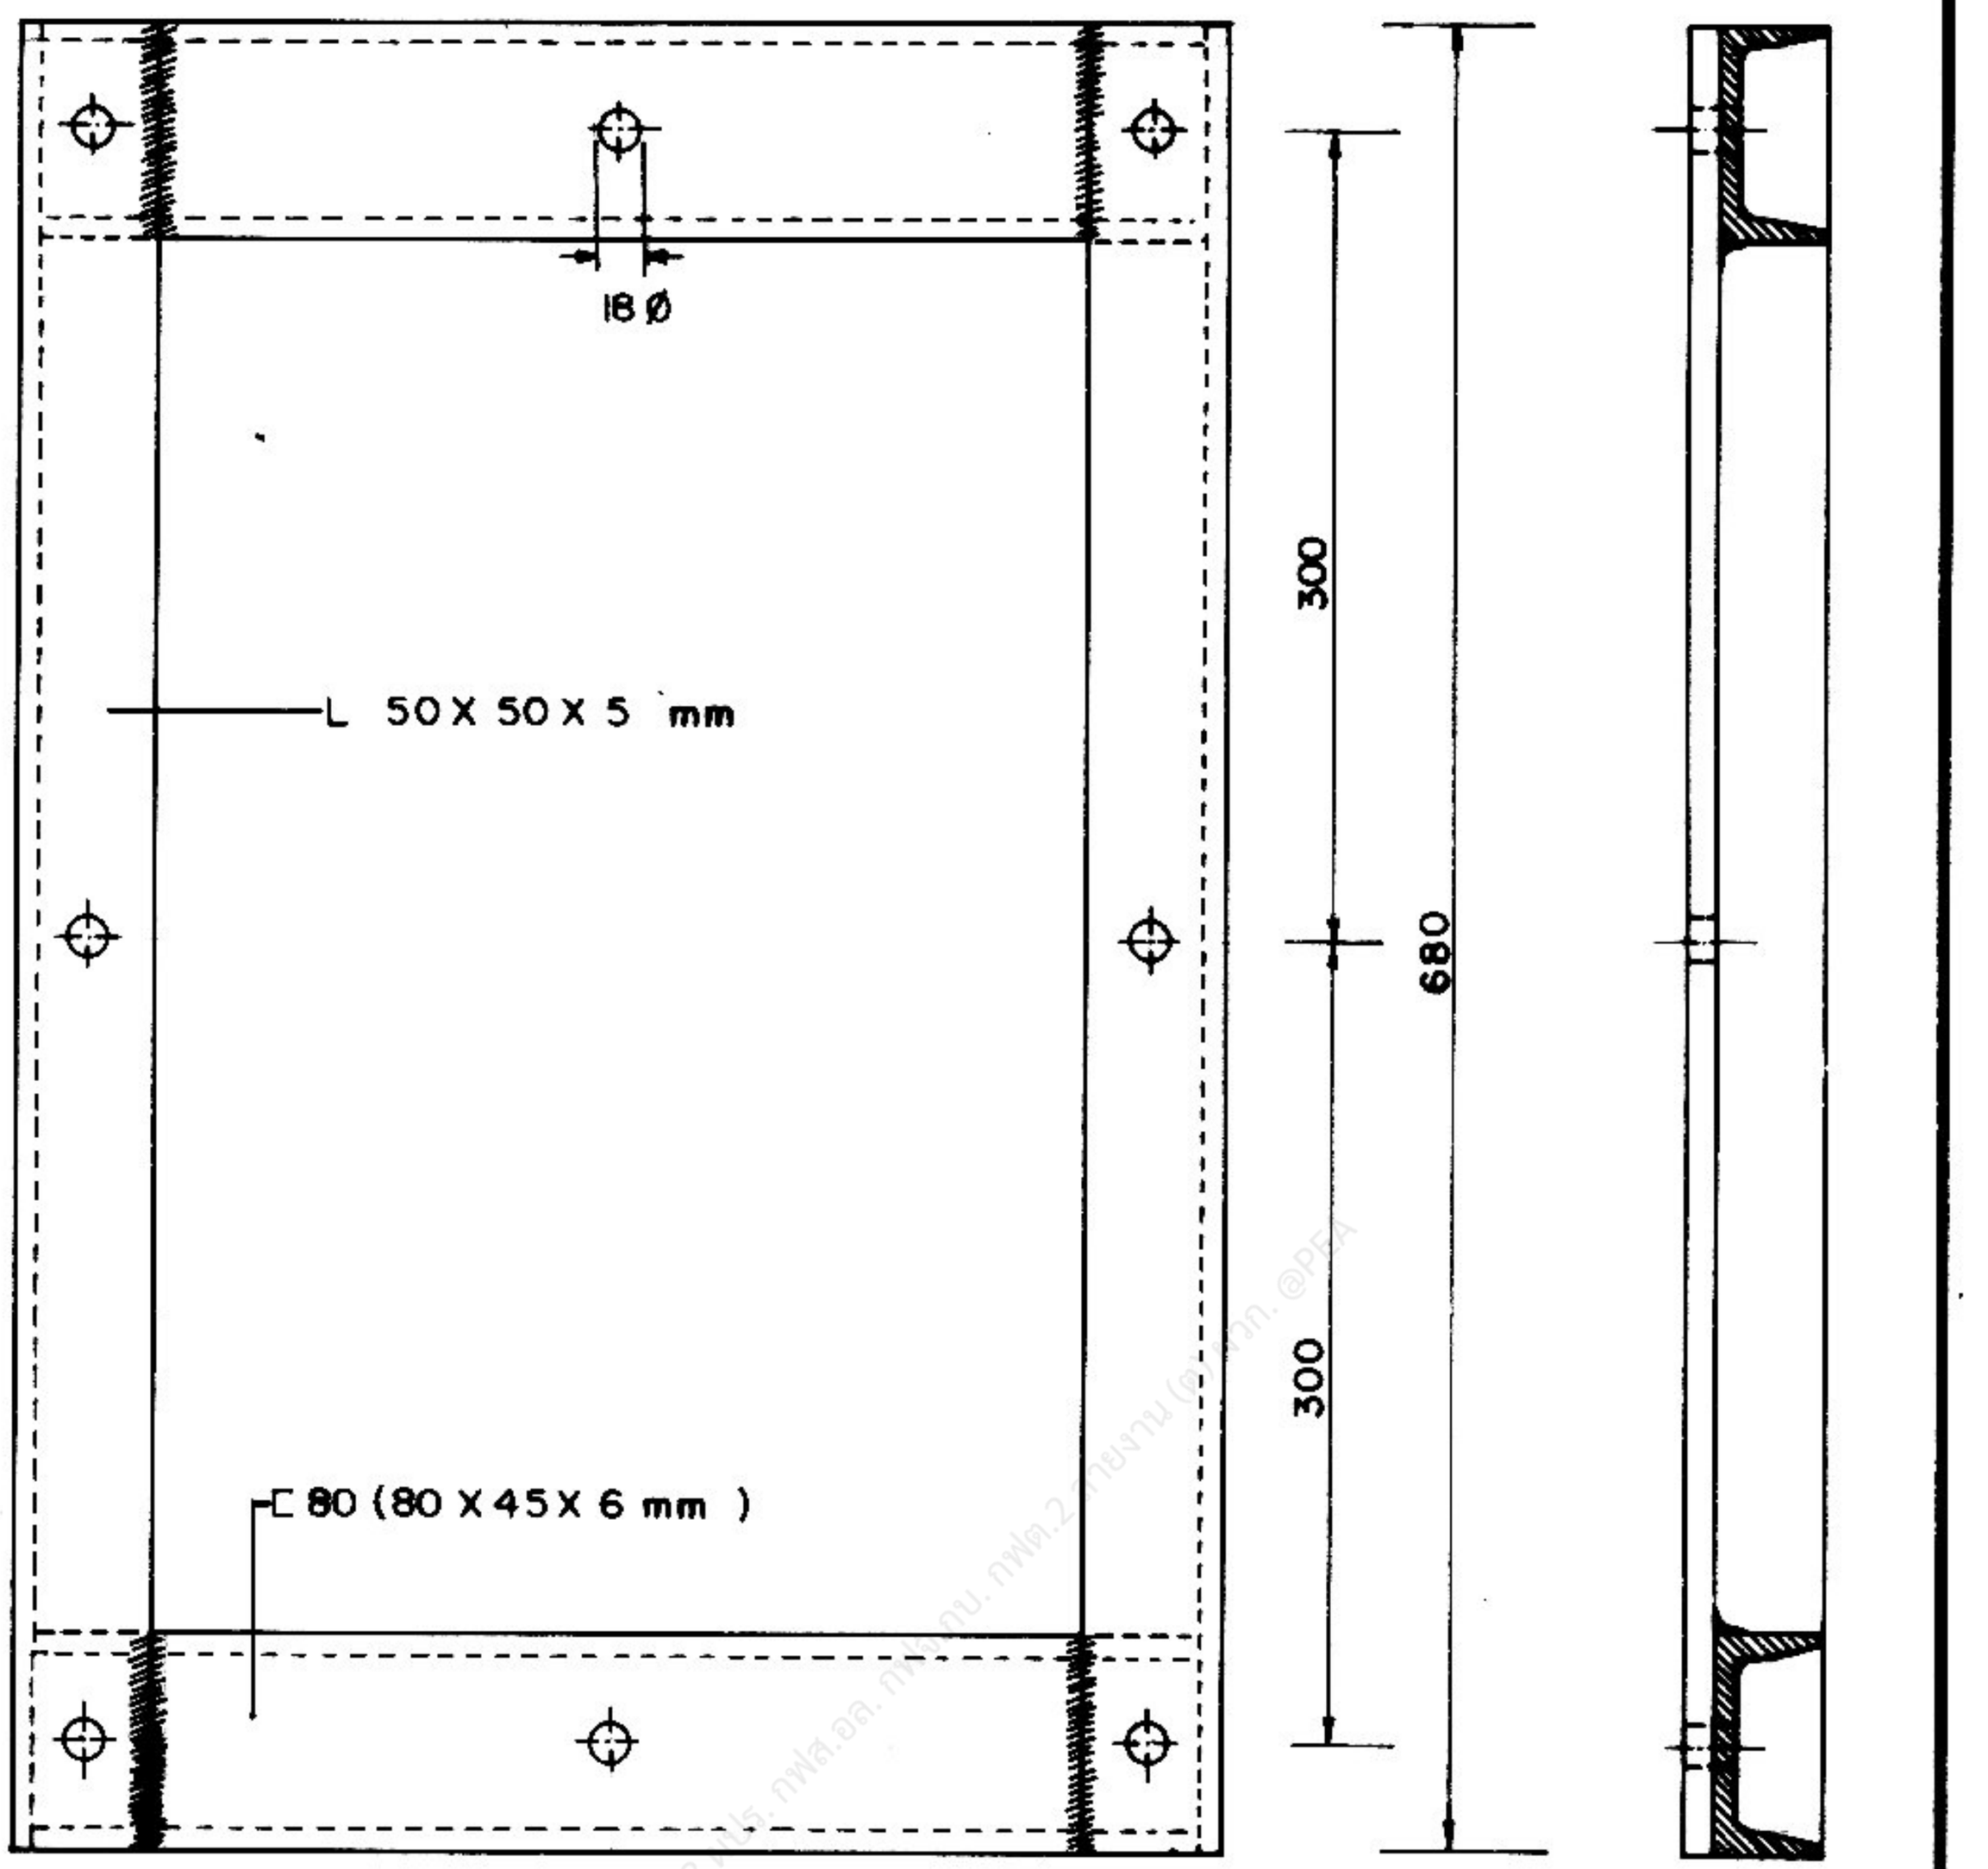



รูปตัด A - A
SECTION A - A

วัสดุ
MATERIAL

L 50 X 5 X 5 mm.	:	2 X 680	mm	LONG
C 80	:	2 X 450	mm	LONG


เชื่อมติดกัน
WELDED TOGETHER

น้ำหนัก : 12, 1 กก.
WEIGHT : 12, 1 Kg


GERMAN ADVISORY TEAM — PROVINCIAL ELECTRICITY AUTHORITY

มาตราส่วน SCALE 1 : 5	วันที่ DATE 10/2/70	นั่งร้านหม้อแปลง การติดตั้งฟิดเดอร์แรงต่ำ สำหรับ 2 วงจร — โครงเหล็กประกอบ
FOR G. A. T.	FOR P. E. A. Drw. by Ram	TRANSFORMER STATION L.T. FEEDER LINE INSTALLATION ARRANGEMENT FOR 2 CIRCUITS — AUX. FRAME
		Z 93 | 13004 | SHEET NO. 1 OF 3

การประกอบเลขที่ ASSEMBLY NO 0306

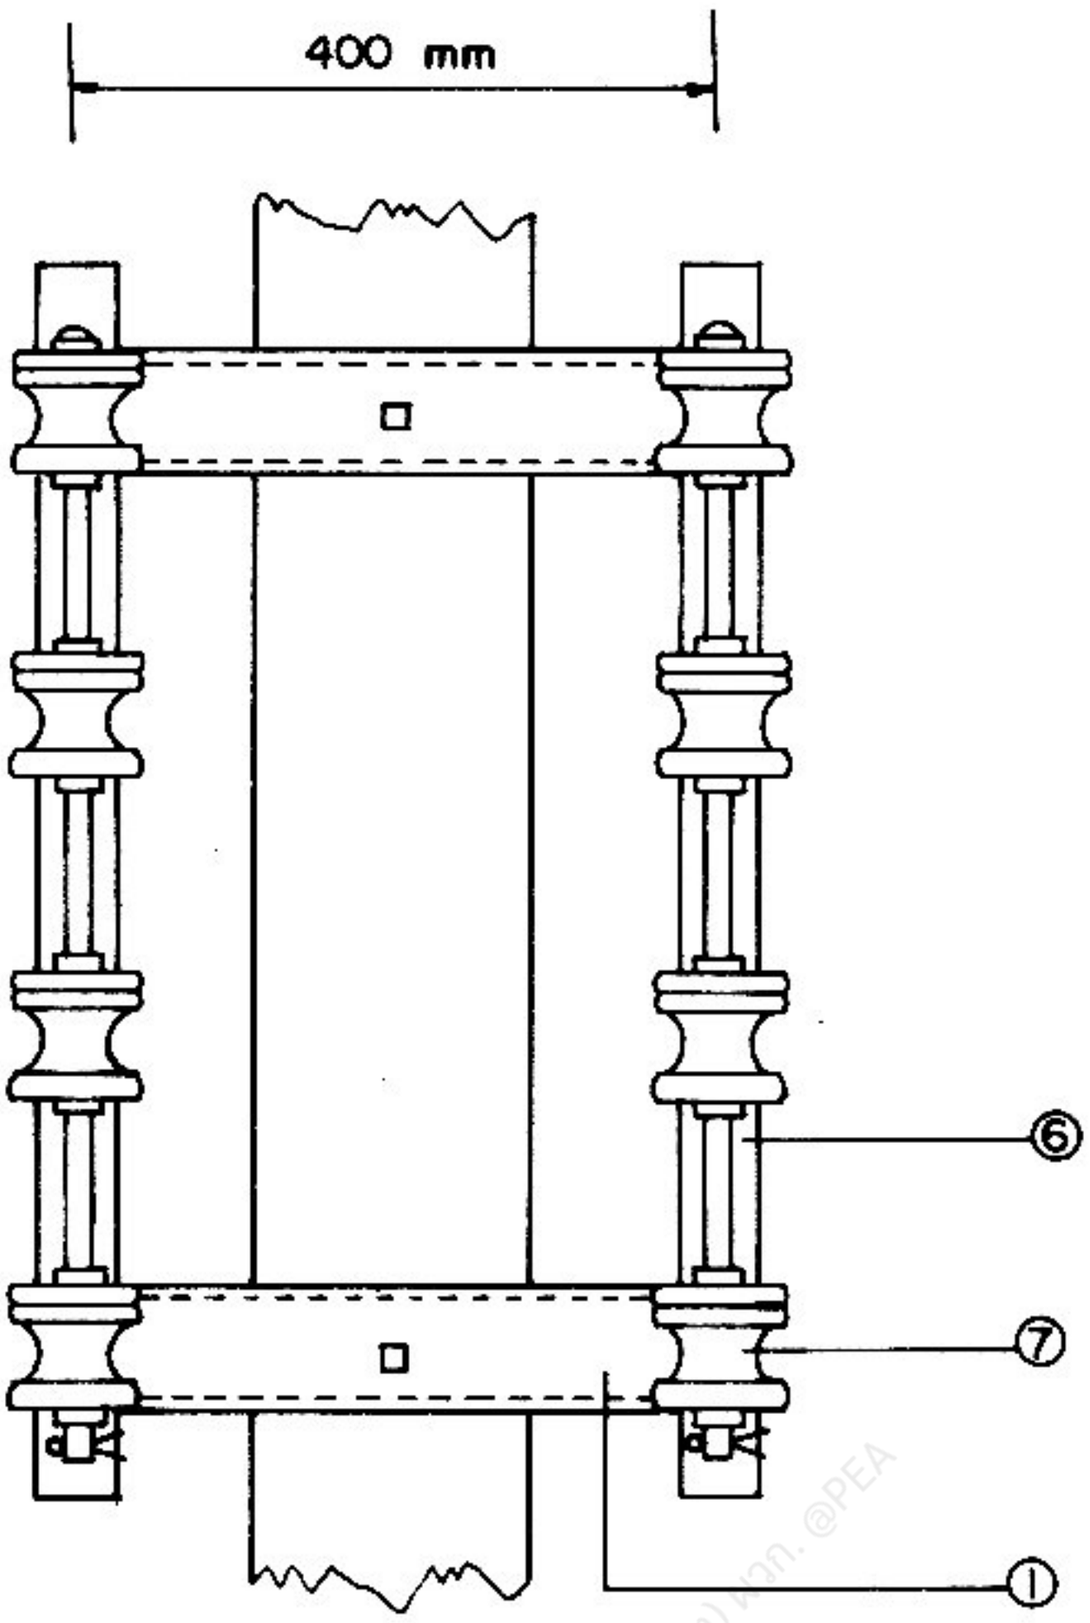

ด้านหน้า
— FRONT VIEW —

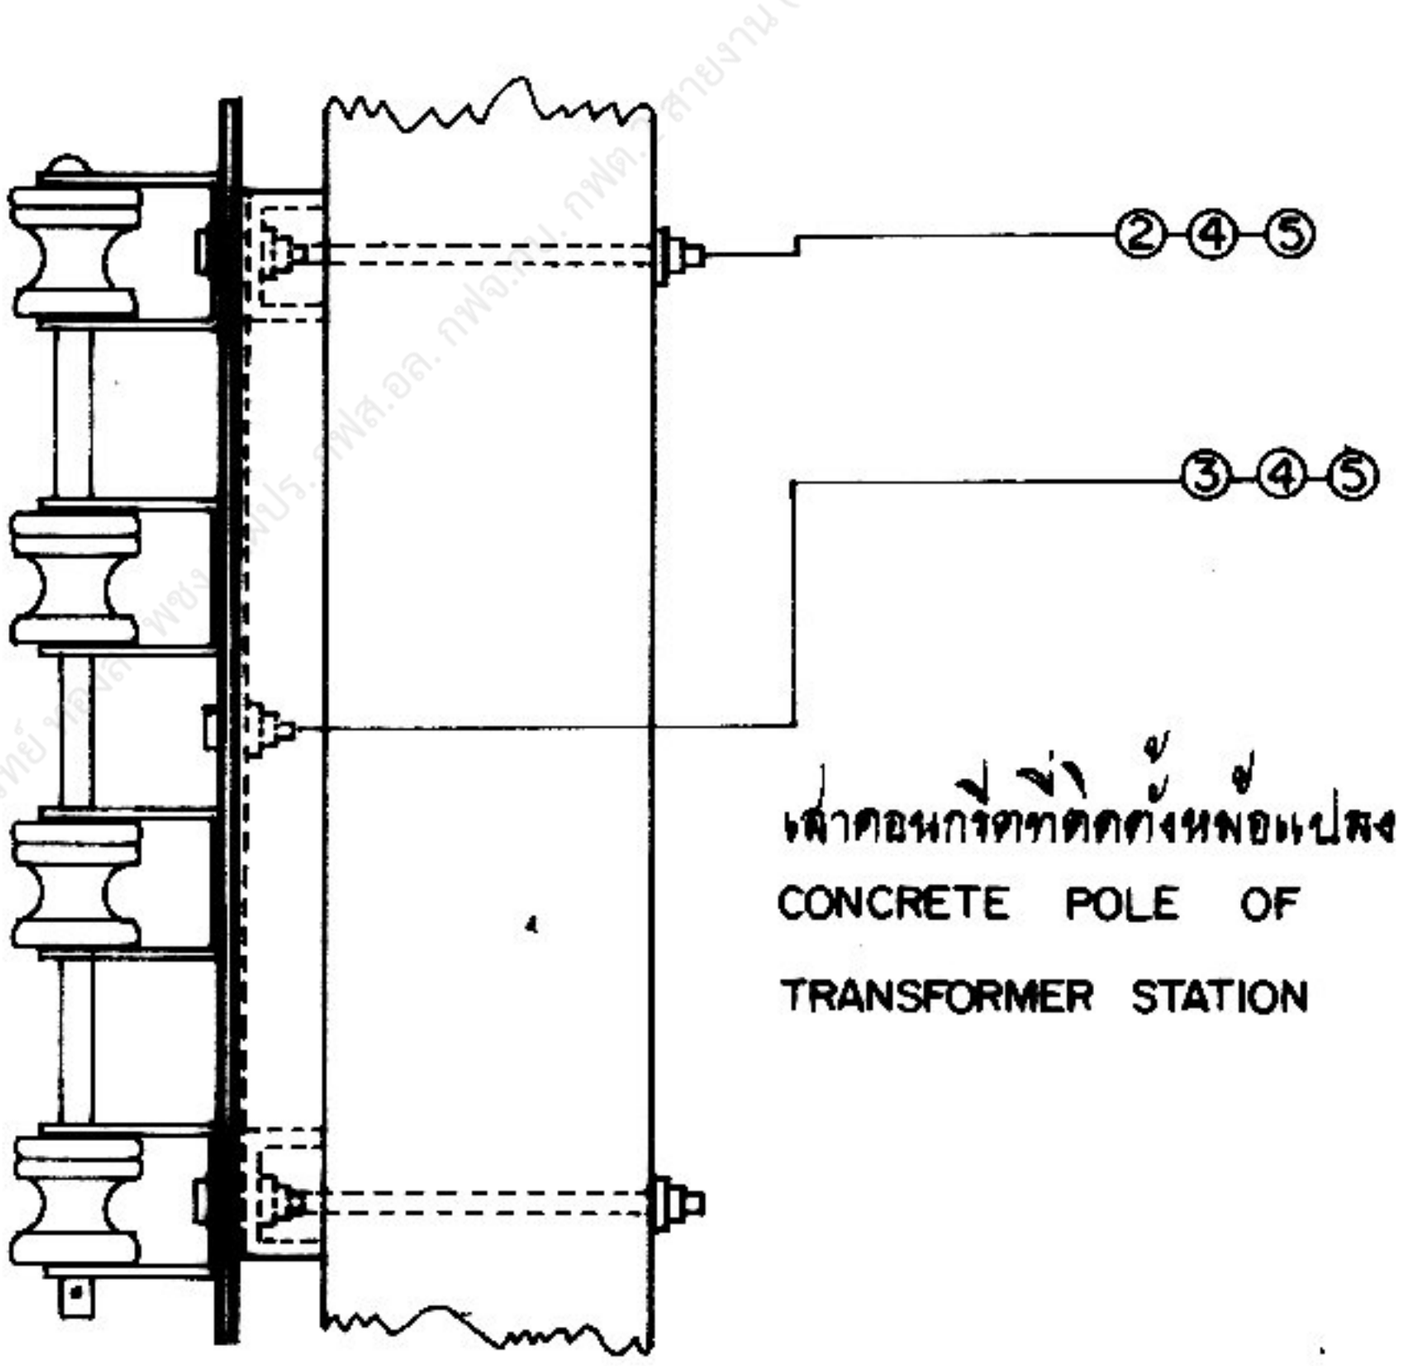

เสาคอนกรีตติดตั้งหม้อแปลง
CONCRETE POLE OF
TRANSFORMER STATION

ด้านข้าง
— SIDE VIEW —

GERMAN ADVISORY TEAM — PROVINCIAL ELECTRICITY AUTHORITY

มาตราส่วน SCALE 1 : 10	วันที่ DATE 10/2/70	หัวข้อหม้อแปลง การวางตำแหน่ง การติดตั้งฟีดเดอร์แรงต่ำ 2 วงจร
FOR G. A. T.	FOR P. E. A. Drw. by Ron	
16/3/70		TRANSFORMER STATION L.T. FEEDER LINE INSTALLATION ARRANGEMENT FOR 2 CIRCUITS
		Z 93 / 13004 / SHEET NO. 2 OF 3

การประกอบเลขที่ ASSEMBLY NO. 0306

BILL OF MATERIAL

ITEM	DESCRIPTION	REQ'D	MAT. NO
1	โครงประกอบ, เหล็ก, ขนาด 680 X 460 มม. AUXILIARY FRAME, STEEL, 680 X 460 mm	1	—
2	สลักเกลียว M 16 X 300 มม. พร้อมน็อทเหลี่ยม BOLT, MACHINE, M16 X 300 mm , COMPLETE WITH SQUARE NUT	2	01110204
3	สลักเกลียว M 16 X 40 มม. พร้อมน็อทเหลี่ยม BOLT, MACHINE, M16 X 40 mm , COMPLETE WITH SQUARE NUT	6	—
4	แหวนสี่เหลี่ยมแบน 52 X 52 X 4.5 มม. รู Ø 18 มม. มอก. 258 WASHER, SQUARE, FLAT, 52 X 52 X 4.5 mm, HOLE Ø 18 mm, TIS 258	2	01180100
5	แหวนสปริง M 16 มอก. 259 WASHER, LOCK, M 16, TIS 259	8	01180318
6	แร็ค 4 X 200 มม. แบบหล่ำย่น RACK, SECONDARY, MEDIUM PRESSED STEEL, 4 x 200 mm EXT BACK	2	03130002
7	ลูกถ้วยแรงต่ำ มอก. 227 แบบ ข (แบบ 53-2) INSULATOR, SPOOL TYPE, L.T., TIS 227, TYPE B (CLASS 53-2)	8	03030000

GERMAN ADVISORY TEAM — PROVINCIAL ELECTRICITY AUTHORITY

มาตราส่วน SCALE	วันที่ DATE 11/2/70	หม้อแปลง การวางตำแหน่ง การติดตั้งฟิดเดอร์แรงต่ำ 2 วงจร
FOR G. A. T.	FOR P. E. A. Drw. by Ron	TRANSFORMER STATION L.T. FEEDER LINE INSTALLATION ARRANGEMENT FOR 2 FEEDERS
		Z 93 | 13004 | SHEET NO. 3 OF 3