การประกอบเลขที่ **5271**
ASSEMBLY NO.

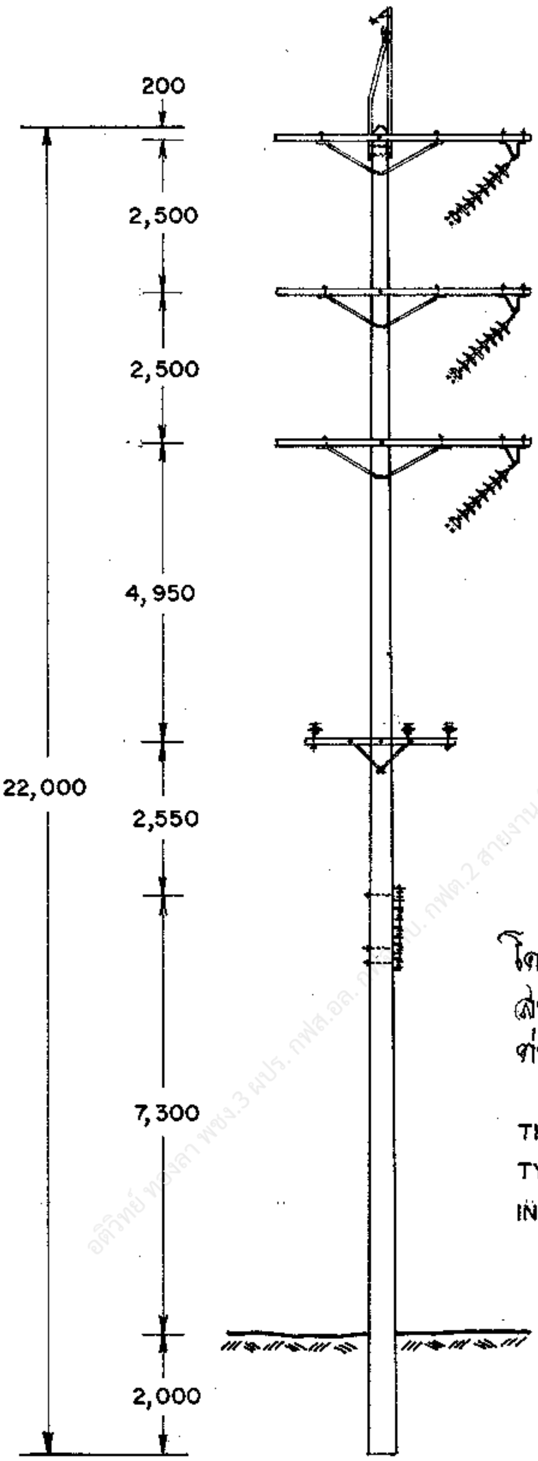

โครงสร้างนี้ ใช้งานได้เช่นเดียวกับโครงสร้าง แบบ SD-SA-1 (โครงสร้างแตกต่างกันที่วัสดุรายการที่ ② และ ⑨)

THIS STRUCTURE IS USED AS SD-SA-1 TYPE STRUCTURE (MATERIAL DIFFERENCE IN ITEM ② AND ⑨ FOR EACH STRUCTURE)

กองวิศวกรรมไฟฟ้าและเครื่องกล ฝ่ายวิศวกรรม	**การไฟฟ้าส่วนภูมิภาค**	ใช้แทนแบบ ถูกแทนโดยแบบ
ผู้เขียน ผู้สำรวจ วิศวกร หัวหน้าแผนก ผู้อำนวยการกอง ผู้อำนวยการฝ่าย	ผู้ว่าการ	เขียนเสร็จวันที่ 29 ก.ค. 35 แก้แบบวันที่ มิติเป็น มิลลิเมตร มาตราส่วน 1 : 125
	115 kV วงจรเดี่ยว สายไฟฟ้าคู่ เสาสำหรับทางโค้ง แบบ SD-SA-4	
รองผู้ว่าการฝ่ายเทคนิค	115 kV SINGLE CIRCUIT DOUBLE CONDUCTOR SMALL ANGLE STRUCTURE TYPE SD-SA-4	แบบเลขที่ SAI-015/35027 แผ่นที่ 1 ของจำนวน 3 แผ่น

@PEA

การประกอบเลขที่ ASSEMBLY NO. **5271**

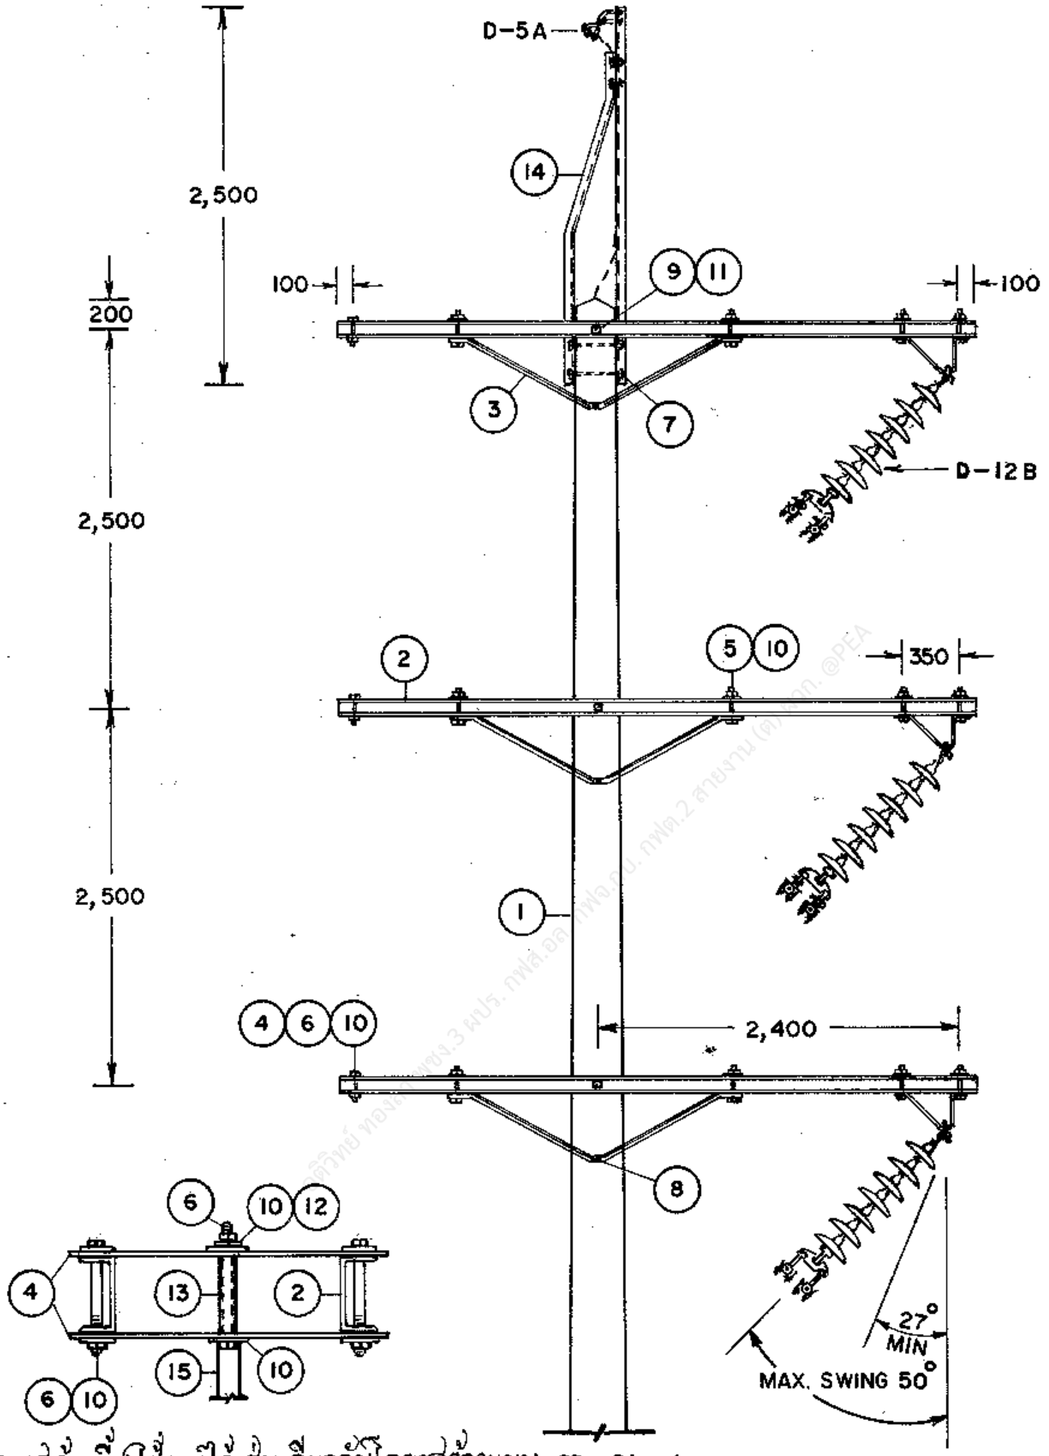

โครงสร้างนี้ ใช้งานได้เช่นเดียวกับโครงสร้างแบบ SD-SA-1
THIS STRUCTURE IS USED AS SD-SA-1 TYPE STRUCTURE

กองวิศวกรรมไฟฟ้าและเครื่องกล
ฝ่ายวิศวกรรม

ผู้เขียน สมหมาย.
ผู้สำรวจ
วิศวกร
หัวหน้าแผนก
ผู้อำนวยการกอง
ผู้อำนวยการฝ่าย

รองผู้ว่าการฝ่ายเทคนิค

การไฟฟ้าส่วนภูมิภาค

ผู้ว่าการ 2 8 พ.ย. 2535

115 kV วงจรเดี่ยว สายไฟฟ้าคู่
เสาสำหรับทางโค้ง
แบบ SD-SA-4

115 kV SINGLE CIRCUIT DOUBLE CONDUCTOR
SMALL ANGLE STRUCTURE
TYPE SD-SA-4

ใช้แทนแบบ
ถูกแทนโดยแบบ
เขียนเสร็จวันที่ 29 ก.ค.35
แก้แบบวันที่
มิติเป็น มิลลิเมตร
มาตราส่วน 1:10, 1:50
แบบเลขที่ SAI-015/35027
แผ่นที่ 2 ของจำนวน 3 แผ่น

[illegible] ทอง[illegible] พชง.3 ผปร. กฟส.อล. กฟจ.[illegible] กฟต.2 สายงาน (ต) ผกก. @PEA

การประกอบเลขที่ ASSEMBLY NO. **5271**

บัญชีวัสดุ
BILL OF MATERIAL

ลำดับที่ ITEM	รายละเอียด DESCRIPTION	จำนวน REQ'D	วัสดุเลขที่ MAT. NO.
1	เสาคอนกรีต 22 ม. POLE, CONCRETE 22 m LONG	1	00010011 (0041)
2	คอนสายแบบเหล็ก รูปรางน้ำ ขนาด 100X50X5 มม. ยาว 4.20 ม. มอก. 116 CROSSARM, STEEL, CHANNEL 100X50X5 mm, 4.20 m LONG, TIS 116	6	
3	เหล็กฉากรับคอนสาย ขนาด 50X50X6 มม. ช่วงกว้าง 1,800 มม. ดรอพ 450 มม. BRACE, ANGLE STEEL, 50X50X6 mm, 1,800 mm, WIDE 450 mm, DROP	6	01200007 (0119)
4	แผ่นเหล็ก ขนาด 6X100X450 มม. PLATE, STEEL 6X100X450 mm	18	01030002 (0143)
5	สลักเกลียว M 16X130 มม. BOLT, MACHINE, M 16X130 mm	12	01110200 (0220)
6	สลักเกลียว M 16X170 มม. BOLT, MACHINE, M 16X170 mm	24	01110201 (0221)
7	สลักเกลียว M 16X300 มม. BOLT, MACHINE, M 16X300 mm	3	01110204 (0224)
8	สลักเกลียว M 16X350 มม. BOLT, MACHINE, M 16X350 mm	3	01110205 (0225)
9	สลักเกลียว M 20X350 มม. BOLT, MACHINE, M 20X350 mm	3	01110300
10	แหวนสี่เหลี่ยมแบน 52X52X4.5 มม. รู Ø 18 มม. มอก. 258 WASHER, SQUARE FLAT 52X52X4.5 mm, HOLE Ø 18 mm, TIS 258	60	01180100 (0355)
11	แหวนสี่เหลี่ยมแบน 62X62X6 มม. รู Ø 22 มม. มอก. 258 WASHER, SQUARE FLAT 62X62X6 mm, HOLE Ø 22 mm, TIS 258	6	01180101 (0356)
12	แหวนสปริง M 16 มอก. 259 WASHER, LOCK, M 16, TIS 259	6	01180301 (0365)
13	ท่อเหล็ก ชื่อขนาด 20 มม. หนา 2.65 มม. ยาว 100 มม. มอก. 277 ประเภท 2 PIPE, IRON, DIA 20 mm I.D. 2.65 mm THICKNESS, 100 mm LONG TIS 277 TYPE 2	6	01050000 (0905)
14	เหล็กฉากรับสายล่อฟ้าทางโค้ง OVERHEAD GROUND WIRE CORNER BAYONET	1	01010005 (0136)
15	ที่แขวนลูกถ้วยทางโค้ง BRACKET, CORNER SUSPENSION	3	03140012 (0489)
	รายละเอียด DETAIL		
D-12B	การประกอบลูกถ้วยแขวน SUSPENSION INSULATOR ASSEMBLY	3	
D-5A	การต่อสายล่อฟ้า OVERHEAD GROUND WIRE CONNECTION	1	
D-10A	ฐานรากเสา POLE FOUNDATION	1	

กองวิศวกรรมไฟฟ้าและเครื่องกล
ฝ่ายวิศวกรรม

การไฟฟ้าส่วนภูมิภาค

ผู้เขียน ____
ผู้ตรวจ ____
วิศวกร ____
หัวหน้าแผนก ____
ผู้อำนวยการกอง ____
ผู้อำนวยการฝ่าย ____

รองผู้ว่าการฝ่ายเทคนิค ____

ผู้ว่าการ ____ 2535

115 kV วงจรเดี่ยว สายไฟฟ้าคู่
เสาสำหรับทางโค้ง
แบบ SD-SA-4

115 kV SINGLE CIRCUIT DOUBLE CONDUCTOR
SMALL ANGLE STRUCTURE
TYPE SD-SA-4

ใช้แทนแบบ ____
ถูกแทนโดยแบบ ____
เขียนเสร็จวันที่ 29 ก.ค. 35
แก้แบบวันที่ ____
มิติเป็น —
มาตราส่วน —

แบบเลขที่ SAI-015/35027
แผ่นที่ 3 ของจำนวน 3 แผ่น

1 9 พ.ค. 2535