การประกอบเลขที่ ASSEMBLY NO. 0210

N- สายเป็นกลาง NEUTRAL LINE
A,B,C- สายเฟส PHASE LINE
L- สายดับไฟถนน STREET LIGHTING LINE

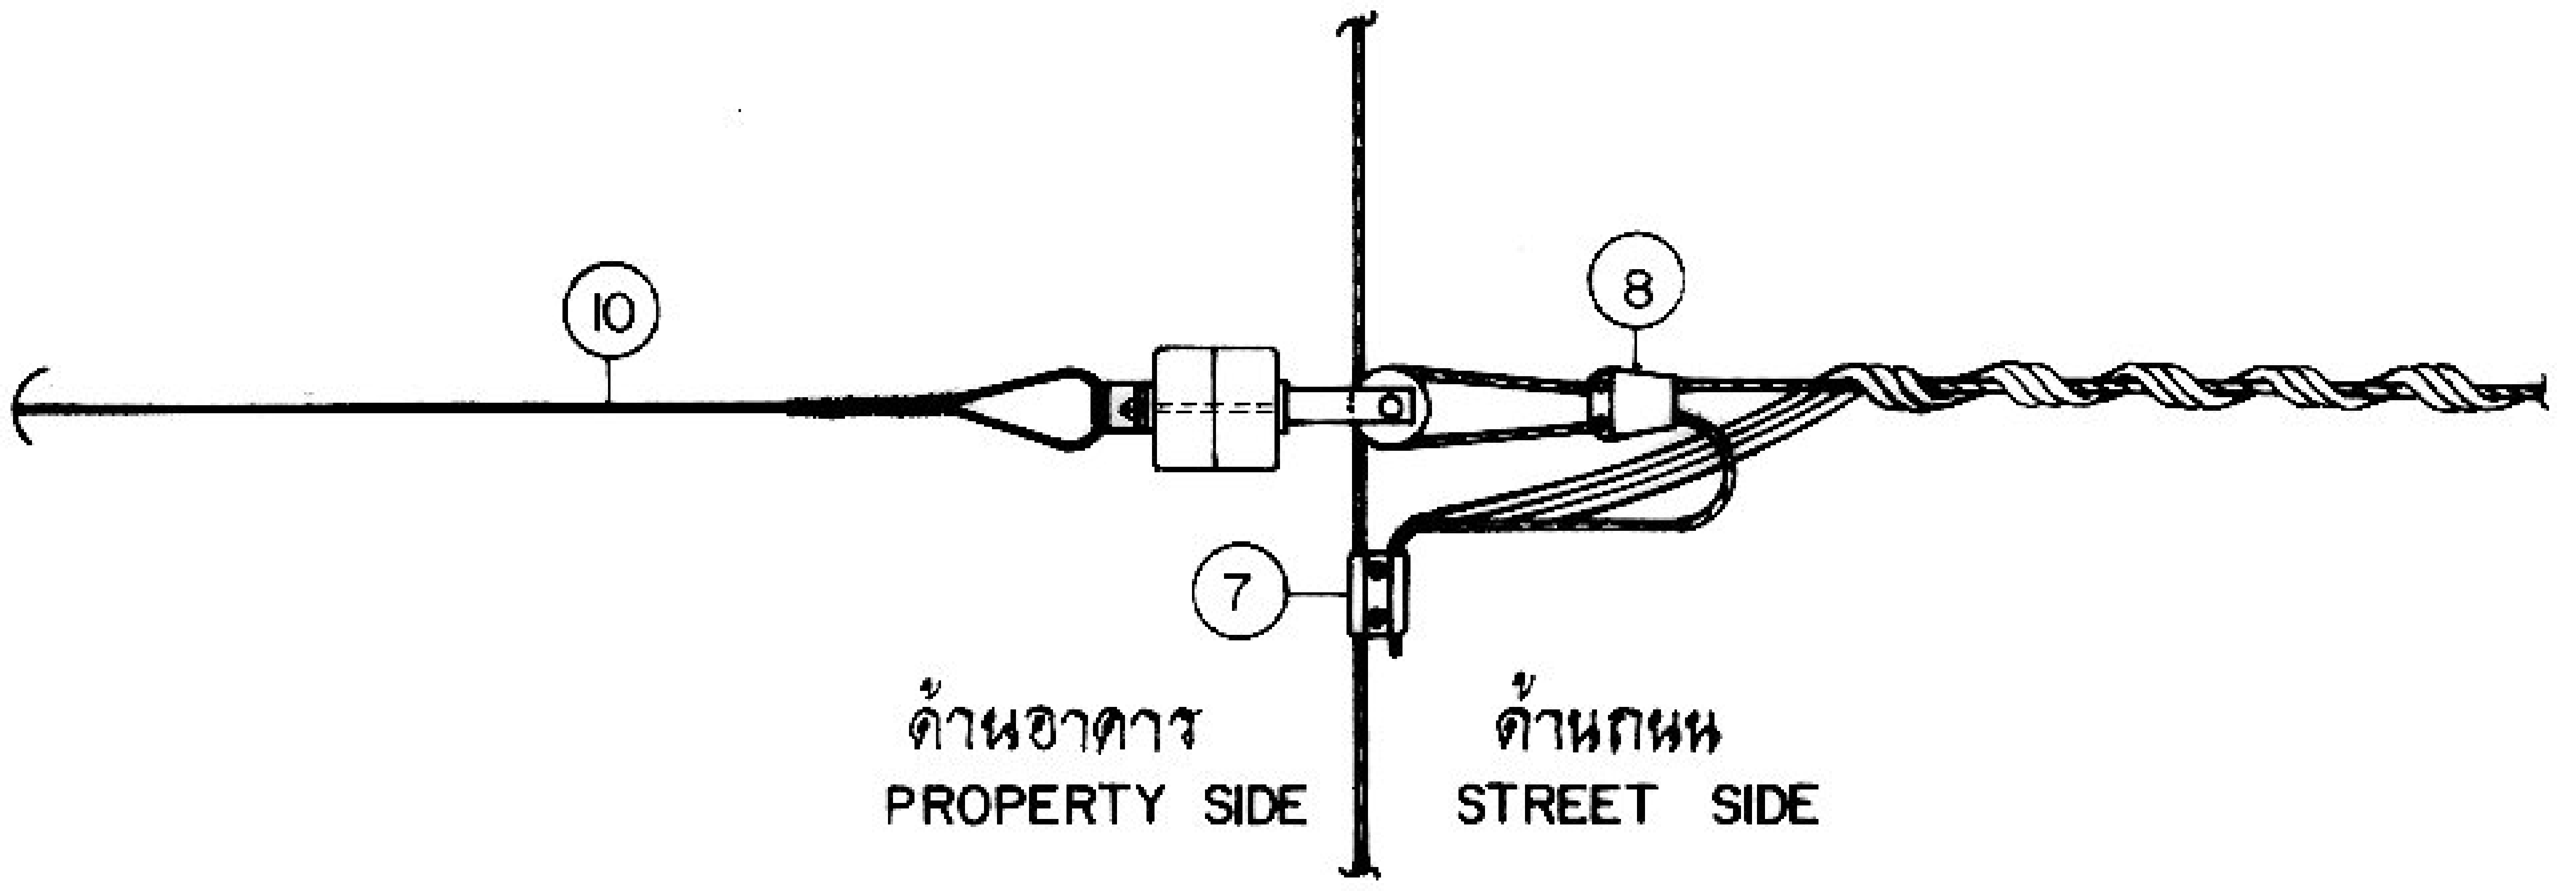

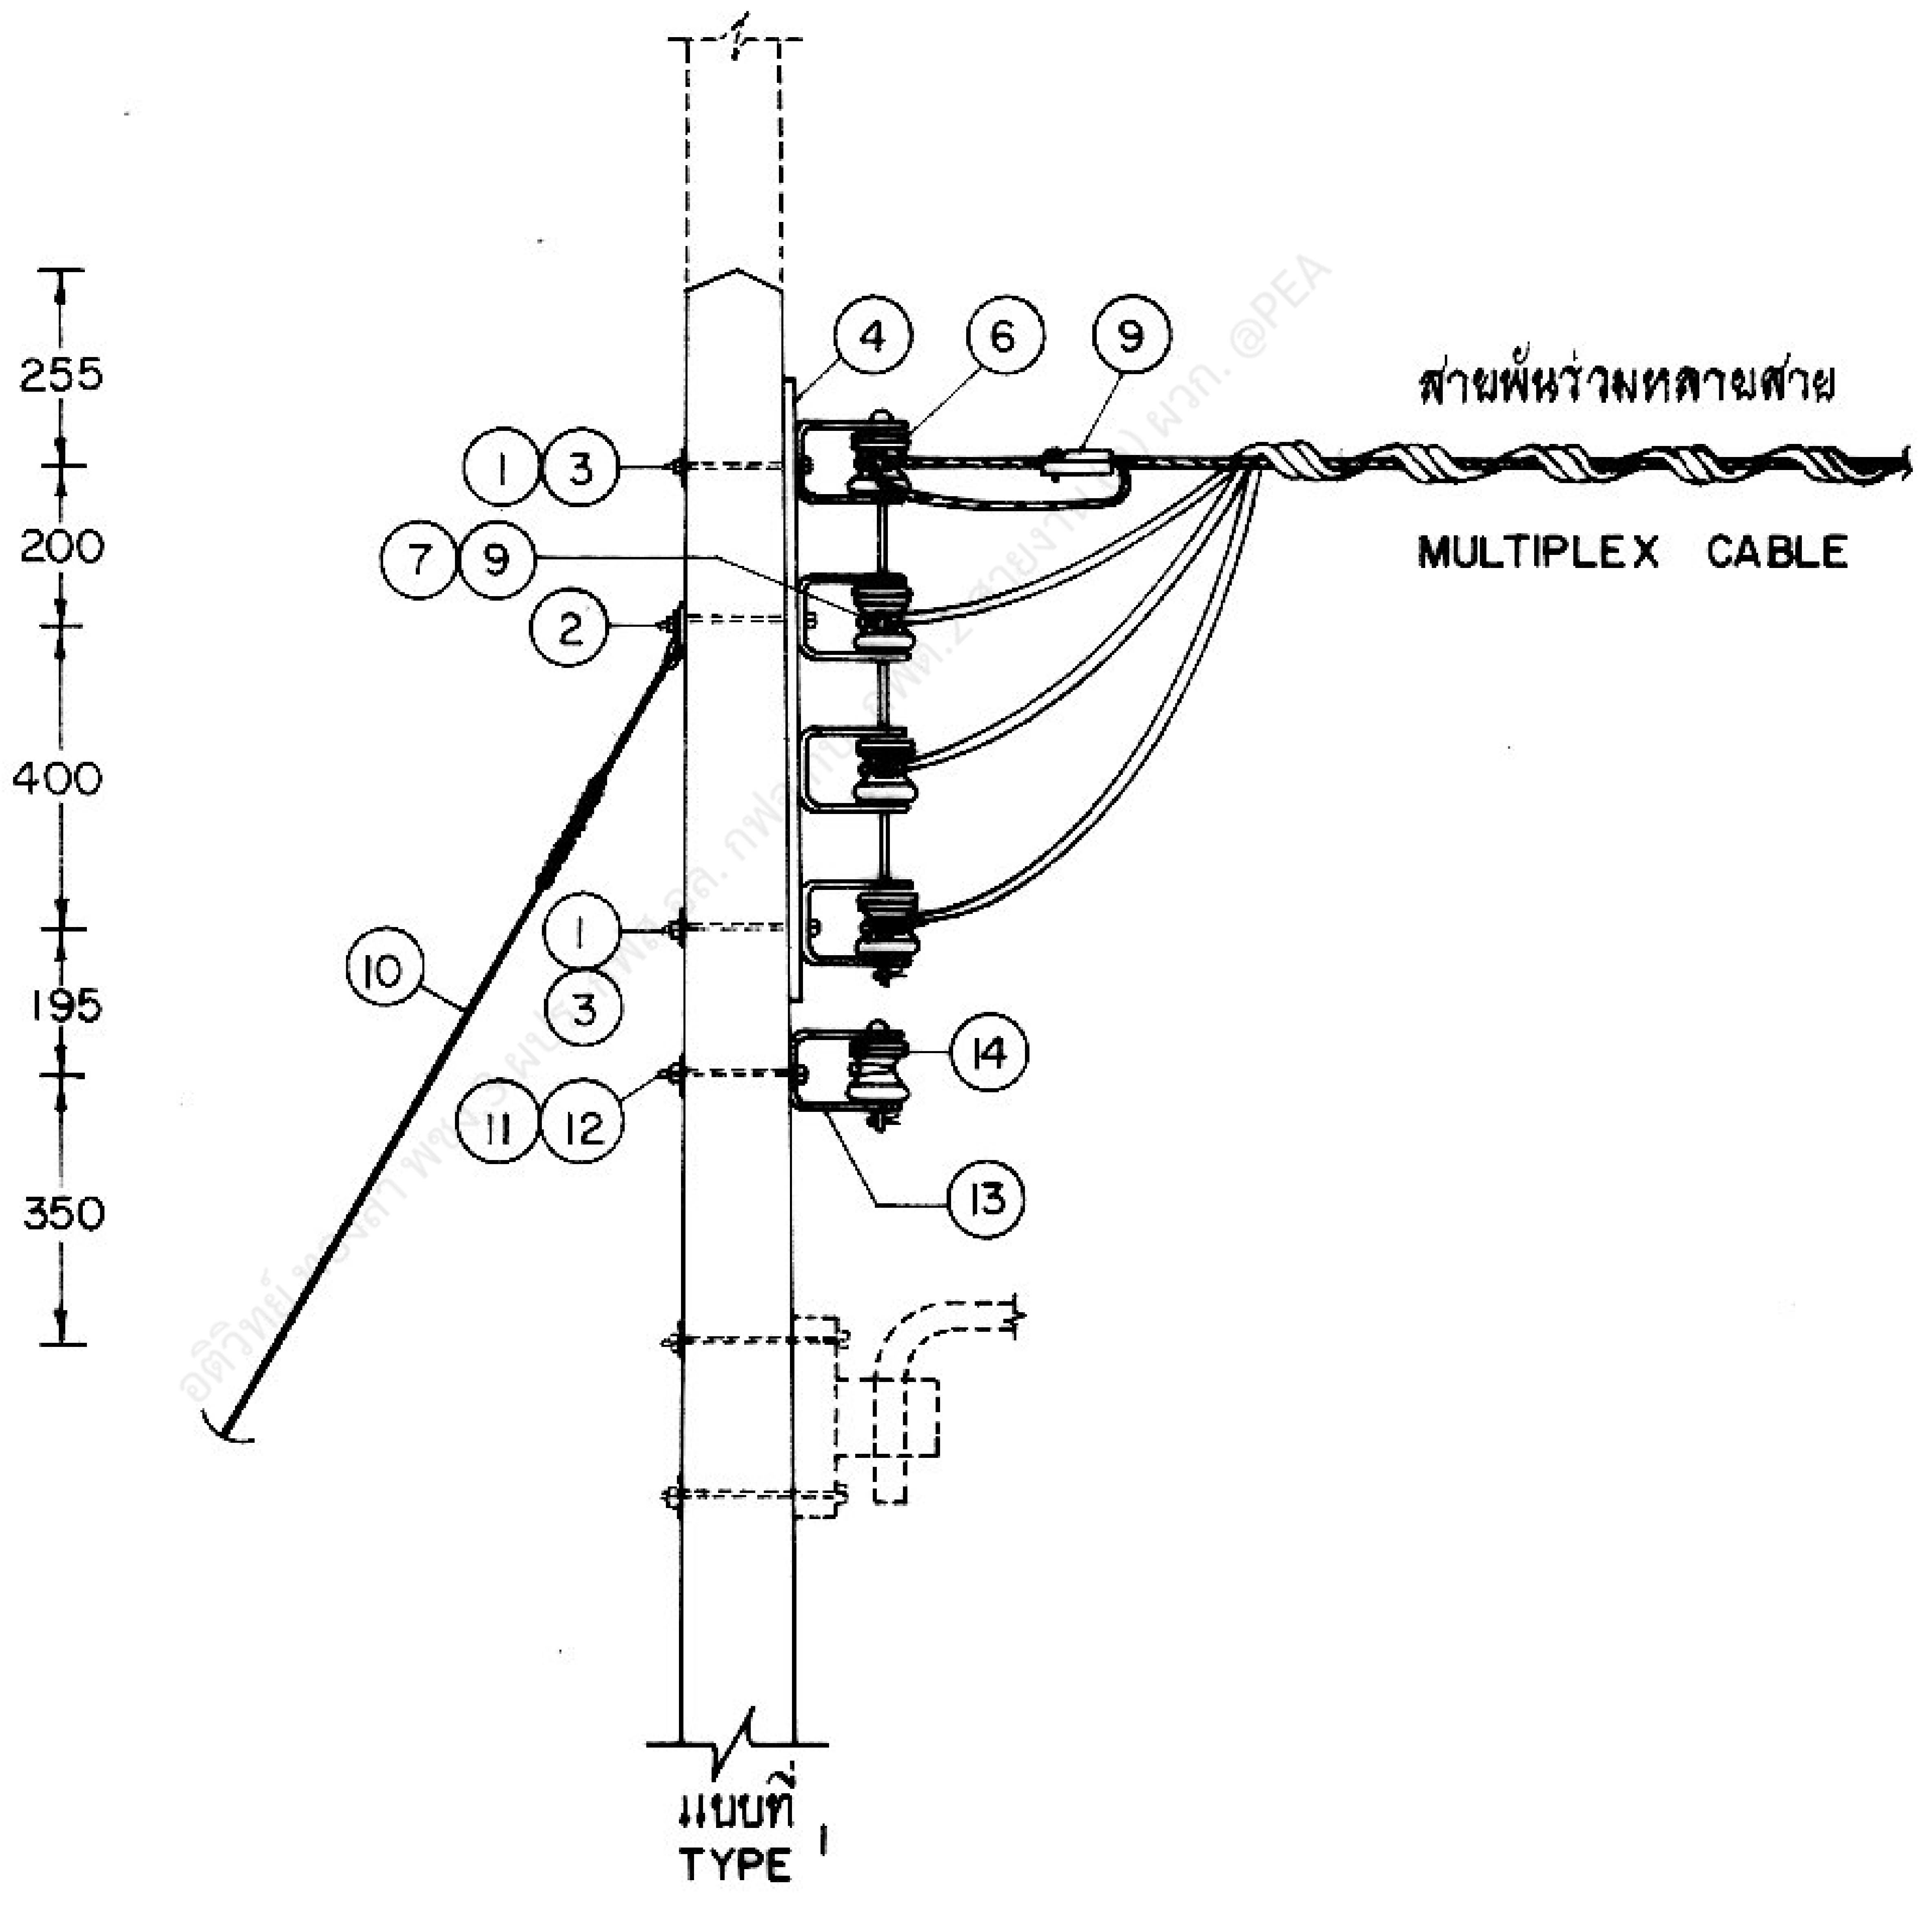

กองวิศวกรรมไฟฟ้าและเครื่องกล ฝ่ายวิศวกรรม	การไฟฟ้าส่วนภูมิภาค	ใช้แทนแบบ ถูกแทนโดยแบบ
ผู้เขียน ผู้สำรวจ วิศวกร หัวหน้าแผนก หัวหน้ากอง ผู้อำนวยการฝ่าย	ผู้ว่าการ การติดตั้งแร็คแรงต่ำกับเสาคอนกรีต 9 ม. สำหรับการต่อแยกสาย	เขียนเสร็จวันที่ 15 สค. 21 แก้แบบวันที่ มิติเป็น มม. มาตราส่วน 1:20
รองผู้ว่าการฝ่ายเทคนิค	SECONDARY RACK INSTALLATION ON 9 m CONCRETE POLE FOR TAP LINE	แบบเลขที่ SAI-015/21046 แผ่นที่ 1 ของจำนวน 4 แผ่น

การประกอบเลขที่ 0210
ASSEMBLY NO.

N- สายนิวทรัล / NEUTRAL LINE
A,B,C- สายเฟส / PHASE LINE
L- สายดับไฟถนน / STREET LIGHTING LINE

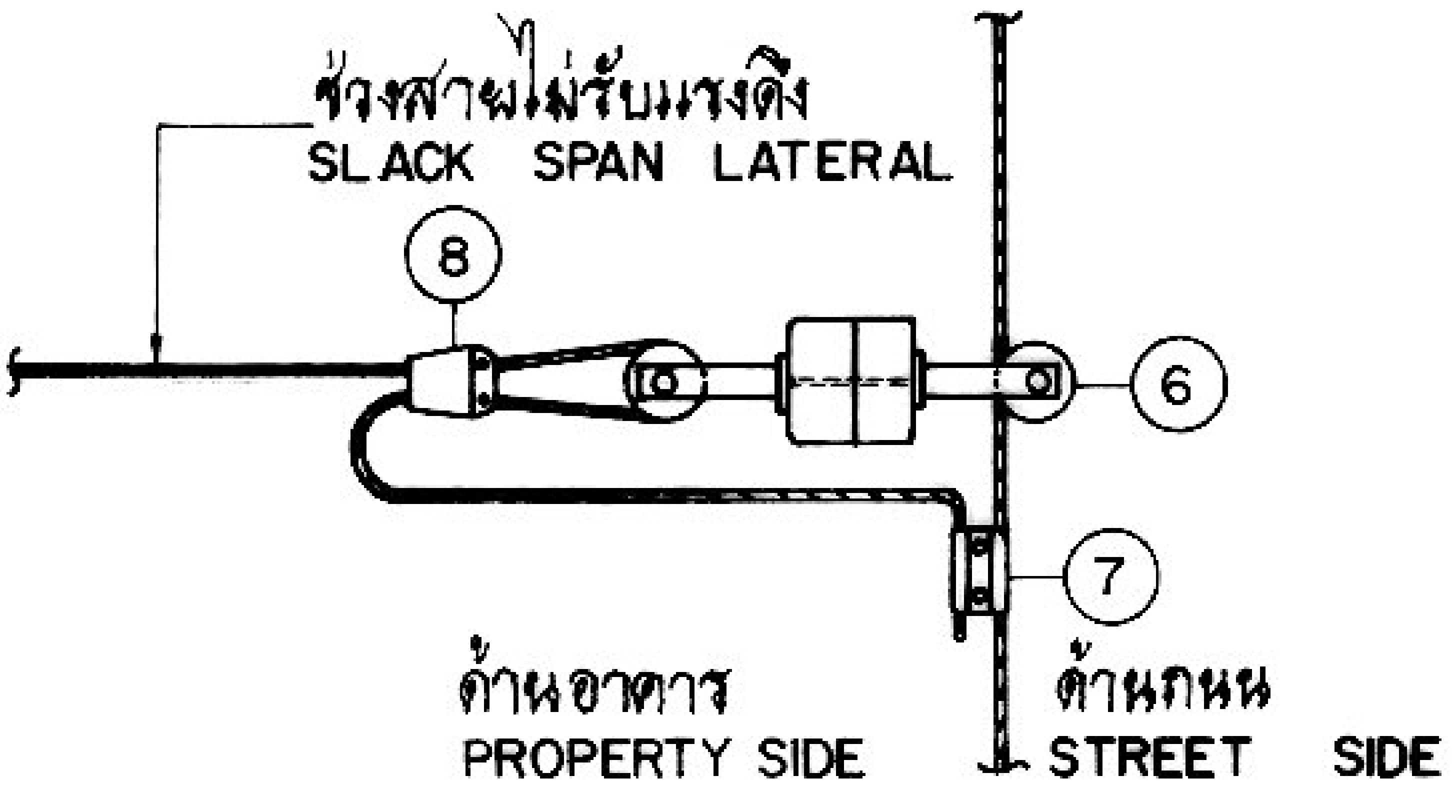

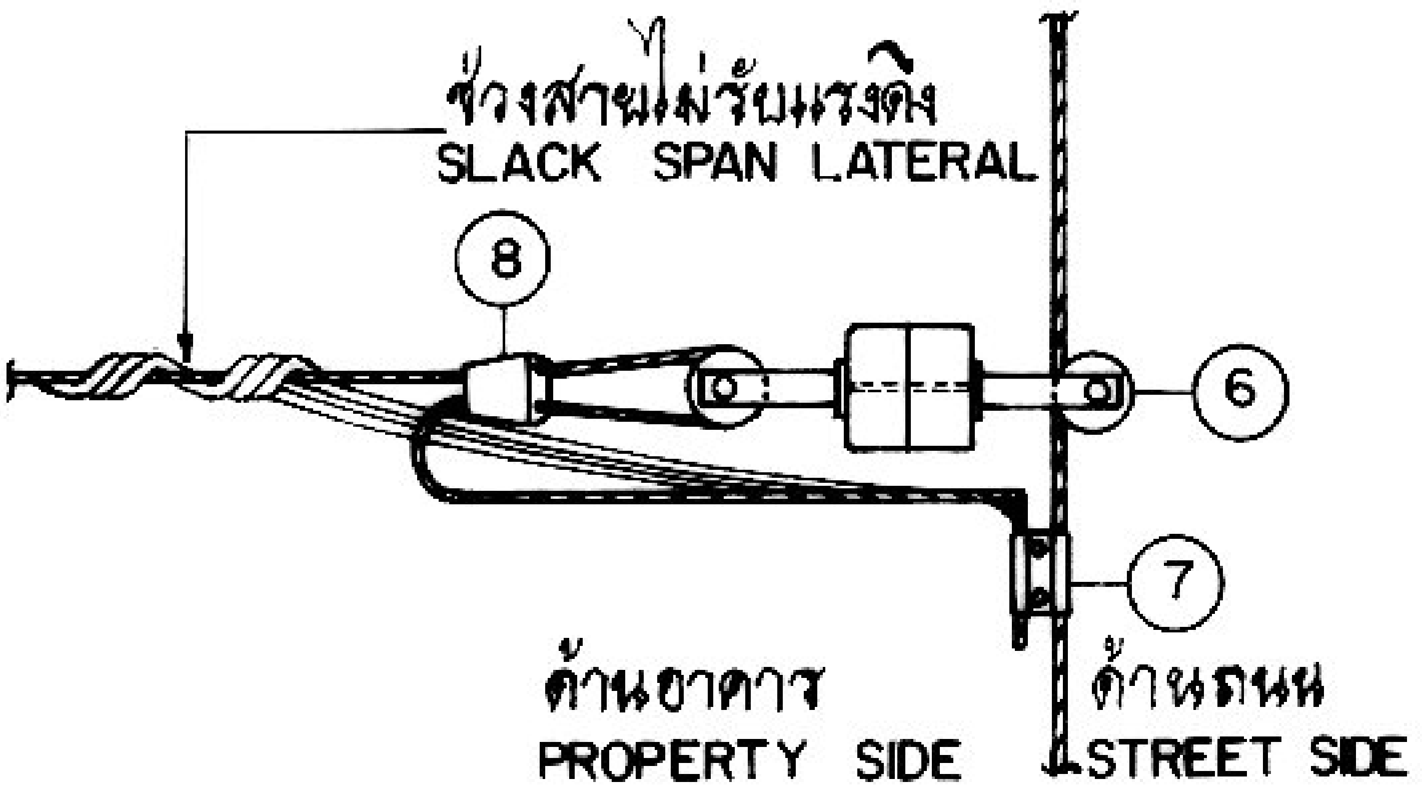

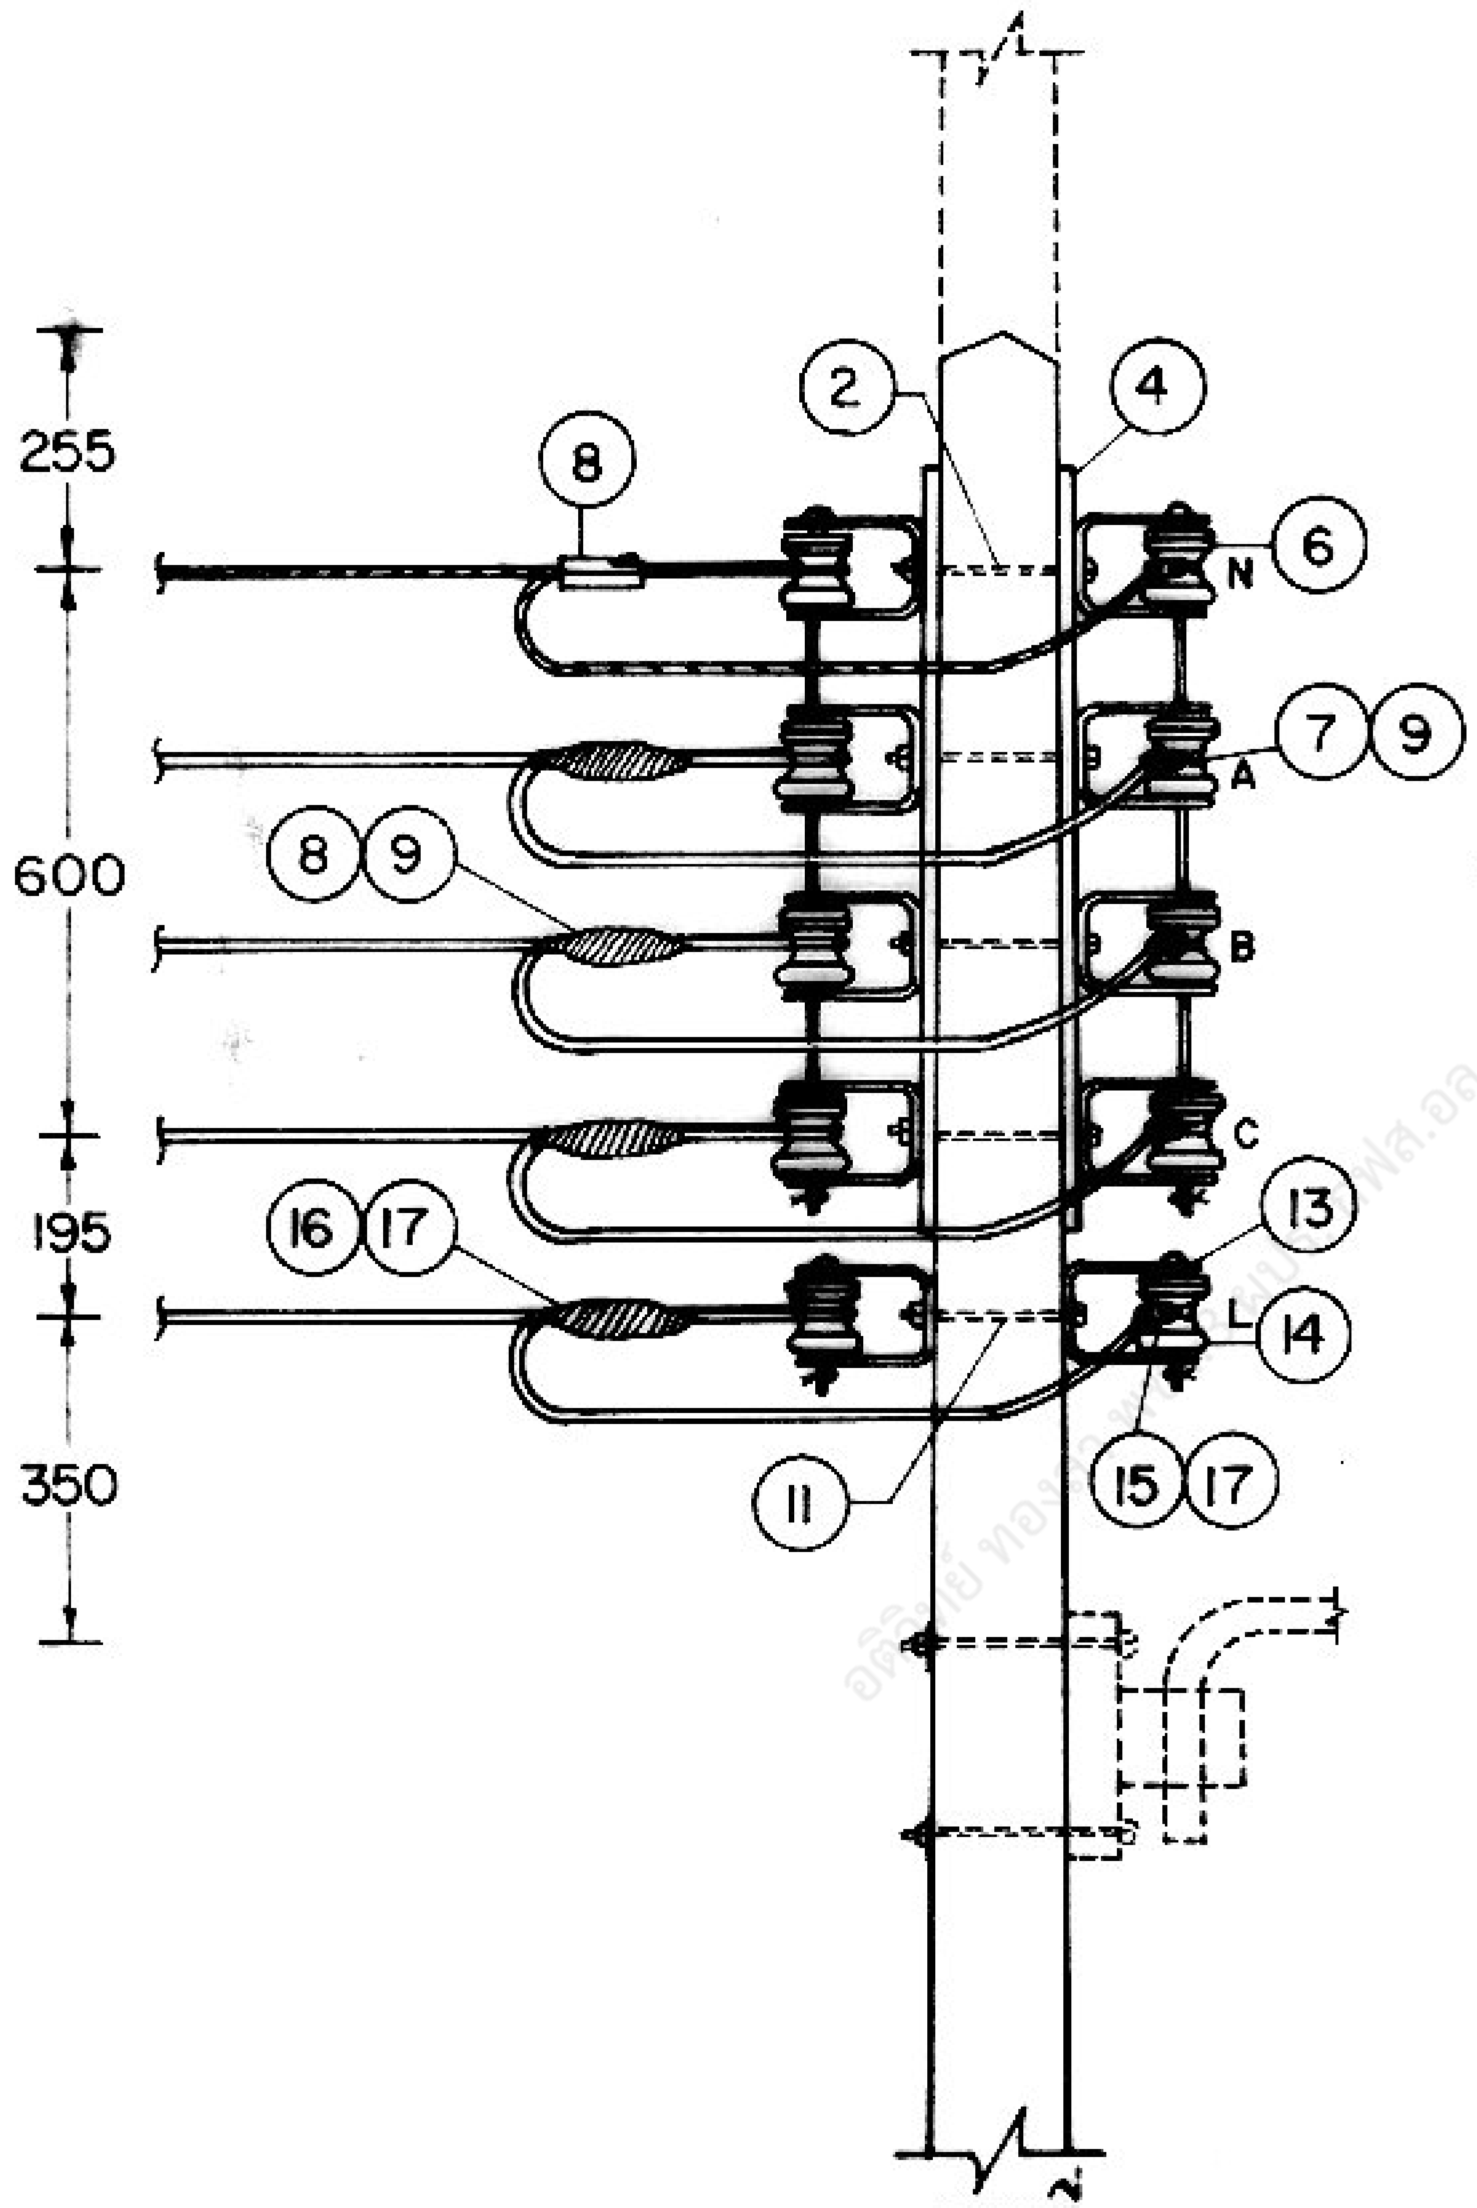

แบบที่ 2
TYPE 2

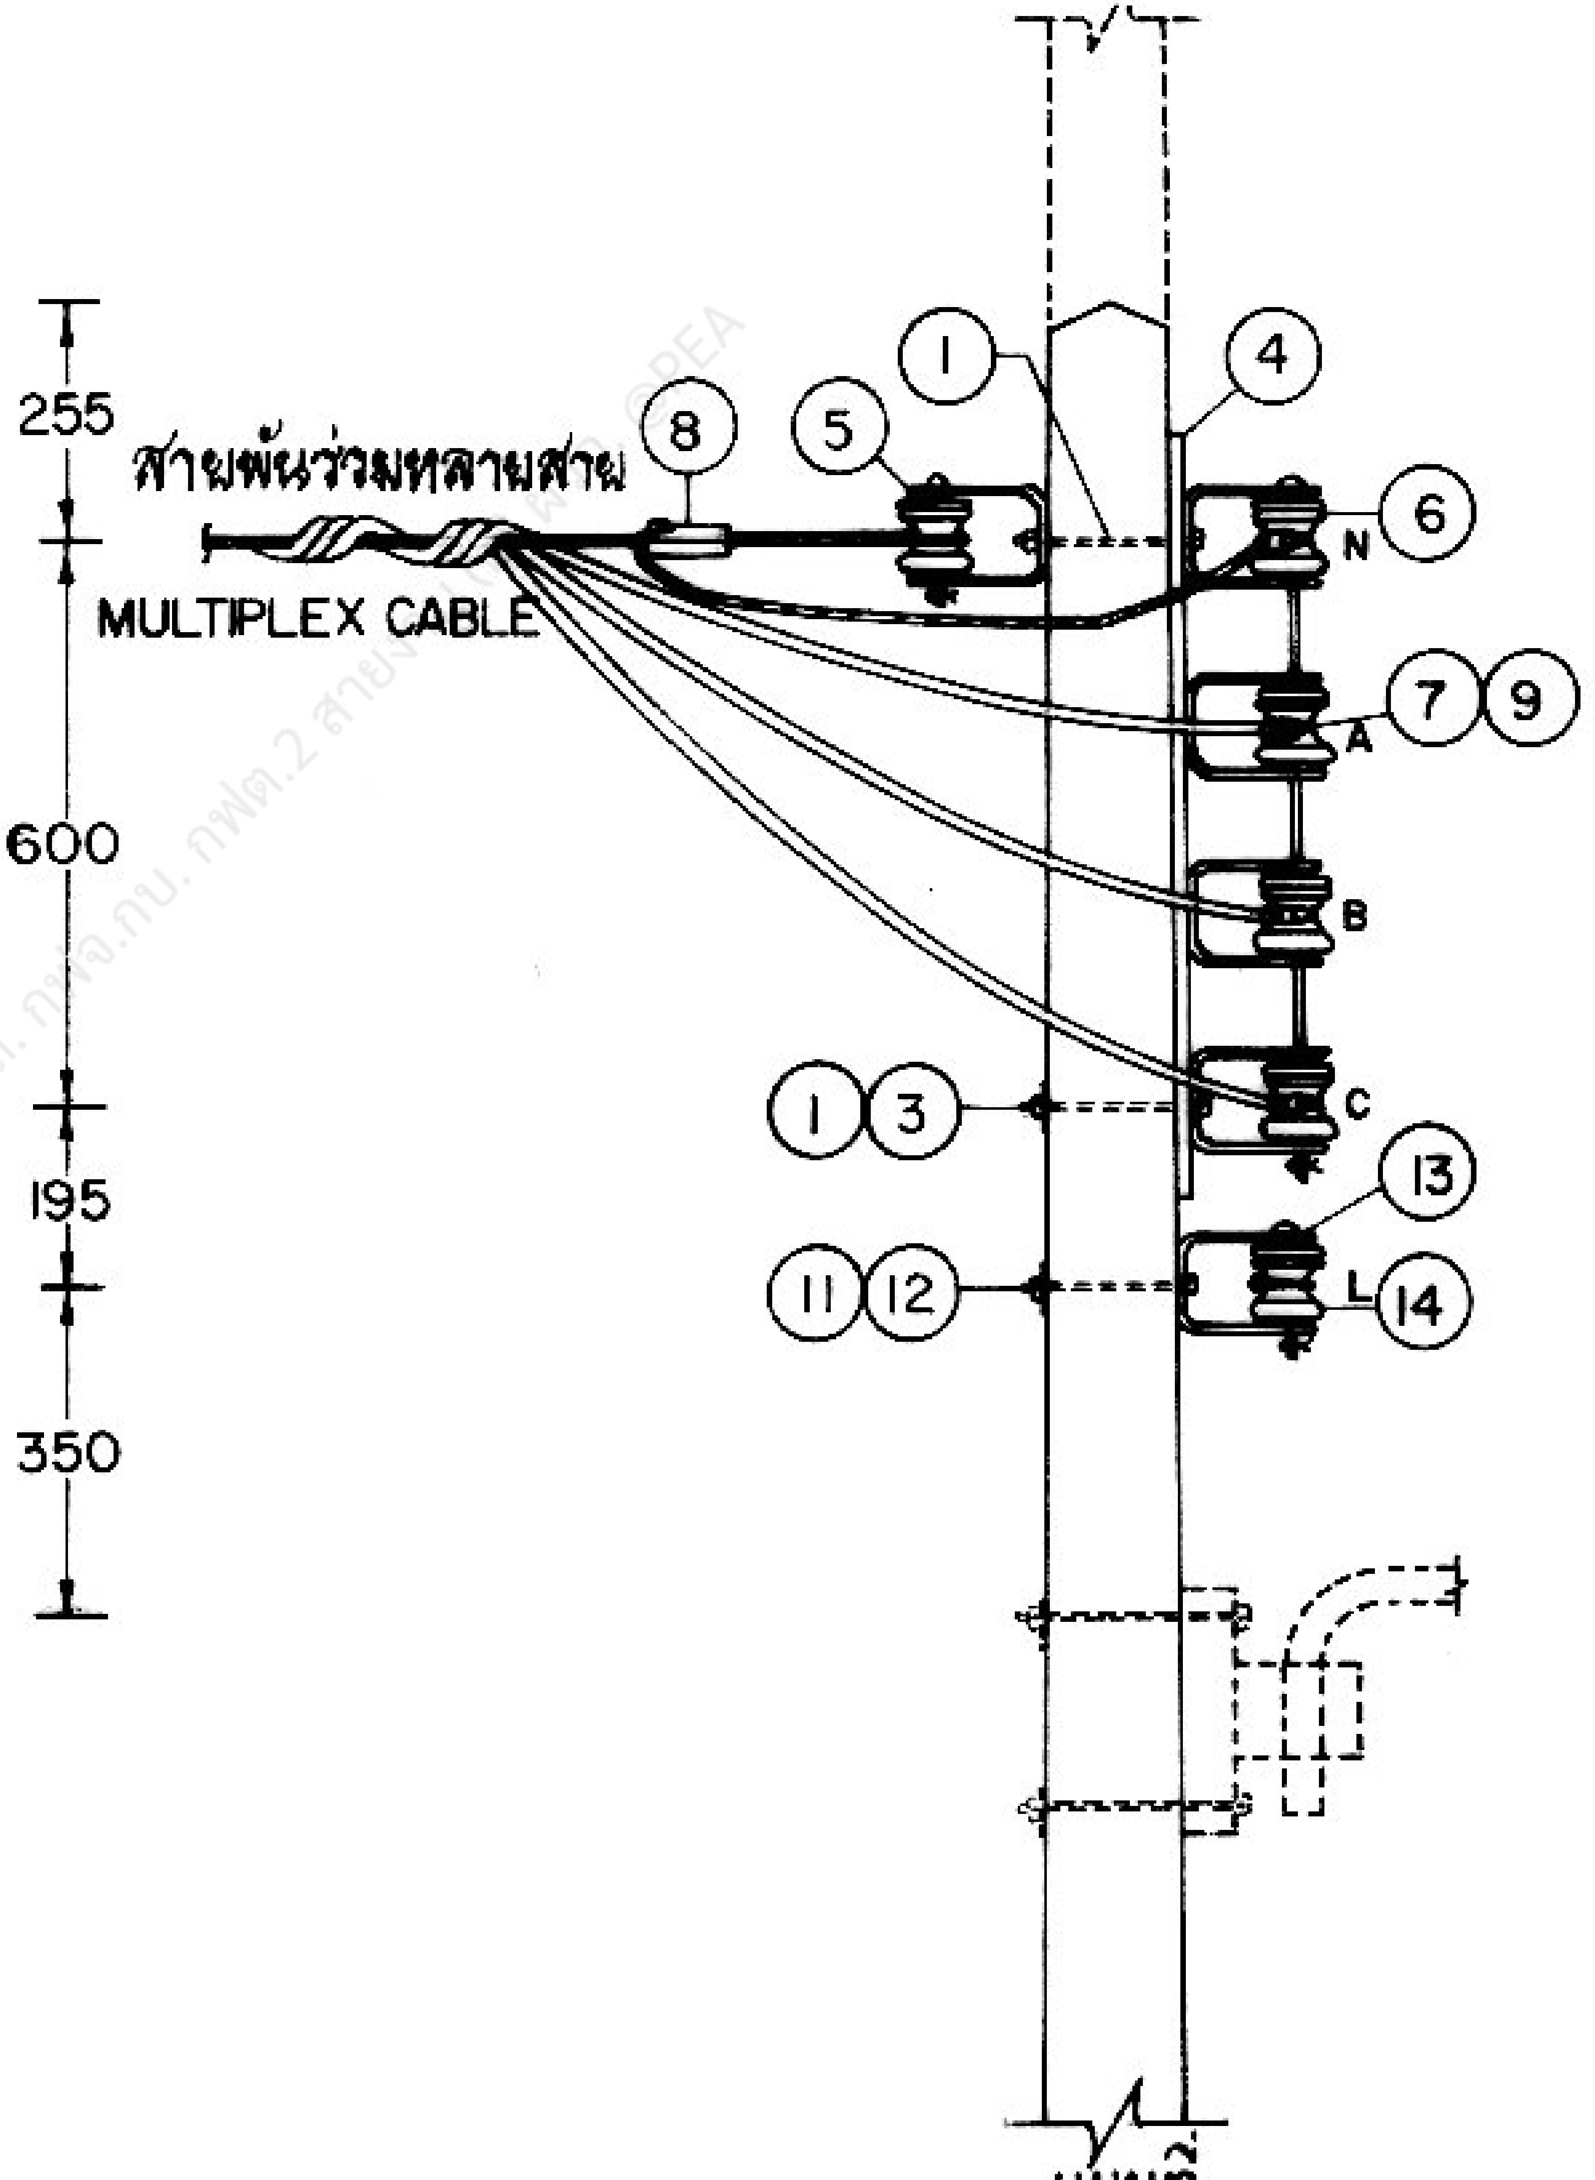

แบบที่ 3
TYPE 3

กองวิศวกรรมไฟฟ้าและเครื่องกล
ฝ่ายวิศวกรรม

ผู้เขียน [illegible]
ผู้ตรวจ
วิศวกร [illegible]
หัวหน้าแผนก [illegible]
หัวหน้ากอง [illegible]
ผู้อำนวยการฝ่าย
รองผู้ว่าการฝ่ายเทคนิค

การไฟฟ้าส่วนภูมิภาค

ผู้ว่าการ

การติดตั้งแร็คแรงต่ำกับเสาคอนกรีต 9 ม.
สำหรับการต่อแยกสาย

SECONDARY RACK INSTALLATION ON 9 m CONCRETE POLE
FOR TAP LINE

ใช้แทนแบบ
ถูกแทนโดยแบบ
เขียนเสร็จวันที่ 15 ส.ค. 21
แก้แบบวันที่
มิติเป็น มม.
มาตราส่วน 1:20
แบบเลขที่ SAI-015/21046
แผ่นที่ 2 ของจำนวน 4 แผ่น

การประกอบเลขที่ ASSEMBLY NO. 0210

บัญชีวัสดุ
BILL OF MATERIAL

ลำดับที่ ITEM	รายละเอียด DESCRIPTION	จำนวน REQUIRED 1	2	3	วัสดุเลขที่ MAT. NO.
1	สลักเกลียว M 16 X 170 มม. BOLT, MACHINE, M 16 X 170 mm	2	–	2	01110201
1a	สลักเกลียว M 16 X 250 มม. สำหรับเสาคอนกรีต 12 ม. BOLT, MACHINE, M 16 X 250 mm FOR 12 m CONCRETE POLE	2	–	2	01110203
2	สลักเกลียว M 16 X 200 มม BOLT, MACHINE, M 16X200 mm	1	4	–	01110202
2a	สลักเกลียว M 16 X 300 มม. สำหรับเสาคอนกรีต 12 ม. BOLT, MACHINE, M 16X300 mm FOR 12 m CONCRETE POLE	1	4	–	01110204
3	แหวนสี่เหลี่ยมแบน 52X52X4.5 มม. รู Ø 18 มม. มอก. 258 WASHER, SQUARE, FLAT, 52X52X4.5 mm HOLE Ø 18 mm TIS 258	2	–	1	01180100
4	แร็ค 4 X 200 มม. แบบหลังขึ้น RACK, SECONDARY, MEDIUM PRESSED STEEL, 4 X 200 mm EXT. BACK	1	2	1	03130002
5	ที่จับลูกรอก สำหรับลูกรอก มอก.227 (แบบ 53-2) CLEVIS, FLAT STEEL, FOR INSULATOR TIS 227 (CLASS 53-2)	–	–	1	03130100
6	ลูกรอกแรงต่ำ มอก. 227 แบบ ข (แบบ 53-2) INSULATOR, SPOOL TYPE, L.T. TIS 227 TYPE B (CLASS 53-2)	4	8	5	03030000
7	พีจี. คอนเนคเตอร์ สำหรับสายอะลูมิเนียม ขนาดตามต้องการ CONNECTOR, PARALLEL GROOVE, Al SIZE AS REQUIRED	4	4	4	02300102-3
8	คอนเนคเตอร์เข้าปลายสายอลูมิเนียม ขนาดตามต้องการ CONNECTOR, DEADEND, Al SIZE AS REQUIRED	1	4	1	02310000-2
9	PVC เทป กว้าง 19 มม. (ใช้ความยาว 2 ม. ต่อจุด) มอก. 386 PVC TAPE 19 mm WIDE (2 m LONG PER POINT) TIS 386				02180001 or 02180002
10	การประกอบสายยึดโยง GY-01 GUY ASSEMBLY GY-01	1	-	-	—
10a	การประกอบสายยึดโยง GY-02 สำหรับเสาคอนกรีต 12 ม. GUY ASSEMBLY GY-02 FOR 12 m CONCRETE POLE	1	-	-	—
	สำหรับการติดตั้งสายดับไฟถนน FOR STREET LIGHTING INSTALLATION				
11	สลักเกลียว M 16X170 มม. BOLT, MACHINE, M 16 X 170 mm	1	1	1	01110201
11a	สลักเกลียว M 16X 250 มม. สำหรับเสาคอนกรีต 12 ม. BOLT, MACHINE, M 16X250 mm FOR 12 m CONCRETE POLE	1	1	1	01110203
12	แหวนสี่เหลี่ยมแบน 52X52X4.5 มม. รู Ø 18 มม. มอก. 258 WASHER, SQUARE, FLAT, 52X52X4.5 mm HOLE Ø 18 mm TIS 258	1	–	1	01180100
13	ที่จับลูกรอกสำหรับลูกรอก มอก. 227 (แบบ 53-2) CLEVIS, FLAT STEEL, FOR INSULATOR TIS 227 (CLASS 53-2)	1	2	1	03130100
14	ลูกรอกแรงต่ำ มอก. 227 แบบ ข (แบบ 53-2) INSULATOR, SPOOL TYPE, L.T. TIS 227 TYPE B (CLASS 53-2)	1	2	1	03030000
15	พี.จี. คอนเนคเตอร์ สลักคู่ สำหรับสายอะลูมิเนียม 25-95 ต.มม. CONNECTOR, PARALLEL GROOVE, DOUBLE BOLT, Al 25 – 95 mm²	–	1	–	02300102

กองวิศวกรรมไฟฟ้าและเครื่องกล
ฝ่ายวิศวกรรม

ผู้เขียน
ผู้สำรวจ
วิศวกร
หัวหน้าแผนก
หัวหน้ากอง
ผู้อำนวยการฝ่าย
รองผู้ว่าการฝ่ายเทคนิค

การไฟฟ้าส่วนภูมิภาค

ผู้ว่าการ

การติดตั้งแร็คแรงต่ำกับเสาคอนกรีต 9 ม.
สำหรับการต่อแยกสาย

SECONDARY RACK INSTALLATION ON 9 m CONCRETE POLE FOR TAP LINE

ใช้แทนแบบ
ถูกแทนโดยแบบ
เขียนเสร็จวันที่ 15 สค. 21
แก้แบบวันที่
มิติเป็น
มาตราส่วน
แบบเลขที่ SAI-015/21046
แผ่นที่ 3 ของจำนวน 4 แผ่น

การประกอบเลขที่
ASSEMBLY NO. 0210

บัญชีวัสดุ
BILL OF MATERIAL

ลำดับที่ ITEM	รายละเอียด DESCRIPTION	จำนวน REQ'D 1	2	3	วัสดุเลขที่ MAT. NO.
16	คอนเนคเตอร์ เข้าปลายสายอะลูมิเนียม 25-35 ต.มม. CONNECTOR, DEADEND, Al 25-35 mm^2	-	1	-	02310000
17	PVC เทป กว้าง 19 มม. (ใช้ความยาว 2 ม. ต่อจุด) มอก. 386 PVC TAPE, 19 mm WIDE (2 m LONG PER POINT) TIS 386	-		-	02180001 or 02180002

	แบบอ้างอิง REFERENCE DRAWING	แบบเลขที่ DWG. NO.	การประกอบเลขที่ ASSEMBLY NO.
1	การประกอบคอนเนคเตอร์ และปรีฟอร์มเข้าปลายสาย สำหรับสายแรงต่ำ DEADEND CONNECTOR AND PREFORMED DEADEND ASSEMBLY, FOR L.T. LINES	SAI-015/22015	9528
2	การประกอบ พี.จี. คอนเนคเตอร์ P.G. CONNECTOR ASSEMBLY	SAI-015/21032	9558

หมายเหตุ :

1 การติดตั้งแร็คแรงต่ำกับเสาคอนกรีต 9 ม. สำหรับการต่อแยกสาย แบบที่ 4 ; ดูแบบเลขที่ SAI-015/34025 (การประกอบเลขที่ 0210 A)

2 การเข้าปลายสายแรงต่ำ สามารถเลือกใช้ลวดอะลูมิเนียมได้อีกแบบหนึ่ง ตามแบบเลขที่ SAI-015/21006 (การประกอบเลขที่ 9529)

NOTES :

1 SECONDARY RACK INSTALLATION ON 9 m CONCRETE POLE, FOR TAP LINE, TYPE 4 ; SEE DWG. NO. SAI-015/34025 (ASSEMBLY 0210 A).

2 FOR L.T. LINES DEADENDING CAN BE ALTERNATELY USED ALUMINIUM TIE WIRE AS DWG. NO. SAI-015/21006 (ASSEMBLY NO. 9529).

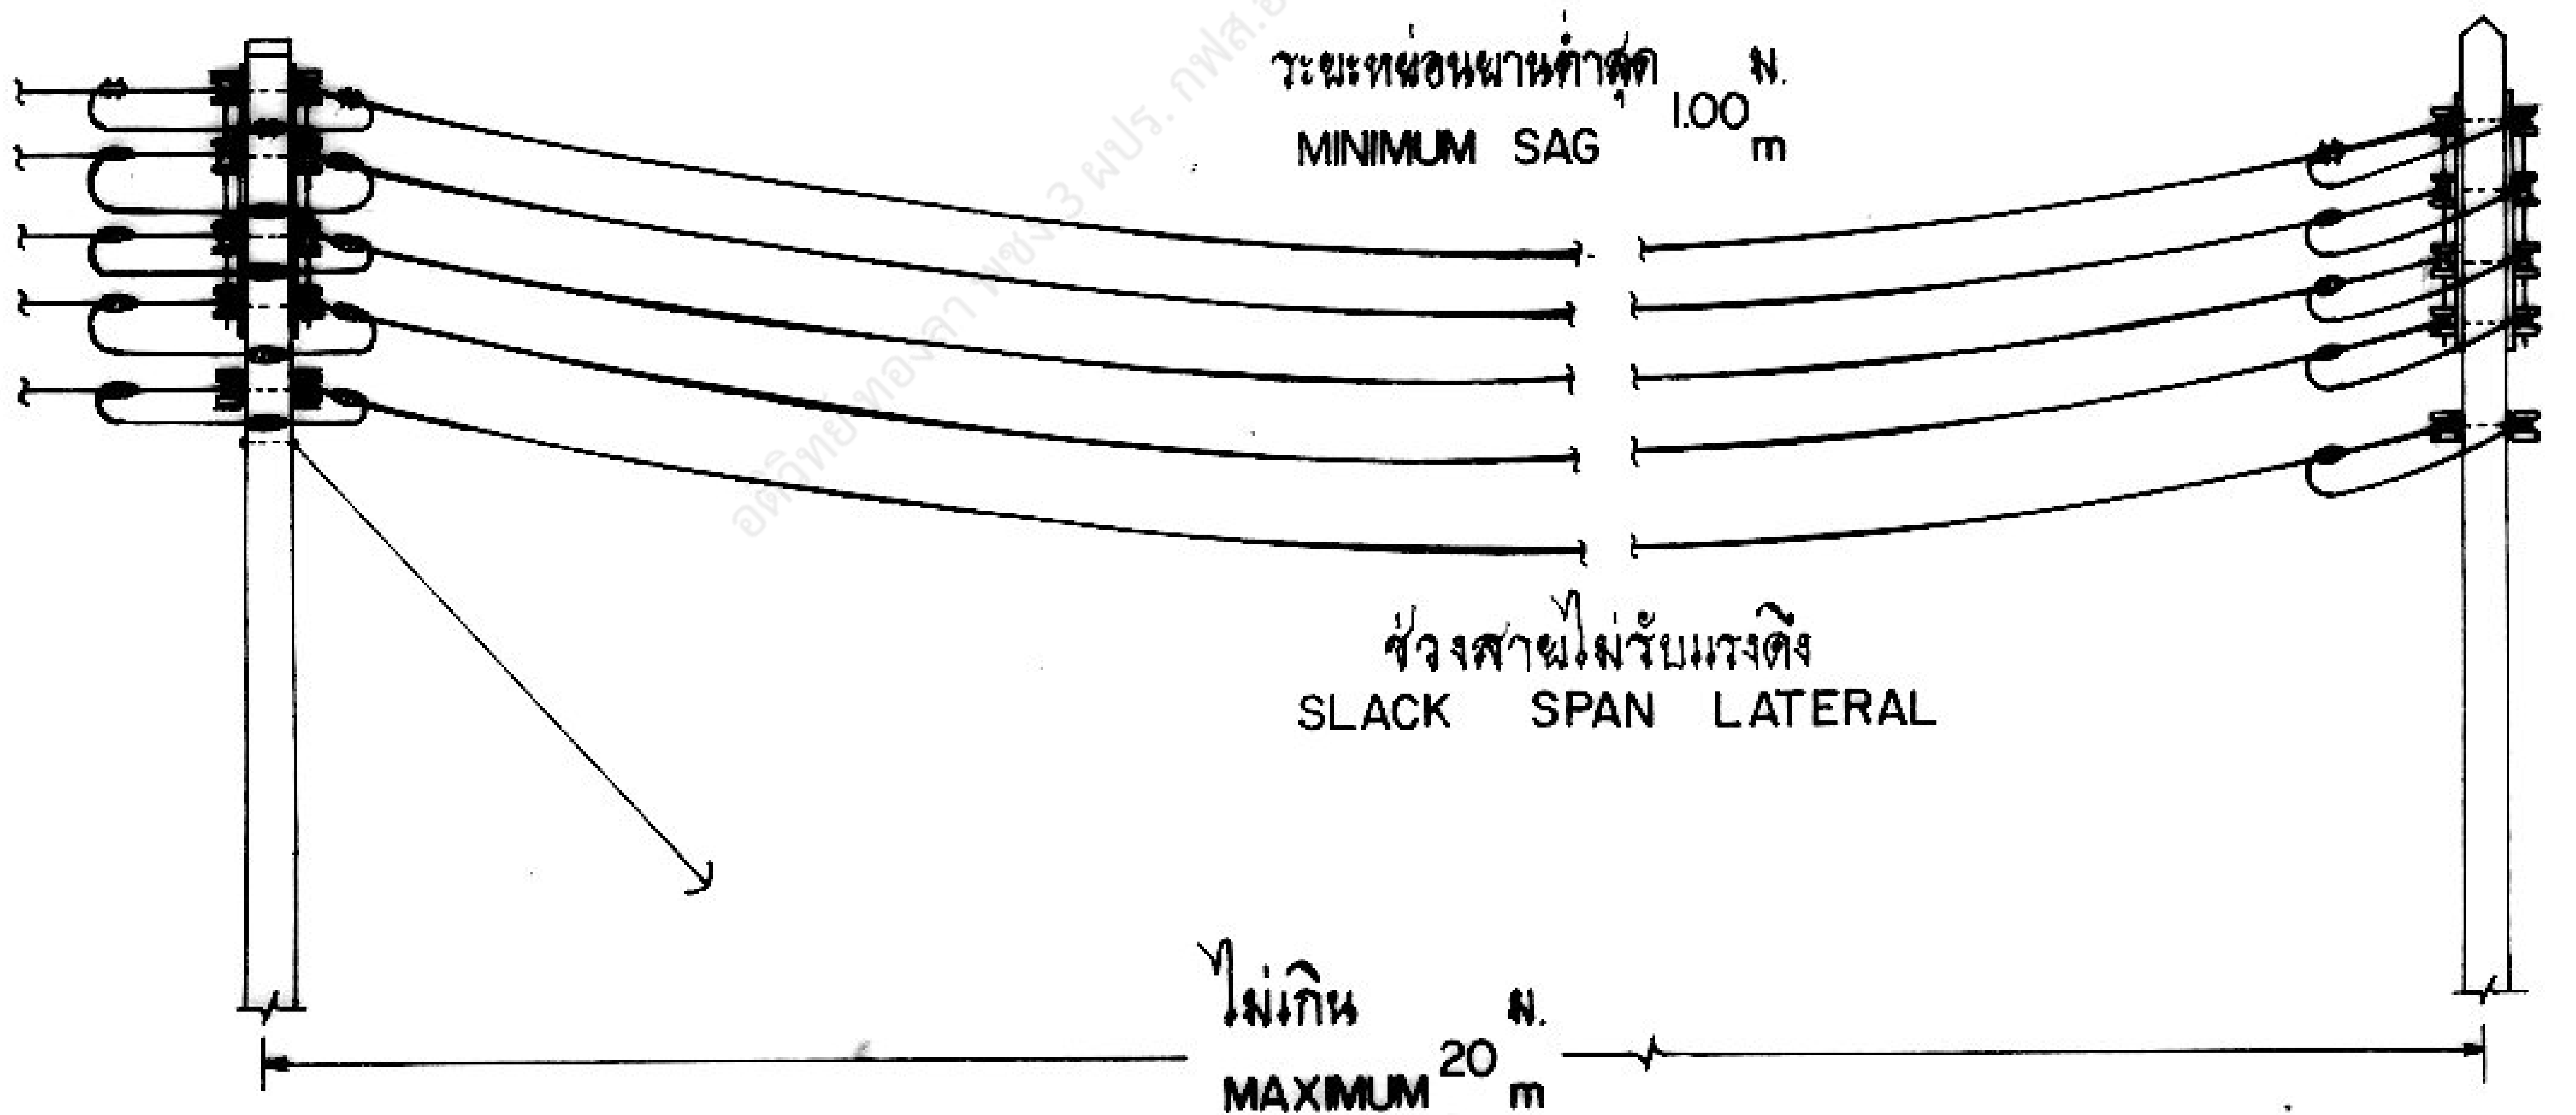

แบบแนะนำการติดตั้ง
APPLICATION STRUCTURE

กองวิศวกรรมไฟฟ้าและเครื่องกล
ฝ่ายวิศวกรรม

ผู้เขียน
ผู้สำรวจ
วิศวกร
หัวหน้าแผนก
หัวหน้ากอง
ผู้อำนวยการฝ่าย
รองผู้ว่าการฝ่ายเทคนิค

การไฟฟ้าส่วนภูมิภาค

ผู้ว่าการ

การติดตั้งแร็คแรงต่ำกับเสาคอนกรีต 9 ม.
สำหรับการต่อแยกสาย

SECONDARY RACK INSTALLATION ON 9 m CONCRETE POLE
FOR TAP LINE

ใช้แทนแบบ
ถูกแทนที่โดยแบบ
เขียนเสร็จวันที่ 15 ส.ค. 21
แก้แบบวันที่ 16 ต.ค. 34
พิมพ์เป็น
มาตราส่วน
แบบเลขที่ SAI-015/21046
แผ่นที่ 4 ของจำนวน 4 แผ่น