
* ให้ดัดโค้งสายขึ้น เพื่อป้องกันน้ำฝนไหลย้อนเข้าจุดที่ต่อปลายสาย


การประกอบเลขที่ ASSEMBLY NO. 0535

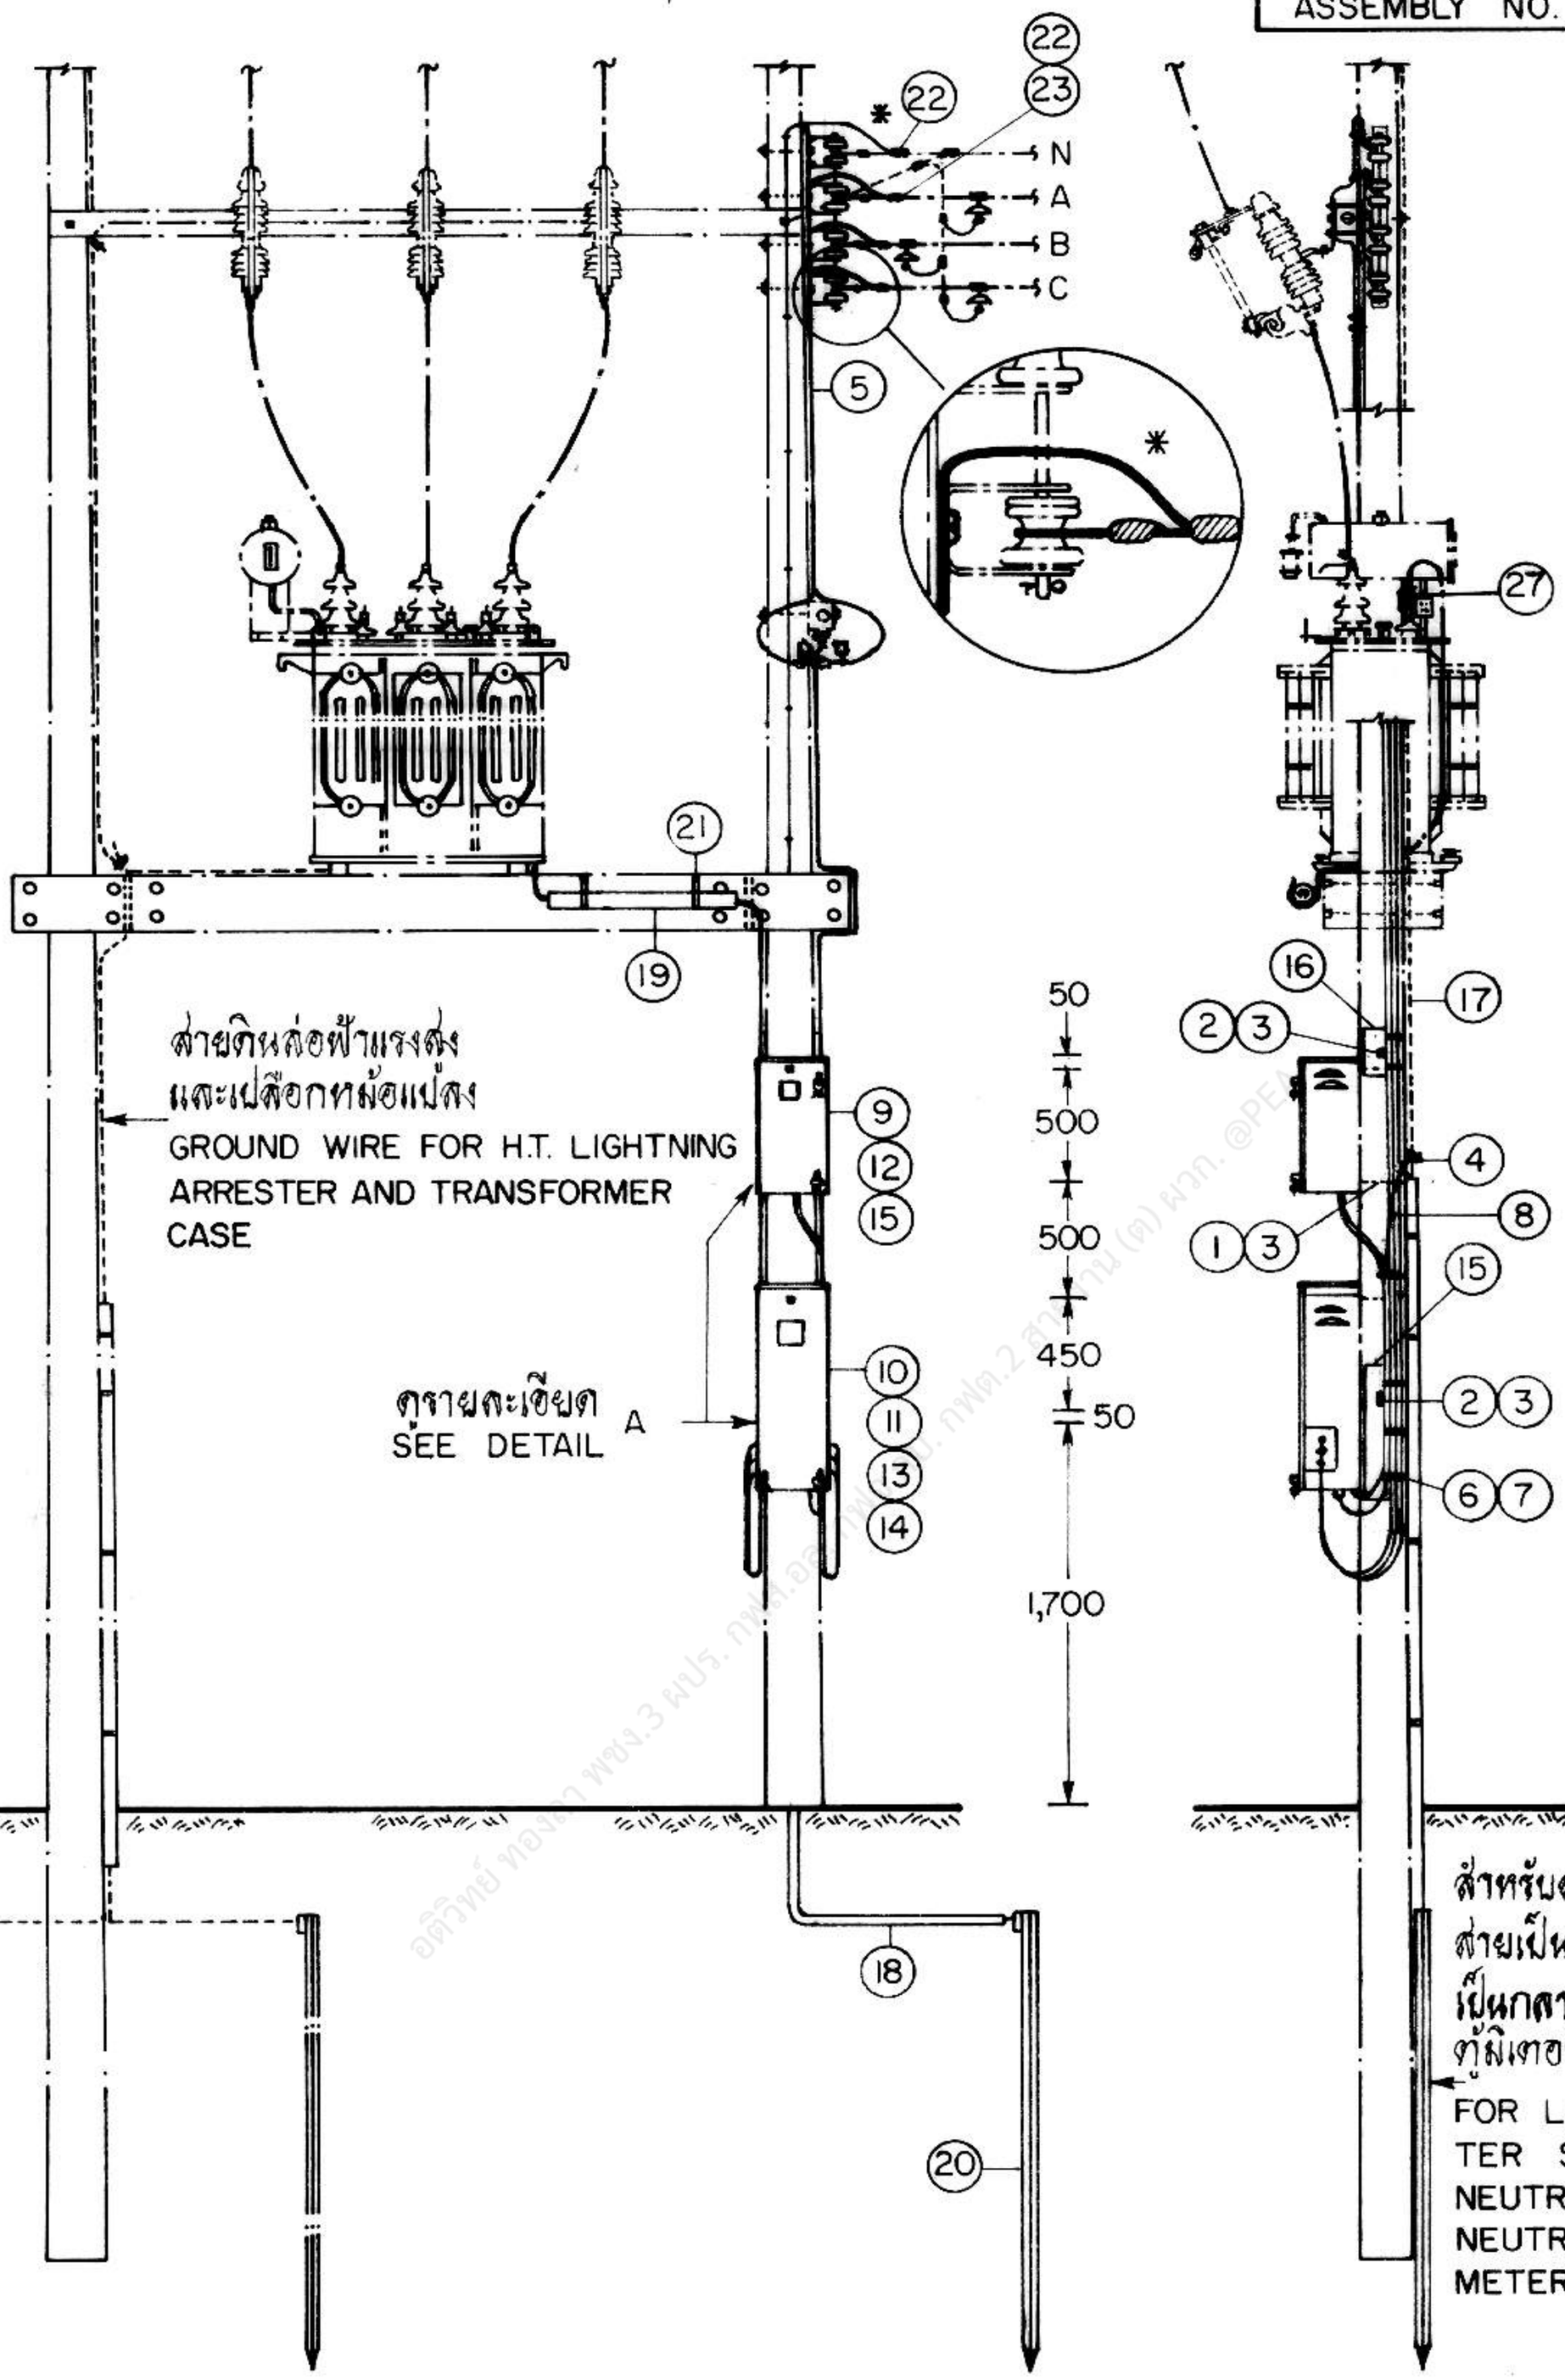



กองวิศวกรรมไฟฟ้าและเครื่องกล ฝ่ายวิศวกรรม	**การไฟฟ้าส่วนภูมิภาค**	ใช้แทนแบบ ถูกแทนโดยแบบ
ผู้เสนอ ผู้สำรวจ วิศวกร หัวหน้าแผนก ผู้อำนวยการกอง ผู้อำนวยการฝ่าย	ผู้ว่าการ การติดตั้งมิเตอร์ 3 เฟส 4 สาย แบบวัดค่า 2 อัตรา ประกอบ ซีที. แรงต่ำ I ที่เสาต้นนั่งร้านหม้อแปลง	เสนอเสร็จวันที่ 18 เม.ย. 28 แก้แบบวันที่ 8 ก.ค. 31 มิติเป็น มม. มาตราส่วน 1 : 50
รองผู้ว่าการฝ่ายเทคนิค	INSTALLATION OF 3-Ø, 4-W TWO-RATE TARIFF METER WITH L.T. CURRENT TRANSFORMERS I AT TRANSFORMER STATION	แบบเลขที่ SA1-015/28011 แผ่นที่ 1 ของจำนวน 6 แผ่น


* ให้ดัดโค้งสายขึ้น เพื่อป้องกันน้ำฝนไหลย้อนเข้าจุดที่ต่อปลายสาย


การประกอบเลขที่ ASSEMBLY NO. 0535

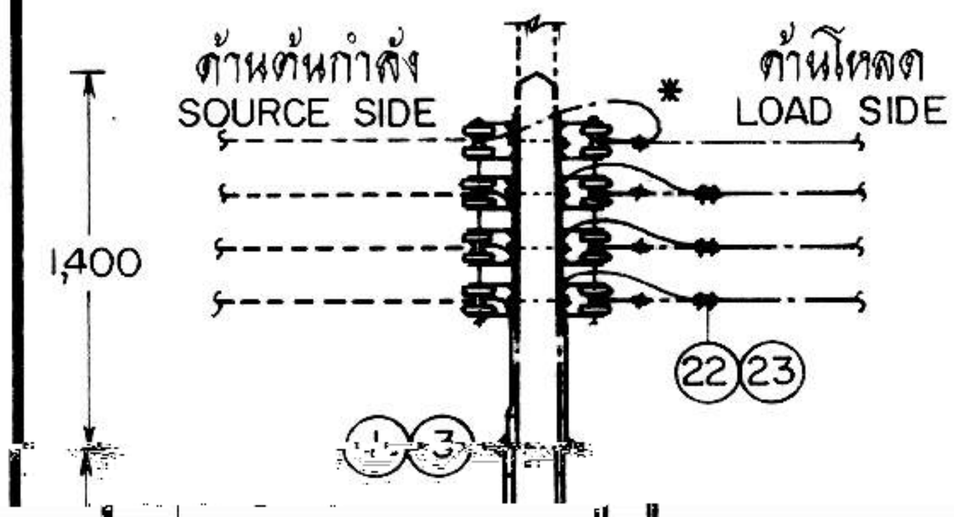

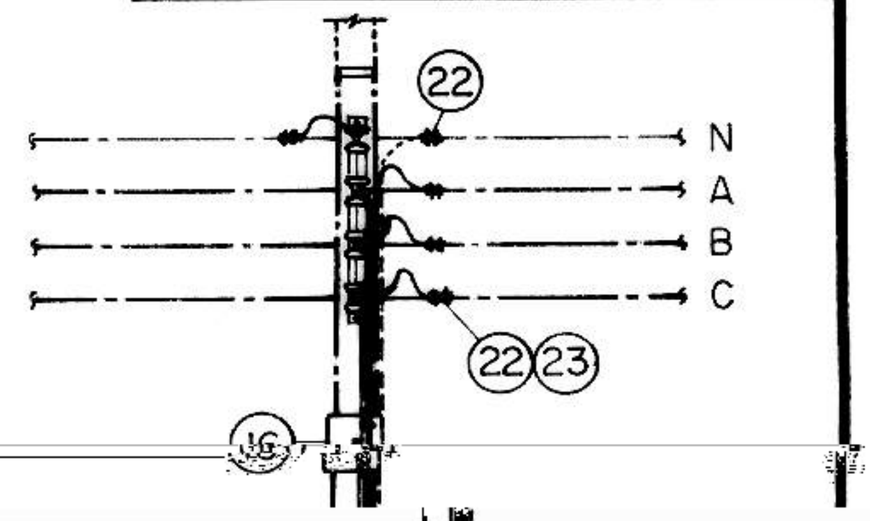

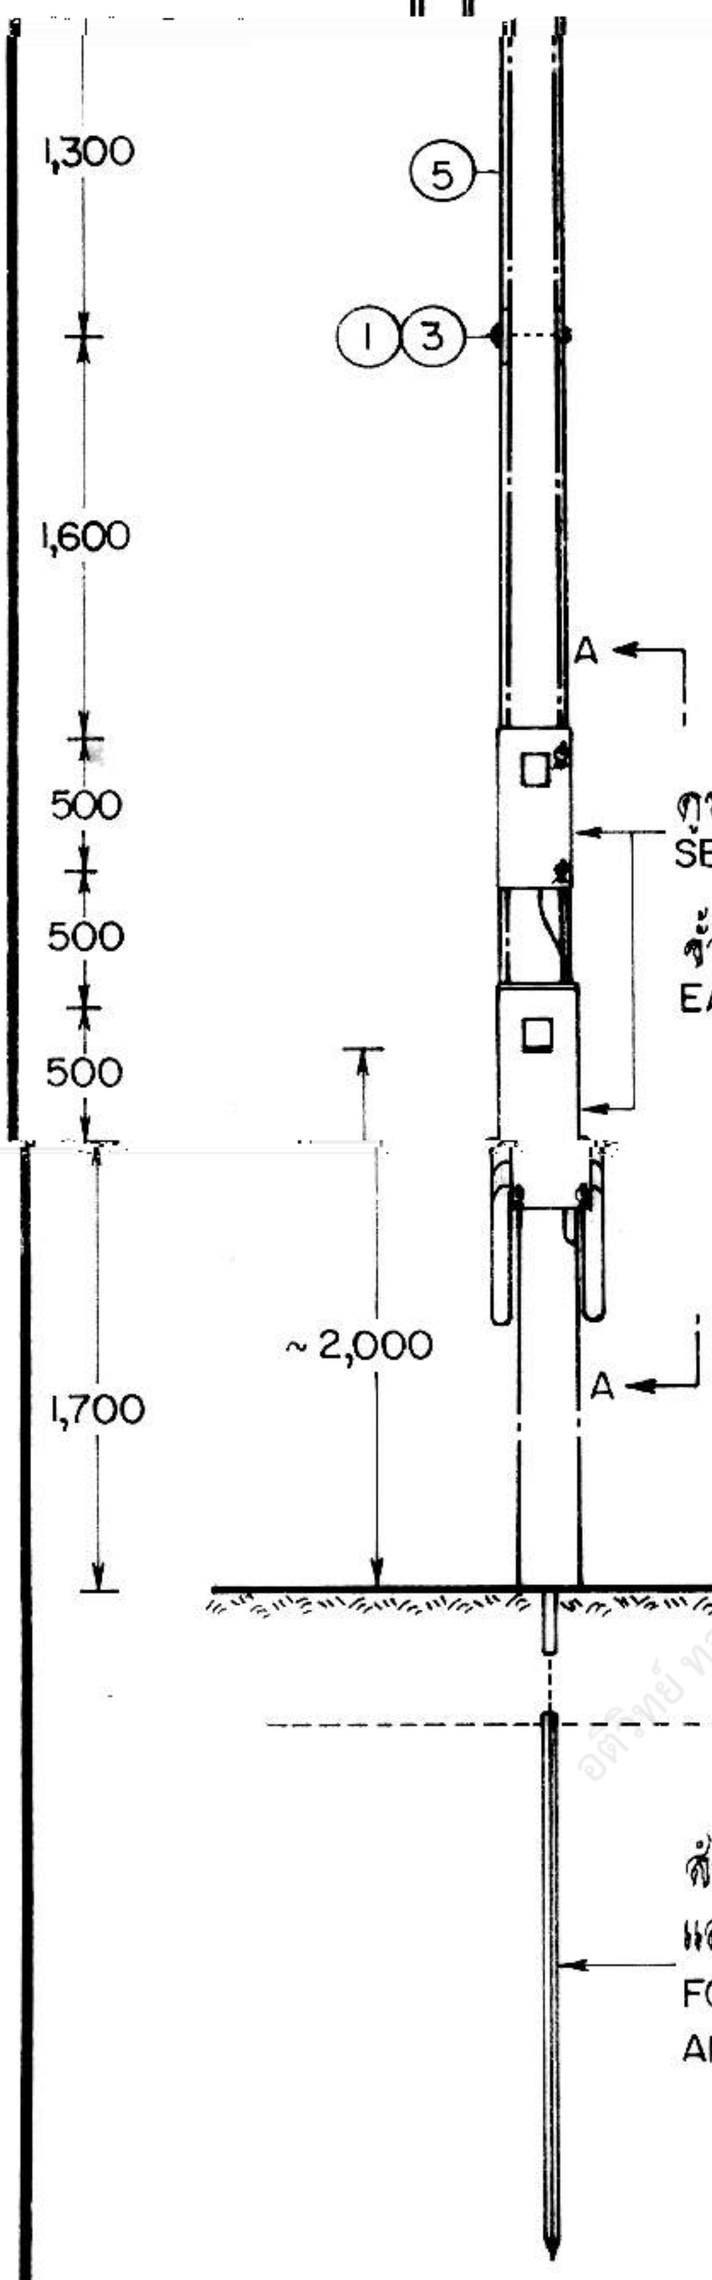

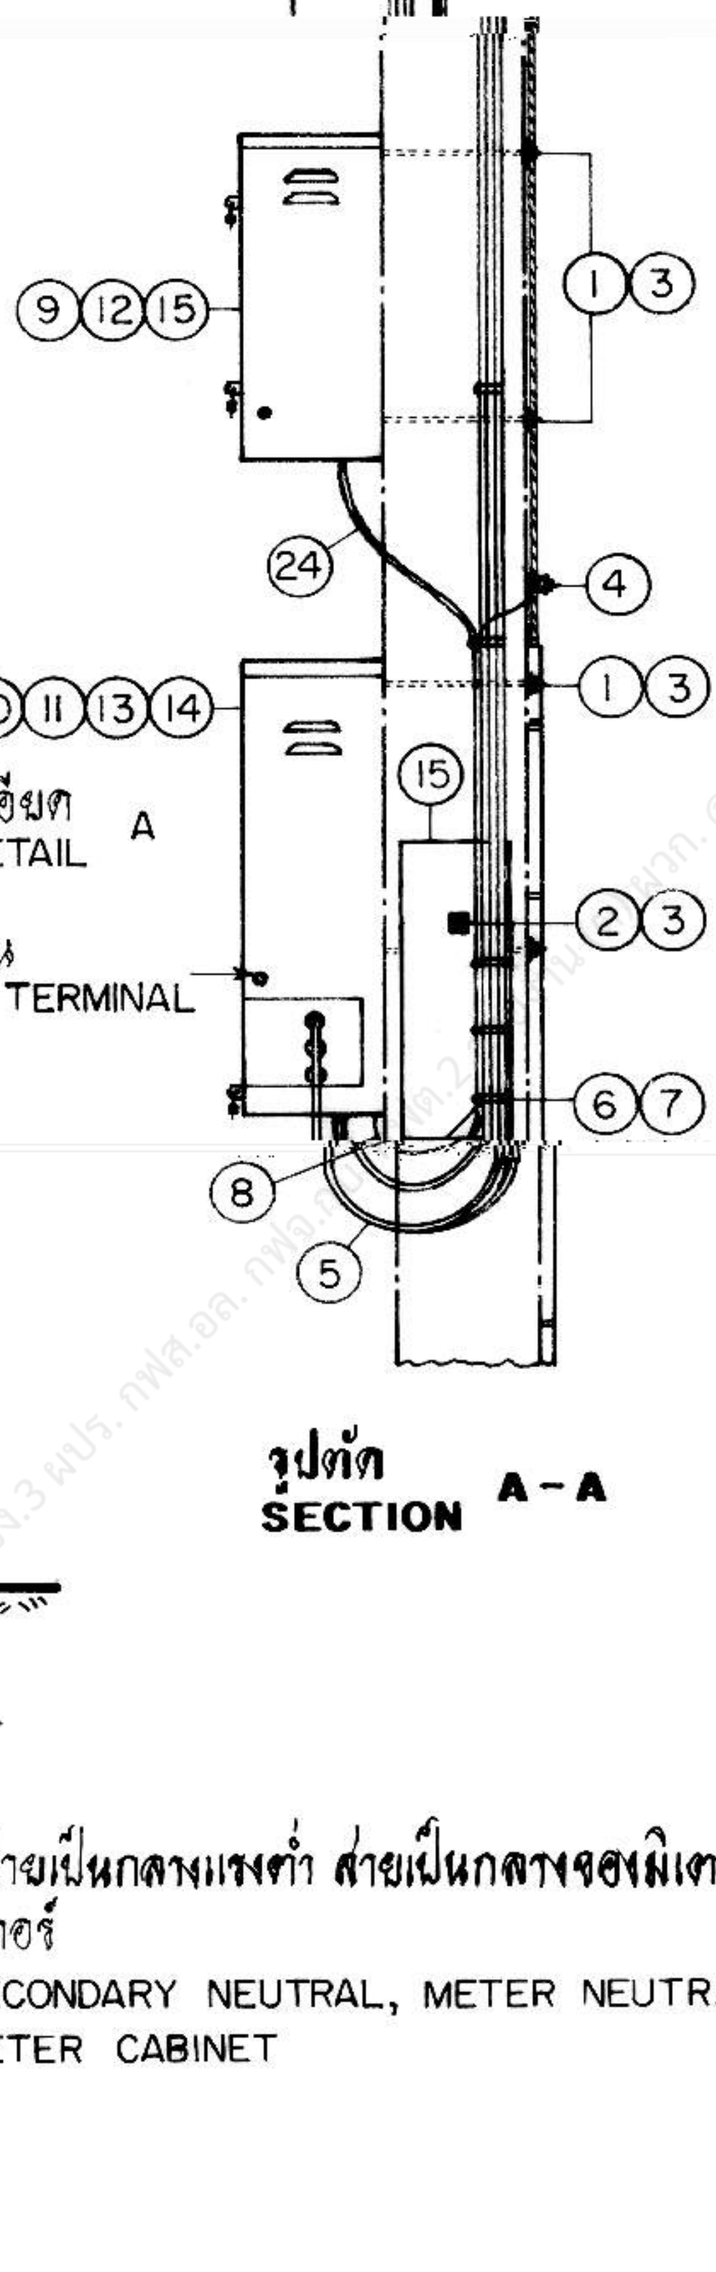

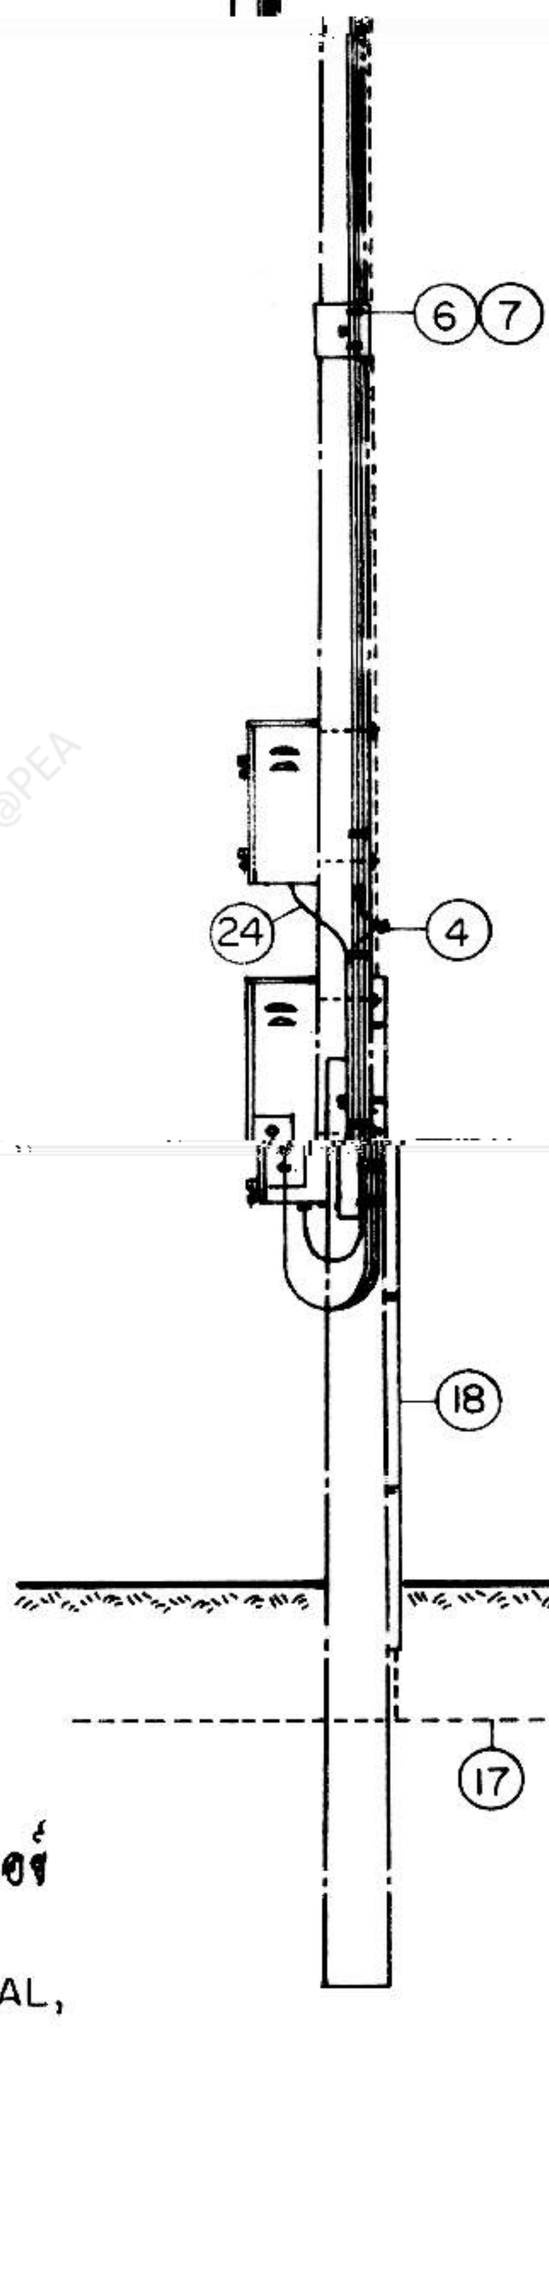


รูปตัด A-A
SECTION A-A

สำหรับสายเป็นกลางแรงต่ำ สายเป็นกลางของมิเตอร์ และตู้มิเตอร์
FOR SECONDARY NEUTRAL, METER NEUTRAL, AND METER CABINET


กองวิศวกรรมไฟฟ้าและเครื่องกล ฝ่ายวิศวกรรม	การไฟฟ้าส่วนภูมิภาค	ใช้แทนแบบ ถูกแทนโดยแบบ เขียนเสร็จวันที่ 18 เม.ย. 28 แก้แบบวันที่ 8 ก.ค. 31 มิติเป็น มม. มาตราส่วน 1 : 50
ผู้เขียน ผู้สำรวจ วิศวกร หัวหน้าแผนก ผู้อำนวยการกอง ผู้อำนวยการฝ่าย	ผู้ว่าการ	
ของผู้ว่าการฝ่ายเทคนิค	การติดตั้งมิเตอร์ 3 เฟส 4 สาย แบบวัดค่า 2 อัตรา ประกอบซี.ที. แรงต่ำ II ที่เสาระบบจำหน่ายแรงต่ำ INSTALLATION OF 3-Ø, 4-W TWO-RATE TARIFF METER WITH L.T. CURRENT TRANSFORMERS II AT L.T. DISTRIBUTION POLE	แผนเลขที่ SAI-015/28011 แผ่นที่ 2 ของจำนวน 6 แผ่น

* ทำความสะอาดสาย และทาคอมเปาด์ช่วยสัมผัสทางไฟฟ้า พันสายแยกรอยสายเมน แล้วรัดด้วยเข็มขัดรัดท่อแบบเกลียวตัวหนอน และพันหุ้มจุดต่อด้วย PVC เทป

การประกอบเลขที่ ASSEMBLY NO. 0535

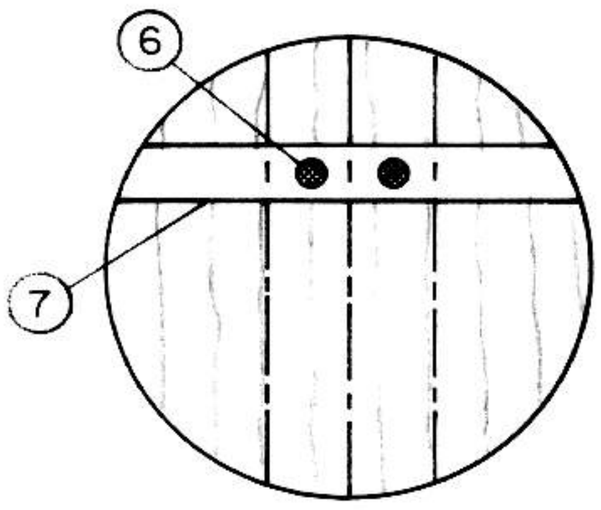

รายละเอียด DETAIL B

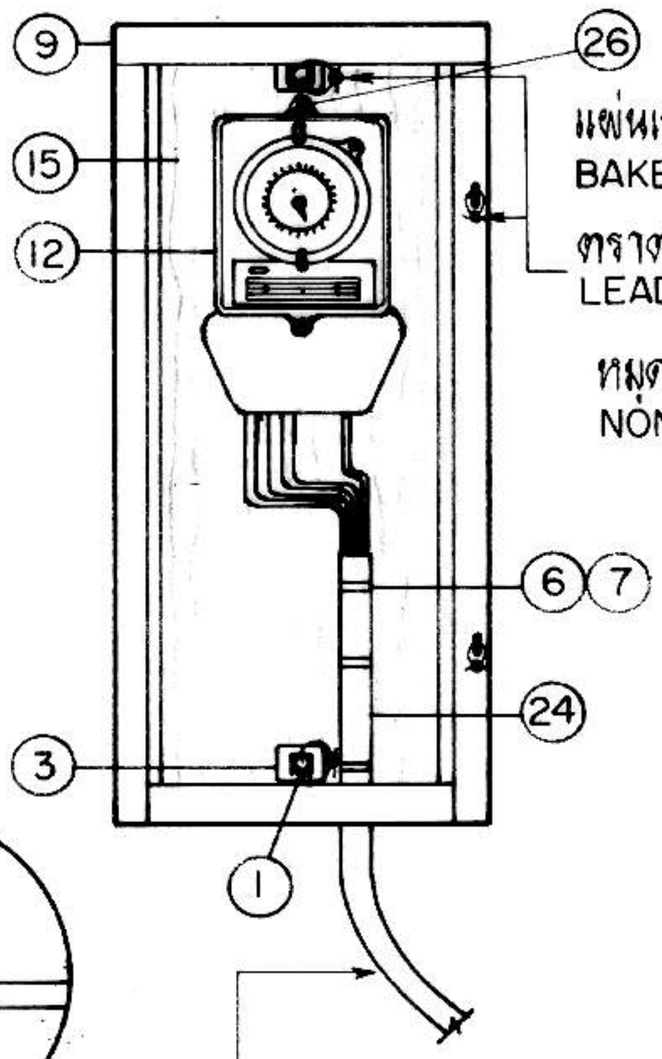


แผ่นเบ็คเกอร์ไลท์ BAKELITE 50X50X8 มม. mm

ตราตะกั่ว LEAD MARK

รู HOLE Ø 24


หมุดย้ำแบบไม่เป็นสนิม NON-FERROUS RIVET

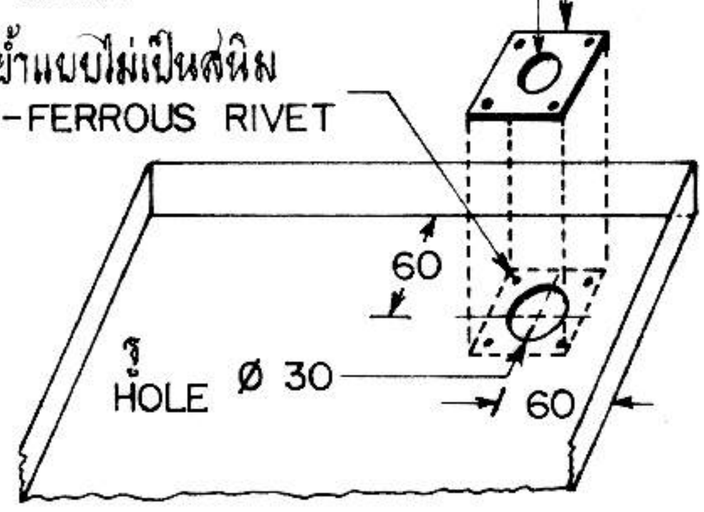


รายละเอียด DETAIL D

ไปต่อกับกิโลวัตต์-ชั่วโมงมิเตอร์ TO BE CONNECTED WITH kwh-METER


เส้นสายอะลูมิเนียม AI COND. WIRE

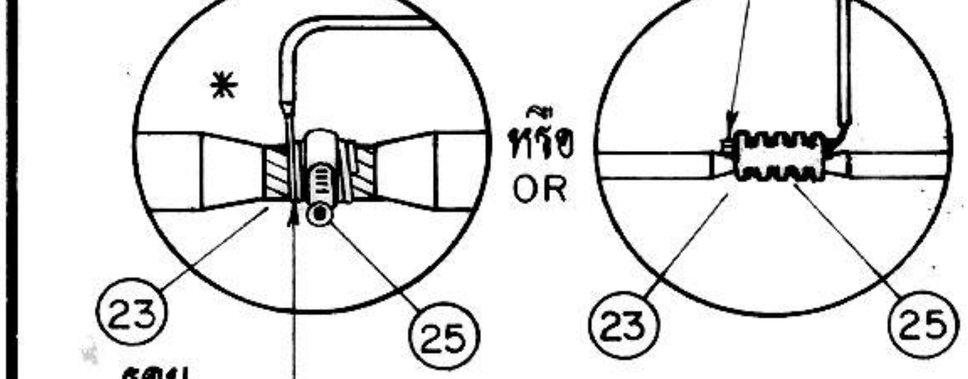

รายละเอียด DETAIL C

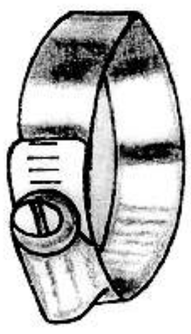

เข็มขัดรัดท่อแบบเกลียวตัวหนอน
WORM DRIVE HOSE CLAMP

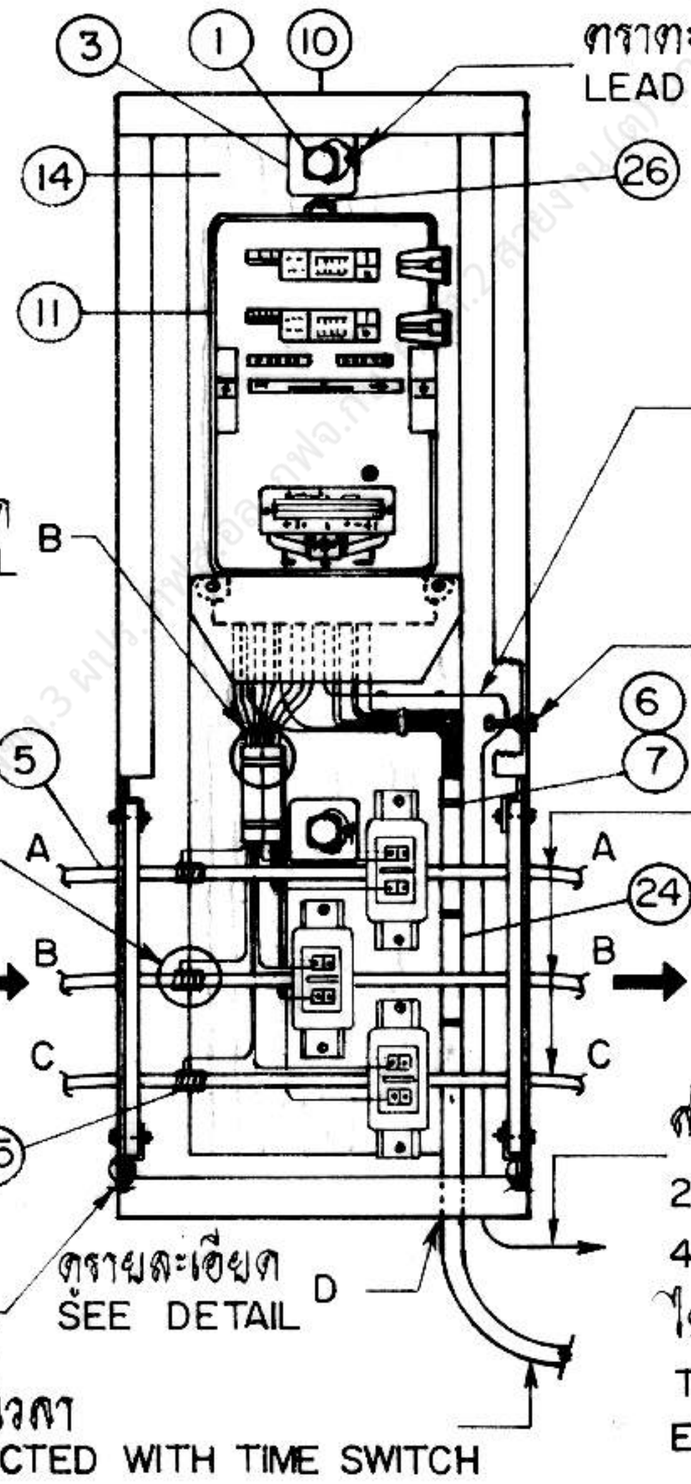

ตราตะกั่ว LEAD MARK

ดูรายละเอียด SEE DETAIL B

ดูรายละเอียด SEE DETAIL C

ด้านต้นกำลัง SOURCE SIDE

ด้านโหลด LOAD SIDE

สายทองแดงหุ้มฉนวน 2.5 ต.มม. (คอนโทรลเคเบิล) $2.5\ mm^2$ Cu INSULATED CABLE (CONTROL CABLE)

ขั้วยึดสายดิน GROUND TERMINAL

สายประธานแรงต่ำ SERVICE ENTRANCE

สายทองแดงหุ้มฉนวนขนาด 4 ต.มม. หรือ 2X2.5 ต.มม.(คอนโทรลเคเบิล 7X2.5 ต.มม.) 4 OR $2X2.5\ mm^2$ Cu INSULATED CABLE

ไปต่อลงดินร่วมกับสายเป็นกลางแรงต่ำ TO BE CONNECTED WITH SERVICE ENTRANCE NEUTRAL

รายละเอียด DETAIL A

ดูรายละเอียด SEE DETAIL D

ตราตะกั่ว LEAD MARK

ไปต่อกับสวิตช์เวลา TO BE CONNECTED WITH TIME SWITCH

กองวิศวกรรมไฟฟ้าและเครื่องกล ฝ่ายวิศวกรรม	# การไฟฟ้าส่วนภูมิภาค	ใช้แทนแบบ ถูกแทนโดยแบบ
ผู้เสนอ ผู้สำรวจ วิศวกร หัวหน้าแผนก ผู้อำนวยการกอง ผู้อำนวยการฝ่าย	ผู้ว่าการ 8 ก.ค. 28	เสนอเสร็จวันที่ 18 เม.ย. 28 แก้แบบวันที่ 8 ก.ค. 31 มิติเป็น มม. มาตราส่วน
ของผู้ว่าการฝ่ายเทคนิค	การติดตั้งมิเตอร์3 เฟส 4สาย แบบวัดค่า 2 อัตรา ประกอบซี.ที.แรงต่ำ INSTALLATION OF 3-Ø, 4-W TWO-RATE TARIFF METER WITH L.T. CURRENT TRANSFORMERS	แบบเลขที่ SAI-015/28011 แผ่นที่ 3 ของจำนวน 6 แผ่น

การประกอบเลขที่ ASSEMBLY NO. 0535

บัญชีวัสดุ
BILL OF MATERIAL

ลำดับที่ ITEM	รายละเอียด DESCRIPTION	จำนวน REQ'D I	จำนวน REQ'D II	วัสดุเลขที่ MAT. NO.
1	สลักเกลียว M 16 X 250 มม. BOLT, MACHINE, M 16 X 250 mm	–	6	01110203
	สลักเกลียว M 16 X 300 มม. สำหรับเสาคอนกรีต 12 ม. BOLT, MACHINE, M 16 X 300 mm FOR 12 m CONCRETE POLE	4	6	01110204
2	สลักเกลียว M 16 X 250 มม. BOLT, MACHINE, M 16 X 250 mm	–	1	01110203
	สลักเกลียว M 16 X 350 มม. สำหรับเสาคอนกรีต 12 ม. BOLT, MACHINE, M 16 X 350 mm FOR 12 m CONCRETE POLE	2	1	01110205
3	แหวนสี่เหลี่ยมแบน 52 X 52 X 4.5 มม. รู Ø 18 มม. มอก. 258 WASHER, SQUARE, FLAT 52 X 52 X 4.5 mm HOLE Ø 18 mm TIS 258	12	14	01180100
4	ยูแคล้มป์ สลักเดียว M 8 CLAMP, SINGLE U-BOLT, M 8	1	1	01230000
5	สายอะลูมิเนียม หรือทองแดงหุ้ม PVC 750 โวลต์ ขนาดตามต้องการ CABLE, Al OR Cu, PVC INSULATED, 750 V, SIZE AS REQUIRED	55 ม. m	35 ม. m	02070002-8
6	ตะปูหัวกลมแบน ยาว 15-20 มม. Ø 1.00 มม. มอก. 113 NAIL, ROUND MILD STEEL WIRE 15-20 mm LONG Ø 1.00 mm TIS 113	30	38	
7	เข็มขัดรัดสาย (ทำด้วยลวดอะลูมิเนียมแบน 1 X 10 มม.) ช่วงระยะ 50 ซม. CABLE STRAP (MADE OF ARMOUR TAPE 1 X 10 mm) AT 50 cm INTERVAL	กก. kg	กก. kg	02200000
8	สายทองแดงหุ้มฉนวนใช้ภายนอก ขนาด 4 ต.มม. หรือ 2 X 2.5 ต.มม. (คอนโทรลเคเบิล) CONDUCTOR, INSULATED, WEATHER-PROOF Cu 4 mm^2 OR 2 X 2.5 mm^2 (CONTROL CABLE)	ม. m	ม. m	
9	ตู้สำหรับดีมานด์มิเตอร์ CABINET, ALUMINIUM, FOR DEMAND METER	1	1	06100007
10	ตู้สำหรับมิเตอร์ พร้อมซีที.แรงต่ำ CABINET, STEEL, FOR WATTHOUR METER WITH L.T.-CURRENT TRANSFORMER	1	1	06100008
11	กิโลวัตต์-ชั่วโมงมิเตอร์ แบบวัดค่า 2 อัตรา 3 เฟส 4 สาย 380/220 โวลต์ 5 แอมป์ TWO-RATE TARIFF kwh-METER, 3-PHASE, 4-WIRE, 380/220 V, 5 A	1	1	
12	สวิตช์เวลา สำหรับกิโลวัตต์-ชั่วโมงมิเตอร์ แบบวัดค่า 2 อัตรา TIME SWITCH, FOR TWO-RATE TARIFF kwh-METER	1	1	
13	ซีที.แรงต่ำ 500 โวลต์ เรโชตามต้องการ RATIO 0.5, 5 VA TRANSFORMER, CURRENT, L.T. 500 V RATIO AS REQUIRED CLASS 0.5, 5 VA	3	3	06030000-5
14	แป้นไม้รองรับมิเตอร์ ไสแล้ว ขนาด 80 X 20 X 2 ซม. METER PLATE (HARD WOOD) SURFACE FINISHED, SIZE 80 X 20 X 2 cm	1	1	
15	แป้นไม้รองรับมิเตอร์ ไสแล้ว ขนาด 60 X 20 X 2 ซม. METER PLATE (HARD WOOD) SURFACE FINISHED, SIZE 60 X 20 X 2 cm	3	3	
16	แป้นไม้ยึดสายไฟฟ้า ไสแล้ว ขนาด 20 X 20 X 2 ซม. CABLE PLATE (HARD WOOD) SURFACE FINISHED, SIZE 20 X 20 X 2 cm	2	4	
17	ลวดเหล็กตีเกลียว 50/7 ต.มม. มอก. 404 WIRE, STEEL STRANDED 50/7 mm^2 TIS 404	9 ม. m	17 ม. m	01100004
18	ท่อ PVC แข็ง ขนาด Ø 20 X 4,000 มม. พร้อมอุปกรณ์ยึด CONDUIT, PVC, RIGID, Ø 20 X 4,000 mm WITH FIXING ACCESSORIES	1	1	08040002

กองวิศวกรรมไฟฟ้าและเครื่องกล
ฝ่ายวิศวกรรม

ผู้เขียน
ผู้สำรวจ
วิศวกร
หัวหน้าแผนก
ผู้อำนวยการกอง
ผู้อำนวยการฝ่าย

รองผู้ว่าการฝ่ายเทคนิค

การไฟฟ้าส่วนภูมิภาค

ผู้ว่าการ 8 ก.ค. 28

การติดตั้งมิเตอร์ 3 เฟส 4 สาย แบบวัดค่า 2 อัตรา
ประกอบซีที.แรงต่ำ

INSTALLATION OF 3-Ø, 4-W TWO-RATE TARIFF METER
WITH L.T. CURRENT TRANSFORMERS

ใช้แทนแบบ
ถูกแทนโดยแบบ
เสียนเสร็จวันที่ 18 เม.ย. 28
แก้แบบวันที่
มิติเป็น
มาตราส่วน

แบบเลขที่ SAI-015/28011
แผ่นที่ 4 ของจำนวน 6 แผ่น

การประกอบเลขที่ ASSEMBLY NO.	0535

บัญชีวัสดุ
BILL OF MATERIAL

ลำดับที่ ITEM	รายละเอียด DESCRIPTION	จำนวน REQ'D I	จำนวน REQ'D II	วัสดุเลขที่ MAT. NO.
19	ท่อ PVC แข็ง ขนาด Ø 65 X 800 มม. มอก. 216 CONDUIT, PVC, RIGID Ø 65 X 800 mm TIS 216	1	–	
20	**หลักดิน** 60 X 60 X 5 มม. ยาว 2 ม. ROD, GROUND 60 X 60 X 5 mm, 2 m LONG	1	1	01220002
21	เหล็กแขวนท่อ PVC (เหล็กแบน 30 X 4 มม. มอก. 55) STEEL BRACKET (FLAT IRON 30 X 4 mm TIS 55)	2	–	05100002
22	พี.จี. คอนเนคเตอร์ หรือ คอนเนคเตอร์ ชนิดบีบ แบบ H สำหรับสายอะลูมิเนียมหรือทองแดงขนาดตามต้องการ CONNECTOR, PARALLEL GROOVE OR H-TYPE COMPRESSION, Al OR Cu SIZE AS REQ'D	4	8	02300101-3 02320003
23	ท่อ PVC แข็ง ขนาด Ø 20 X 2,500 – 4,000 มม. พร้อมอุปกรณ์ยึด CONDUIT, PVC RIGID, Ø 20 X 2,500 – 4,000 mm, COMP. WITH FIXING ACCESS			08040002 or 08040001
24	คอนโทรลเคเบิล ขนาด 7 X 2.5 ต.มม. CONTROL CABLE, SIZE 7 X 2.5 mm^2	5 ม. m	5 ม. m	02080402
25	เข็มขัดรัดท่อ แบบเกลียวต้วหนอน ขนาด 1/2" – 1" หรือ คอนเนคเตอร์ชนิดบีบ แบบ H CLAMP, WORM DRIVE HOSE SIZE Ø 1/2" – 1" OR H-TYPE COMPRESSION CONNECTOR	3	3	02210001 02210003
26	ตะปูเกลียวชุบโครเมียม ขนาด 15 – 20 มม. SCREW, CHROME PLATED, SIZE 15 – 20 mm	12	12	
27	เทปพันเคเบิลอากาศแรงสูง ขนาด 3/4" X 30' ELECTRICAL SPLICING TAPE, FOR H.T. AERIAL CABLE, SIZE 3/4" X 30'	ม้วน roll	–	02180003

แบบอ้างอิง REFERENCE DRAWING		แบบเลขที่ DWG. NO.	การประกอบเลขที่ ASSEMBLY NO.
1	การติดตั้งฟิวส์สวิตช์แรงต่ำบนคอน คอนกอร. สปัน 100 X 100 X 2,500 มม. L.T. FUSE-SWITCH INSTALL. ON SPUN PRESTRESSED CONCRETE CROSSARM	SAI-015/25004	0407
2	แผนผังแสดงการต่อมิเตอร์ 3 เฟส 4 สาย แบบวัดค่า 2 อัตรา ประกอบซีที. แรงต่ำ CONNECTION DIAGRAM OF 3-Ø, 4-W TWO-RATE TARIFF METER WITH L.T. – CT. TRANSFORMER	SAI-015/28006	0534
3	วิธีการอ่าน และหาค่า กิโลวัตต์ ชั่วโมง และดีมานด์สูงสุด METHOD OF KILOWATT-HOUR AND MAXIMUM DEMAND READING	SAI-015/25001	0529
4	ขนาดของสายไฟฟ้าแรงต่ำที่ออกจากหม้อแปลง แผ่นที่ 6 และ 7 THE SIZE OF L.T. CABLE FROM TRANSFORMER, SHEET NO. 6 AND 7	SAI-015/22034	0601
5	การกำหนดขนาด HRC ฟิวส์ แรงต่ำ สำหรับหม้อแปลง แผ่นที่ 3 และ 4 THE RATING OF L.T. HRC FUSE FOR TRANSFORMER, SHEET NO. 3 AND 4	SOI-015/18006	0602
6	การต่อสายแรงต่ำออกจากหม้อแปลง ที่นั่งร้านหม้อแปลง คาน คอร. L.T. WIRING FROM TRANSFORMER AT PRESTRESSED CONCRETE PLATFORM	SAI-015/21007	0604
7	การต่อลงดิน ระบบแรงสูง และแรงต่ำ แผ่นที่ 2 และ 4 H.T. AND L.T. EARTHING SYSTEM, SHEET NO. 2 AND 4	SO2-015/20039	9701
8	การประกอบสายลงดิน วิธียึดลวดเหล็ก GROUND LEAD ASSEMBLY, STEEL WIRE FITTING	SO2-015/19166	9703
9	การประกอบที่ยึดท่อ PVC สำหรับสายดิน PVC PIPE FITTING ASSEMBLY FOR GROUND WIRE	SO2-015/19128	9704

กองวิศวกรรมไฟฟ้าและเครื่องกล ฝ่ายวิศวกรรม	**การไฟฟ้าส่วนภูมิภาค**	ใช้แทนแบบ..... ถูกแทนโดยแบบ..... เขียนเสร็จวันที่ 18 เม.ย. 2 แก้แบบวันที่..... มิติเป็น..... มาตราส่วน.....
ผู้เขียน ผู้สำรวจ วิศวกร หัวหน้าแผนก ผู้อำนวยการกอง ผู้อำนวยการฝ่าย	ผู้ว่าการ 8 ก.ค. 28	
รองผู้ว่าการฝ่ายเทคนิค	การติดตั้งมิเตอร์ 3 เฟส 4 สาย แบบวัดค่า 2 อัตรา ประกอบซีที. แรงต่ำ INSTALLATION OF 3-Ø, 4-W TWO-RATE TARIFF METER WITH L.T. CURRENT TRANSFORMERS	แบบเลขที่ SAI-015/28011 แผ่นที่ 5 ของจำนวน 6