
การประกอบเลขที่ ASSEMBLY NO. 3212 B

ข้อกำหนดการก่อสร้างช่วงไม่รับแรงดึง

REGULATION ON SLACK SPAN CONSTRUCTION

1 แบบแนะนำการก่อสร้างเสาช่วงไม่รับแรงดึง ให้ก่อสร้างดังรูป

1 SUGGESTION OF SLACK SPAN CONSTRUCTION SEE FIGURE.

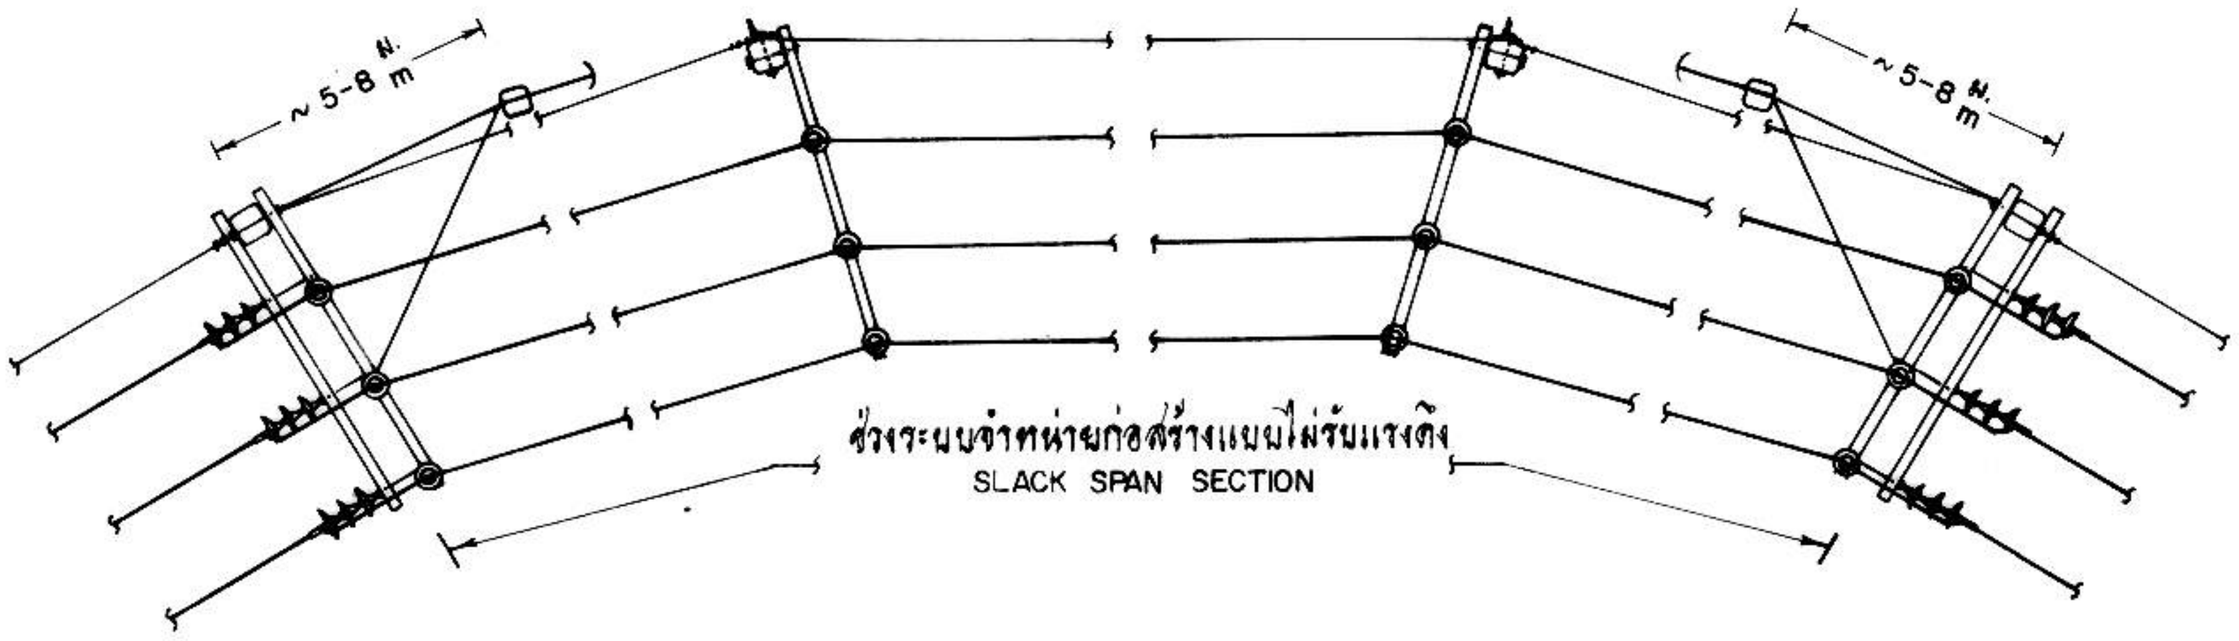

ช่วงระยะขนาดหน่ายก่อสร้างแบบไม่รับแรงดึง
SLACK SPAN SECTION

2 ระยะระหว่างเสา และระยะหย่อนยานของสายช่วงไม่รับแรงดึง

2.1 สายไฟฟ้า

2 SPAN AND SAG IN SLACK SPAN CONSTRUCTION.

2.1 CONDUCTOR.

ขนาดสายไฟฟ้า CONDUCTOR SIZE		ระยะช่วงเสาไม่รับแรงดึงปกติ ม. NORMAL SLACK SPAN LENGTH m	ระยะหย่อนยานของสาย ม. CONDUCTOR SAG m
อะลูมิเนียม, อะลูมิเนียมอัลลอย AI, AI-ALLOY	อะลูมิเนียมแกนเหล็ก ACSR		
ไม่เกิน NOT EXCEED 120 ต.ผม. mm^2	35/6 , 50/8	20	1.00
185 ต.ผม. mm^2	—	15	1.00

2.2 สายล่อฟ้า ระยะหย่อนยาน 0.70 ม.

2.2 OVERHEAD GROUND WIRE SAG 0.70 m.

3 การประกอบไม้ตอนเดี่ยวแบบท้าวแขน ในช่วงไม่รับแรงดึง ใช้ได้ในกรณีทางโค้งมุมไม่เกิน 30°

3 SINGLE CROSSARM(ALLEY) ASSEMBLY IN SLACK SPAN SECTION IS USED FOR LINE ANGLE NOT EXCEED 30°

4 แบบการยึดโยง ดูแบบเลขที่ SAI-015/20023 แผ่นที่ 11

4 GUYING SEE DWG. NO. SAI-015/20023 SHEET 11

5 ระยะระหว่างเสา และตำแหน่งปักเสารับสายยึดโยง สามารถเปลี่ยนแปลงได้ตามสภาพแวดล้อม ทั้งนี้เฉลี่ยระยะระหว่างเสาต้องไม่เกินกว่าที่กำหนดไว้

5 THE SPAN LENGTH AND LOCATION OF STUB GUY POLE SETTING MAY BE VARIED ACCORDING TO LOCAL CONDITIONS, BUT THE AVERAGE SPANS SHALL NOT EXCEED THE LIMIT STIPULATED.

กองวิศวกรรมไฟฟ้าและเครื่องกล ฝ่ายวิศวกรรม	การไฟฟ้าส่วนภูมิภาค	ใช้แทนแบบ..... ถูกแทนโดยแบบ..... เขียนเสร็จวันที่ 23 พ.ย. 21 แก้แบบวันที่..... มิติเป็น..... พาตราส่วน.....
ผู้เขียน ผู้สำรวจ วิศวกร หัวหน้าแผนก หัวหน้ากอง ผู้อำนวยการฝ่าย รองผู้ว่าการฝ่ายเทคนิค	ผู้ว่าการ 13 ธ.ค. 21	
	การก่อสร้างช่วงไม่รับแรงดึง (แบบท้าวแขน) ระบบ 33 kV	
	SLACK SPAN CONSTRUCTION (ALLEY ARM) 33 kV SYSTEM	แบบเลขที่ SAI-015/21074 แผ่นที่ 1 ของจำนวน 1 แผ่น