การประกอบเลขที่
ASSEMBLY NO. 3232

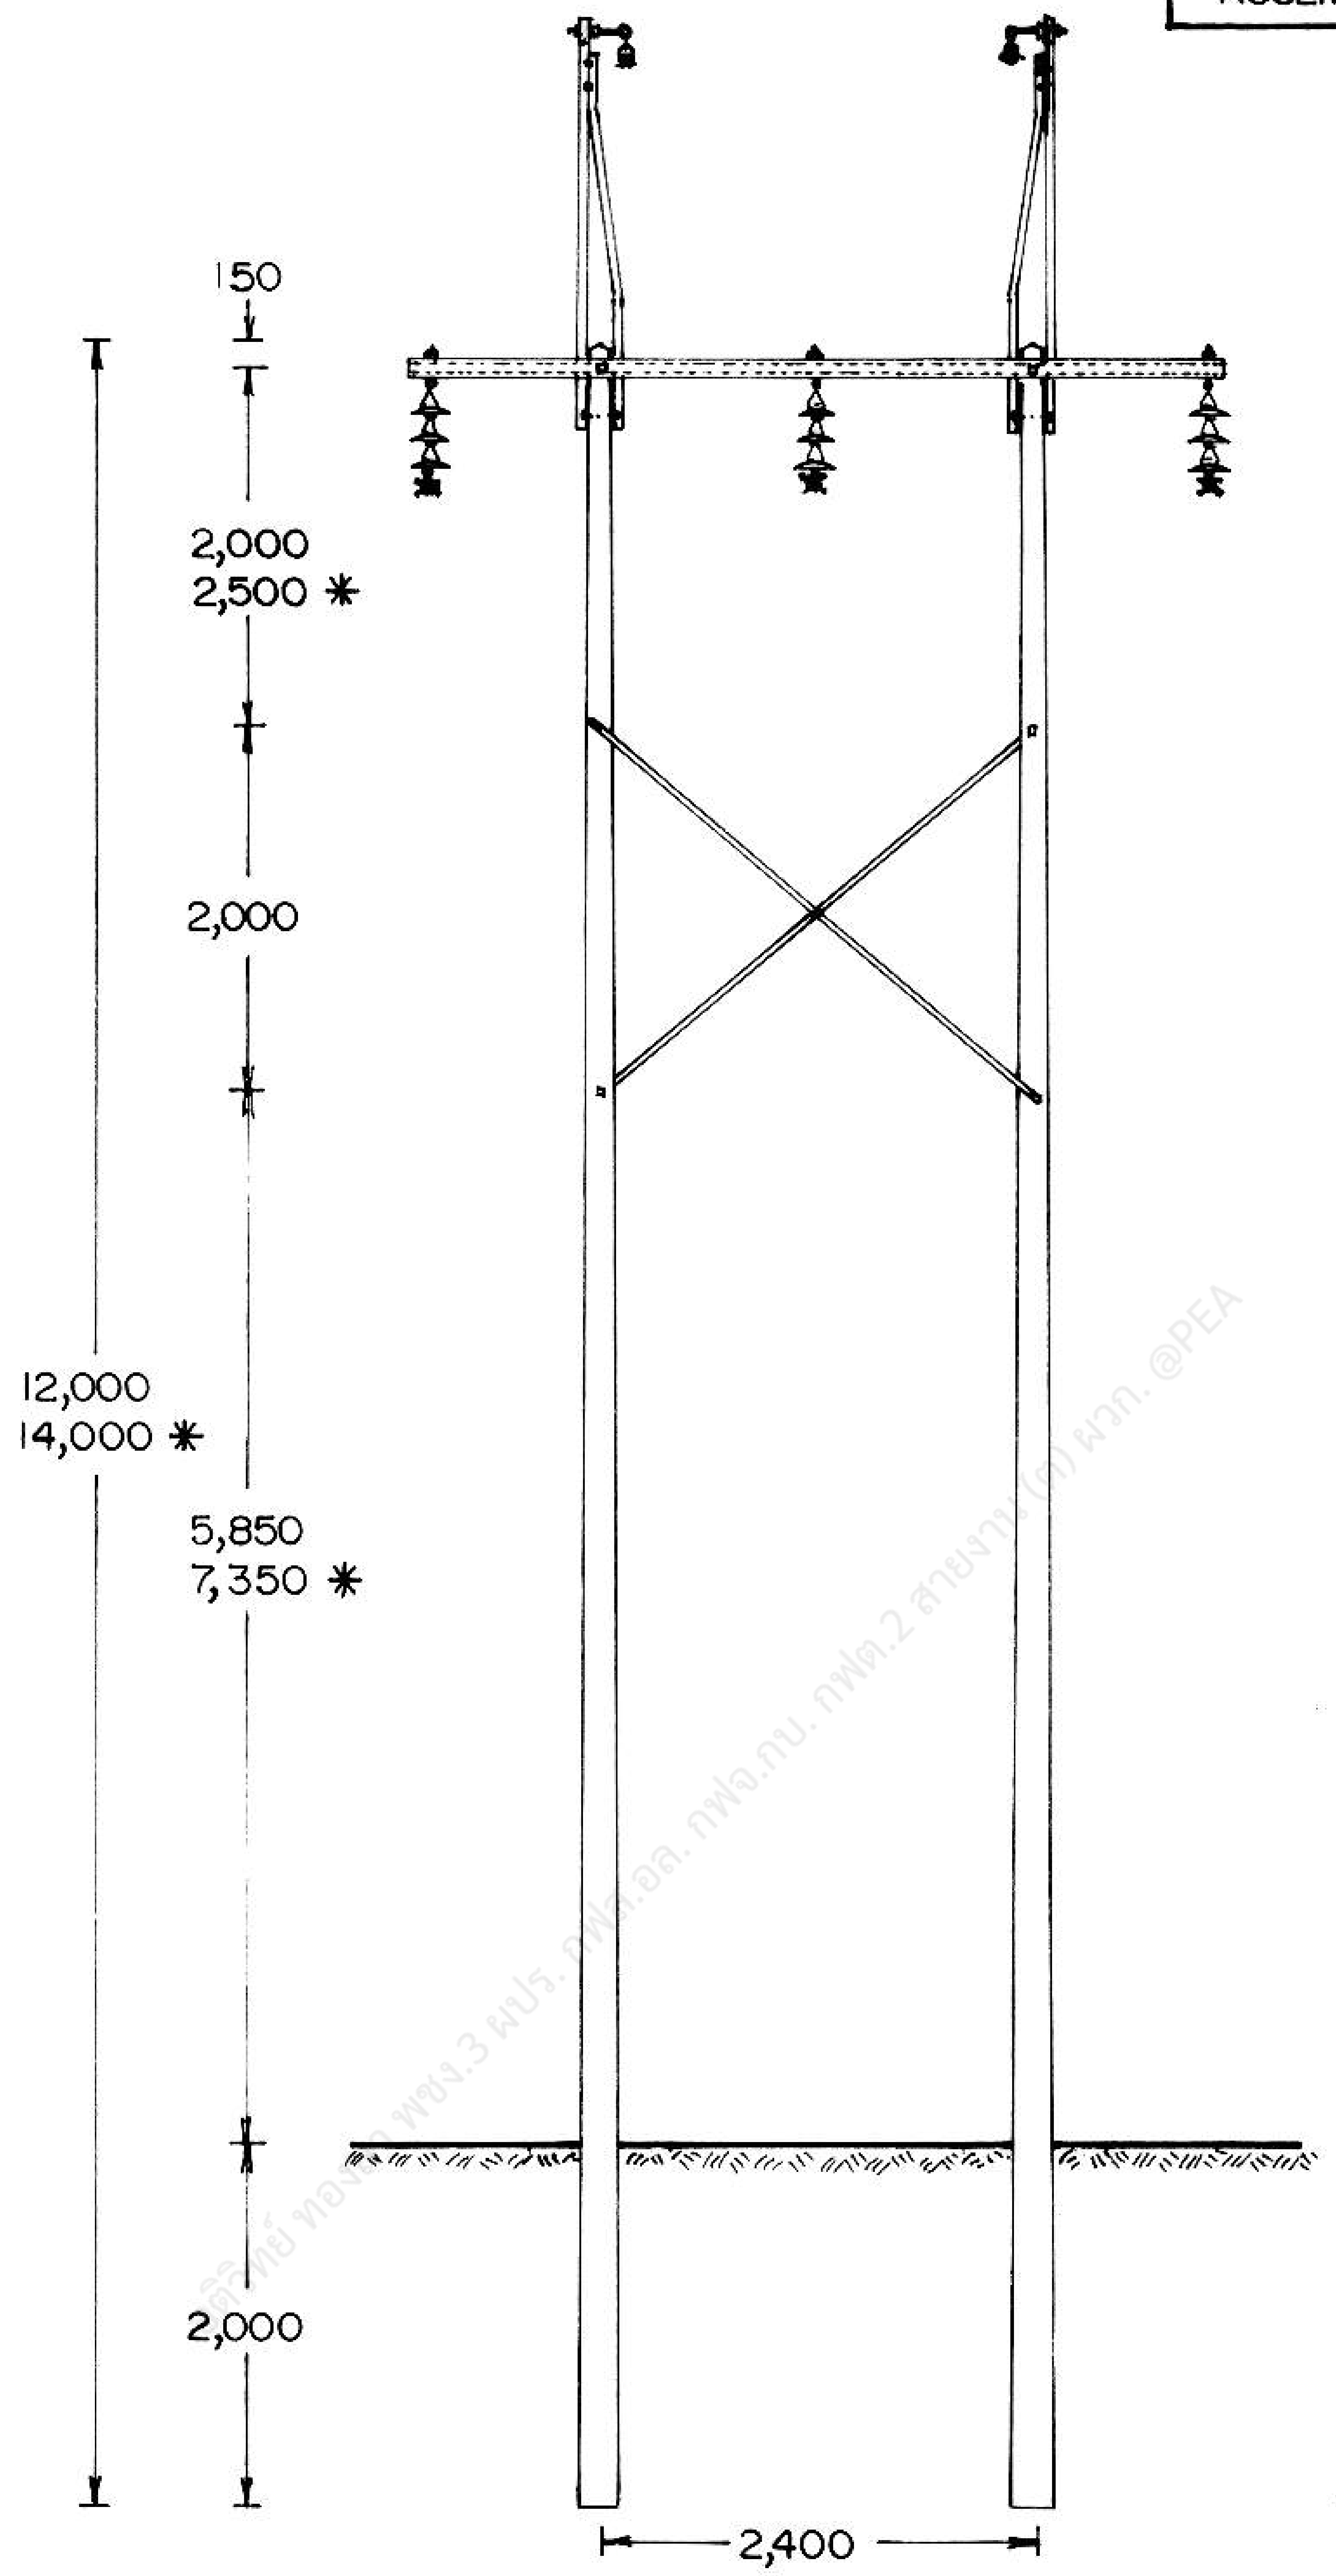

* สำหรับเสา 14 ม.
FOR 14 m POLE

กองวิศวกรรมไฟฟ้าและเครื่องกล
ฝ่ายวิศวกรรม

การไฟฟ้าส่วนภูมิภาค

ผู้เขียน
ผู้สำรวจ
วิศวกร
หัวหน้าแผนก
ผู้อำนวยการกอง
ผู้อำนวยการฝ่าย
รองผู้ว่าการฝ่ายเทคนิค

ผู้ว่าการ 16 ก.ย. 34

โครงสร้างเสาสำหรับการติดตั้งระบบจำหน่าย 33 kV
แบบแขวนสายไฟฟ้ากับเสาคู่ ช่วงเสา 120-200 ม.

POLE STRUCTURE FOR INSTALLATION 33 kV SYSTEM
H-FRAME SUSPENSION, SPAN 120-200 m

ใช้แทนแบบ
ถูกแทนโดยแบบ
เขียนเสร็จวันที่ 19 ส.ค. 34
แก้แบบวันที่
มิติเป็น มิลลิเมตร
มาตราส่วน 1:75
แบบเลขที่ SA1-015/34018
แผ่นที่ 1 ของจำนวน 2 แผ่น

12 ก.ย. 2534

การประกอบเลขที่
ASSEMBLY NO. 3232

ข้อกำหนด

1. ใช้สำหรับก่อสร้างระบบจำหน่าย 33 kV ที่มีระยะห่างระหว่างเสาเกิน 120 ม. เช่น บริเวณพื้นที่ที่เป็นทางคดเคี้ยวไปตามภูเขา หรือ ทางขึ้น – ลงเขา และไม่สามารถใช้ระยะห่างระหว่างเสาปกติ ตามแบบเลขที่ SAI-015/21050 (การประกอบเลขที่ 9302) ได้
2. ขนาดสายสูงสุด :-
   สายล่อฟ้า : ลวดเหล็กตีเกลียว 25 ต.มม.
   ระบบ 33 kV : สายอะลูมิเนียมแกนเหล็ก 185/30 ต.มม.
   หรือ สายอะลูมิเนียมเจือ 185 ต.มม.
3. สายไฟฟ้าต้องมีระดับความสูงเหนือพื้นดินไม่น้อยกว่า 5.20 ม.
4. สายไฟฟ้าต้องมีระดับความสูงเหนือยอดของต้นไม้ไม่น้อยกว่า 2.10 ม.
5. ระยะห่างของสมอบกคอนกรีตจากศูนย์กลางของโคนเสา ต้องไม่น้อยกว่า 7.00 ม.
6. รายละเอียด การติดตั้งอุปกรณ์ต่าง ๆ, ฐานรากเสา, และสมอบกคอนกรีต ดูแบบเลขที่ SAI-015/34019 ถึงเลขที่ SAI-015/34022

REGULATIONS

1. USE FOR CONSTRUCTION 33 kV DISTRIBUTION LINES; HAVING SPAN LENGTH EXCEED 120 m SUCH AS MEANDER ALONG THE VALLEY OR UP-DOWN HILL, AND CAN NOT USE THE NORMAL RULING SPAN ACCORDING TO DWG. NO. SAI-015/21050 (ASSEMBLY NO. 9302).
2. MAXIMUM CONDUCTOR SIZE :-
   OHGW : STEEL STRANDED WIRE 25 mm^2.
   33 kV SYSTEM : ACSR 185/30 mm^2, OR Al-ALLOY CONDUCTOR 185 mm^2.
3. CONDUCTORS SHALL BE ABOVE GROUND OF NOT LESS THAN 5.20 m.
4. CONDUCTORS SHALL BE ABOVE TOP OF TREES OF NOT LESS THAN 2.10 m.
5. THE DISTANCE OF CONCRETE ANCHOR FROM POLE CENTER LINE SHALL NOT BE LESS THAN 7.00 m.
6. DETAILS OF MATERIAL ASSEMBLY, POLE FOUNDATION, AND CONCRETE ANCHOR; SEE DWGS. NO. SAI-015/34019 TO SAI-015/34022.

กองวิศวกรรมไฟฟ้าและเครื่องกล
ฝ่ายวิศวกรรม

ผู้เขียน
ผู้ตรวจ
วิศวกร
หัวหน้าแผนก
ผู้อำนวยการกอง
ผู้อำนวยการฝ่าย
รองผู้ว่าการฝ่ายเทคนิค

การไฟฟ้าส่วนภูมิภาค

ผู้ว่าการ 16 ก.ย. 34

โครงสร้างเสาสำหรับการติดตั้งระบบจำหน่าย 33 kV
แบบแขวนสายไฟฟ้ากับเสาคู่ ช่วงเสา 120-200 ม.

POLE STRUCTURE FOR INSTALLATION 33 kV SYSTEM
H-FRAME SUSPENSION, SPAN 120-200 m

ใช้แทนแบบ
ถูกแทนโดยแบบ
เขียนเสร็จวันที่ 19 ส.ค. 34
แก้แบบวันที่
มิติเป็น
มาตราส่วน
แบบเลขที่ SAI-015/34018
แผ่นที่ 2 ของจำนวน 2 แผ่น

12 ก.ย 2534