การประกอบเลขที่ ASSEMBLY NO. 5301

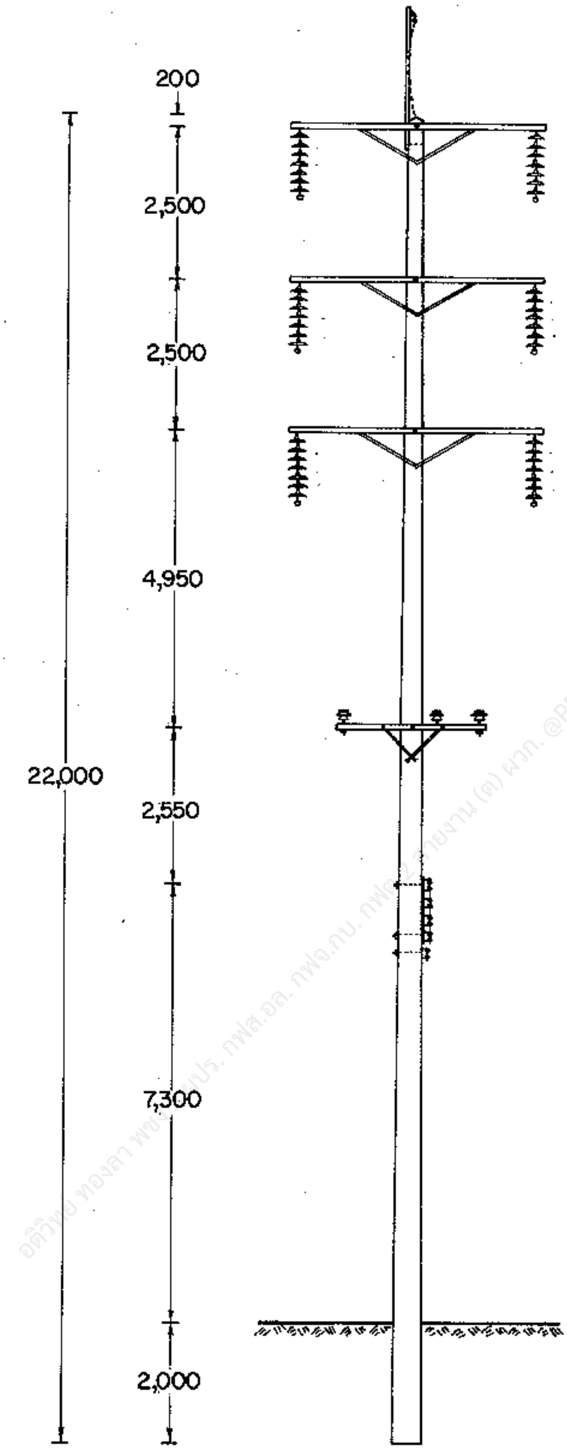

อดิศักดิ์ ทองลา ... กฟส.อล. กฟฉ.กบ. ... @PEA

กองวิศวกรรมไฟฟ้าและเครื่องกล
ฝ่ายวิศวกรรม

ผู้เขียน ....
ผู้สำรวจ ....
วิศวกร ....
หัวหน้าแผนก ....
หัวหน้ากอง ....
ผู้อำนวยการฝ่าย ....

รองผู้ว่าการฝ่ายเทคนิค

การไฟฟ้าส่วนภูมิภาค

ผู้ว่าการ .... 24 มี.ค. 23

115 kV วงจรคู่ สายไฟฟ้าเดี่ยว
เสาสำหรับทางตรง
แบบ DS - TG - 1

115 kV DOUBLE CIRCUIT SINGLE CONDUCTOR
TANGENT STRUCTURE
TYPE DS - TG - 1

ใช้แทนแบบ ....
ถูกแทนโดยแบบ ....
เขียนเสร็จวันที่ 3 ม.ค.23
แก้แบบวันที่ ....
มิติเป็น มม.
มาตราส่วน 1 : 125
แบบเลขที่ SAL-015/23015
แผ่นที่ 1 ของจำนวน 3 แผ่น

การประกอบเลขที่ ASSEMBLY NO. **5301**

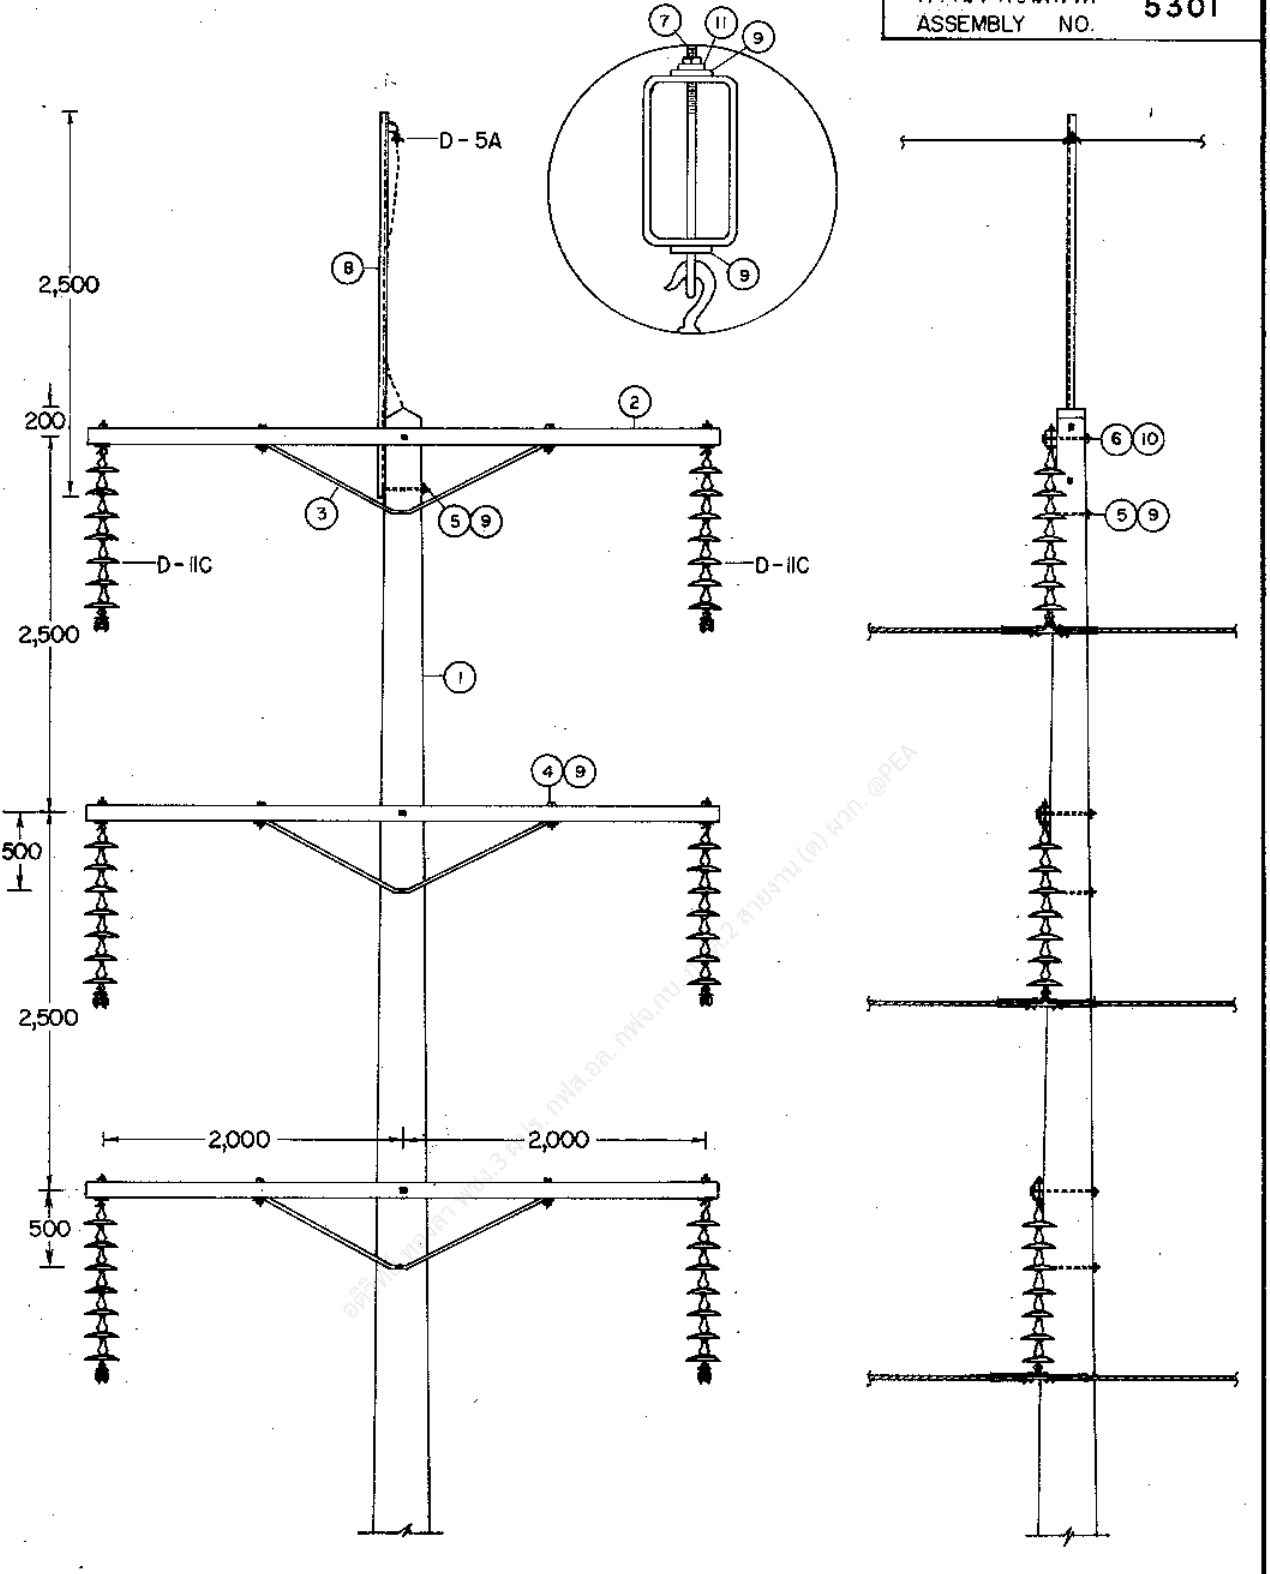

กองวิศวกรรมไฟฟ้าและเครื่องกล
ฝ่ายวิศวกรรม

ผู้เขียน
ผู้สำรวจ
วิศวกร
หัวหน้าแผนก
หัวหน้ากอง
ผู้อำนวยการฝ่าย

รองผู้ว่าการฝ่ายเทคนิค

การไฟฟ้าส่วนภูมิภาค

ผู้ว่าการ .... 24 มี.ค. 23

115 kV วงจรคู่ สายไฟฟ้าเดี่ยว
เสาสำหรับทางตรง
แบบ DS - TG - I

115 kV DOUBLE CIRCUIT SINGLE CONDUCTOR
TANGENT STRUCTURE
TYPE DS - TG - I

ใช้แทนแบบ
ถูกแทนโดยแบบ
เขียนเสร็จวันที่ 3 ม.ค.23
แก้แบบวันที่
มิติเป็น มม.
มาตราส่วน 1 : 50

แบบเลขที่ SA-015/23015
แผ่นที่ 2 ของจำนวน 3 แผ่น

1 ? ส.ค. 2523

การประกอบเลขที่
ASSEMBLY NO. **5301**

บัญชีวัสดุ
BILL OF MATERIAL

ลำดับที่ ITEM	รายละเอียด DESCRIPTION	จำนวน REQ'D	วัสดุเลขที่ MAT. NO.
1	เสาคอนกรีต 22 ม. POLE, CONCRETE 22 m. LONG	1	00010011 (0041)
2	คอนสายแบบเหล็ก ขนาด 100 X 50 X 3.2 มม.ยาว 4.20 ม. CROSSARM, STEEL 100 X 50 X 3.2 mm, 4.20 m LONG	3	00120001 (0116)
3	เหล็กฉากรับคอนสาย ขนาด 50 X 50 X 6 มม. ช่วงกว้าง 1,800 มม. ตกลง 450 มม. BRACE, ANGLE STEEL, 50 X 50 X 6 mm 1,800 mm WIDE 450 mm DROP	3	01200007 (0119)
4	สลักเกลียว M 16 X 130 มม. BOLT, MACHINE, M 16 X 130 mm	6	01110200 (0220) *
5	สลักเกลียว M 16 X 350 มม. BOLT, MACHINE, M 16 X 350 mm	5	01110205 (0225)
6	สลักเกลียว M 20 X 400 มม. BOLT, MACHINE, M 20 X 400 mm	3	01110301 (0233)
7	สลักห่วงโอแวล M 16 X 150 มม. BOLT, OVAL EYE M 16 X 150 mm	6	01150000 (0257)
8	เหล็กฉากรับสายล่อฟ้าทางตรง ยาว 2.50 ม. OVERHEAD GROUND WIRE BAYONET 2.50 m LONG	1	01010004 (0135)
9	แหวนสี่เหลี่ยมแบน 52X52X4.5 มม. รู Ø 18 มม. มอก. 258 WASHER, SQUARE **FLAT** 52X52X4.5mm HOLE Ø 18 mm TIS 258	23	01180100 (0355)
10	แหวนสี่เหลี่ยมแบน 62X62X6 มม. รู Ø 22 มม. มอก. 258 WASHER, SQUARE FLAT **62X62X6** mm HOLE Ø 22mm **TIS 258**	6	01180101 (0356)
11	แหวนสปริง M 16 มอก. 259 WASHER, LOCK, M 16, **TIS 259**	6	01180301 (0365)
	รายละเอียด DETAIL		
D-11C	การประกอบลูกถ้วยแขวน SUSPENSION INSULATOR ASSEMBLY	6	
D-5A	การต่อสายล่อฟ้า OVERHEAD GROUND WIRE CONNECTION	1	
D-10A	ฐานรากเสา POLE FOUNDATION	1	

กองวิศวกรรมไฟฟ้าและเครื่องกล ฝ่ายวิศวกรรม	**การไฟฟ้าส่วนภูมิภาค**	ใช้แทนแบบ.......... ถูกแทนโดยแบบ..........
ผู้เขียน.......... ผู้ตรวจ.......... วิศวกร.......... หัวหน้าแผนก.......... หัวหน้ากอง.......... ผู้อำนวยการฝ่าย.......... 23	ผู้ว่าการ.......... 24 มี.ค. 23 115 kV วงจรคู่ สายไฟฟ้าเดี่ยว เสาสำหรับทางตรง แบบ DS - TG - 1	เขียนเสร็จวันที่ 3 ม.ค.23 แก้แบบวันที่.......... มิติเป็น.......... มาตราส่วน..........
รองผู้ว่าการฝ่ายเทคนิค	115 kV DOUBLE CIRCUIT SINGLE CONDUCTOR TANGENT STRUCTURE TYPE DS - TG - 1	แบบเลขที่ SAI-015/23015 แผ่นที่ 3 ของจำนวน 3 แผ่น

19 มี.ค. 2523