การประกอบเลขที่ ASSEMBLY NO. 0301

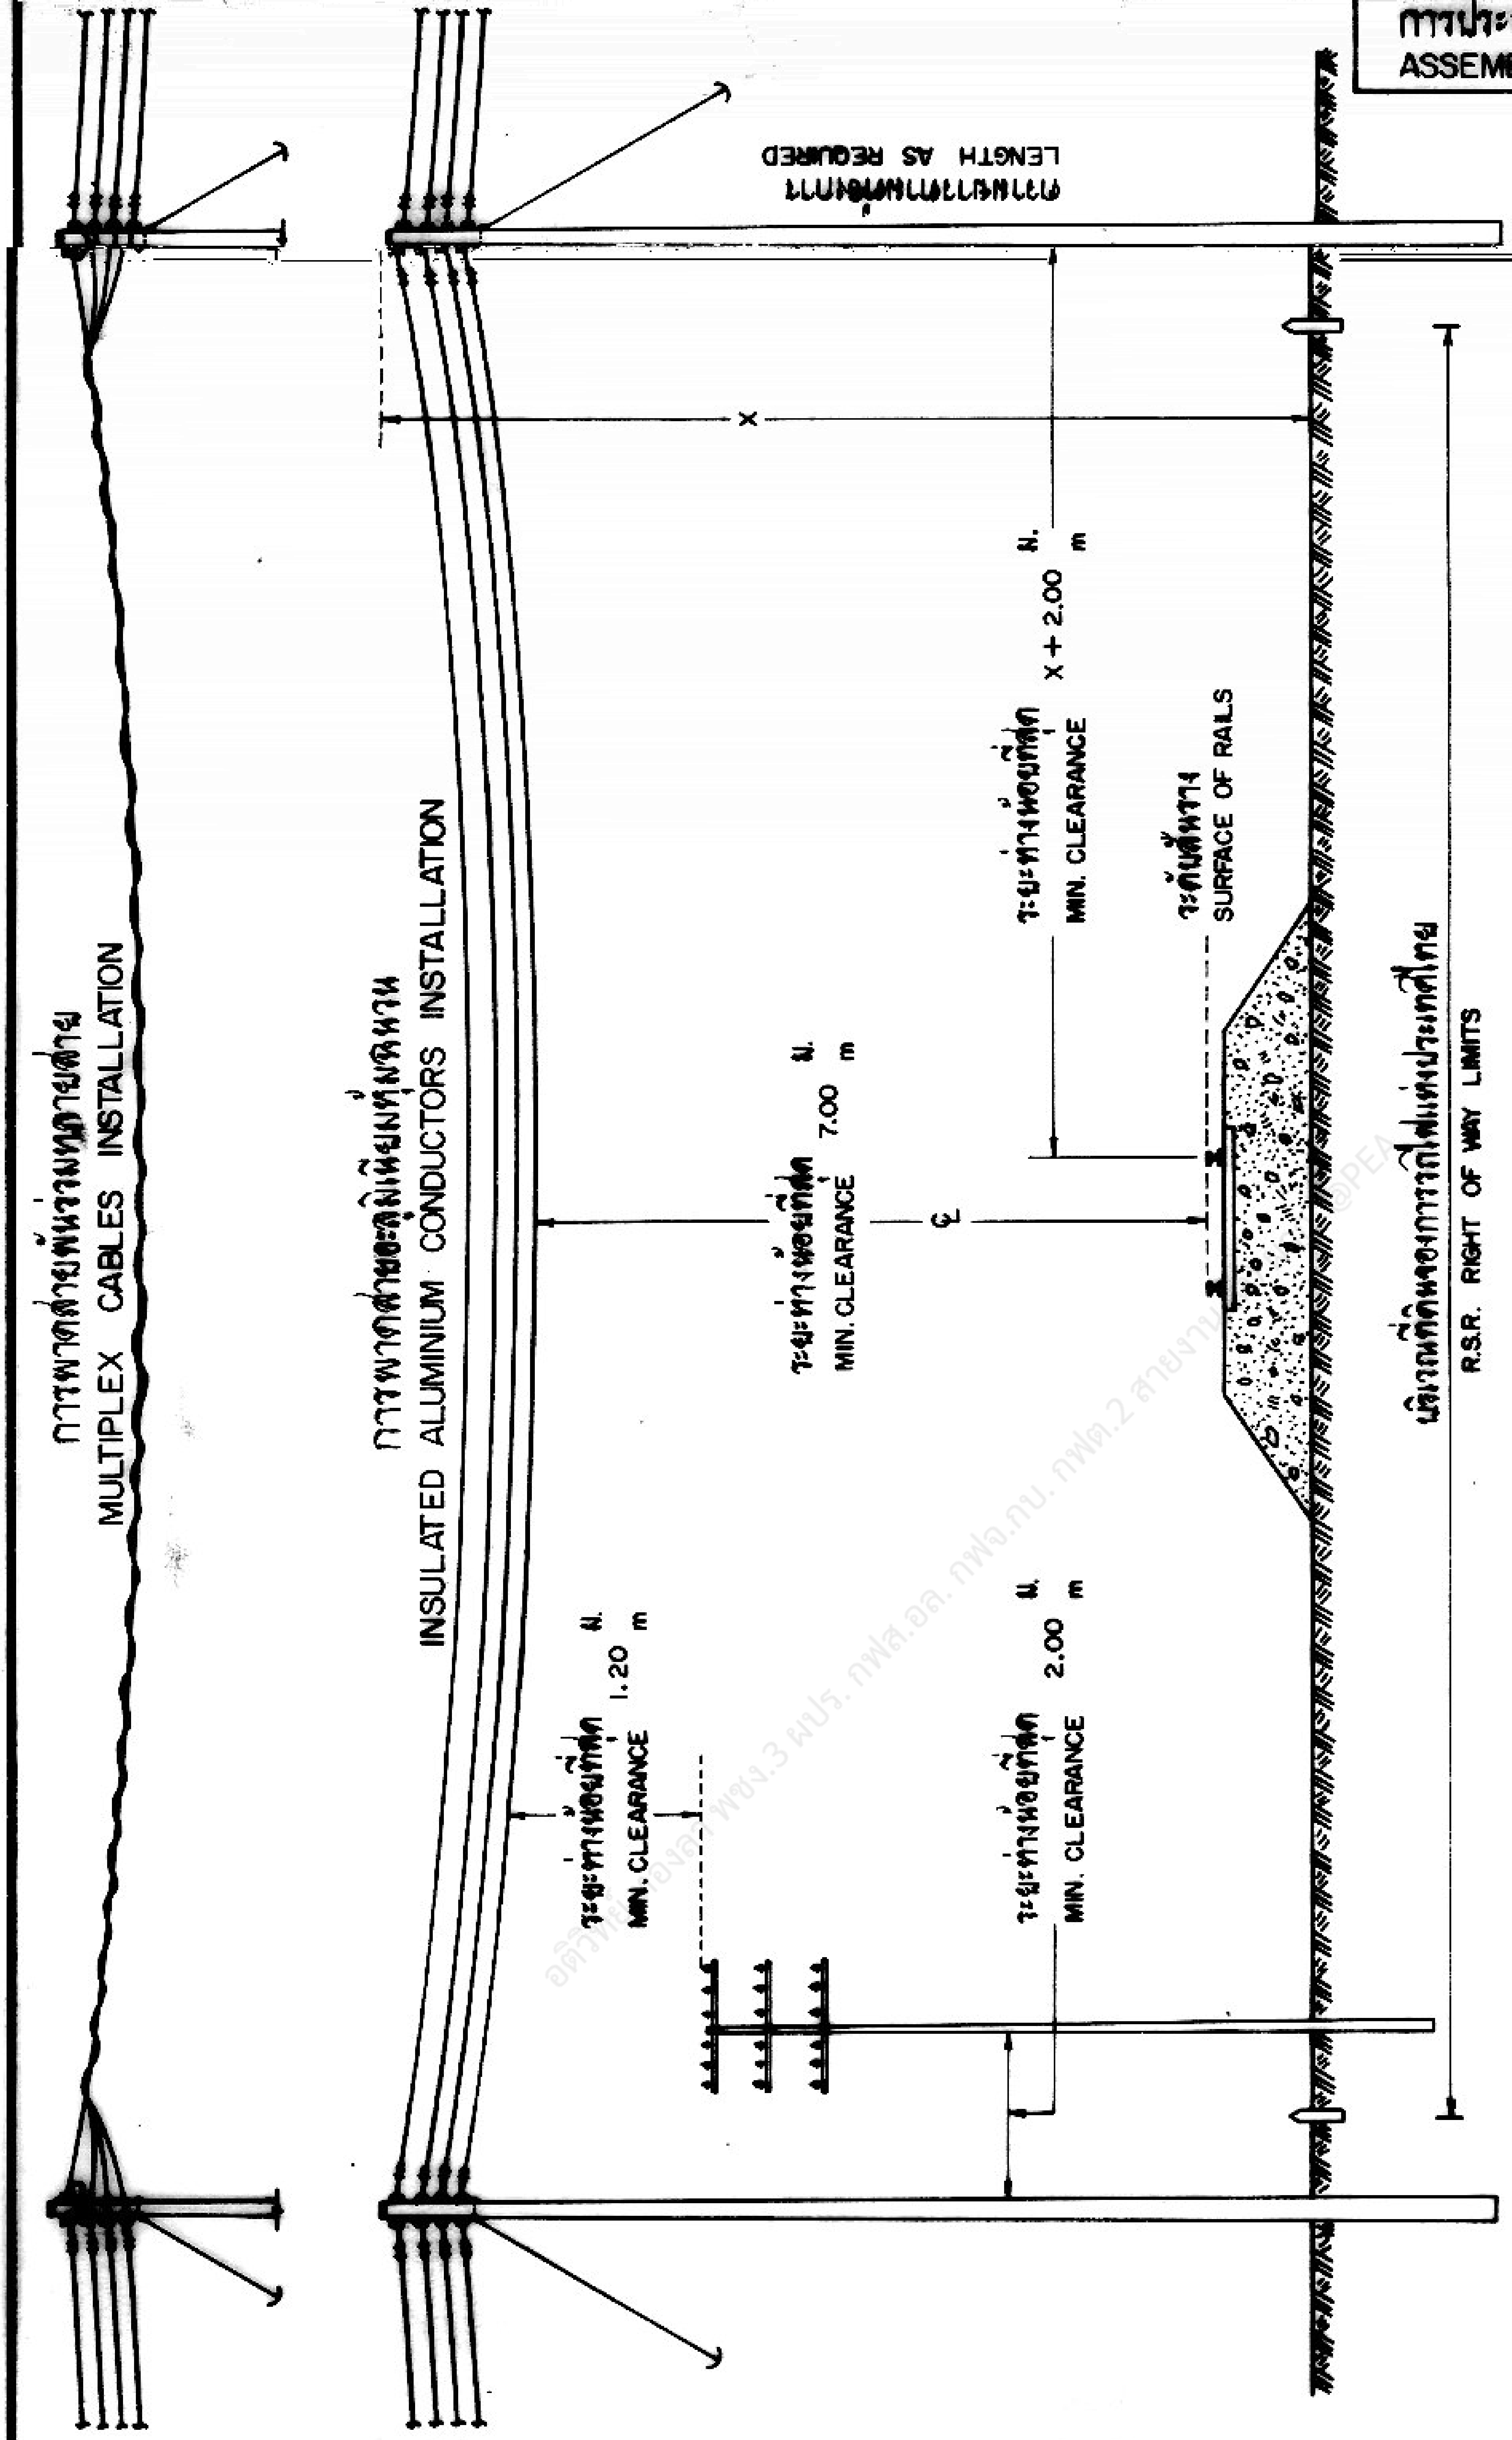
การพาดสายพันรวมหลายสาย
MULTIPLEX CABLES INSTALLATION
การพาดสายอะลูมิเนียมหุ้มฉนวน
INSULATED ALUMINIUM CONDUCTORS INSTALLATION
ความยาวตามต้องการ
LENGTH AS REQUIRED
X
ระยะห่างน้อยที่สุด MIN. CLEARANCE X + 2.00 ม. m
ระดับสันราง SURFACE OF RAILS
ระยะห่างน้อยที่สุด MIN. CLEARANCE 7.00 ม. m
℄
เขตที่ดินของการรถไฟแห่งประเทศไทย
R.S.R. RIGHT OF WAY LIMITS
ระยะห่างน้อยที่สุด MIN. CLEARANCE 1.20 ม. m
ระยะห่างน้อยที่สุด MIN. CLEARANCE 2.00 ม. m

หมายเหตุ ขนาดสายเล็กที่สุด 1 สายอะลูมิเนียมหุ้มฉนวน 35 ต.มม.

2 สายนิวทรัลของสายพันรวมหลายสาย

2.1 อะลูมิเนียมเปลือยหรืออะลูมิเนียมอัลลอย 35 ต.มม.

2.2 อะลูมิเนียมแกนเหล็ก 35/6 ต.มม.

(25/4 ต.มม. สำหรับสายพันรวมสองสาย)

ระยะช่วงเสาสูงสุดไม่เกิน 50 ม.

NOTES MIN. CONDUCTOR SIZE 1 INSULATED ALUMINIUM CONDUCTOR 35 mm²

2 NEUTRAL OF MULTIPLEX CABLE

2.1 BARE ALUMINIUM, Al-ALLOY 35 mm²

2.2 ACSR 35/6 mm²

(25/4 mm² FOR DUPLEX CABLE)

LIMITING SPAN 50 m

กองวิศวกรรมไฟฟ้าและเครื่องกล ฝ่ายวิศวกรรม	การไฟฟ้าส่วนภูมิภาค	ใช้แทนแบบ ถูกแทนโดยแบบ เขียนเสร็จวันที่ 4 ต.ค. 20
ผู้เขียน ผู้สำรวจ วิศวกร หัวหน้าแผนก หัวหน้ากอง ผู้อำนวยการฝ่าย	ผู้ว่าการ การพาดสายแรงต่ำ ไม่เกิน 1 KV ข้ามทางรถไฟ สำหรับสายหุ้มฉนวน	แก้แบบวันที่ พิมพ์เขียน มาตราส่วน
รองผู้ว่าการฝ่ายเทคนิค	L.T. LINE 1 kV OR LESS ACROSS THE RAILROAD FOR INSULATED CONDUCTORS	แบบเลขที่ SAI-015/20021 แผ่นที่ 1 ของจำนวน 1 แผ่น