การประกอบเลขที่ ASSEMBLY NO. 0810

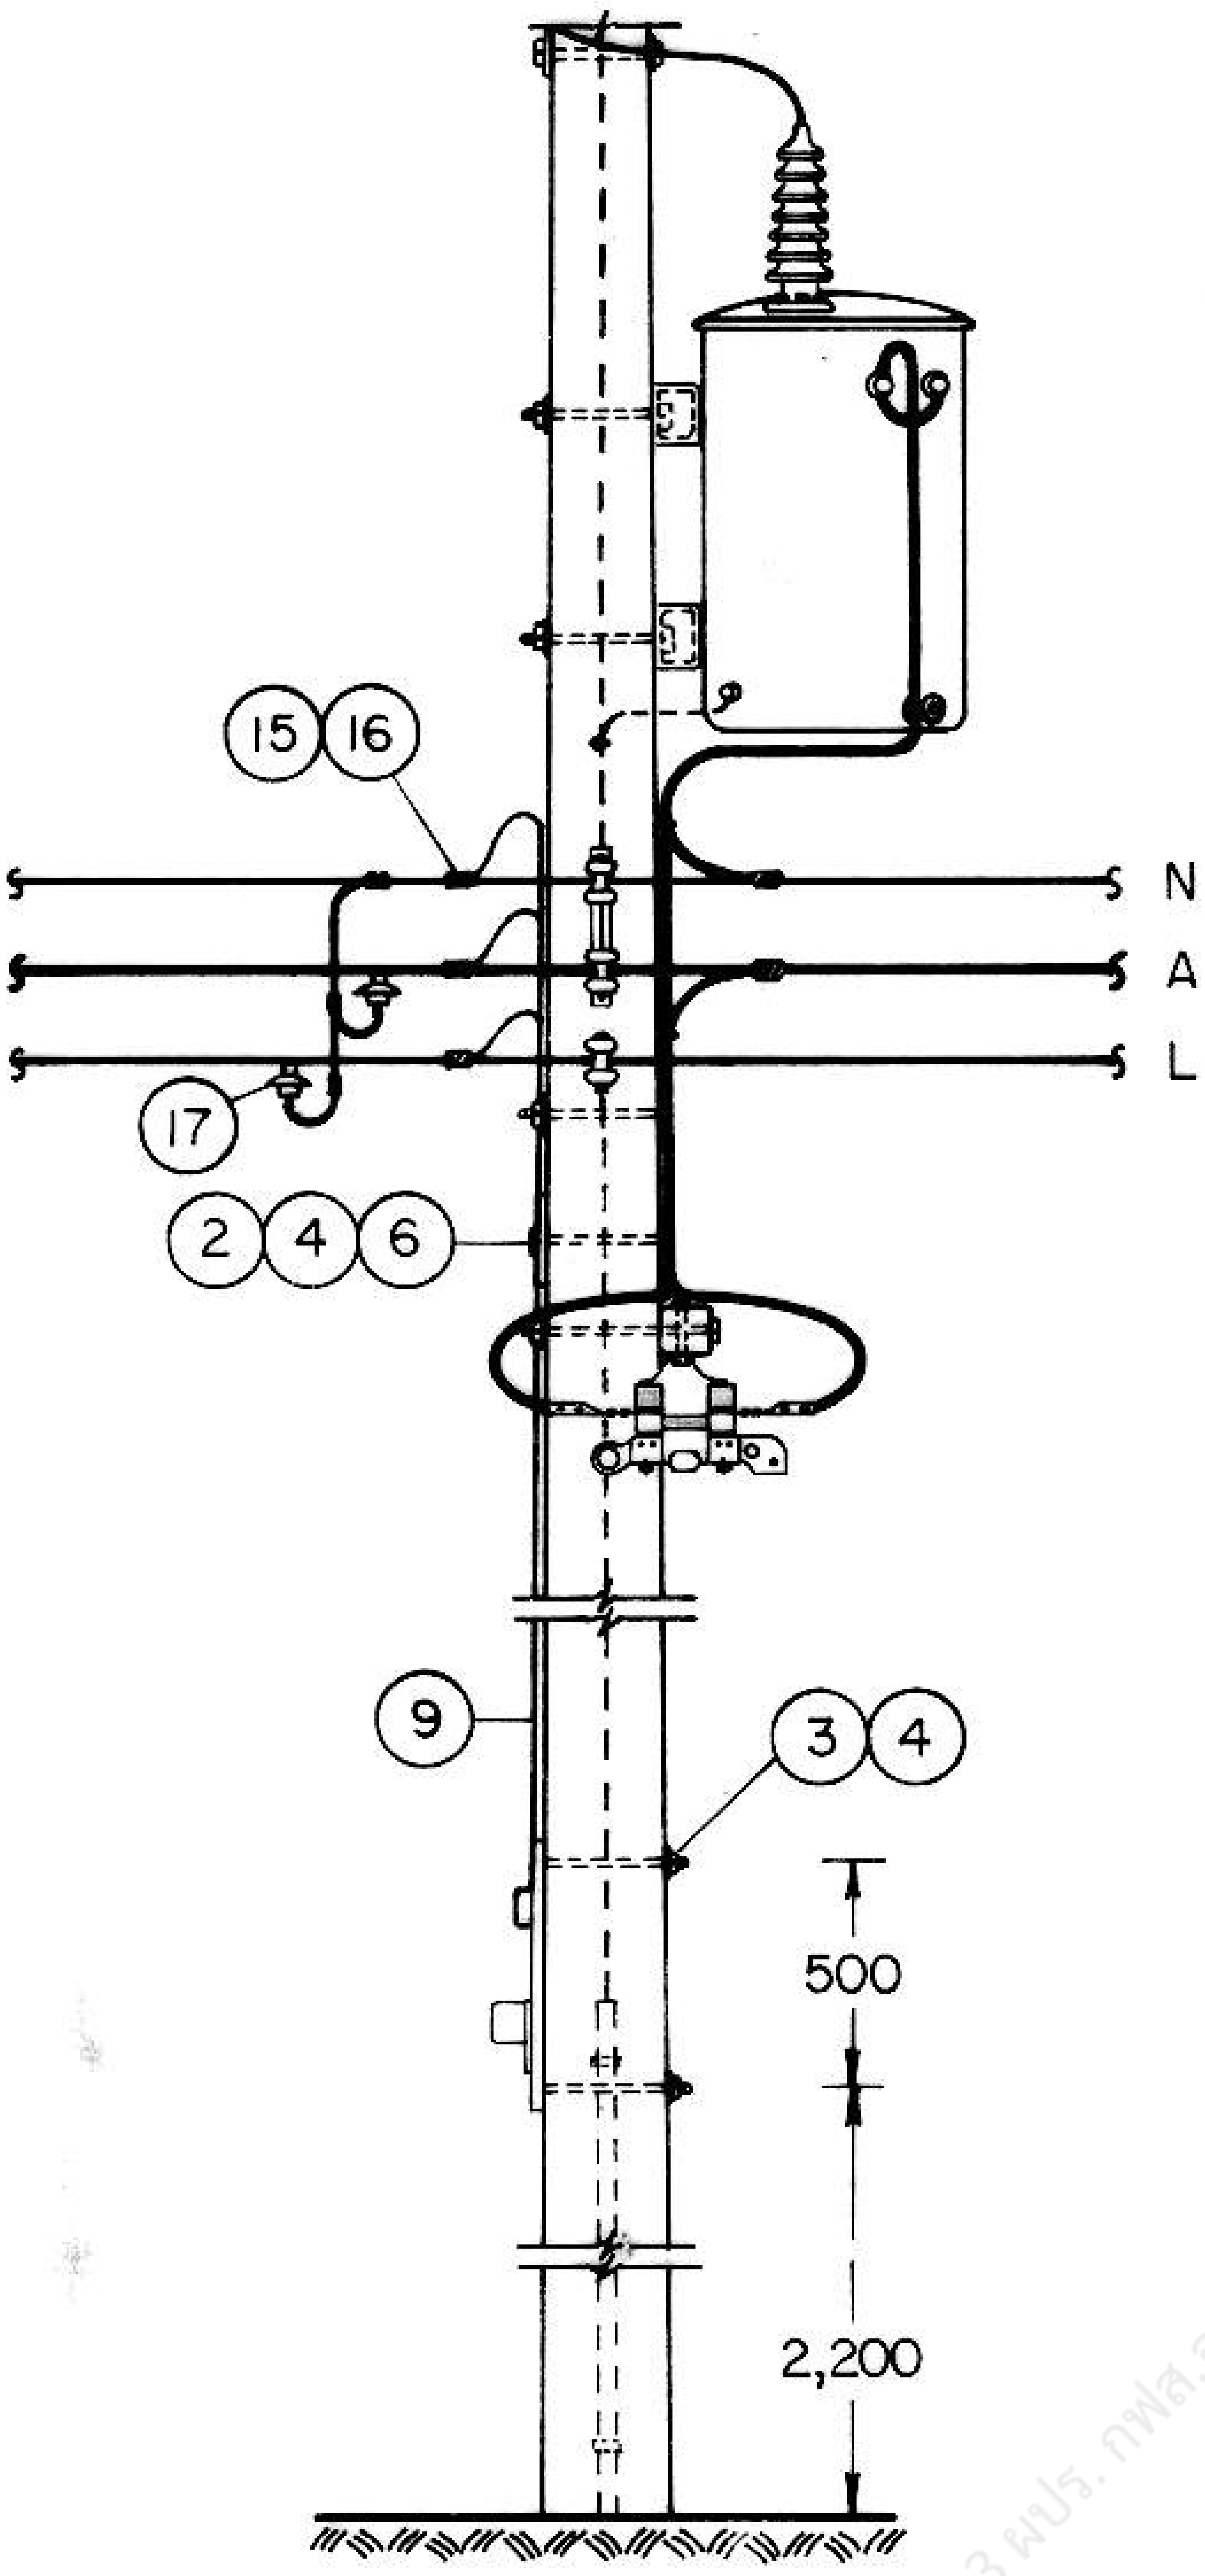
15
16
N
A
L
17
2
4
6
9
3
4
500
2,200

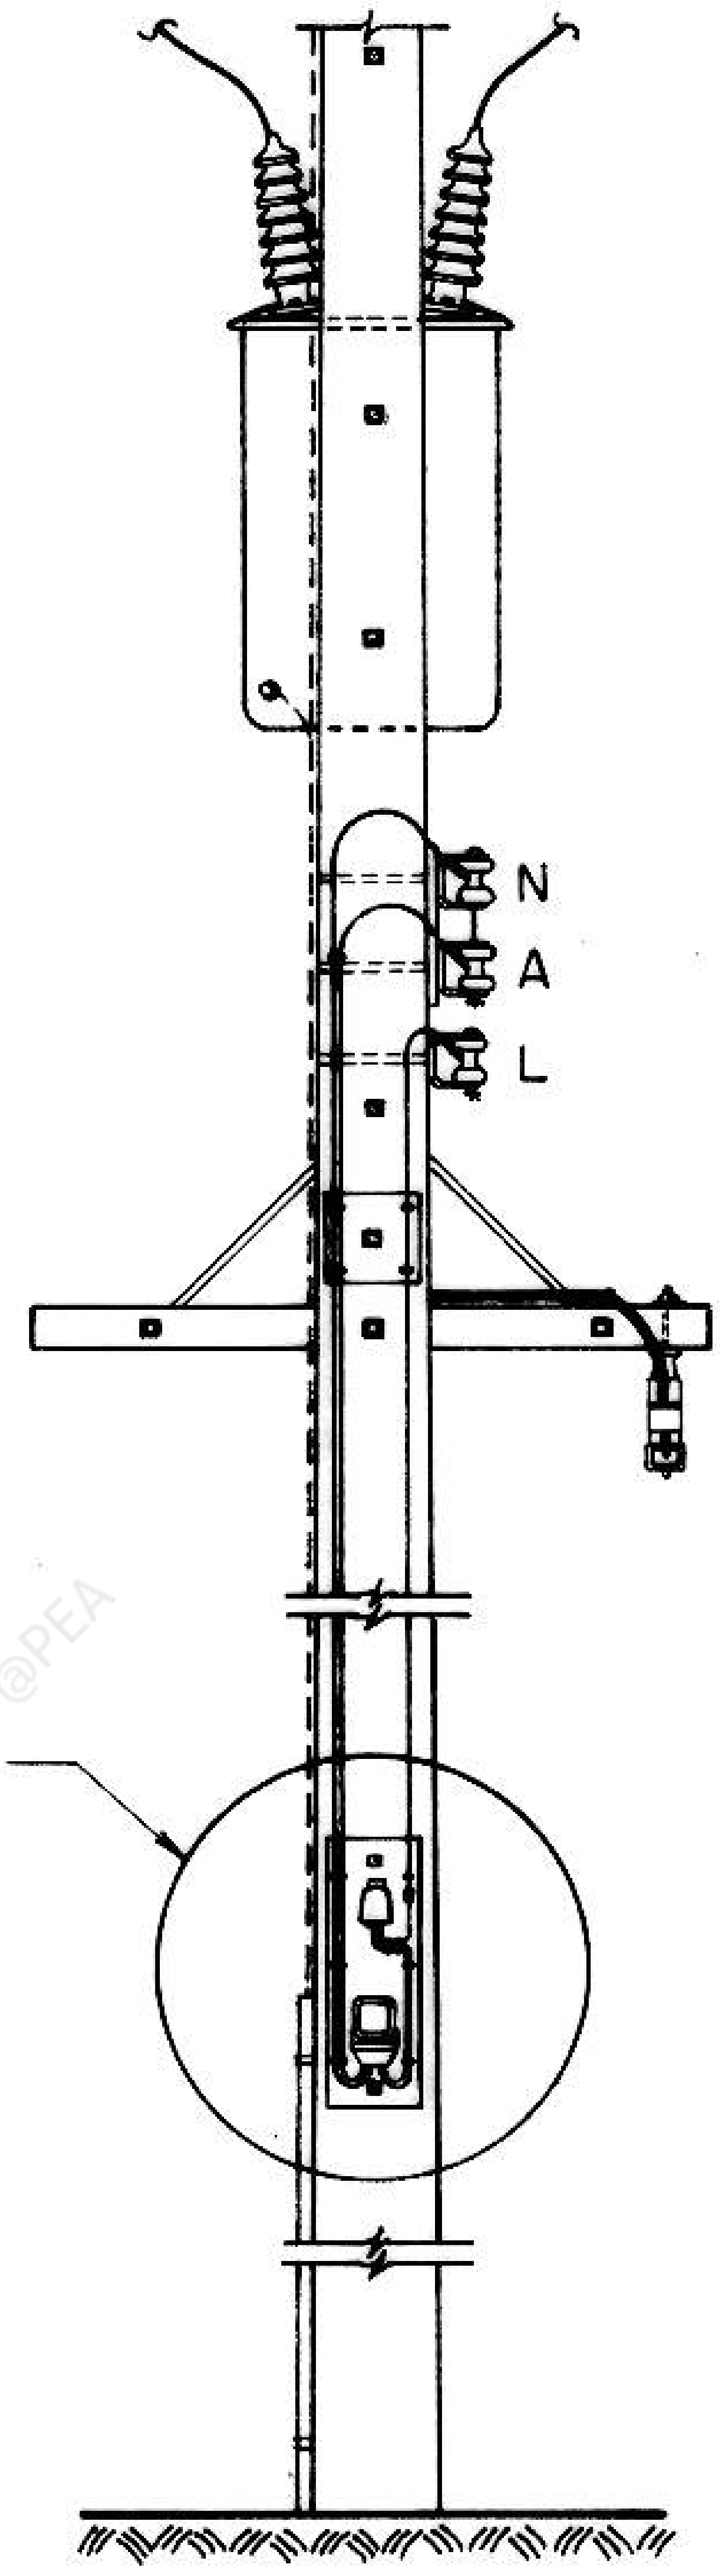
N
A
L
ดูรายละเอียด
SEE DETAIL
A

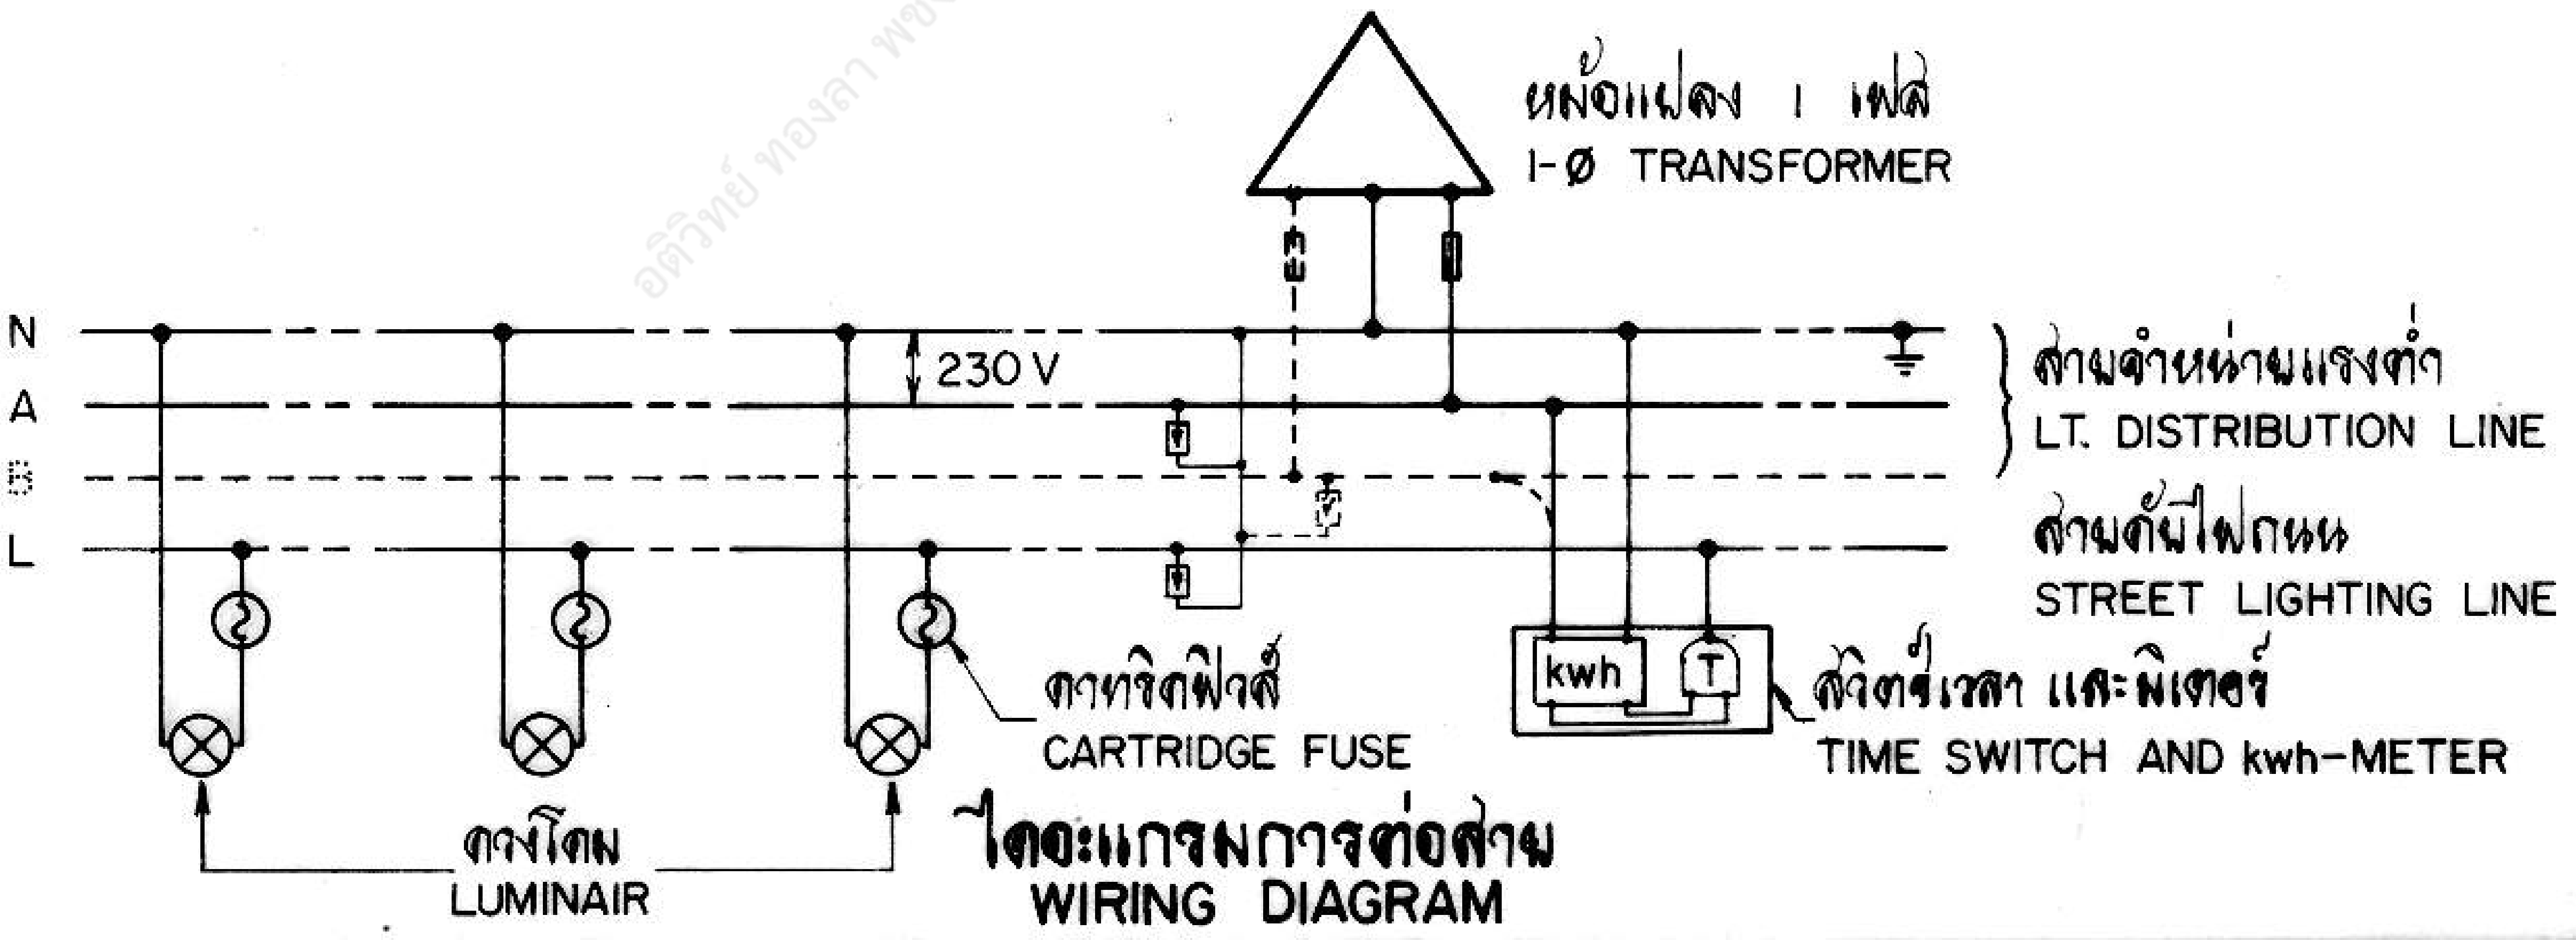
หม้อแปลง 1 เฟส
I-Ø TRANSFORMER
N
A
B
L
230 V
สายจำหน่ายแรงต่ำ
LT. DISTRIBUTION LINE
สายต้นไฟถนน
STREET LIGHTING LINE
kwh
T
คาทริดฟิวส์
CARTRIDGE FUSE
สวิตช์เวลา และมิเตอร์
TIME SWITCH AND kwh-METER
ดวงโคม
LUMINAIR

ไดอะแกรมการต่อสาย
WIRING DIAGRAM

อดิวิทย์ ทองลาภ พชง.3 ผปร. กฟส.อล. กฟจ.กบ. กฟต.2 สายงาน (ต) ผวภ. @PEA

กองวิศวกรรมไฟฟ้าและเครื่องกล ฝ่ายวิศวกรรม	การไฟฟ้าส่วนภูมิภาค	ใช้แทนแบบ ถูกแทนโดยแบบ เขียนเสร็จวันที่ 3 มี.ค. 26 แก้แบบวันที่ ผลิตเป็น ผผ. มาตราส่วน 1 : 40
ผู้เขียน ผู้สำรวจ วิศวกร หัวหน้าแผนก ผู้อำนวยการกอง ผู้อำนวยการฝ่าย	ผู้ว่าการ . 11 ส.ค. 26 การติดตั้งสวิตช์เวลา ก ที่เสาต้นติดตั้งหม้อแปลงแบบแขวน	
รองผู้ว่าการฝ่ายเทคนิค	TIME SWITCH INSTALLATION A ON SINGLE-PHASE TRANSFORMER POLE	แบบเลขที่ SAI-015/26009 แผ่นที่ 1 ของจำนวน 6 แผ่น

- 5 ส.ค. 2526

การประกอบเลขที่ ASSEMBLY NO. 0810

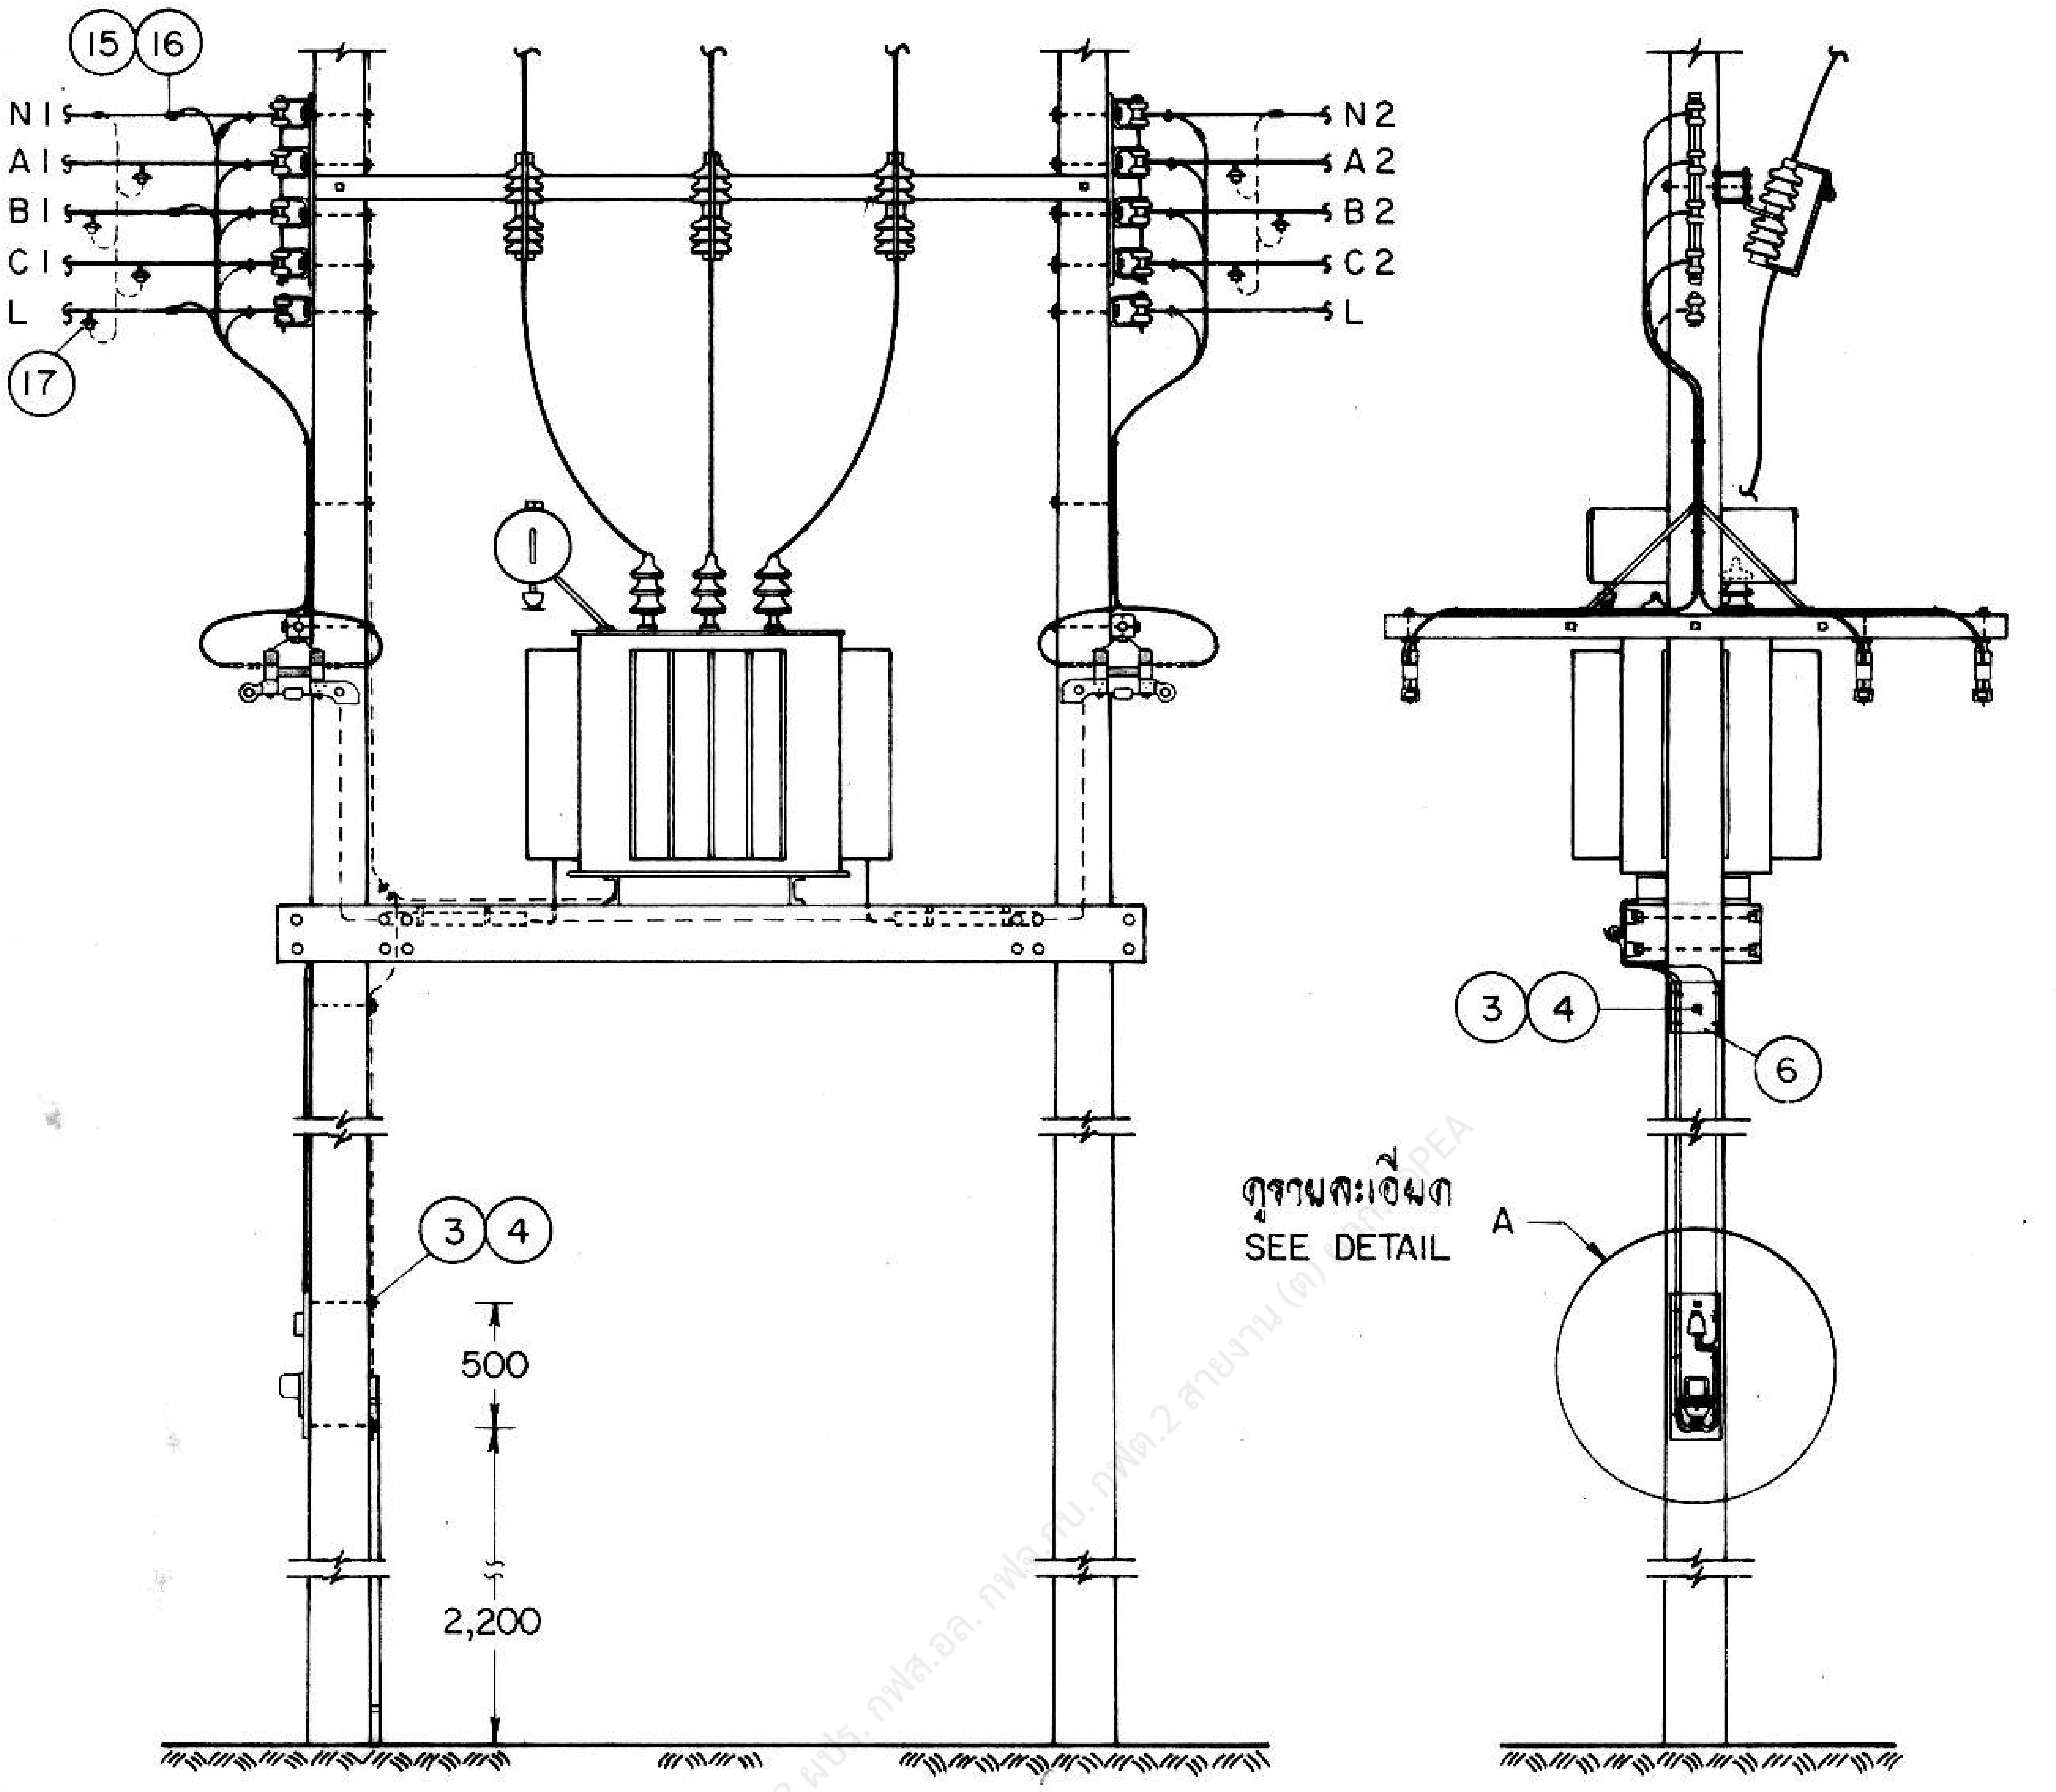
15
16
N1
A1
B1
C1
L
17
N2
A2
B2
C2
L
1
3
4
500
2,200
3
4
6
ดูรายละเอียด
SEE DETAIL
A

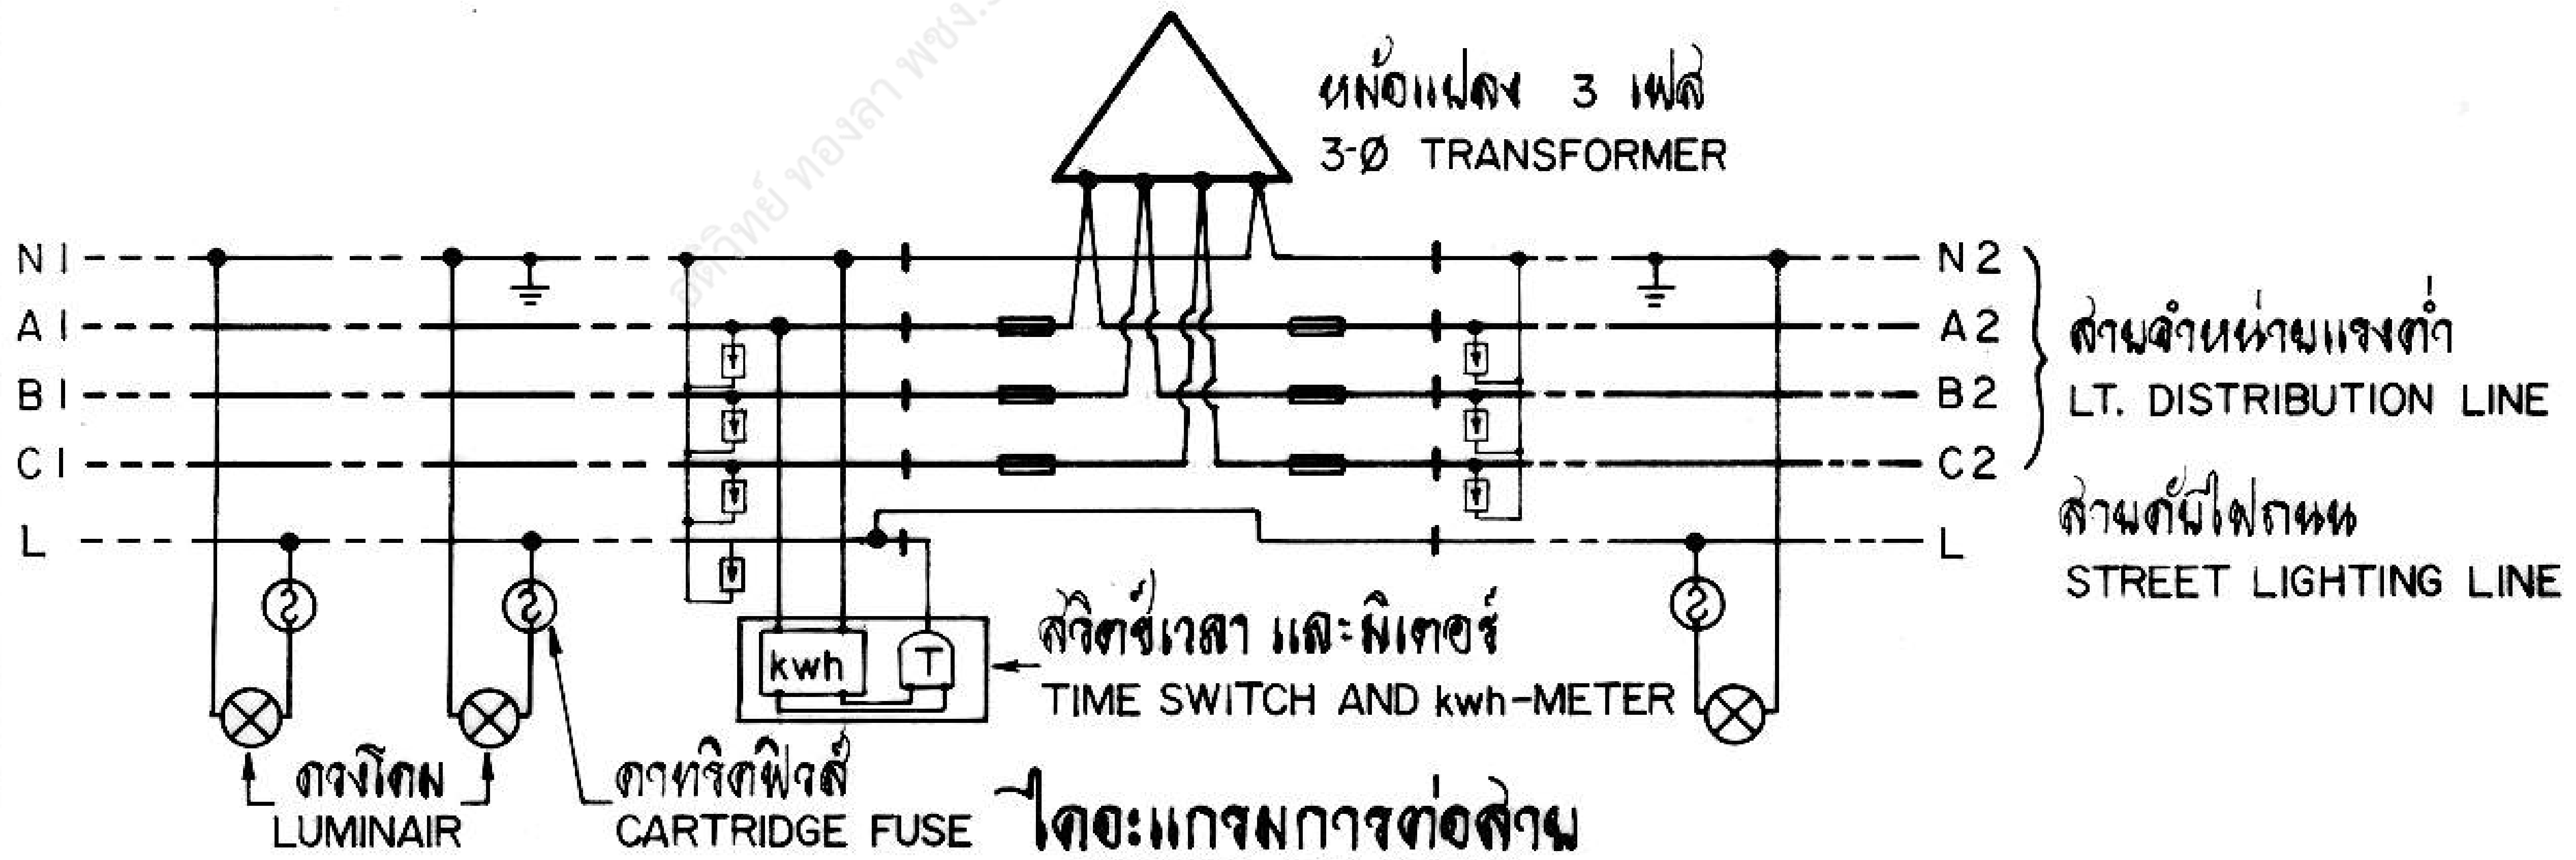
หม้อแปลง 3 เฟส
3-Ø TRANSFORMER
N1
A1
B1
C1
L
N2
A2
B2
C2
L
สายจำหน่ายแรงต่ำ
LT. DISTRIBUTION LINE
สายดับไฟถนน
STREET LIGHTING LINE
kwh
T
สวิตช์เวลา และ มิเตอร์
TIME SWITCH AND kwh-METER
ดวงโคม
LUMINAIR
คาทริดฟิวส์
CARTRIDGE FUSE

ไดอะแกรมการต่อสาย
WIRING DIAGRAM

สถิตย์ ทองลา พชง.3 ผปร. กฟส.อล. กฟจ.อบ. กฟต.2 สายงาน (ต) PEA

กองวิศวกรรมไฟฟ้าและเครื่องกล
ฝ่ายวิศวกรรม

ผู้เขียน
ผู้สำรวจ
วิศวกร
หัวหน้าแผนก
ผู้อำนวยการกอง
ผู้อำนวยการฝ่าย

รองผู้ว่าการฝ่ายเทคนิค

การไฟฟ้าส่วนภูมิภาค

ผู้ว่าการ : 11 มี.ค. 26

การติดตั้งสวิตช์เวลา
ข ที่เสาต้นนั่งร้านหม้อแปลง

TIME SWITCH INSTALLATION
B ON THREE-PHASE TRANSFORMER POLE
(PLATFORM MOUNTING)

ใช้แทนแบบ
ถูกแทนโดยแบบ
เขียนเสร็จวันที่ 3 มี.ค. 26
แก้แบบวันที่
มิติเป็น มม.
มาตราส่วน 1 : 50

แบบเลขที่ SAI-015/26009
แผ่นที่ 2 ของจำนวน 6 แผ่น

การประกอบเลขที่
ASSEMBLY NO. 0810

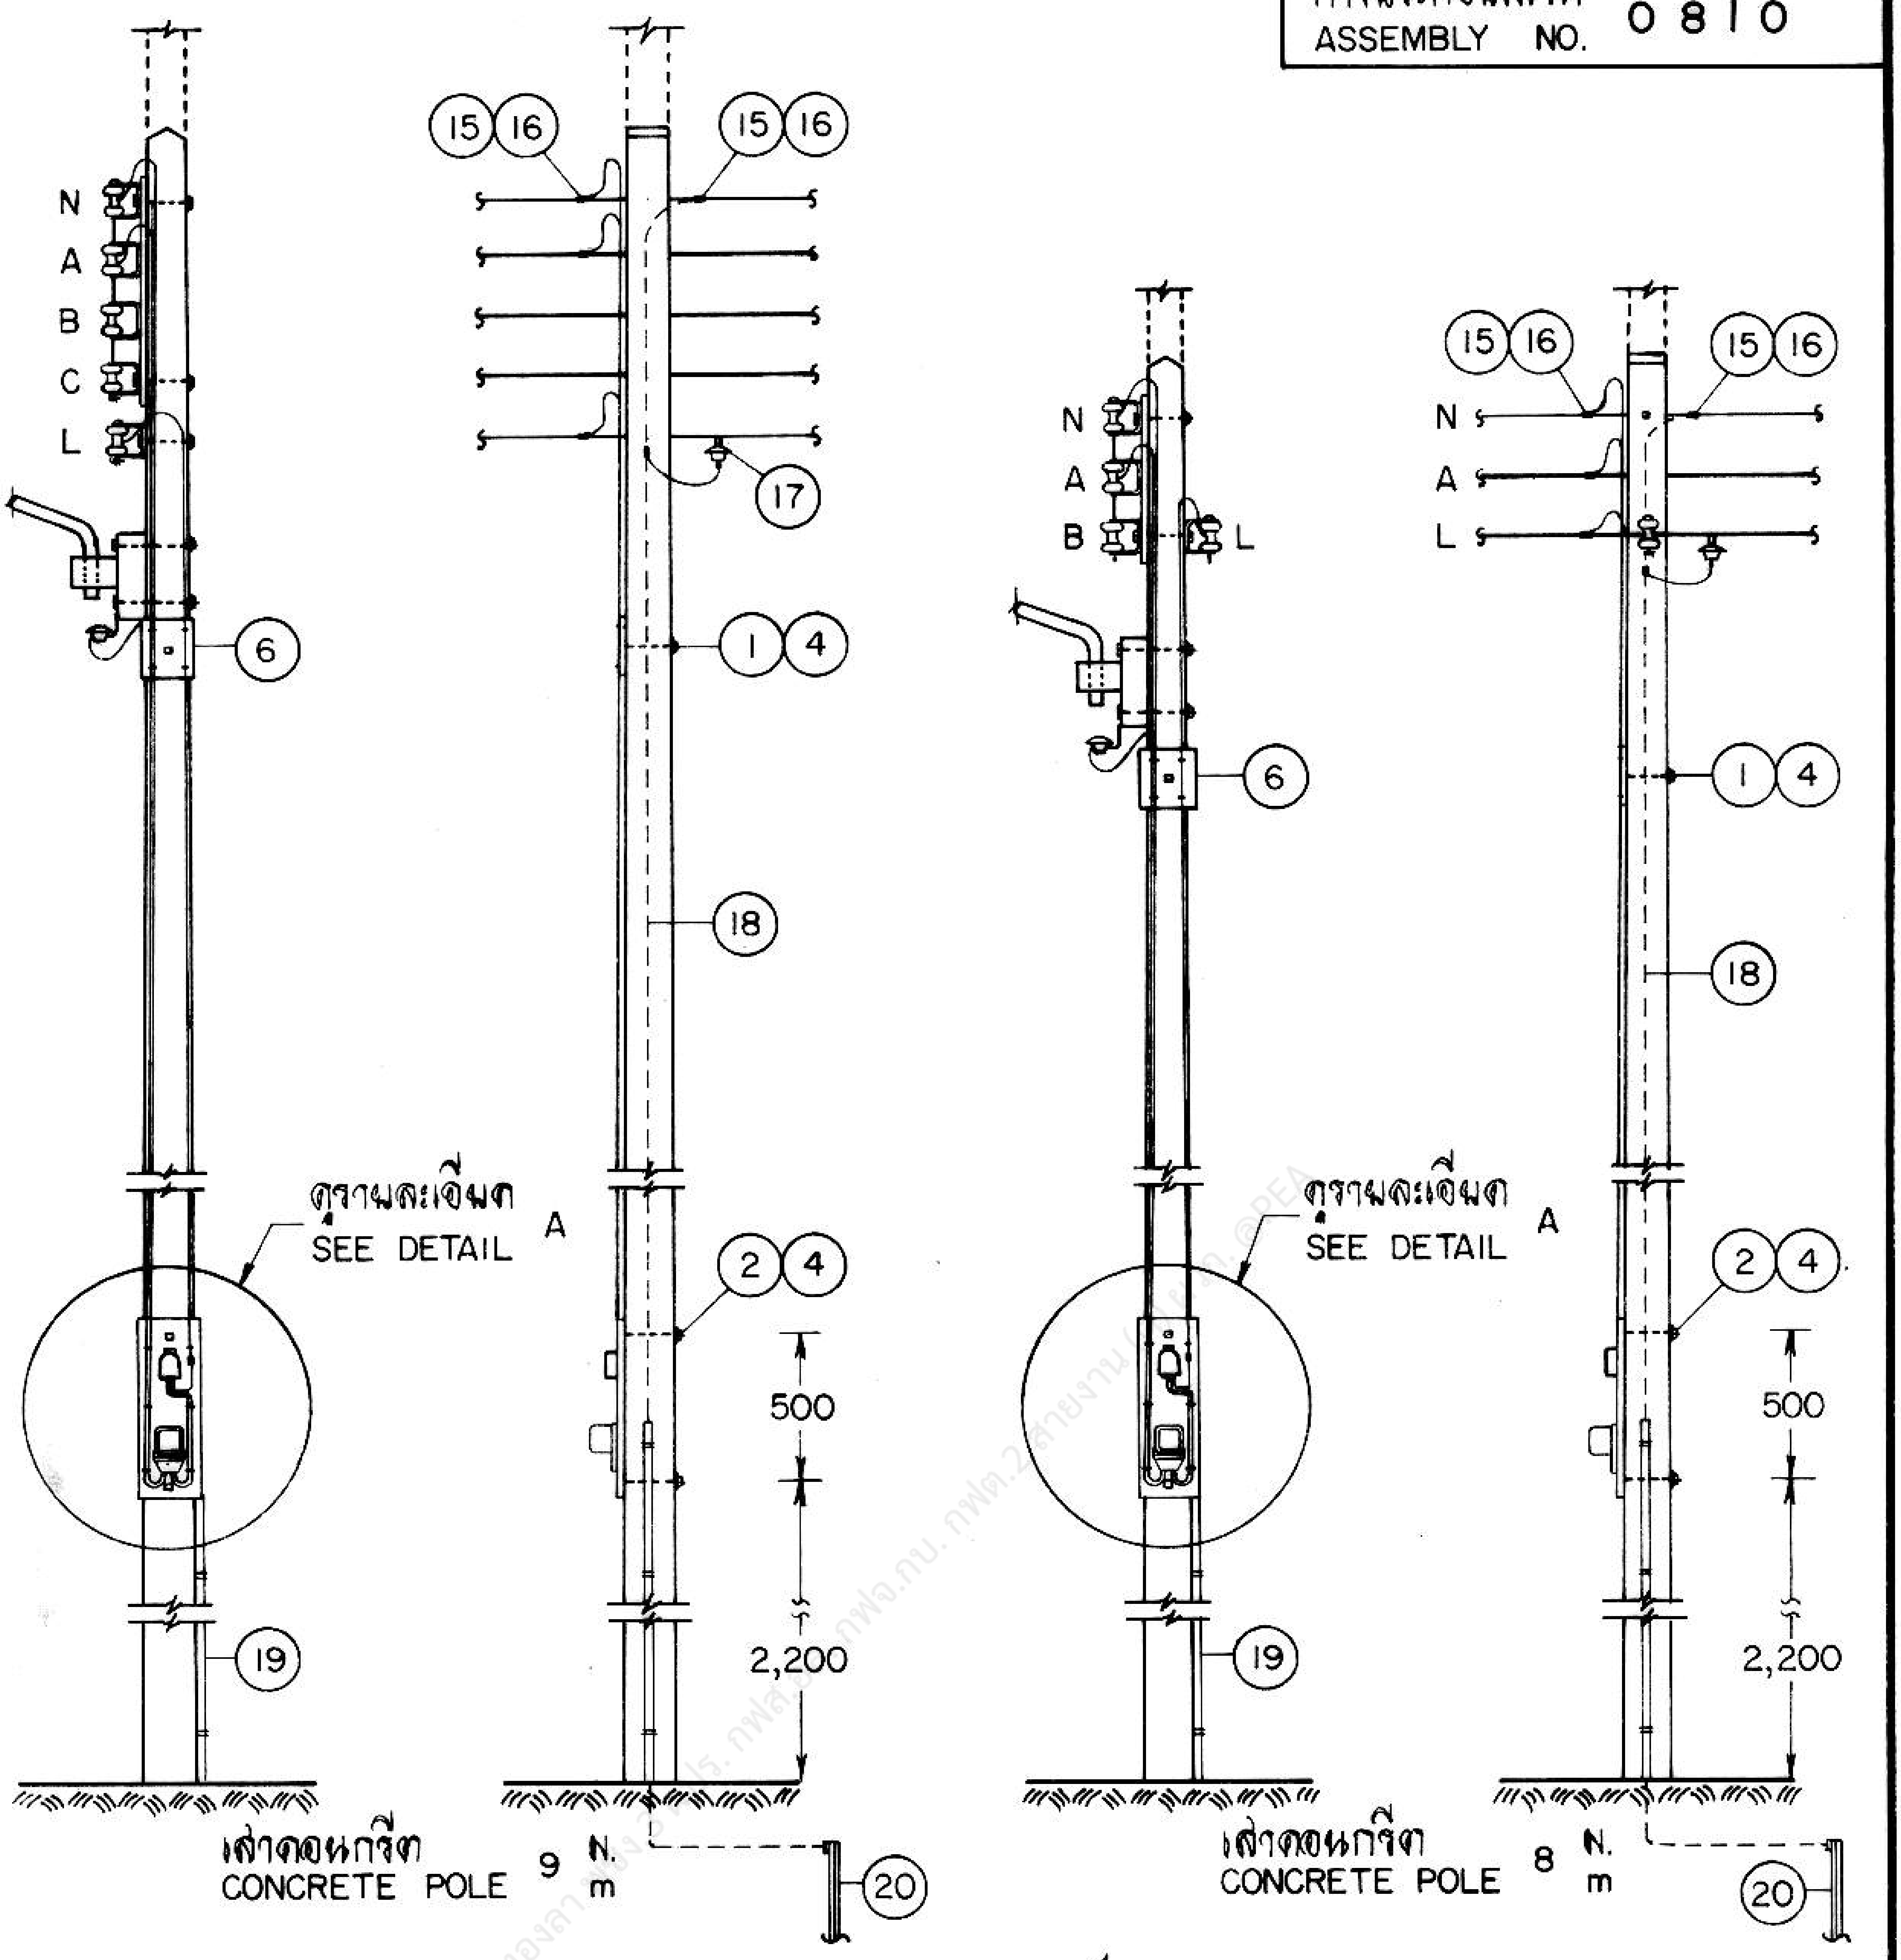
N
A
B
C
L
15
16
17
6
1
4
18
2
4
19
20
ดูรายละเอียด
SEE DETAIL A
500
2,200
เสาคอนกรีต
CONCRETE POLE 9 ม. m
เสาคอนกรีต
CONCRETE POLE 8 ม. m

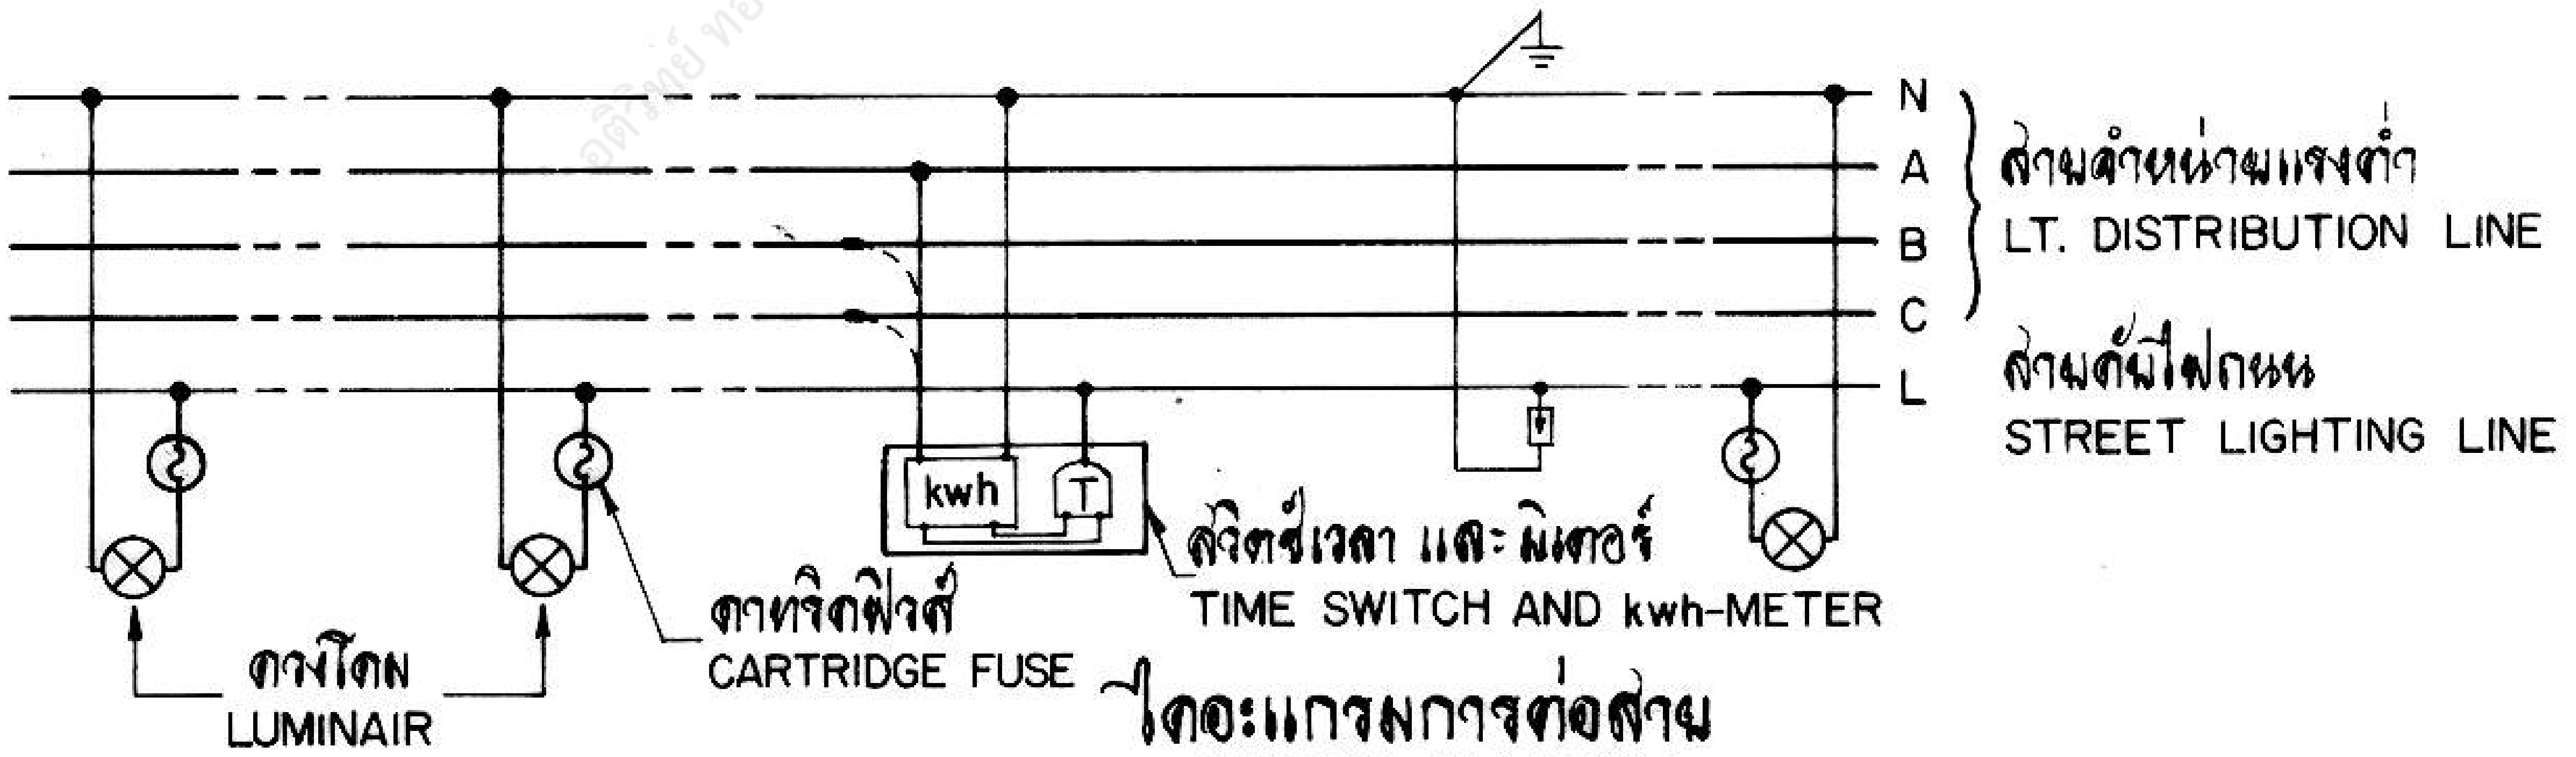
N
A
B
C
L
สายจำหน่ายแรงต่ำ
LT. DISTRIBUTION LINE
สายคุมไฟถนน
STREET LIGHTING LINE
kwh
T
สวิตช์เวลา และ มิเตอร์
TIME SWITCH AND kwh-METER
คาทริดฟิวส์
CARTRIDGE FUSE
ดวงโคม
LUMINAIR

ไดอะแกรมการต่อสาย
WIRING DIAGRAM

กองวิศวกรรมไฟฟ้าและเครื่องกล
ฝ่ายวิศวกรรม

ผู้เขียน
ผู้สำรวจ
วิศวกร
หัวหน้าแผนก
ผู้อำนวยการกอง
ผู้อำนวยการฝ่าย

รองผู้ว่าการฝ่ายเทคนิค

การไฟฟ้าส่วนภูมิภาค

ผู้ว่าการ . 11 ธ.ค. 26

การติดตั้งสวิตช์เวลา
ค ที่เสาต้นในไลน์ระบบจำหน่ายแรงต่ำ

TIME SWITCH INSTALLATION
C ON THE POLE IN LT. DISTRIBUTION LINE

ใช้แทนแบบ
ถูกแทนโดยแบบ
เขียนเสร็จวันที่ 3 มี.ค. 26
แก้แบบวันที่
มิติเป็น มม.
มาตราส่วน 1 : 40

แบบเลขที่ SAI–015/26009
แผ่นที่ 3 ของจำนวน 6 แผ่น

การประกอบเลขที่
ASSEMBLY NO. 0810

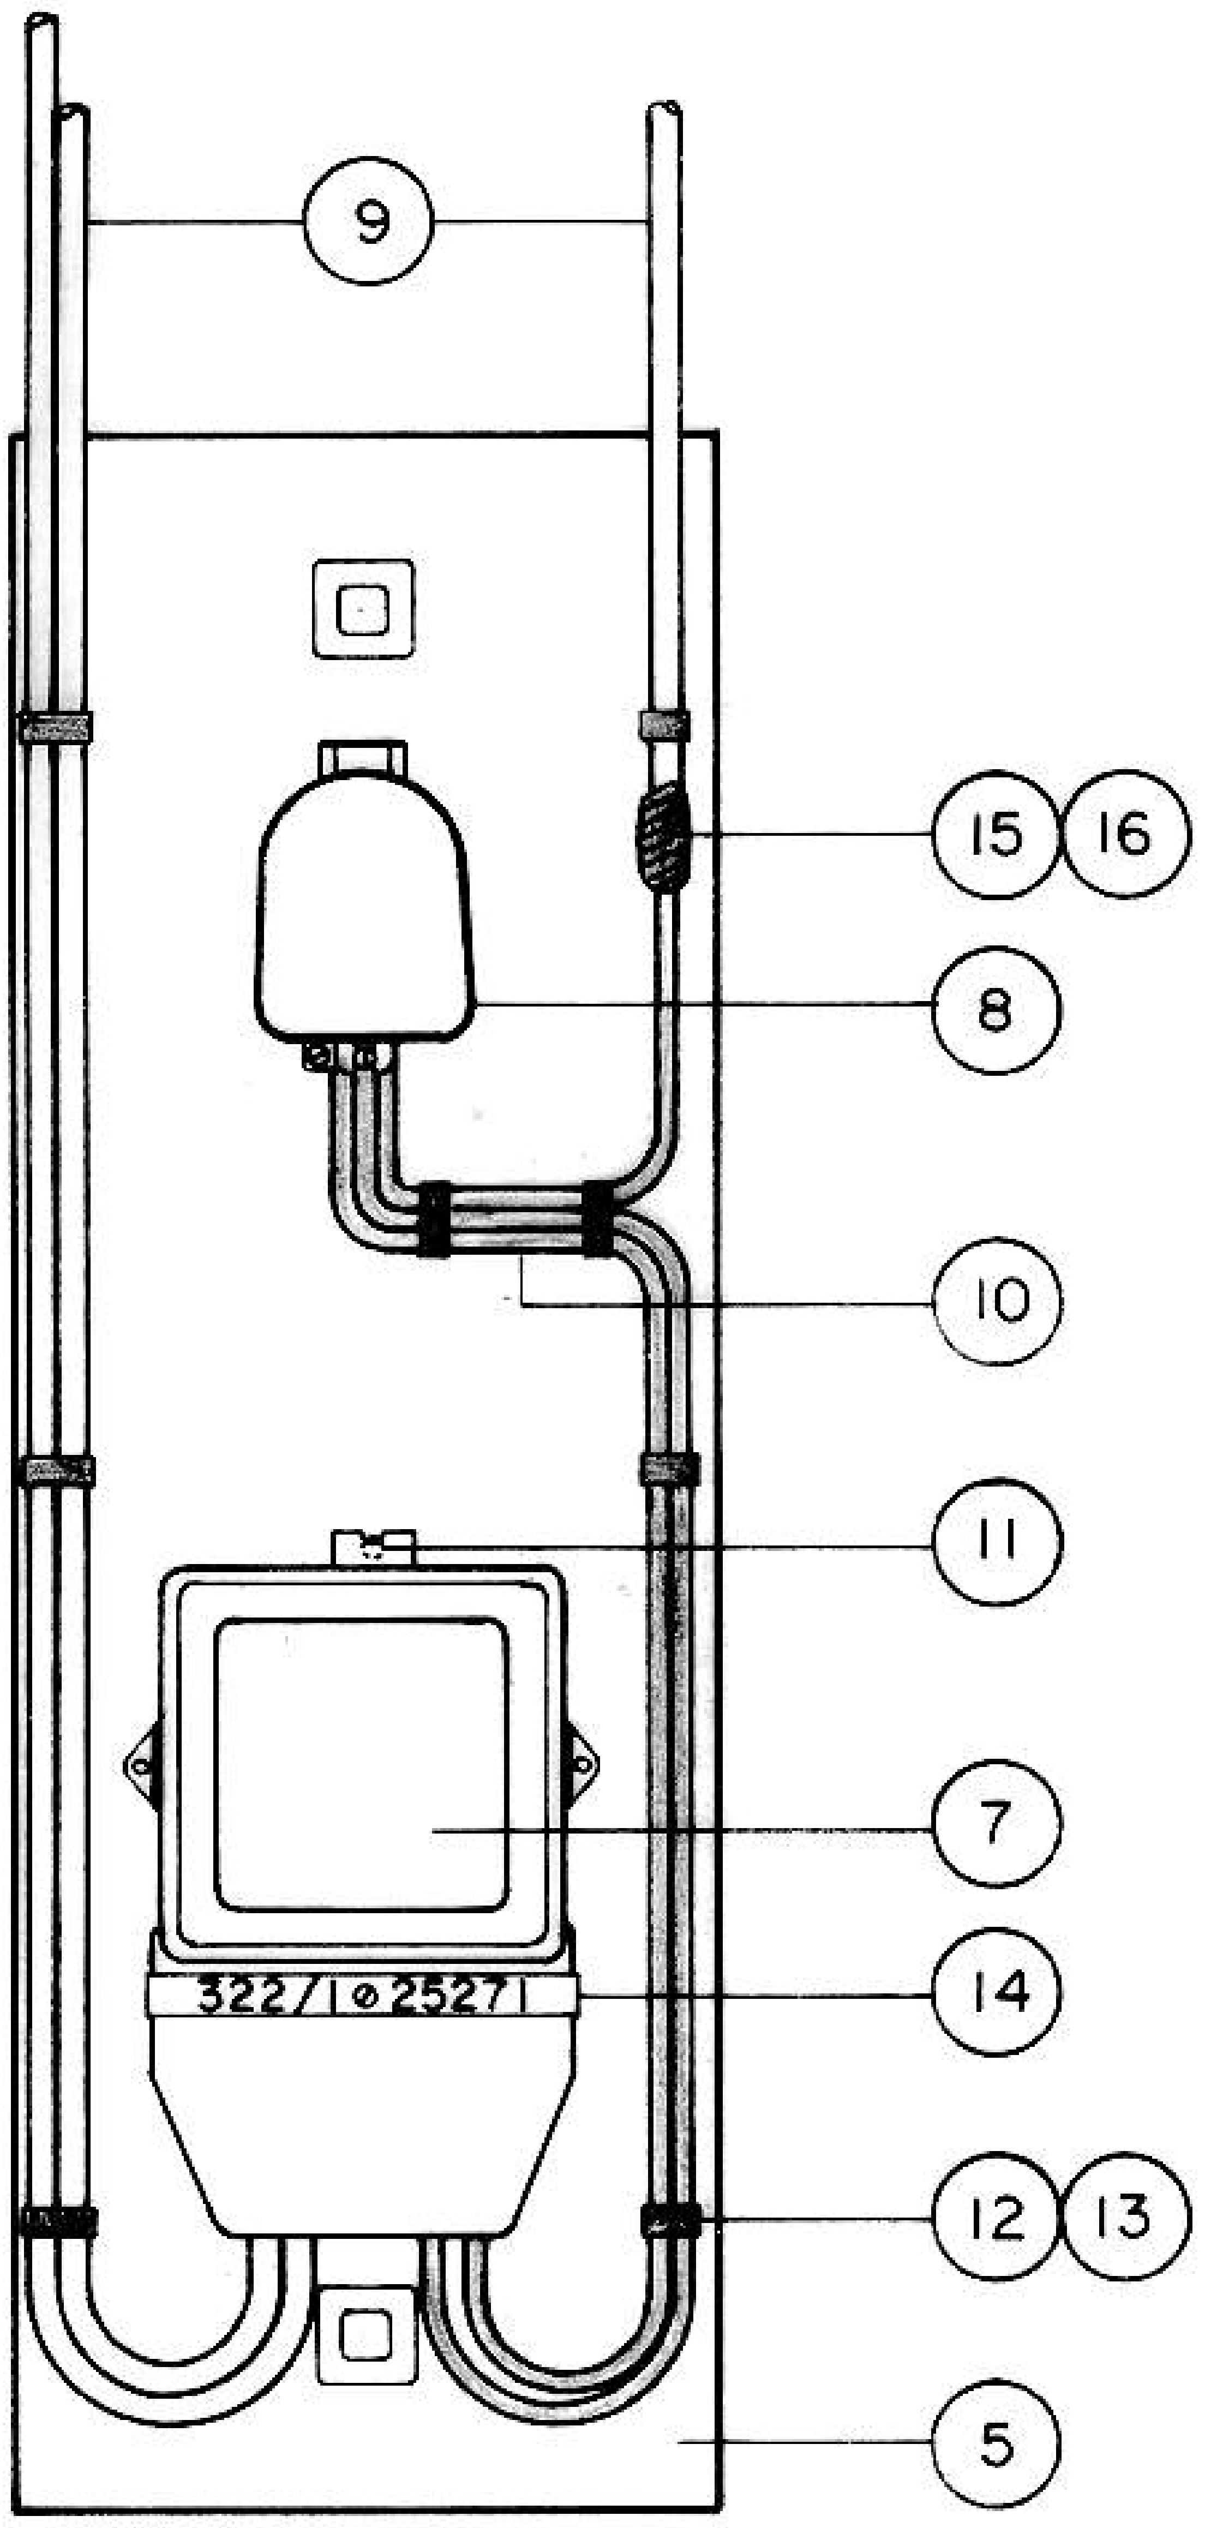

รายละเอียด A
DETAIL

การติดตั้งนี้ สำหรับสวิตช์เวลาแบบติดตั้งภายนอก เช่น ผลิตภัณฑ์ HORSTMANN (30A) และผลิตภัณฑ์ TORK (40A) ขนาดสายไฟเข้าออกสวิตช์เวลา ให้ดูตาราง ①

THIS INSTALLATION IS FOR OUTDOOR TYPE TIME SWITCH, SUCH AS HORSTMANN (30 A) AND TORK (40 A). THE SIZE OF CABLE ENTRANCE TO TIME SWITCH SEE TABLE ①

ตาราง ①
TABLE

ขนาดของสวิตช์เวลา SIZE OF TIME SWITCH	ขนาดของสายไฟ SIZE OF CONDUCTOR	หมายเหตุ REMARK
30 A	10—16 ต.มม. mm^2	1. ใช้สายทองแดงหุ้มฉนวน พีวีซี. 750 โวลต์ 75°C และควรเป็นสายตัวนำเส้นเดียว 2. ที่ขั้วต่อสายของสวิตช์เวลา ผลิตภัณฑ์ TORK ให้เข้าปลายสายด้วยหางปลาสำหรับสายทองแดง (ต้องจัดหาเพิ่มใหม่) 1. USE COPPER CONDUCTOR PVC INSULATED 750 VOLT, 75°C, AND SHOULD BE SOLID CONDUCTOR. 2. FOR TORK'S TIME SWITCH, AT TERMINAL, USE COPPER CABLE LUG IN CONNECTION..
40 A	16—25 ต.มม. mm^2	

กองวิศวกรรมไฟฟ้าและเครื่องกล ฝ่ายวิศวกรรม	การไฟฟ้าส่วนภูมิภาค	ใช้แทนแบบ ถูกแทนโดยแบบ
ผู้เขียน ผู้สำรวจ วิศวกร หัวหน้าแผนก ผู้อำนวยการกอง ผู้อำนวยการฝ่าย	ผู้ว่าการ 11 [illegible] 26	เขียนเสร็จวันที่ 3 มี.ค. 26 แก้แบบวันที่ มิติเป็น มม. มาตราส่วน 1 : 15
	การติดตั้งสวิตช์เวลา	
รองผู้ว่าการฝ่ายเทคนิค	TIME SWITCH INSTALLATION	แบบเลขที่ SAI-015/26009 แผ่นที่ 4 ของจำนวน 6 แผ่น

5 ส.ค. 2526

อดิศักดิ์ ทองลา พชง.3 ผจ.กบ. กฟต.2 สายงาน (ต) ผวภ. @PEA

การประกอบเลขที่ ASSEMBLY NO.	0810

บัญชีวัสดุ
BILL OF MATERIAL

ลำดับที่ ITEM	รายละเอียด DESCRIPTION	จำนวน REQ'D ก/A	 ข/B	 ค/C	วัสดุเลขที่ MAT. NO.
1	สลักเกลียว M 16 X 200 มม. BOLT, MACHINE, M 16 X 200 mm	–	–	1	01110202
2	สลักเกลียว M 16 X 250 มม. BOLT, MACHINE, M 16 X 250 mm	1	–	2	01110203
3	สลักเกลียว M 16 X 300 มม. BOLT, MACHINE, M 16 X 300 mm	2	2	–	01110204
4	แหวนสี่เหลี่ยมแบน ขนาด 52 X 52 X 4.5 มม. รู Ø 18 มม. มอก. 258 WASHER, SQUARE, FLAT 52 X 52 X 4.5 mm HOLE Ø 18 mm, TIS 258	6	4	6	01180100
5	แป้นไม้รองมิเตอร์ไสแล้ว ขนาด 60 X 20 X 2 ซม. METER, PLATE (HARD WOOD) SURFACE FINISHED SIZE 60 X 20 X 2 cm	1	1	1	
6	แป้นไม้สำหรับยึดสายเข้าและออกจากมิเตอร์ไสแล้ว ขนาด 20 X 20 X 2 ซม. CABLE, PLATE (HARD WOOD) SURFACE FINISHED SIZE 20 X 20 X 2 cm	1	1	1	–
7	วัตต์อาวร์มิเตอร์ 1 เฟส 2 สาย 220 โวลต์ 20(40) แอมป์ ใช้ภายนอก METER, WATTHOUR, SINGLE-PHASE, 2-WIRE, 220 VOLT, 20(40) A WEATHER PROOF	1	1	1	06000003
8	สวิตช์เวลาวงจรเดียว สำหรับระบบ 220 โวลต์ ขนาด 30-40 แอมป์ (แบบใช้ภายนอก) TIME SWITCH, SINGLE CIRCUIT, FOR 220 V, 30-40 A (OUTDOOR TYPE)	1	1	1	07030802-3
9	สายอะลูมิเนียมหุ้มฉนวน PVC 750 โวลต์ 75°ซ. 25 ต.มม. มอก. 293 CABLE, AL PVC INSULATED, 750 V, 75°C, 25 mm^2 TIS 293	18 ม. m	18 ม. m	18 ม. m	02070000
10	สายทองแดงหุ้มฉนวน PVC 750 โวลต์ 75°ซ. มอก. 11 ขนาดตามต้องการ CABLE, COPPERS CONDUCTOR, PVC INSULATED, 750 V, 75°C, TIS 11 SIZE AS REQ'D.	1.5 ม. m	1.5 ม. m	1.5 ม. m	–
11	ตะปูเกลียวชุบโครเมียม ขนาด 15-20 มม. SCREW, CHROME PLATED, SIZE 15-20 mm	6	6	6	
12	ตะปูหัวกลมแบนยาว 15-20 มม. Ø 1.00 มม. มอก. 113 NAIL, ROUND, MILD STEEL WIRE 15-20 mm LONG Ø 1.00 mm TIS 113	12	12	12	
13	เข็มขัดรัดสาย (ทำด้วยลวดอะลูมิเนียมแบน 1 X 10 มม.) CABLE STRAP (MADE OF ARMOUR TAPE 1 X 10 mm)				
14	หมายเลขผู้ใช้ไฟ (ทำด้วยแผ่นอะลูมิเนียม 15 X 100 มม. หนา 0.5 มม.) NUMBER OF CUSTOMER (MADE OF ALUMINIUM PLATE 15 X 100 mm, 0.5 mm THICKNESS)	1	1	1	
15	คอนเนคเตอร์ชนิดบีบแบบ H สำหรับสายอะลูมิเนียม ขนาดตามต้องการ CONNECTOR, COMPRESSION, H-TYPE, FOR AL CONDUCTOR SIZE AS REQUIRED	4	4	5	02320003-2
16	PVC เทป กว้าง 19 มม. (ใช้ความยาว 2 ม. ต่อ 1 จุด) มอก. 386 PVC TAPE, 19 mm WIDE (2 m LONG PER POINT) TIS 386				02180001 or 02180002
17	ล่อฟ้า 250-500 โวลต์ 2.5-5 กิโลแอมป์ LIGHTNING ARRESTER 250-500 VOLT, 2.5-5 kA	1	1	1	04000300
18	ลวดเหล็กตีเกลียว 50/7 ต.มม. มอก. 404 WIRE, STEEL STRANDED 50/7 mm^2, TIS 404	–	–	20 ม. m	01100004
19	ท่อ PVC แข็ง ขนาด 20 X 2,500 มม. พร้อมอุปกรณ์ยึด CONDUIT, PVC RIGID 20 X 2,500 mm COMPLETE WITH FIXING ACCESSORY	–	–	1	08040001
20	หลักดิน 60 X 60 X 5 มม. ยาว 2 ม. ROD, GROUND 60 X 60 X 5 mm 2 m LONG	–	–	1	01220002

กองวิศวกรรมไฟฟ้าและเครื่องกล
ฝ่ายวิศวกรรม

ผู้เขียน
ผู้ตรวจ
วิศวกร
หัวหน้าแผนก
ผู้อำนวยการกอง
ผู้อำนวยการฝ่าย

รองผู้ว่าการฝ่ายเทคนิค

การไฟฟ้าส่วนภูมิภาค

ผู้ว่าการ 11 ส.ค. 26.

การติดตั้งสวิตช์เวลา

TIME SWITCH INSTALLATION

ใช้แทนแบบ
ถูกแทนโดยแบบ
เขียนเสร็จวันที่ 3 มี.ค. 26
แก้แบบวันที่
มิติเป็น
มาตราส่วน

แบบเลขที่ SAI-015/26009
แผ่นที่ 5 ของจำนวน 6 แผ่น

- 5 ส.ค. 2526

การประกอบเลขที่ 0810
ASSEMBLY NO. 0810

หมายเหตุ

1. ในกรณีติดตั้งหม้อแปลงเฉพาะเพื่อจ่ายไฟให้กับวงจรไฟถนน ให้ติดตั้งฟิวส์สวิตช์แรงต่ำป้องกันวงจรไฟถนนที่เสาต้นหม้อแปลง
2. จำนวนดวงโคม ขนาดสวิตช์เวลา และขนาด ดี-คาทริดฟิวส์ ให้ดูรายละเอียดตามแบบเลขที่ SAI-015/23039 (การประกอบเลขที่ 0807)

NOTES

1. IN CASE OF TRANSFORMER INSTALLATION FOR STREET LIGHTING CIRCUIT ONLY, L.T. FUSE SWITCH SHALL BE INSTALLED AT TRANSFORMER POLE FOR PROTECTION STREET LIGHTING CIRCUIT.
2. NUMBER OF LUMINAIRS, SIZE OF TIME SWITCH AND SIZE OF D-CARTRIDGE FUSE SEE DETAIL IN DRAWING NO. SAI-015/23039 (ASSEMBLY NO. 0807)

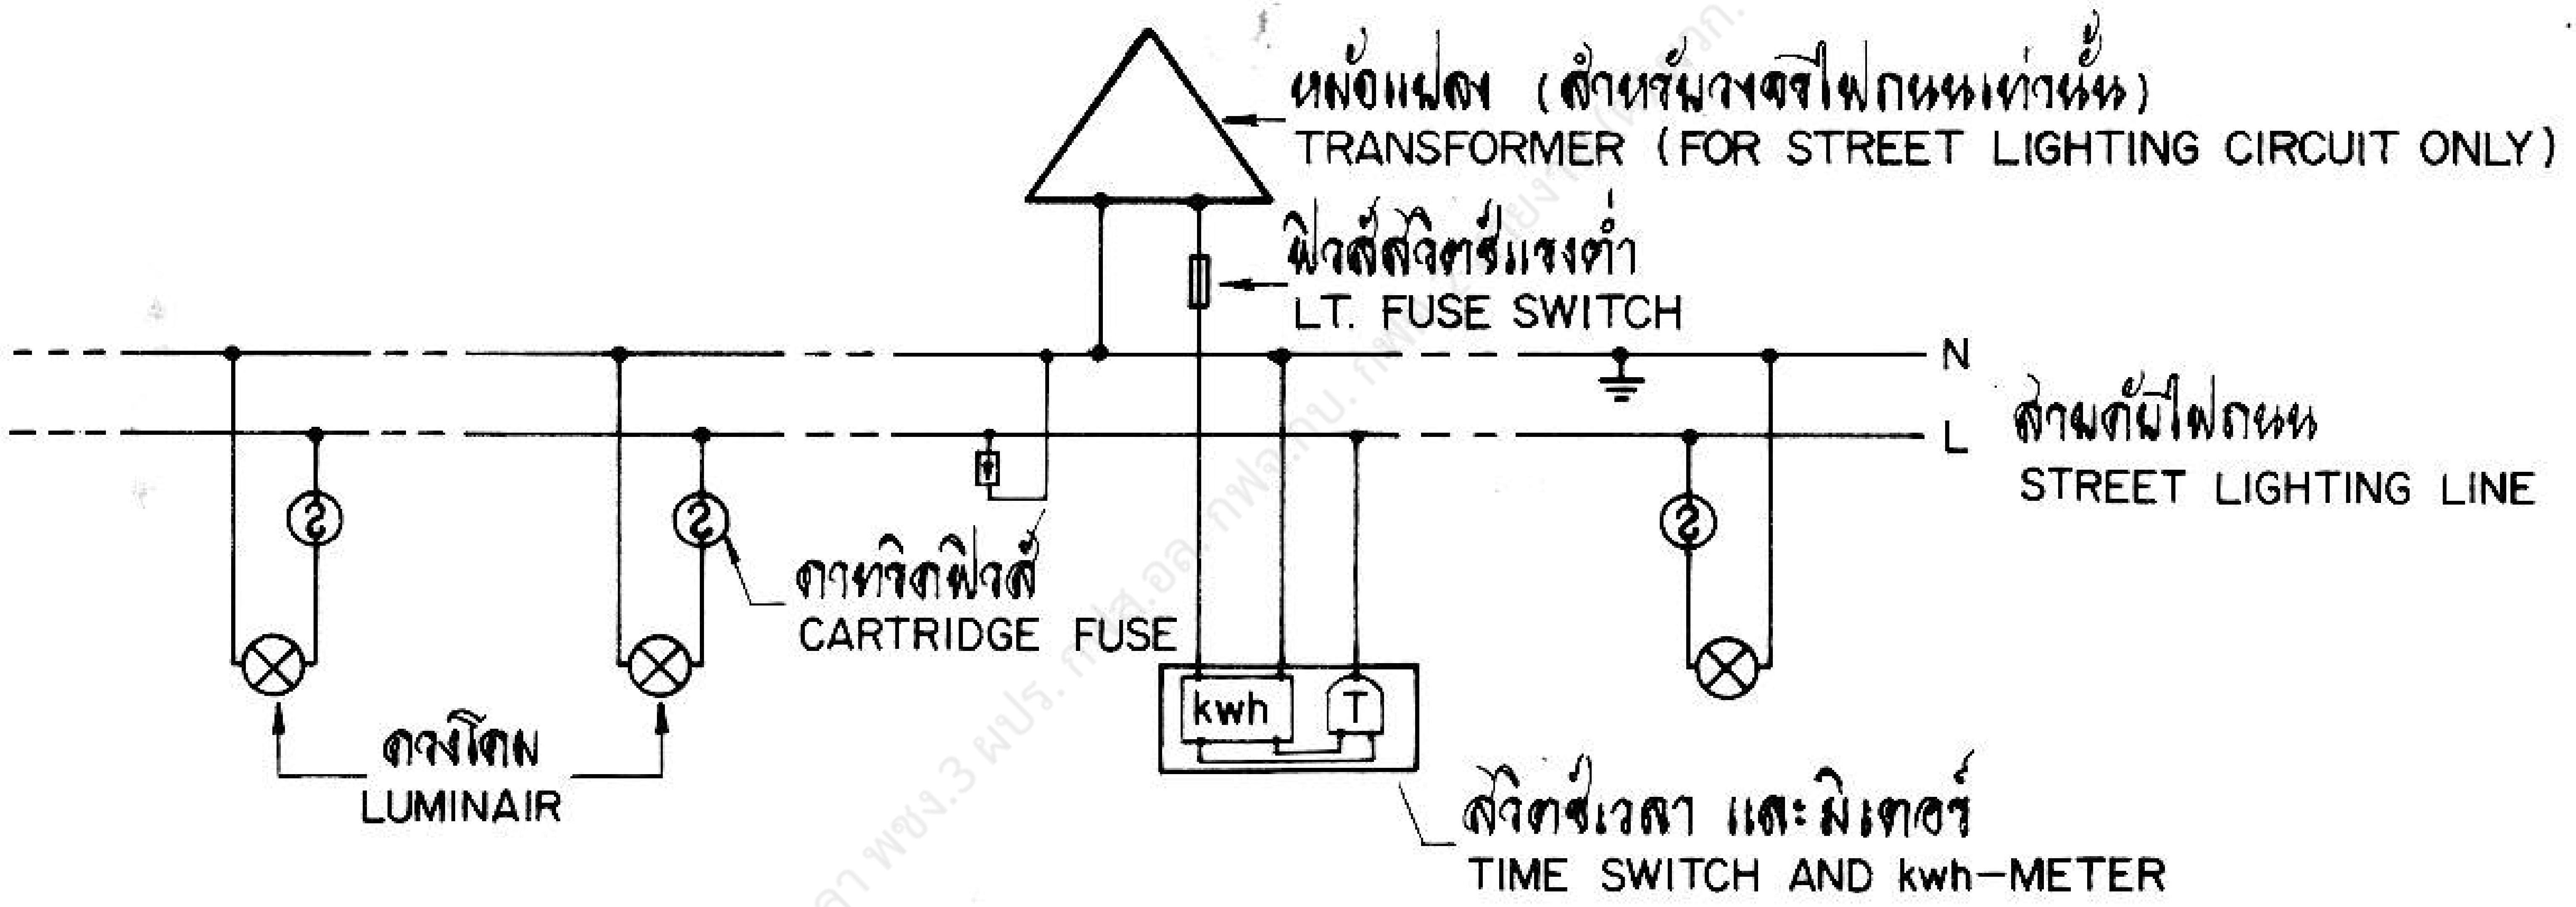
หม้อแปลง (สำหรับวงจรไฟถนนเท่านั้น)
TRANSFORMER (FOR STREET LIGHTING CIRCUIT ONLY)
ฟิวส์สวิตช์แรงต่ำ
L.T. FUSE SWITCH
N
L
สายดับไฟถนน
STREET LIGHTING LINE
คาทริดฟิวส์
CARTRIDGE FUSE
kwh
T
ดวงโคม
LUMINAIR
สวิตช์เวลา และมิเตอร์
TIME SWITCH AND kwh-METER

อดิวิทย์ ทองลา พชง.3 ผปร. กฟส.อล. @PEA

ไดอะแกรมการต่อสาย
WIRING DIAGRAM

กองวิศวกรรมไฟฟ้าและเครื่องกล
ฝ่ายวิศวกรรม

ผู้เขียน [illegible]
ผู้สำรวจ
วิศวกร ช.ต.
หัวหน้าแผนก
ผู้อำนวยการกอง
ผู้อำนวยการฝ่าย
รองผู้ว่าการฝ่ายเทคนิค

การไฟฟ้าส่วนภูมิภาค

ผู้ว่าการ [illegible] ส.ค. ๒๖.

การติดตั้งสวิตช์เวลา

TIME SWITCH INSTALLATION

ใช้แทนแบบ
ถูกแทนโดยแบบ
เขียนเสร็จวันที่ 3 มี.ค. 26
แก้แบบวันที่
มิติเป็น
มาตราส่วน

แบบเลขที่ SAI-015/26009
แผ่นที่ 6 ของจำนวน 6 แผ่น