การประกอบเลขที่ ASSEMBLY NO. **3209 A**

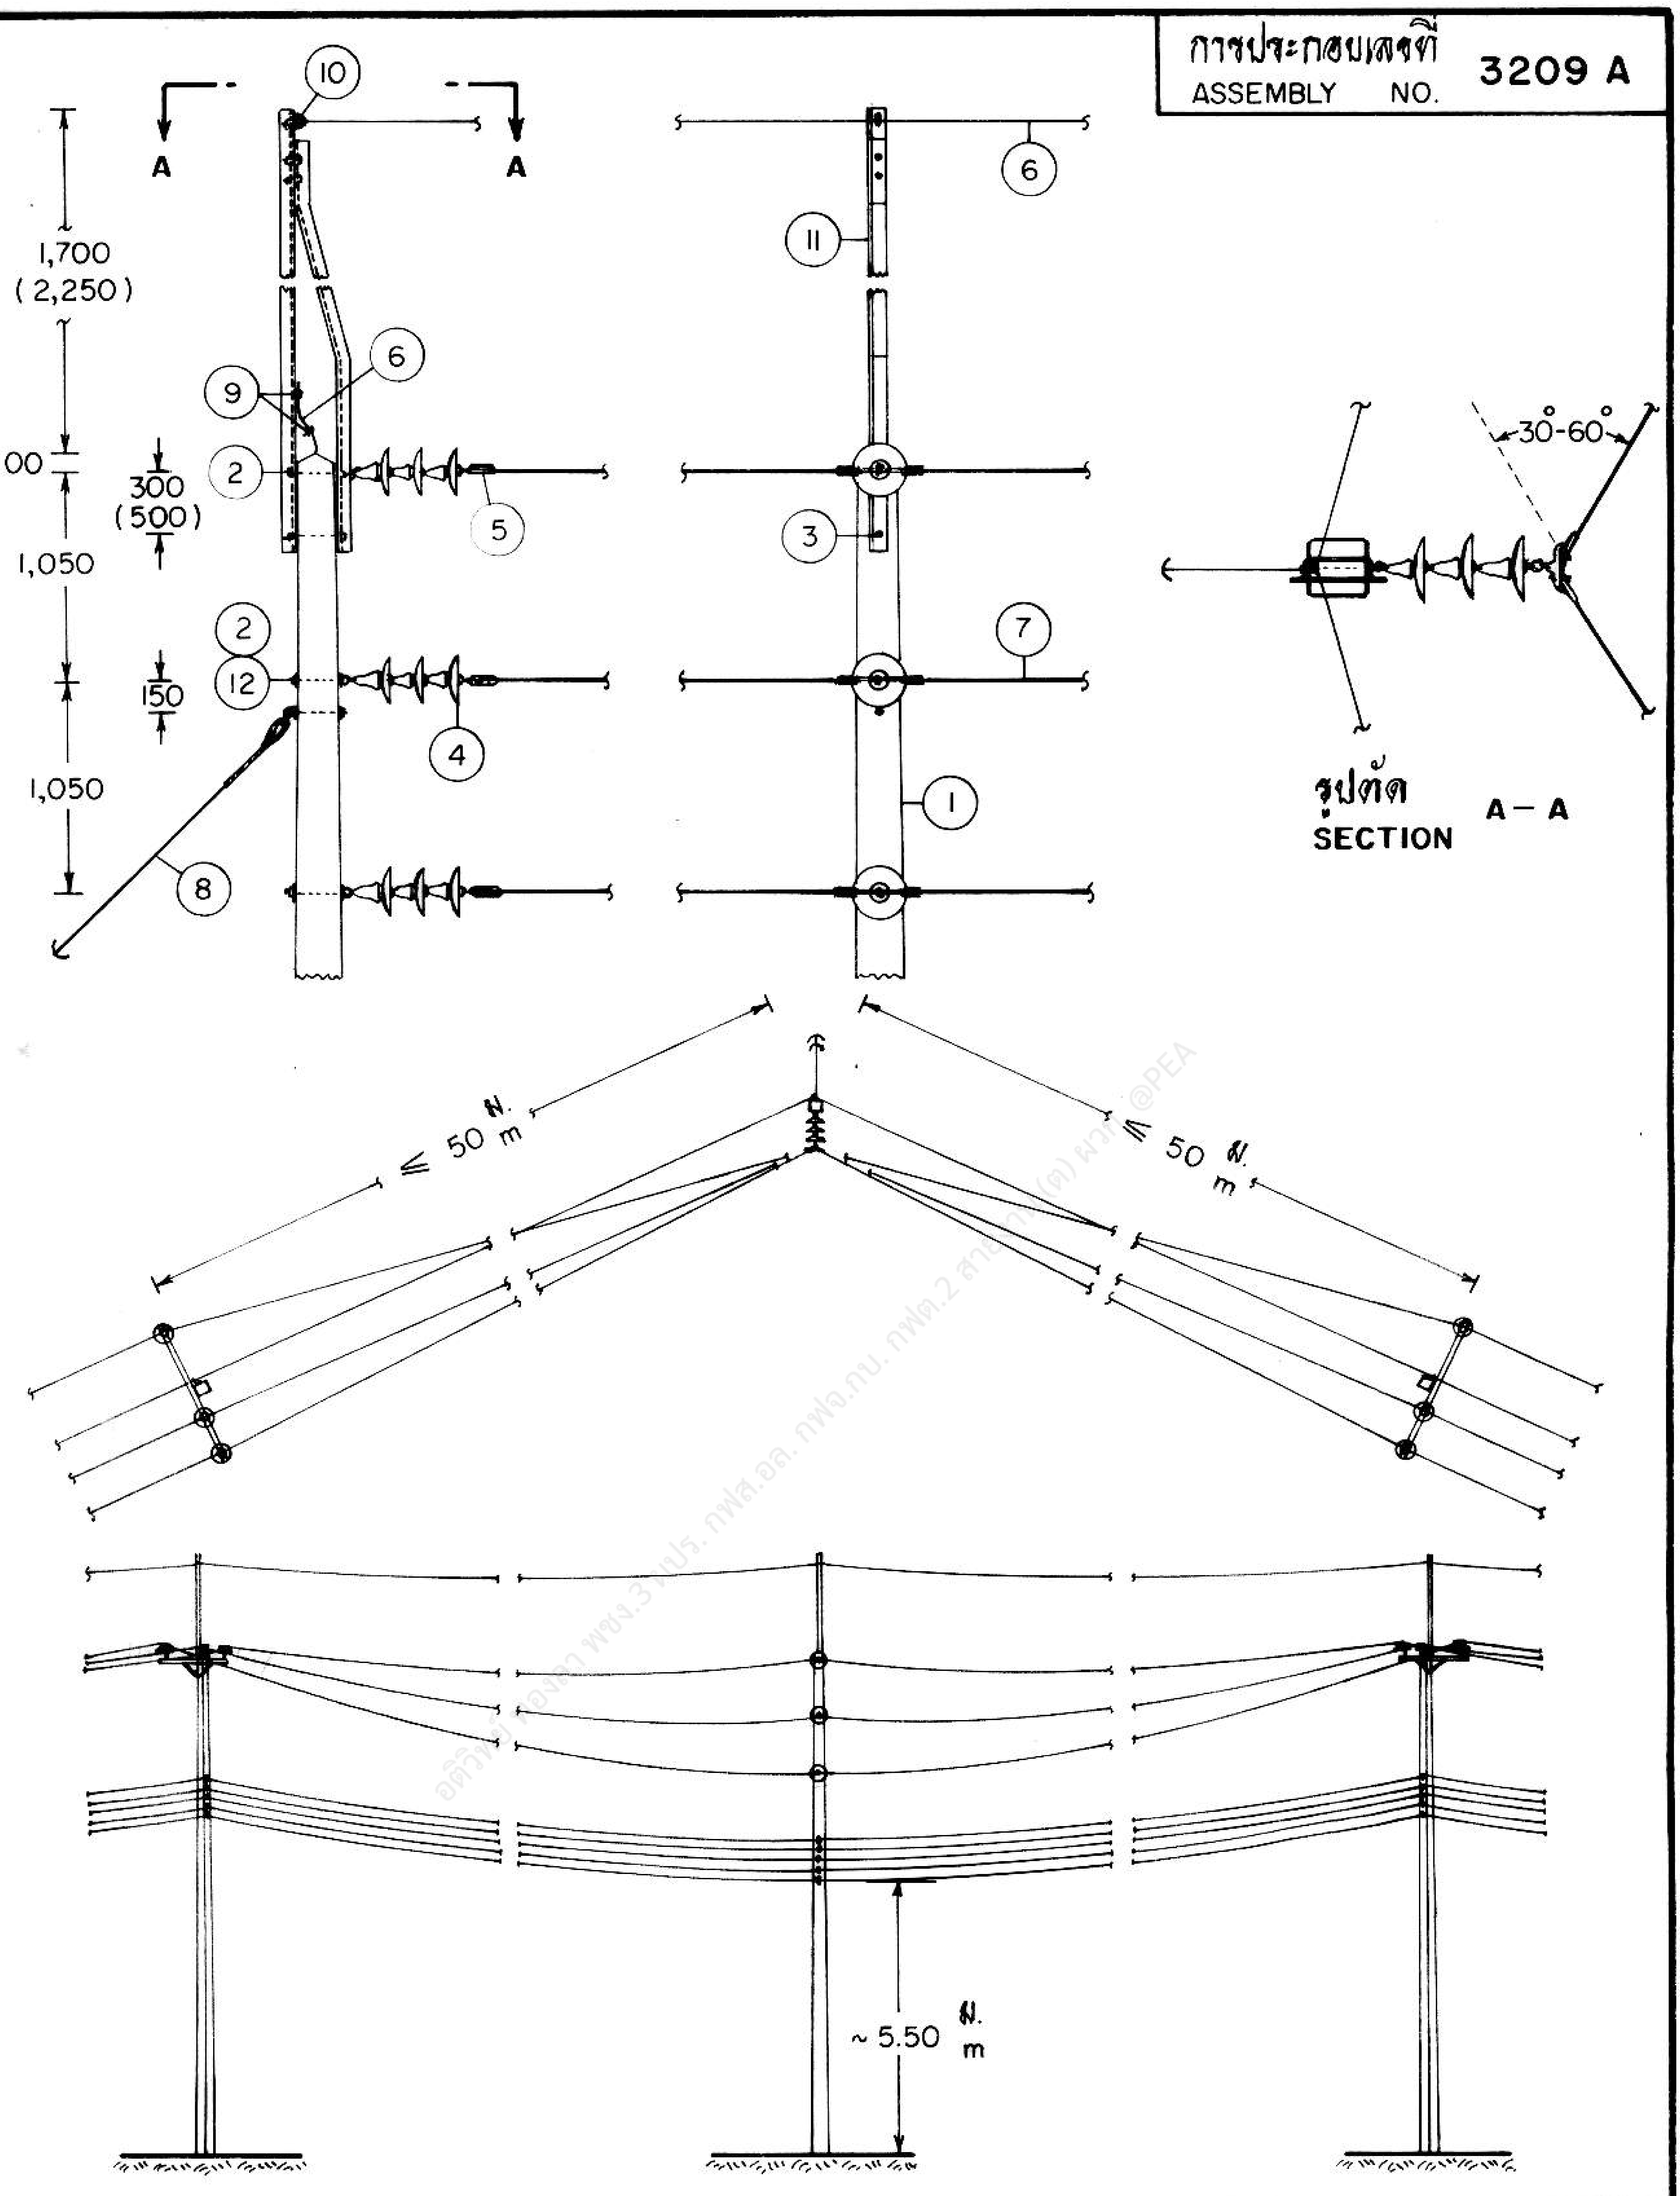

อติวิทย์ ทองอา พชง.3 บปร. กฟส.อล. กฟจ.กบ. กฟต.2 สายงาน(ต) ผวก. @PEA

กองวิศวกรรมไฟฟ้าและเครื่องกล
ฝ่ายวิศวกรรม

ผู้เขียน
ผู้สำรวจ
วิศวกร
หัวหน้าแผนก
ผู้อำนวยการกอง
ผู้อำนวยการฝ่าย

รองผู้ว่าการฝ่ายเทคนิค

การไฟฟ้าส่วนภูมิภาค

ผู้ว่าการ 3 ม.ค. 35

การประกอบลูกถ้วยแขวนกับเสาคอนกรีต
ระบบ 33 kV
สำหรับเสาต้นทางโค้ง 30° - 60°

SUSPENSION INSULATOR ASSEMBLY ON CONCRETE POLE
33 kV SYSTEM
FOR 30°- 60° ANGLE STRUCTURE

ใช้แทนแบบ
ถูกแทนโดยแบบ
เขียนเสร็จวันที่ 10 มิ.ย. 34
แก้แบบวันที่
มิติเป็น มิลลิเมตร
มาตราส่วน 1 : 50

แบบเลขที่ SAI-015/34015
แผ่นที่ 1 ของจำนวน 2 แผ่น

การประกอบเลขที่
ASSEMBLY NO. **3209 A**

บัญชีวัสดุ
BILL OF MATERIAL

ลำดับที่ ITEM	รายละเอียด DESCRIPTION	จำนวน REQ'D	วัสดุเลขที่ MAT. NO.
1	เสาคอนกรีต 12 ม. POLE, CONCRETE, 12 m LONG	1	00010003 (0034)
2	สลักห่วงกลม M 16 X 250 มม. BOLT, ROUND EYE, M 16 X 250 mm	3	01140002 (0254)
3	สลักเกลียว M 16 X 250 มม. BOLT, MACHINE, M 16 X 250 mm	1	01110203 (0223)
4	ลูกถ้วยแขวน มอก. 354 แบบ ง (แบบ 52-4) INSULATOR, SUSPENSION TYPE, TIS 354, TYPE D (CLASS 52-4)	9	03020002 (0415)
5	ซัสเพนชั่นแคล้มป์ แบบเคลวิส สำหรับสายอะลูมิเนียม 35-70 ต.มม. CLAMP, SUSPENSION, CLEVIS TYPE, Al 35-70 mm^2	3	03120100 (0292)
6	ลวดเหล็กตีเกลียว 25 ต.มม. มอก. 404 ความยาวตามต้องการ WIRE, STEEL STRANDED, 25 mm^2; TIS 404; LENGTH AS REQUIRED	ม. m	01100002 (0181)
7	สายอะลูมิเนียมเปลือย หรืออะลูมิเนียมแกนเหล็ก 35-50 ต.มม. CONDUCTOR, Al OR ACSR, 35-50 mm^2	ม. m	02010001-3 or 02020001-3
8	สายยึดโยง ระบบ 33 kV พร้อมสมอบกครบชุด GY-32 ANCHOR GUY, FOR 33 kV SYSTEM, GY-32	1 ชุด set	—
9	ยูแคล้มป์ สลัก 1 ตัว M 8 (ไวร์โรป คลิพ) CLAMP, SINGLE U-BOLT, M 8 (WIRE ROPE CLIP)	2	01230000 (0165)
10	กราวด์วายแคล้มป์ แบบ J 1152 GROUND WIRE CLAMP, J 1152	1	01230205 (0296)
11	เหล็กฉากรับสายล่อฟ้าทางโค้ง พร้อมสลักเกลียว M 12 X 35 มม. และแหวนสปริง (วัสดุเลขที่ 0212 และ 0364) จำนวน 2 ชุด OVERHEAD GROUND WIRE CORNER BAYONET; COMP. WITH 2 SETS OF M 12X35 mm BOLT AND SPRING WASHER (MAT. NO. 0212 AND 0364)	1	01010002 or 01010007
12	แหวนสี่เหลี่ยมแบน 52 X 52 X 4.5 มม. รู Ø 18 มม. มอก. 258 WASHER, SQUARE, FLAT, 52 X 52 X 4.5 mm, HOLE Ø 18 mm, TIS 258	4	01180100 (0355)

ข้อแนะนำในการติดตั้ง

1. ขนาดสายไฟฟ้าสูงสุด :
   สายอะลูมิเนียมเปลือย ขนาด 50 ต.มม. หรือ
   สายอะลูมิเนียมแกนเหล็ก ขนาด 50/8 ต.มม.
2. ระยะห่างระหว่างเสาช่วงทางโค้งสูงสุด: 50 ม.
3. ระยะหย่อนยานของสายไฟฟ้า ช่วงทางโค้ง ต่ำสุด : 0.50 ม.
4. หากพาดสายโตกว่าขนาด 50 ต.มม. ขึ้นไป ให้ก่อสร้างตามแบบเลขที่ I50-015/120341 (การประกอบเลขที่ 3209) แทน

SUGGESTION

1. MAXIMUM CONDUCTOR SIZE :
   ALUMINIUM CONDUCTOR, 50 mm^2 OR
   ACSR CONDUCTOR, 50/8 mm^2.
2. MAXIMUM SPAN LENGTH, FOR ANGLE SPAN SECTION : 50 m .
3. MINIMUM SAG OF ALL CONDUCTORS, FOR ANGLE SPAN SECTION : 0.50 m .
4. IF CONDUCTOR SIZE LARGER THAN 50 mm^2, IT SHALL BE CONSTRUCTED ACCORDING TO DWG. NO. I50-015/120341 (ASSEMBLY NO. 3209) .

กองวิศวกรรมไฟฟ้าและเครื่องกล
ฝ่ายวิศวกรรม

ผู้เขียน
ผู้สำรวจ
วิศวกร
หัวหน้าแผนก
ผู้อำนวยการกอง
ผู้อำนวยการฝ่าย

รองผู้ว่าการฝ่ายเทคนิค

การไฟฟ้าส่วนภูมิภาค

ผู้ว่าการ 3 ม.ค. 35

การประกอบลูกถ้วยแขวนกับเสาคอนกรีต
ระบบ 33 kV
สำหรับเสาต้นทางโค้ง 30°- 60°

SUSPENSION INSULATOR ASSEMBLY ON CONCRETE POLE
33 kV SYSTEM
FOR 30°-60° ANGLE STRUCTURE

ใช้แทนแบบ
ถูกแทนโดยแบบ
เขียนเสร็จวันที่ 10 มิ.ย. 34
แก้แบบวันที่
มิติเป็น
มาตราส่วน

แบบเลขที่ SAI-015/34015
แผ่นที่ 2 ของจำนวน 2 แผ่น